


断面 A　縦断（展開）：保育室の中ほど r=197 m、西を見る

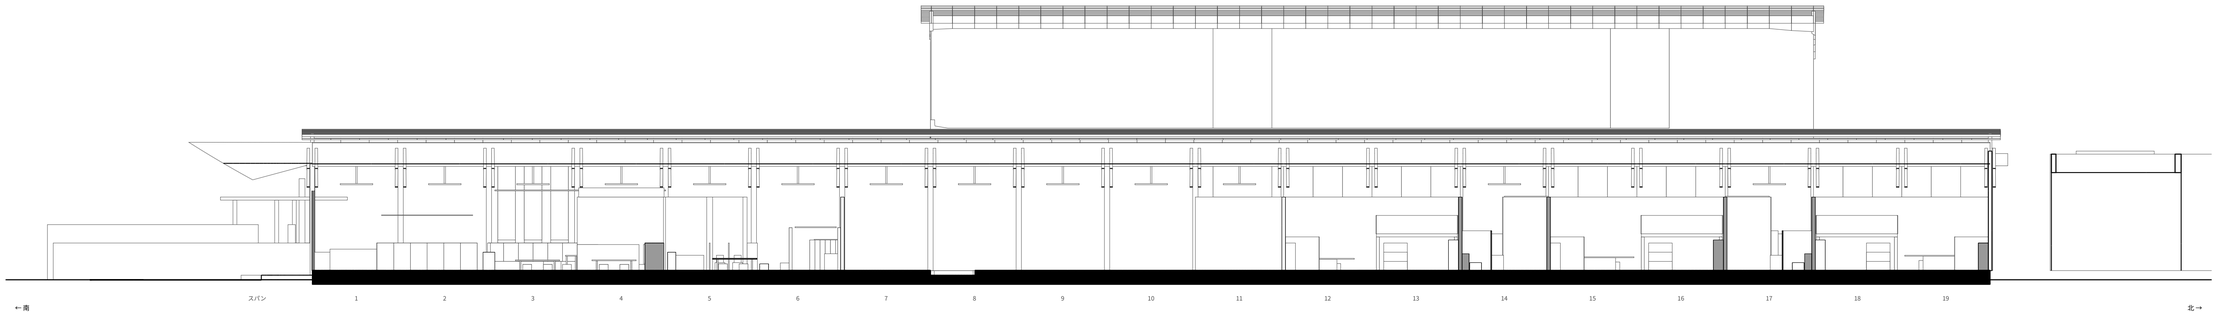


断面 B　海峡（スパン 8+0.75）：南の入口・キッチン・2 階・緑側　北を見る

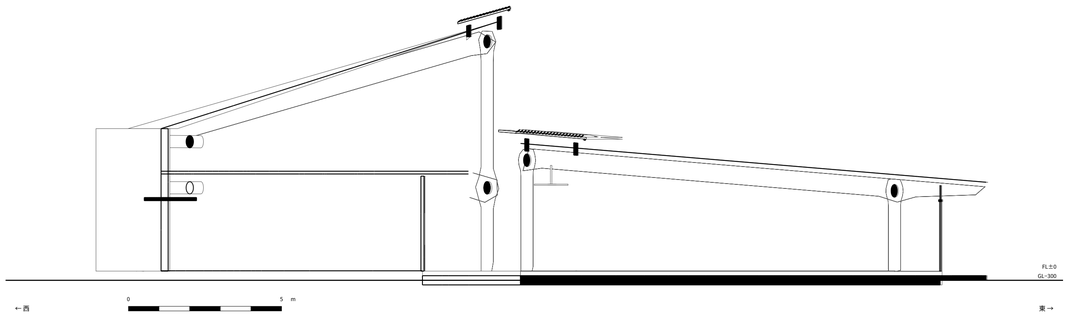


断面 C　4 歳・遊戯室（スパン 16 の中央）　北を見る

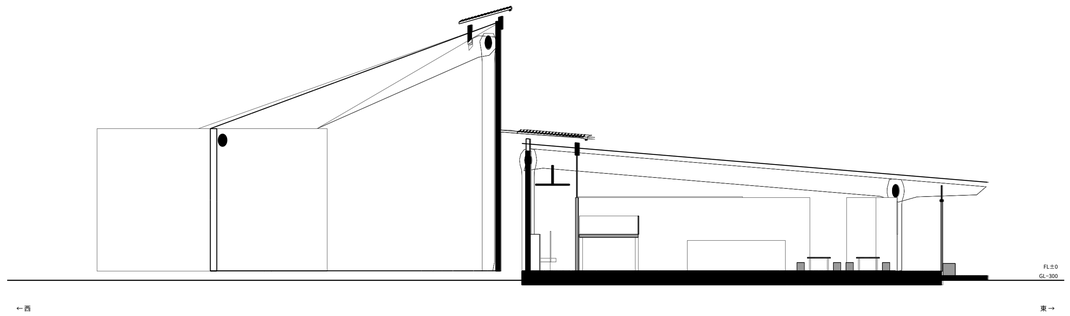


断面図 A（縦断・展開）・B・C　1/100（A1）

こどもたちの育ち舎　3dm（sodachiya_exact.3dm）から自動で作図