

断面 A　縦断（展開）　保育室の中ほど r=197 m の弧で切って平らに伸ばす、西を見る

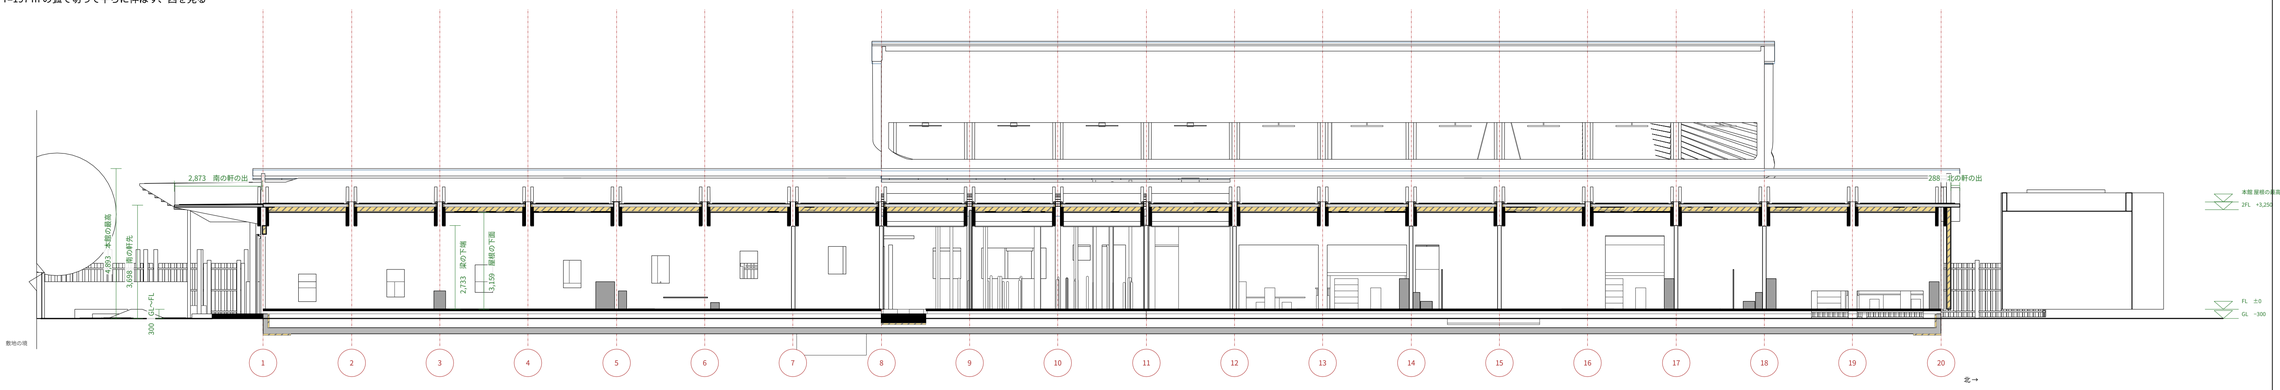


←南（高野川の側）

断面 B　海峡（スパン 8+0.75）　南の入口・キッチン・2 階・すき間・本館・縁側、北を見る

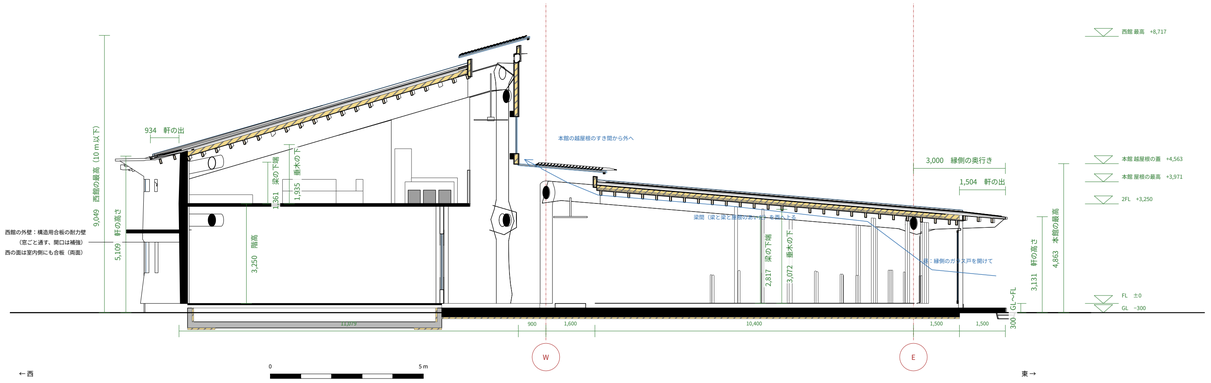

断面 C　4 歳・遊戯室の摺鉢ネット（スパン 15+0.6）　北を見る

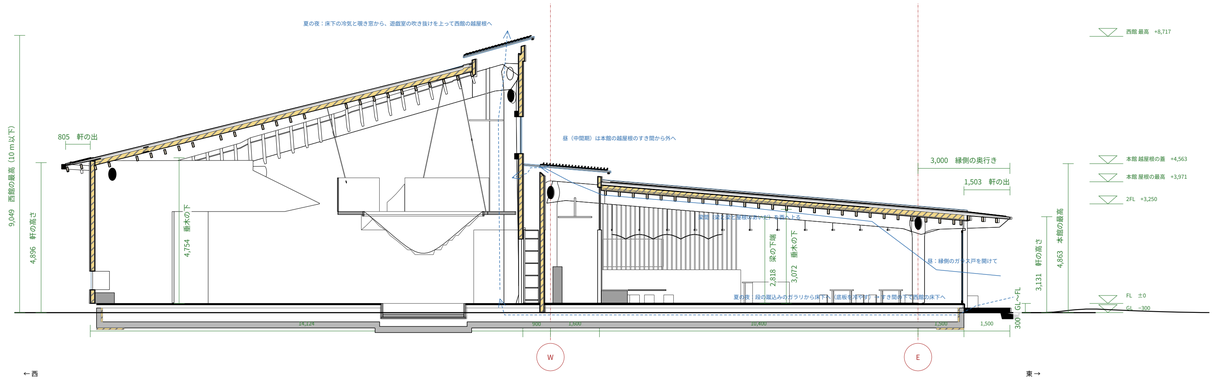

断面図 A（縦断・展開）・B・C　1/100（A1）