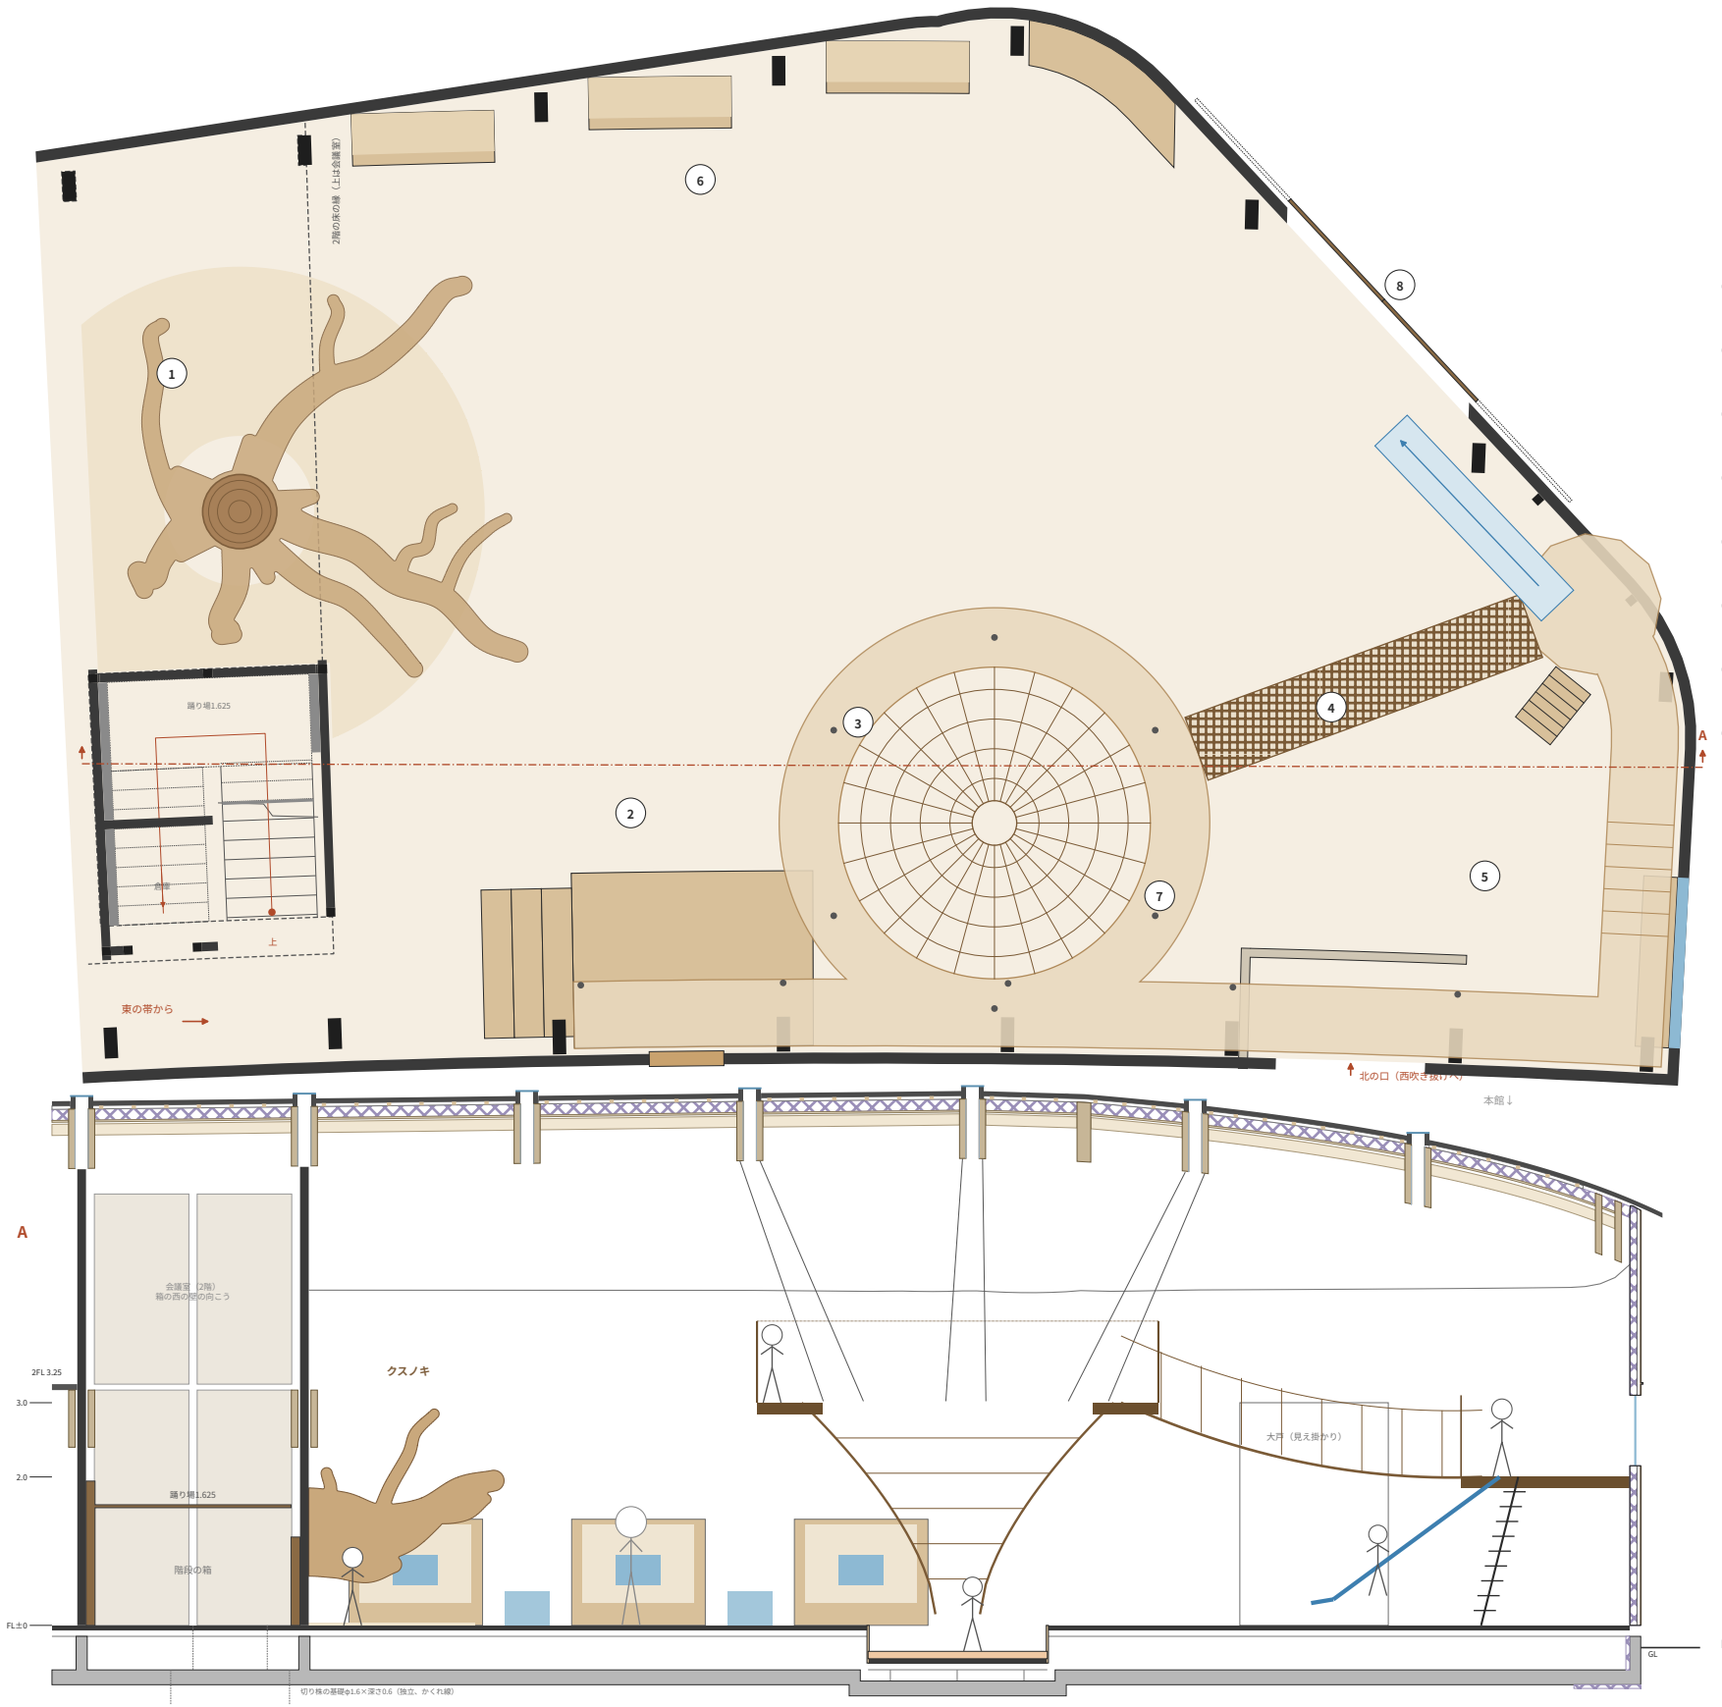


平面・断面A 1/100

平面はFL+1.2で切る。淡い茶はキャットウォーク・輪・踊り場（h3.0／2.0）、黒い点は吊り材。
断面Aは東から4.3で切って西を見る（階段の箱の踊り場を通る）

遊び方

1. 洞とクスノキ
てっぺんが2階の床に届く
2. デッキと登り壁
→キャットウォークh3.0
3. 摺鉢ネットと穴の底
ネットからも輪へ登れる
4. 輪→網の吊り橋→踊り場h2.0
空中で一周する
5. 北の段3.0→2.0・はしご・
すべり台（落下2.0 m以下）
6. ひだ：くぼみ・丸いベンチ・
窓辺の腰掛け（モミジを見る）
7. 北の口のついたて（吸音）
8. 搬入の大戸（外付けの引き戸）

安全

手すりは縦格子h1.1・すき間90
（頭が通らない、横桟なし）
床の板のすき間8未満
網目は上90・下50、ロープφ18

支え方

重さは梁から吊る（梁のあいだを
通す、吊り材M20）。横の揺れは壁と
ハの字の吊り材で止め、吊り橋だけ
揺れる。吊り橋の引きはキャットウォーク
との閉じた輪で受ける。梁90×800×2
（強い集成材）は満員でも持つ

音

階段の箱がホールとの衝立。
北の口に吸音のついたて、
東の嚊き窓は夜だけ開く

断面の構成

屋根：屋根材・野地64／通気垂木45／
　断熱150（梁のあいだ）／構造用合板t24
　（天井に現す）／母屋60×150（現し）
外壁（約150）：杉の大和張り・通気層・
　構造用合板（耐力壁）・断熱
床：スギ板t30＋合板t28／大引90・
　鋼製束／床下約450／ベタ基礎の
　底板t200（基礎断熱の内側）

北

0　5 m