平面図　1階　FL+1500 で切断／2階（西館）2FL+1000 で切断　1/100

高野川を下に（配置図と同じ向き）。2階は西の道路の外に同じ向きで置いた（遊戯室は吹き抜けから見下ろす）。一点鎖線は敷地の境。二点鎖線は切断より上にある物（屋根の外形・越屋根・2階の床の縁など）

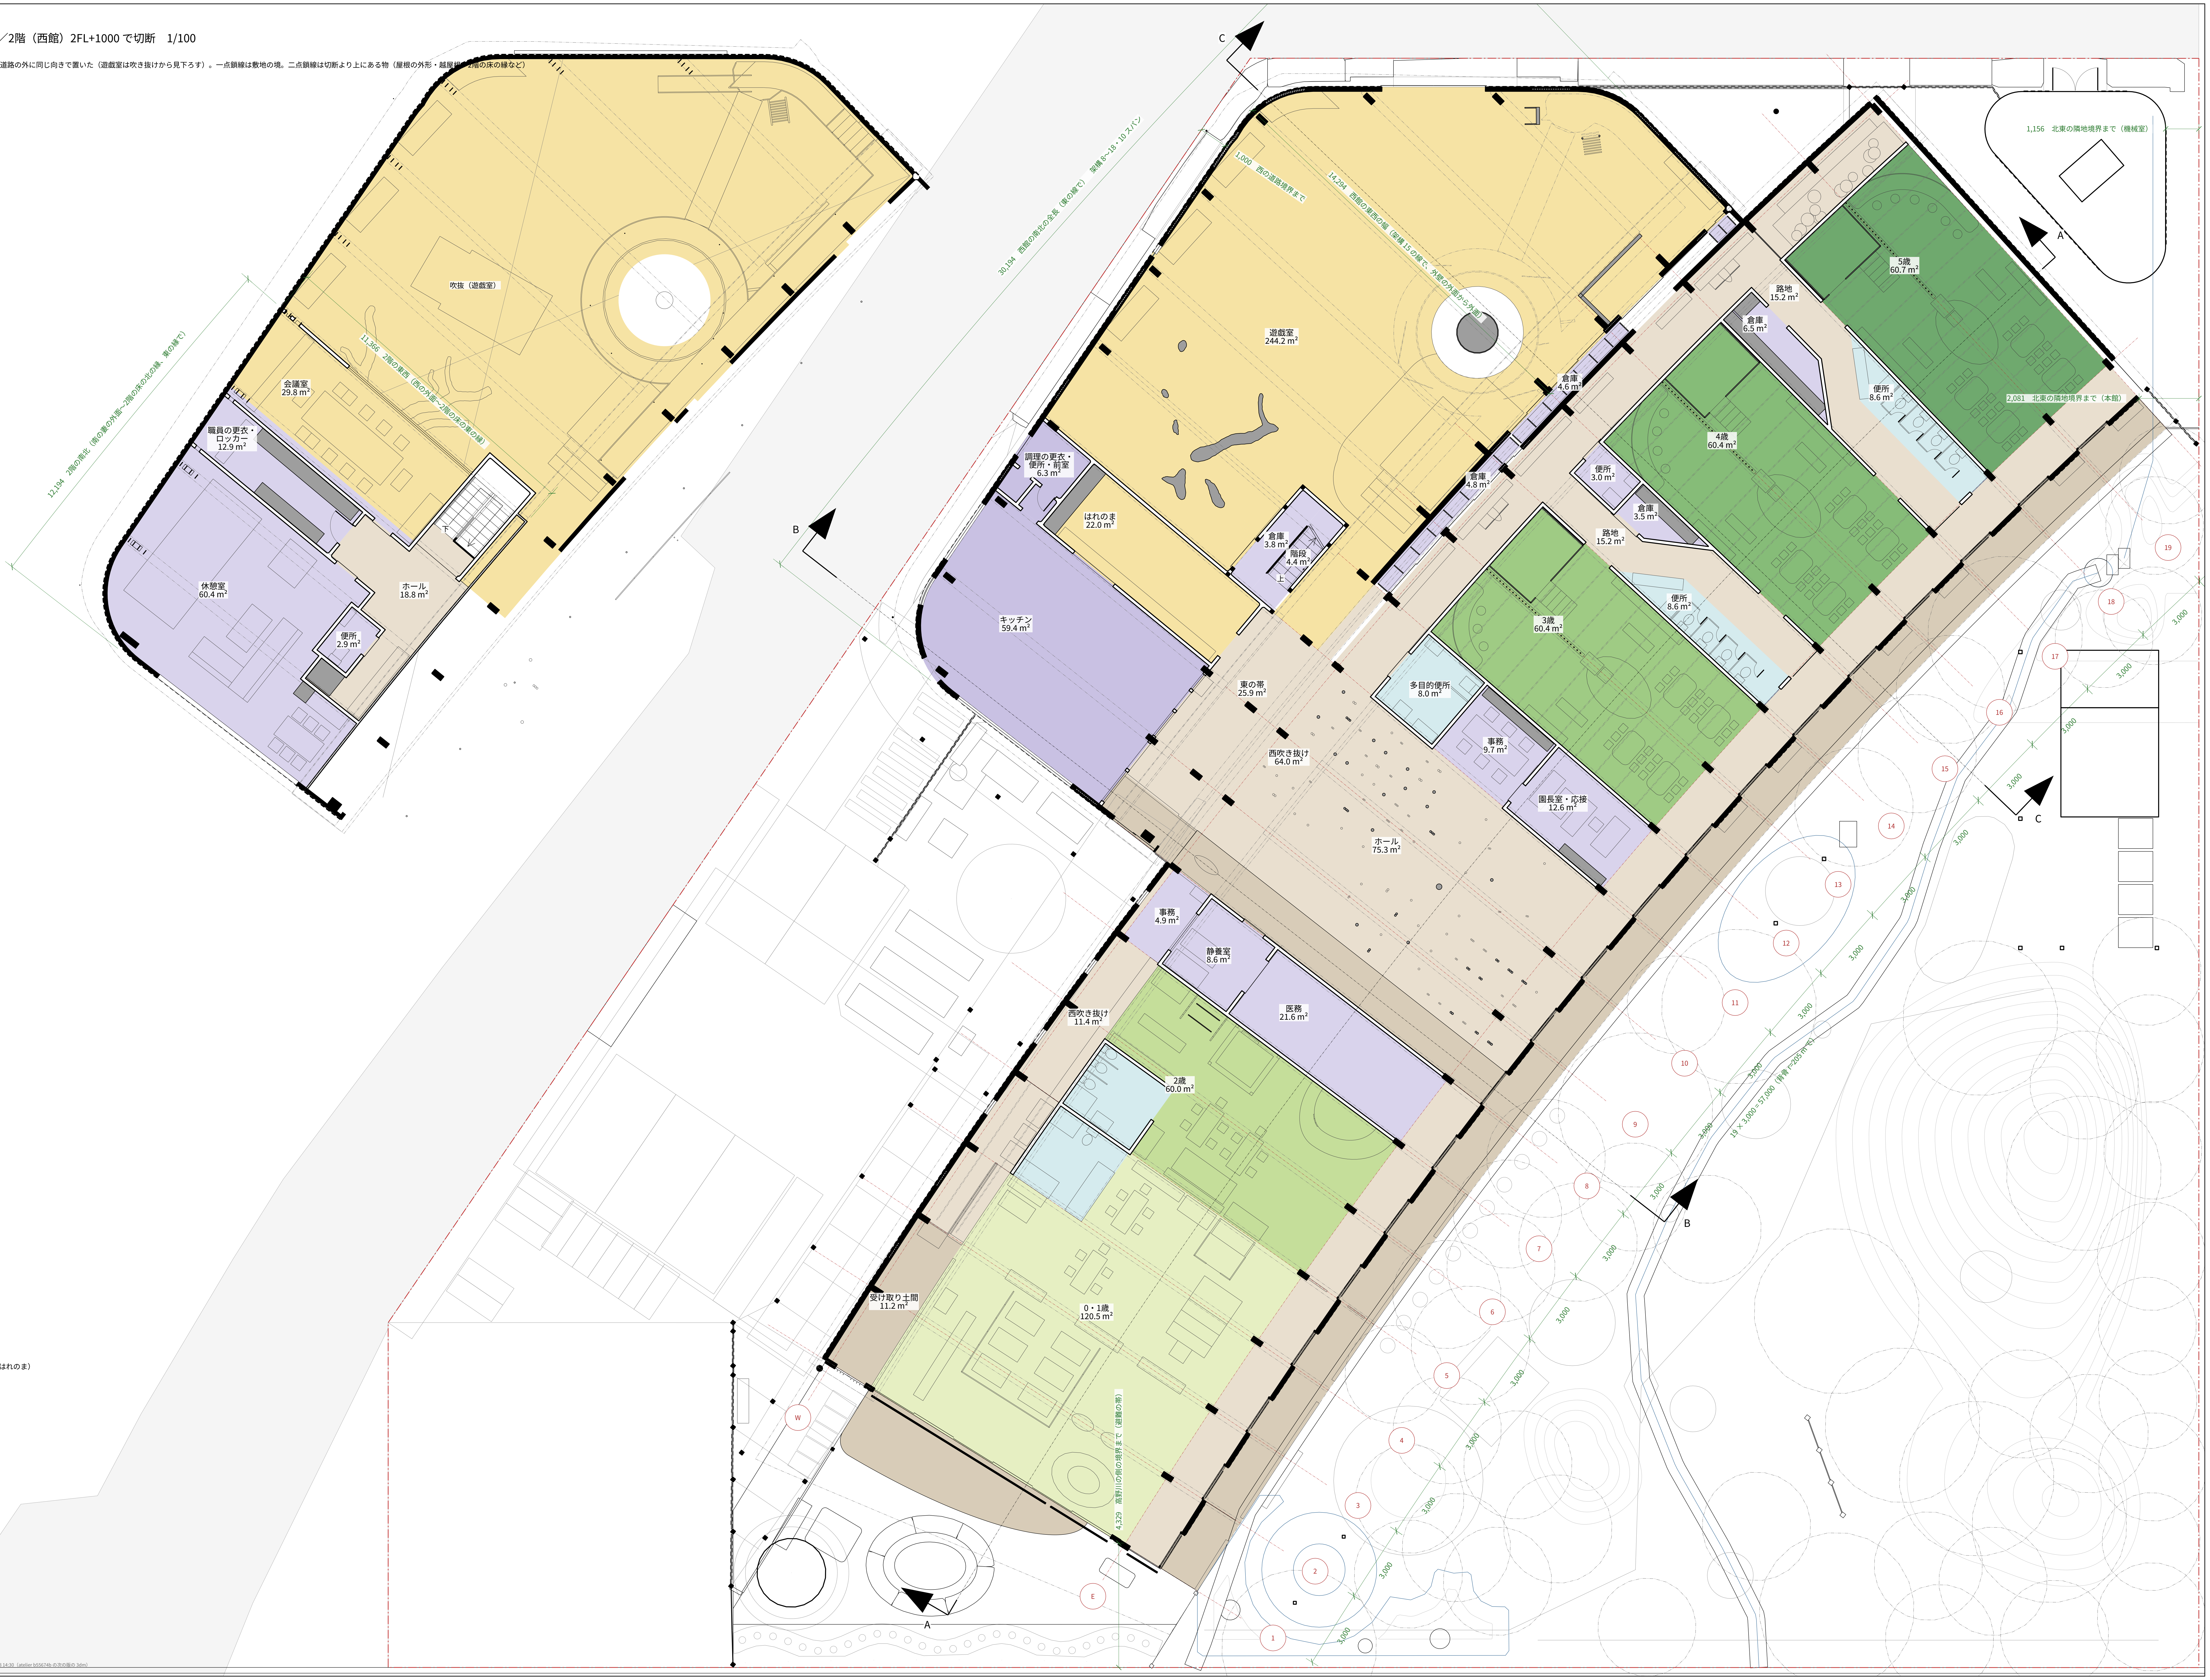

部屋の色

🟩 0・1歳〜5歳

▨ こどものみんなの場所（遊戯室・はれのま）

▨ 通り・つなぐ場所（はだし）

▨ 土足の床

▨ 大人の場所

▨ キッチン・調理の更衣

▨ 水まわり

0　5 m

こどもたちの育ち舎　3dm（sodachiya.3dm）から自動で作図　2026-10-28 14:30（atelier b55674b の次の版の 3dm）