平面図　1階　FL+1500 で切断／2階（西館）2FL+1000 で切断　1/100

高野川を下に（配置図と同じ向き）。2階は西の道路の外に同じ向きで置いた（遊戯室は吹き抜けから見下ろす）。一点鎖線は敷地の境。二点鎖線は切断より上にある物（屋根の外形・越屋根・2階の床の縁など）

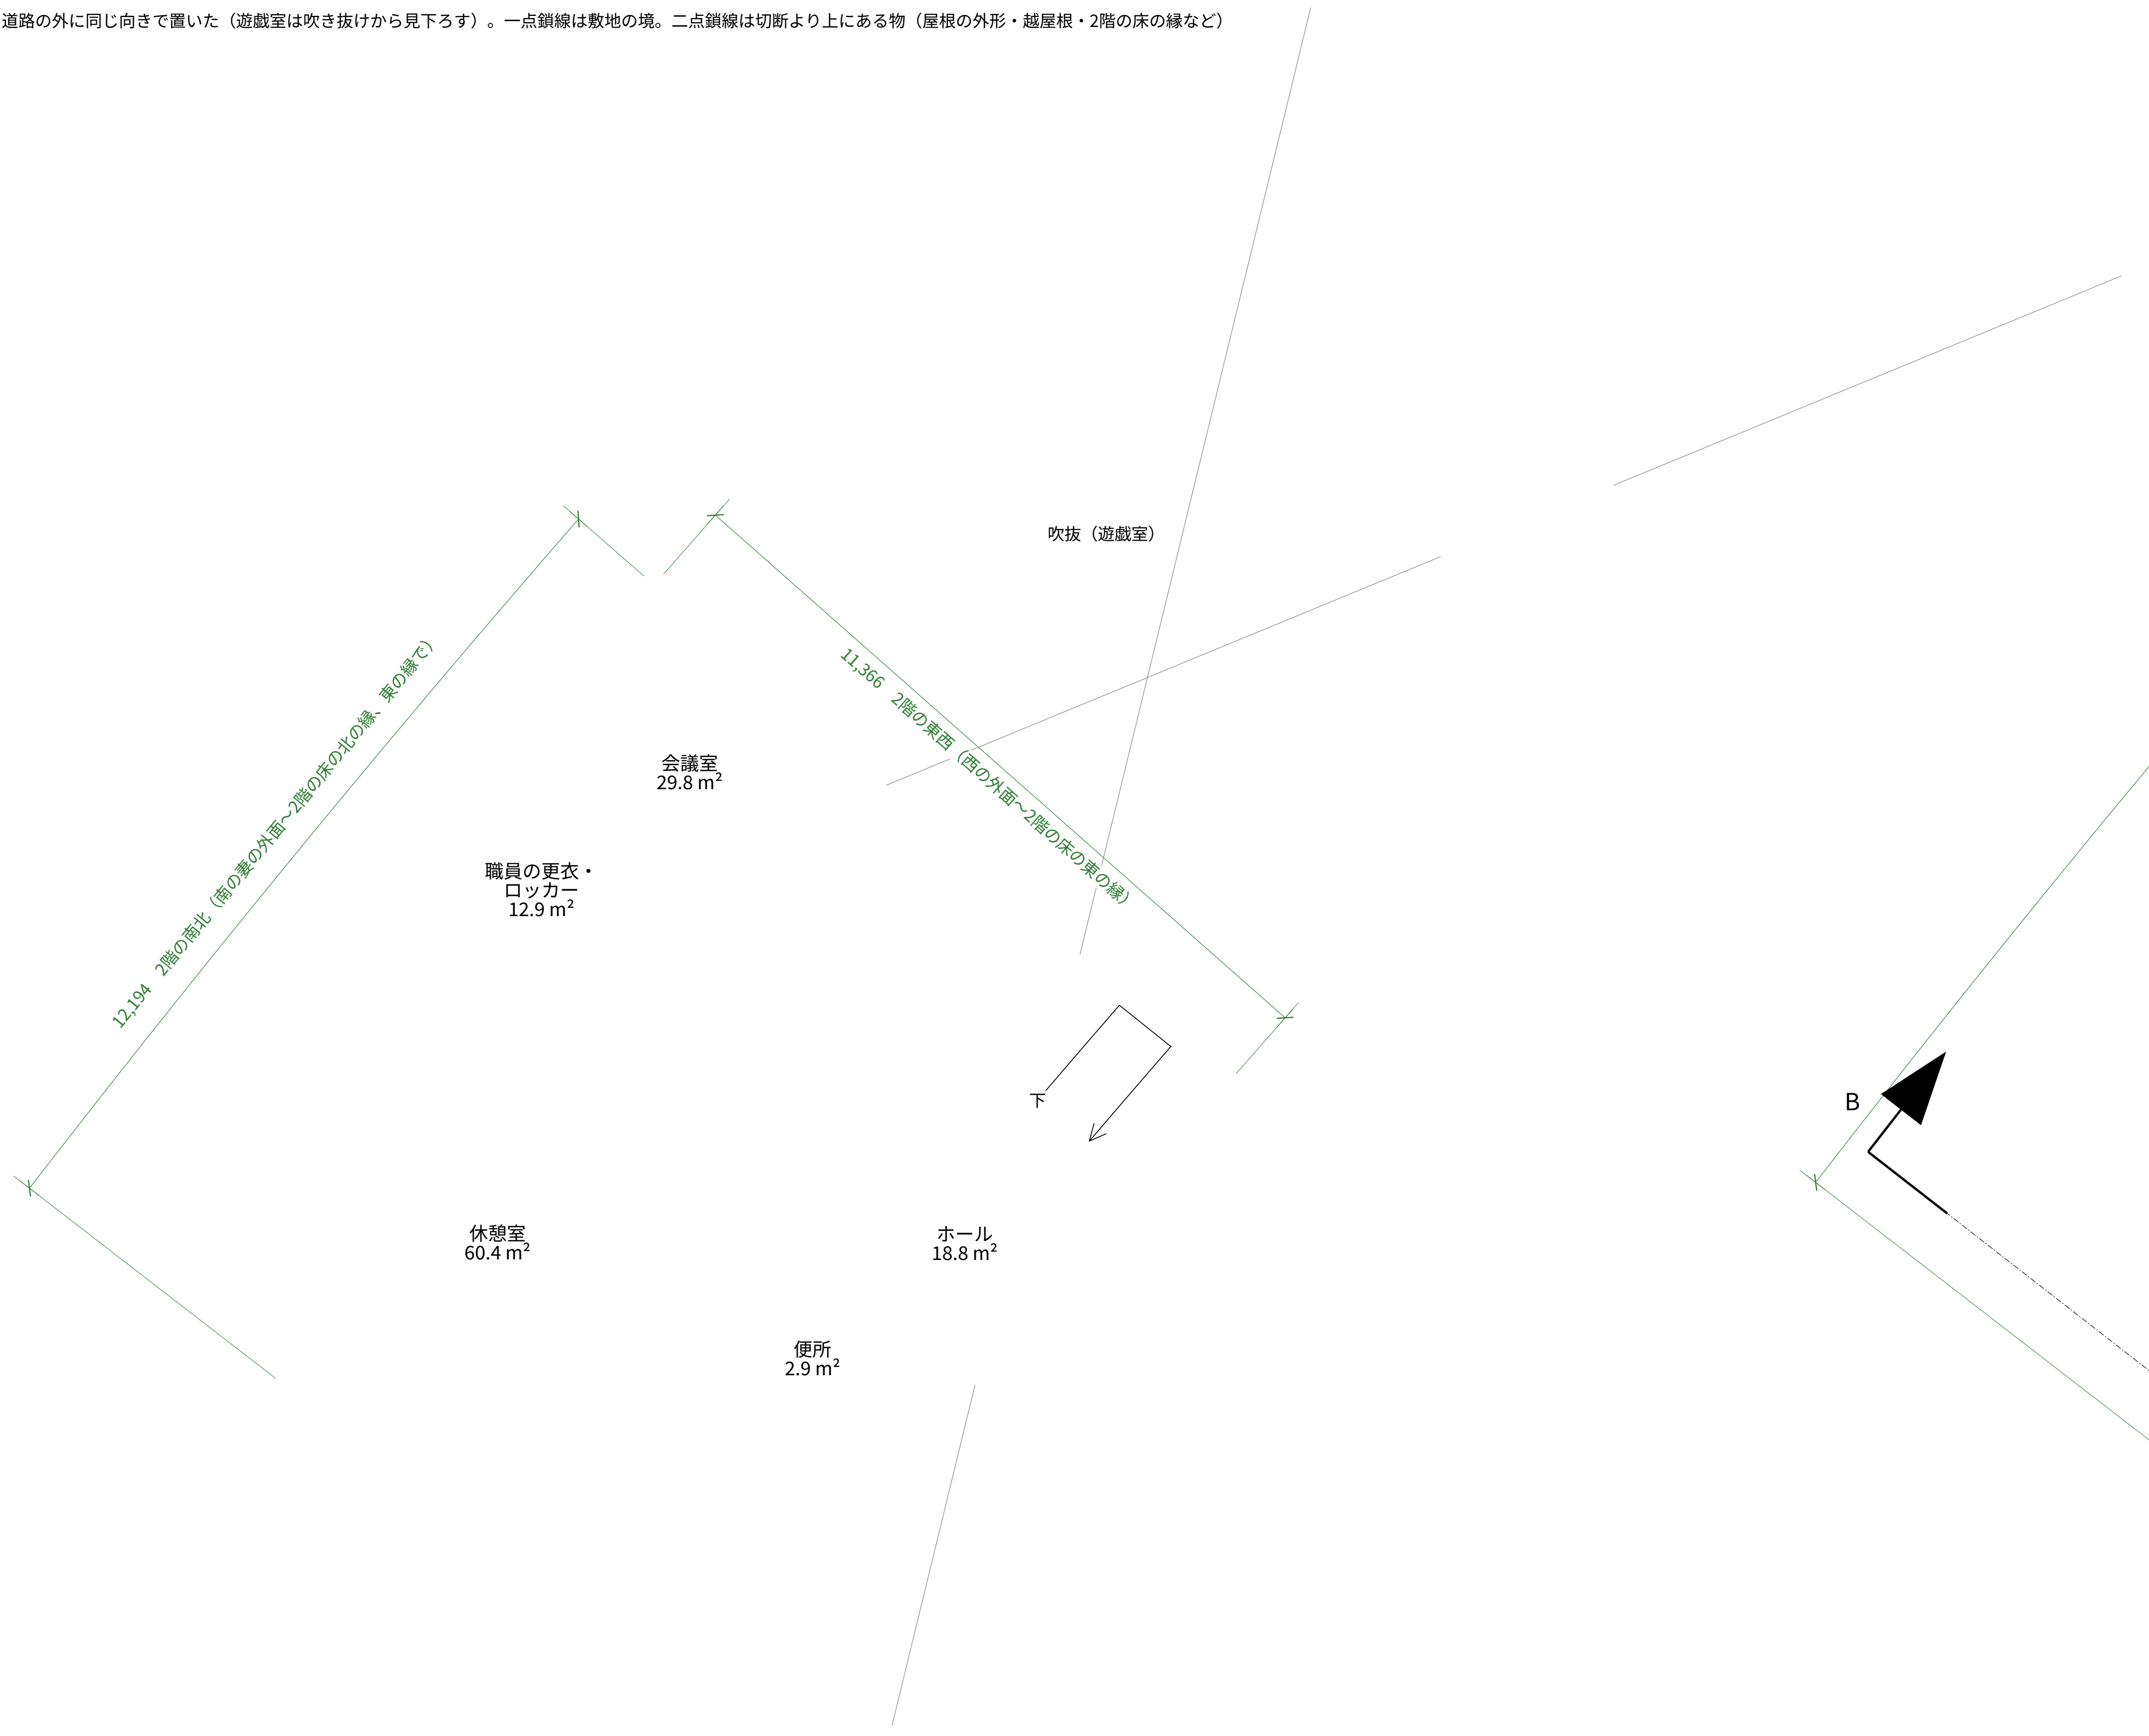
吹抜（遊戯室）
12,194　2階の南北（南の妻の外面〜2階の床の北の縁、東の縁で）
11,366　2階の東西（西の外面〜2階の床の東の縁）
会議室
29.8 m²
職員の更衣・
ロッカー
12.9 m²
下
休憩室
60.4 m²
ホール
18.8 m²
便所
2.9 m²

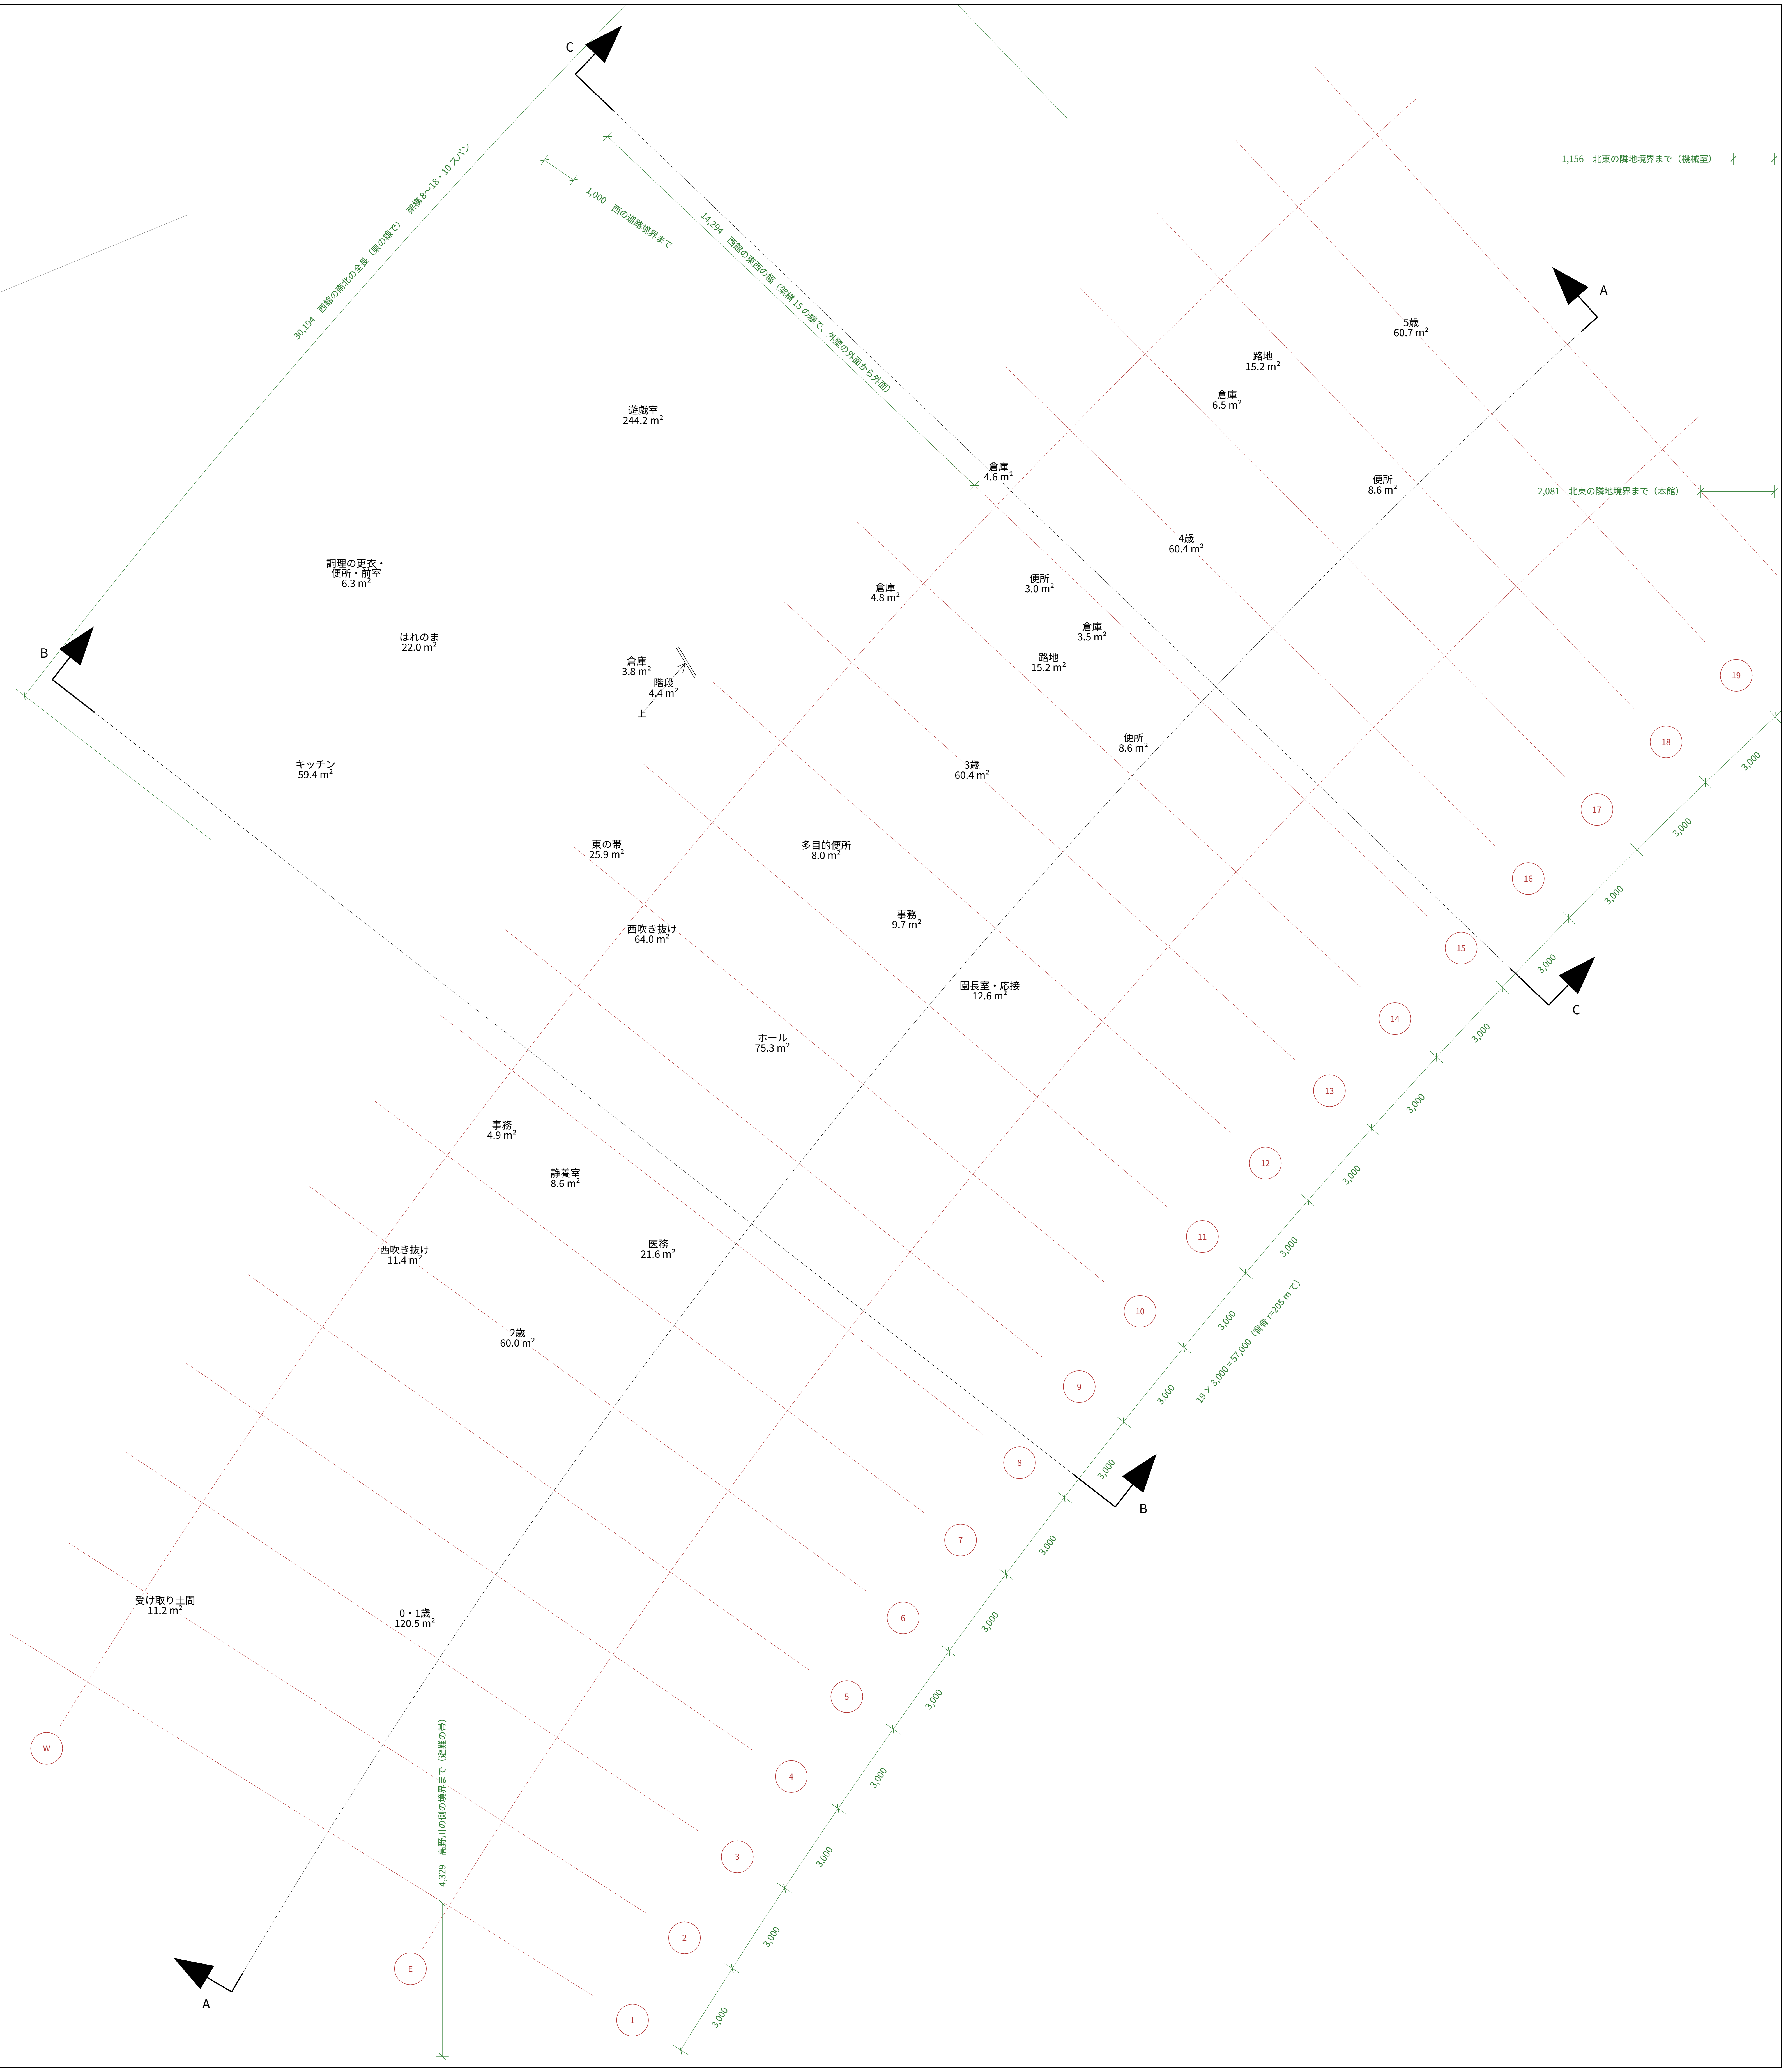

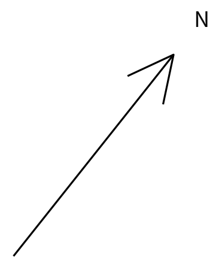

部屋の色

🟩	0・1歳〜5歳
🟨	こどものみんなの場所（遊戯室・はれのま）
▨	通り・つなぐ場所（はだし）
▨	土足の床
🟪	大人の場所
🟪	キッチン・調理の更衣
▨	水まわり

0　5 m

こどもたちの育ち舎　3dm（sodachiya.3dm）から自動で作図　2026-10-28 14:30（atelier b55674b の次の版の 3dm）