壁に貼ったとき　3列：1 ｜ 2・3 ｜ 4・5（1は二段の真ん中）

目の高さ1.5 m

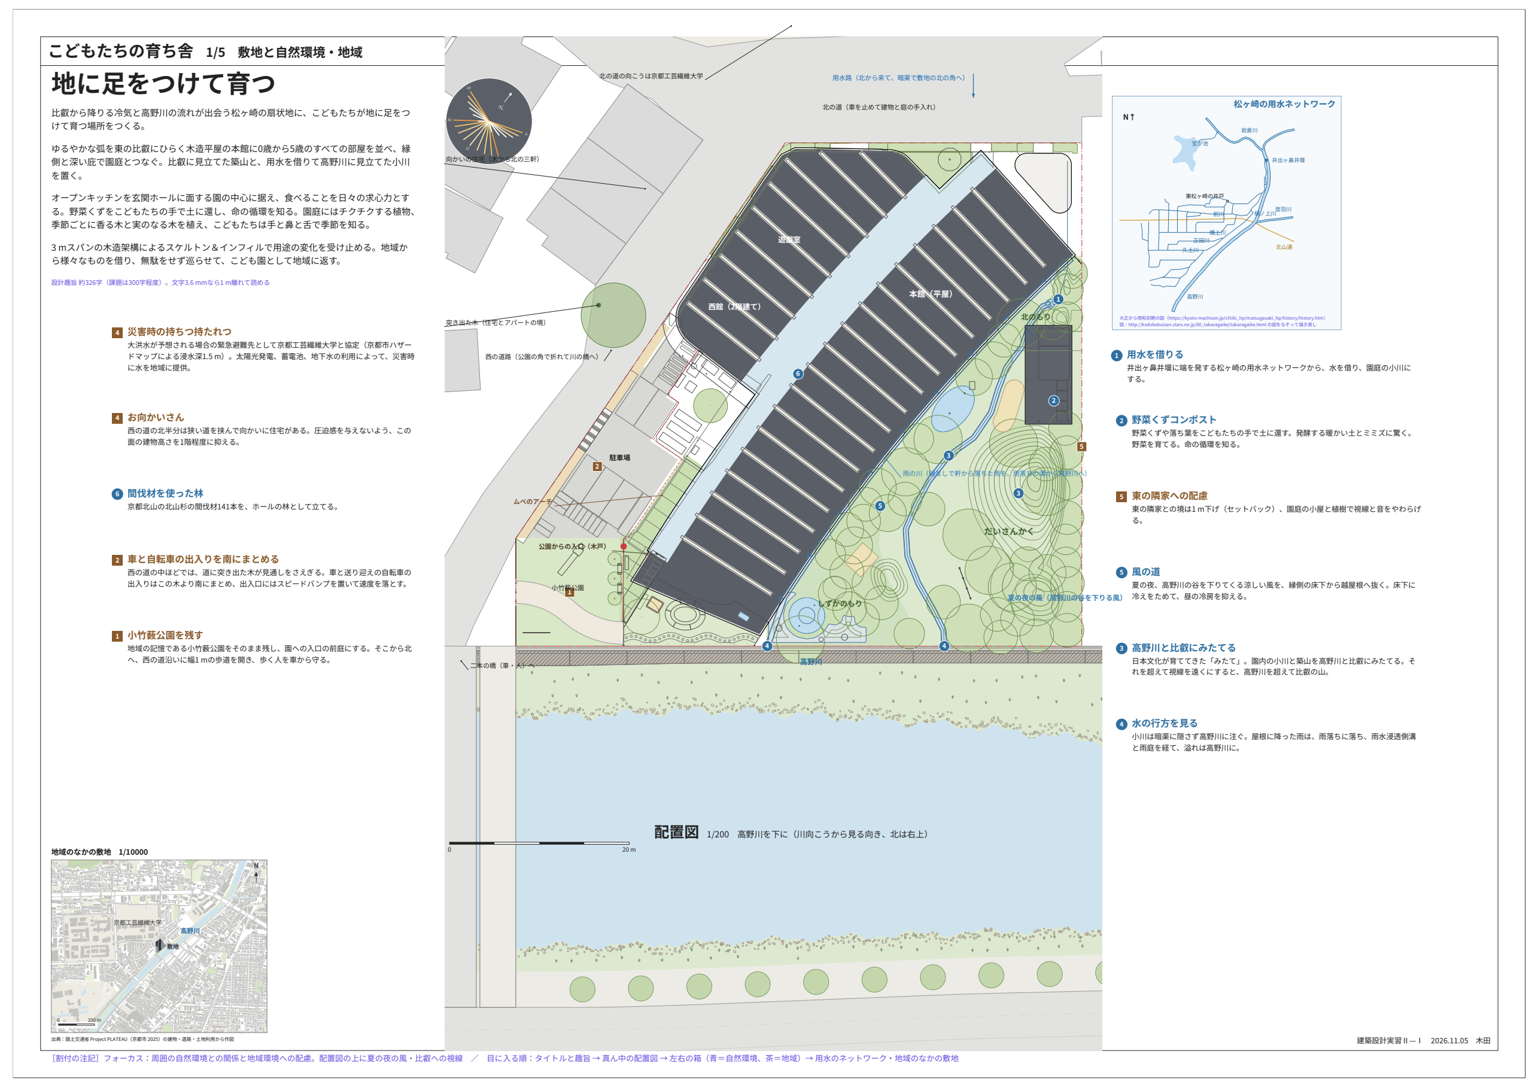
こどもたちの育ち舎　1/5　敷地と自然環境・地域

地に足をつけて育つ

配置図　1/200

1　敷地と自然環境・地域（二段の真ん中）。

その右に2　景観（立面図1/100、下の段に沿川の景観立面）、その下に3　断面と環境（断面図1/100）。

その右に4　平面図、その下に5　動線とこどもたちの環境（一日の帯は平面図の続き）。

外から中へ：敷地→外から見た姿と切った姿→中の平面と暮らし。

2・3・4枚目の立面・断面・平面は3dmから自動の図を実寸で貼る。

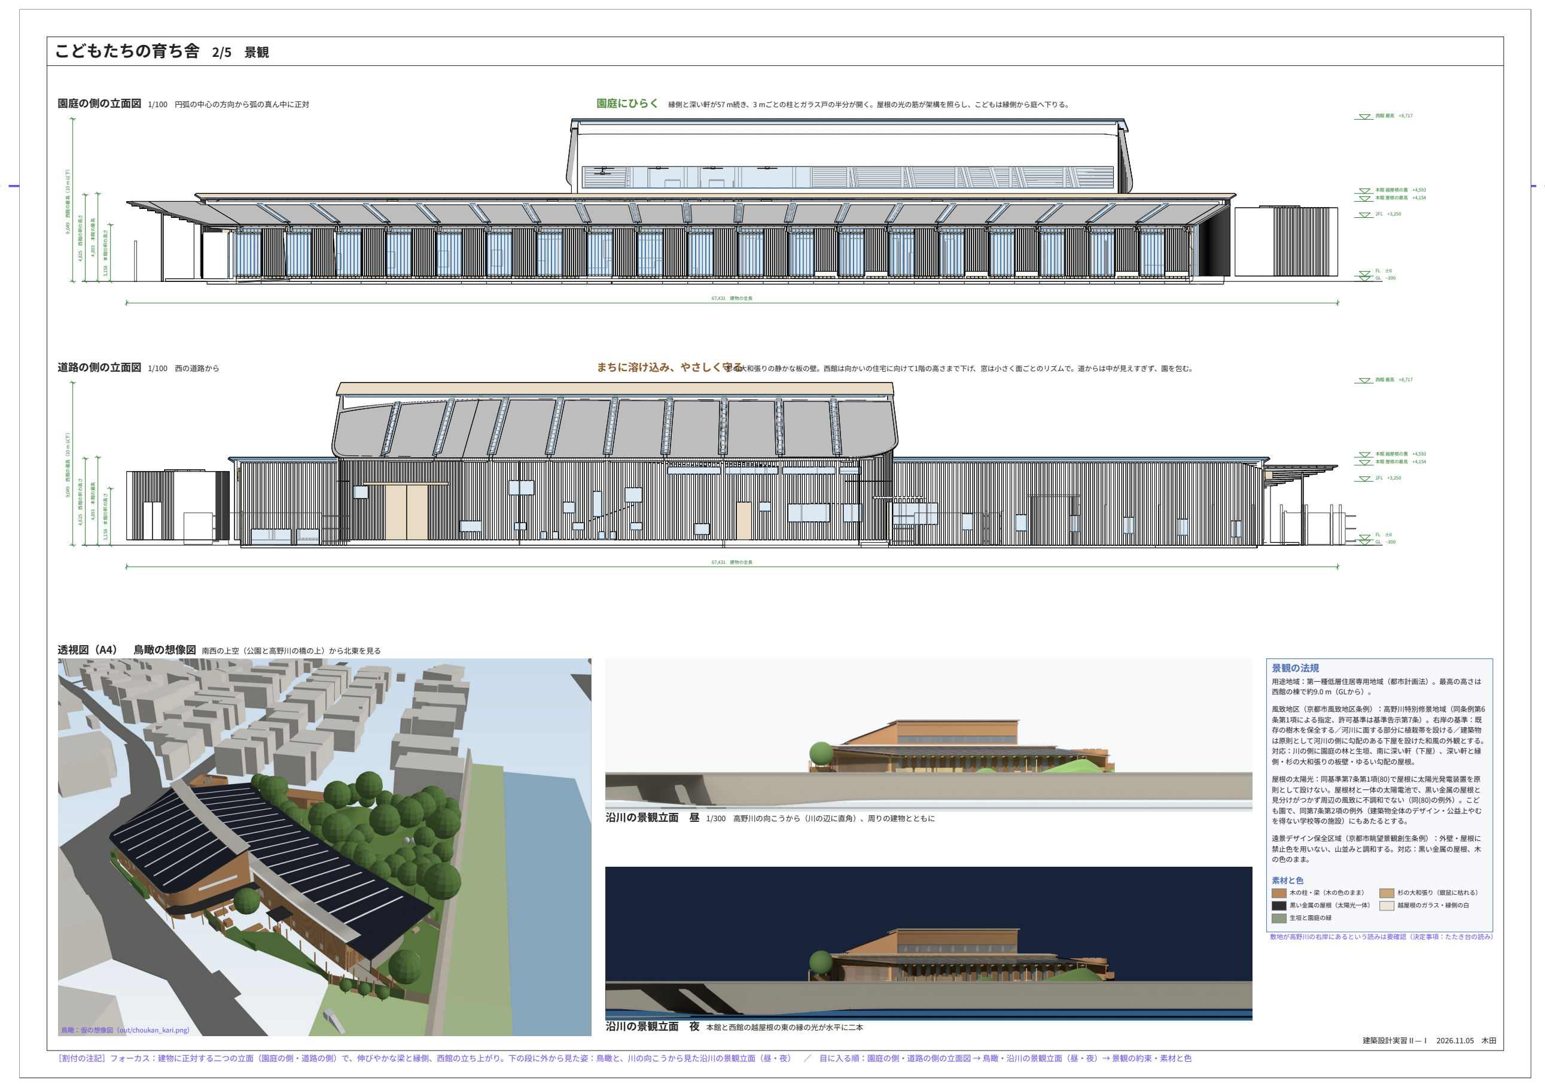
こどもたちの育ち舎　2/5　景観

園庭の側の立面図　1/100

園庭にひらく

道路の側の立面図　1/100　西の道路から

まちに溶け込み、やさしく守る

透視図（A4）　鳥瞰の想像図

沿川の景観立面　昼　1/300

沿川の景観立面　夜

景観の法規

素材と色

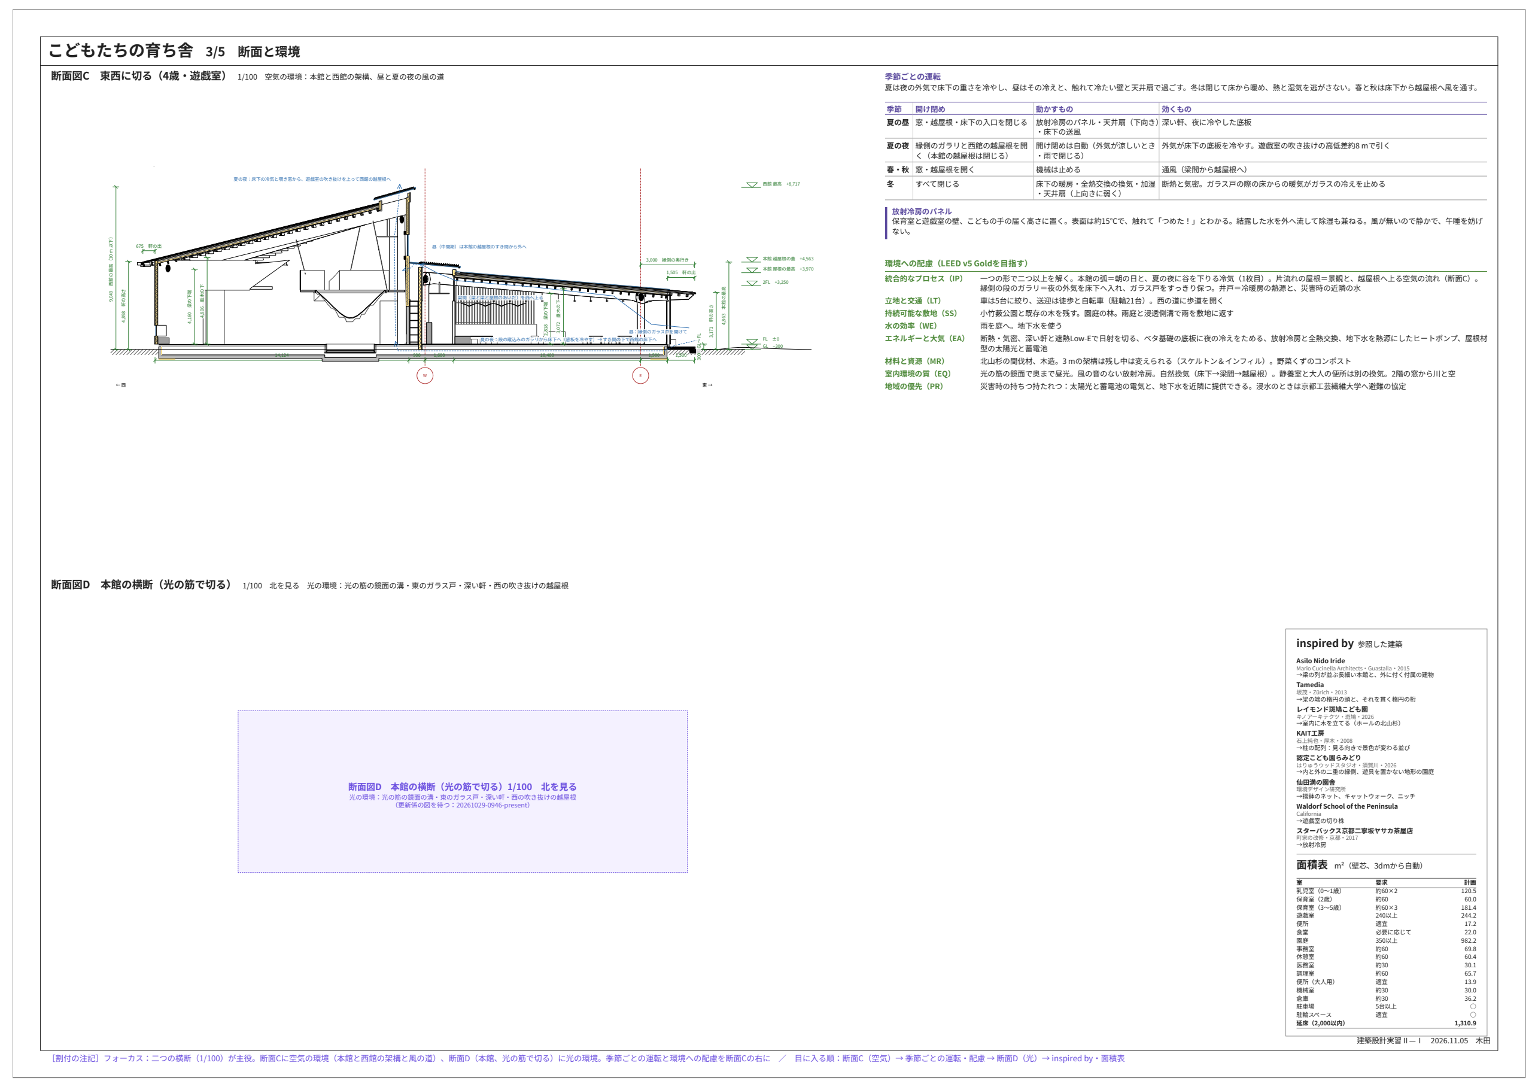
こどもたちの育ち舎　3/5　断面と環境

断面図C　東西に切る（4歳・遊戯室）　1/100

季節ごとの運転

環境への配慮（LEED v5 Goldを目指す）

断面図D　本館の横断（光の筋で切る）　1/100　北を見る

inspired by

面積表

こどもたちの育ち舎　4/5　平面図　1階・2階

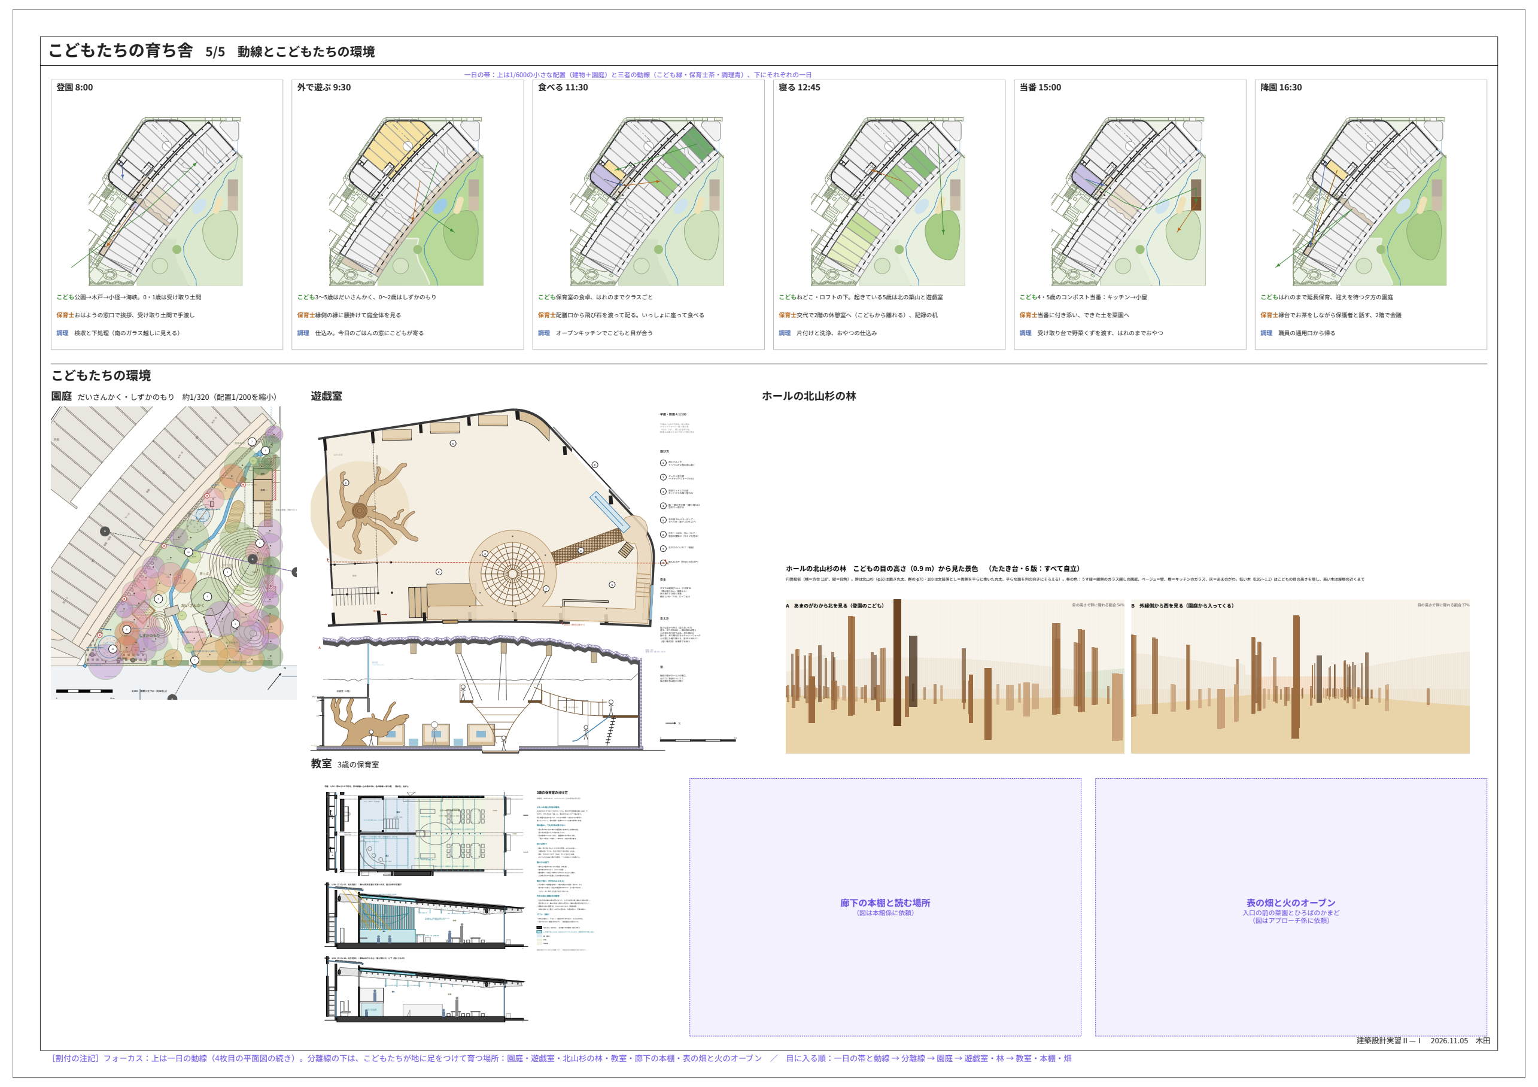
こどもたちの育ち舎　5/5　動線とこどもたちの環境

こどもたちの環境

園庭

遊戯室

ホールの北山杉の林

教室

廊下の本棚と読む場所

表の畑と火のオーブン

床