
西館 2 階平面図　2FL+1200 で切断　1/100（梁は破線）

1 階平面図　FL+1200 で切断　1/100　（右が北の端、下が園庭）

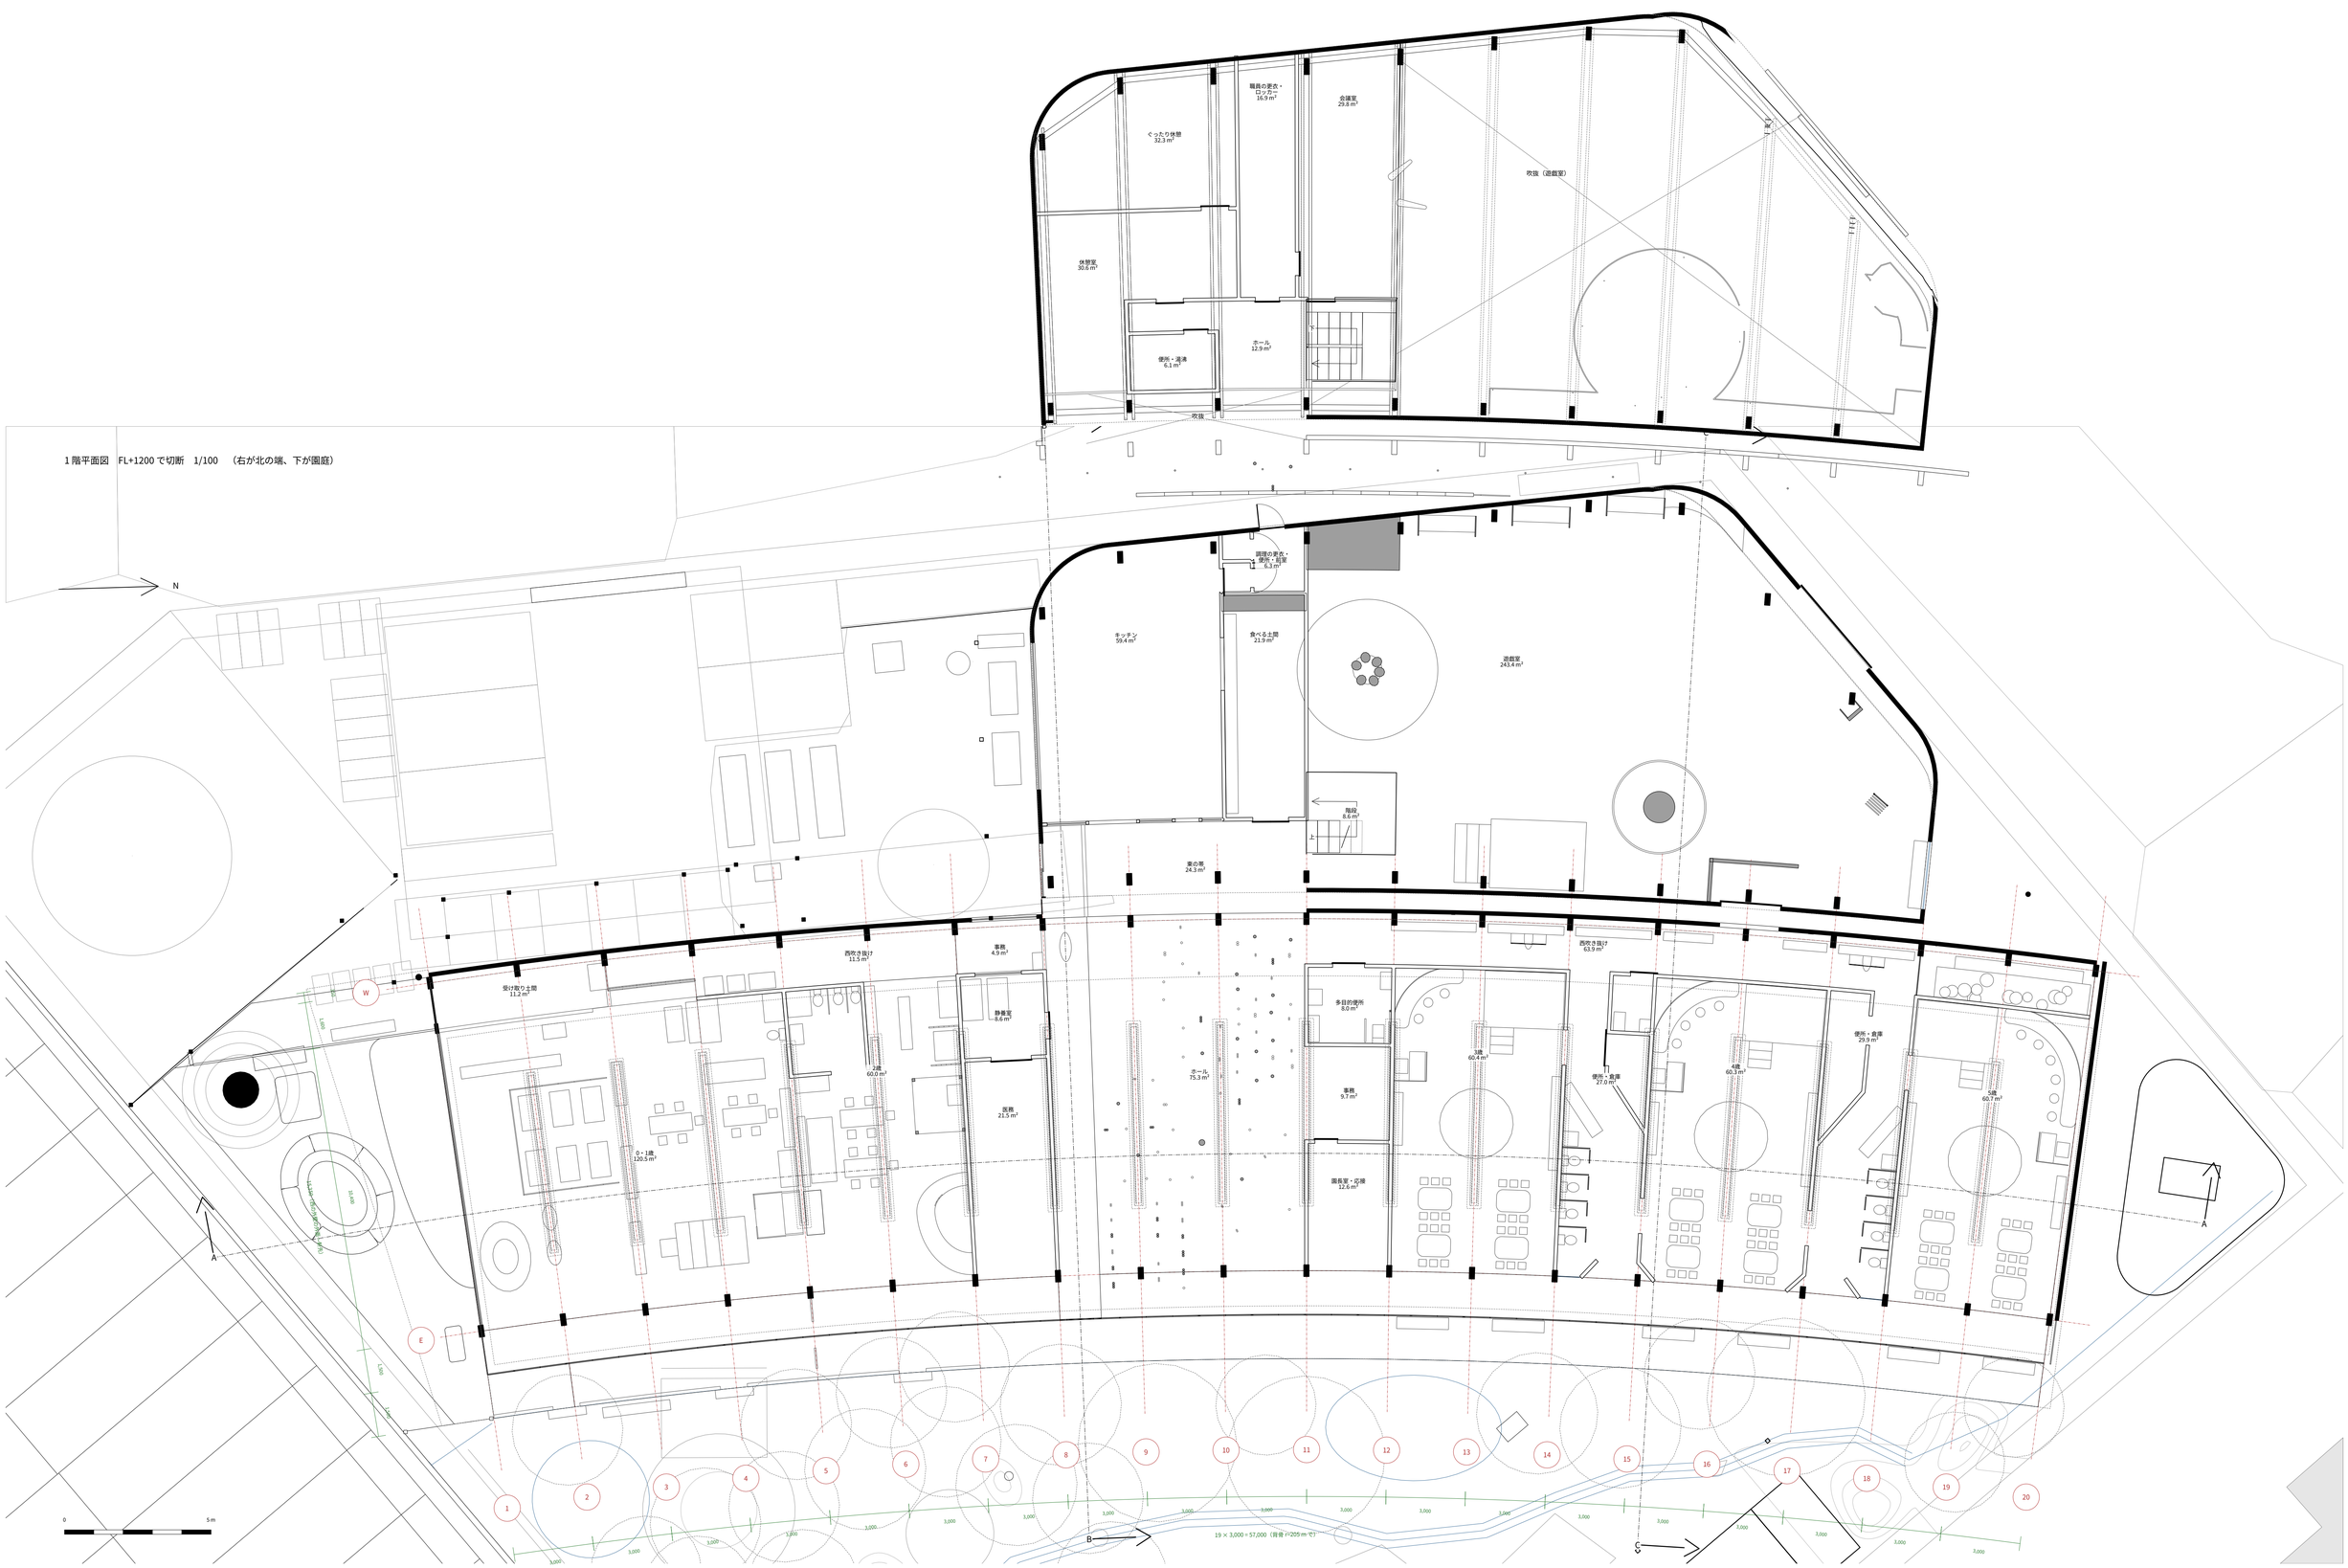

1 階平面図・西館 2 階平面図　1/100（A1）　建物の軸に合わせて回してある（北は方位の矢印）