配置図　1/200

駐車 5台（うち搬入 1）・乗入れ 1か所
歩道（開放）敷地の境から 1.0、公園の上の端〜食材納品場
駐輪 保護者 11台・職員 9台

保護者・来客の出入口は公園の木戸だけ（赤い破線＝セキュリティの線）。
送り迎えは徒歩と自転車が前提。車は南（川沿い）から入り、駐車 5台（うち搬入 1）。行事の日は駐車場を駐輪に。
高野川沿いは緑の目隠し h1.5（ムベ）。上は開けて本館の南の妻の架構を見せる。
避難の帯 1.5（平らで固い芝）から非常用の門を通って公園へ。
西の道路沿いの敷地の境から 1.0 は歩道として開放（公園の上の端〜食材納品場）。車路の前はスピードバンプが歩道を続ける。

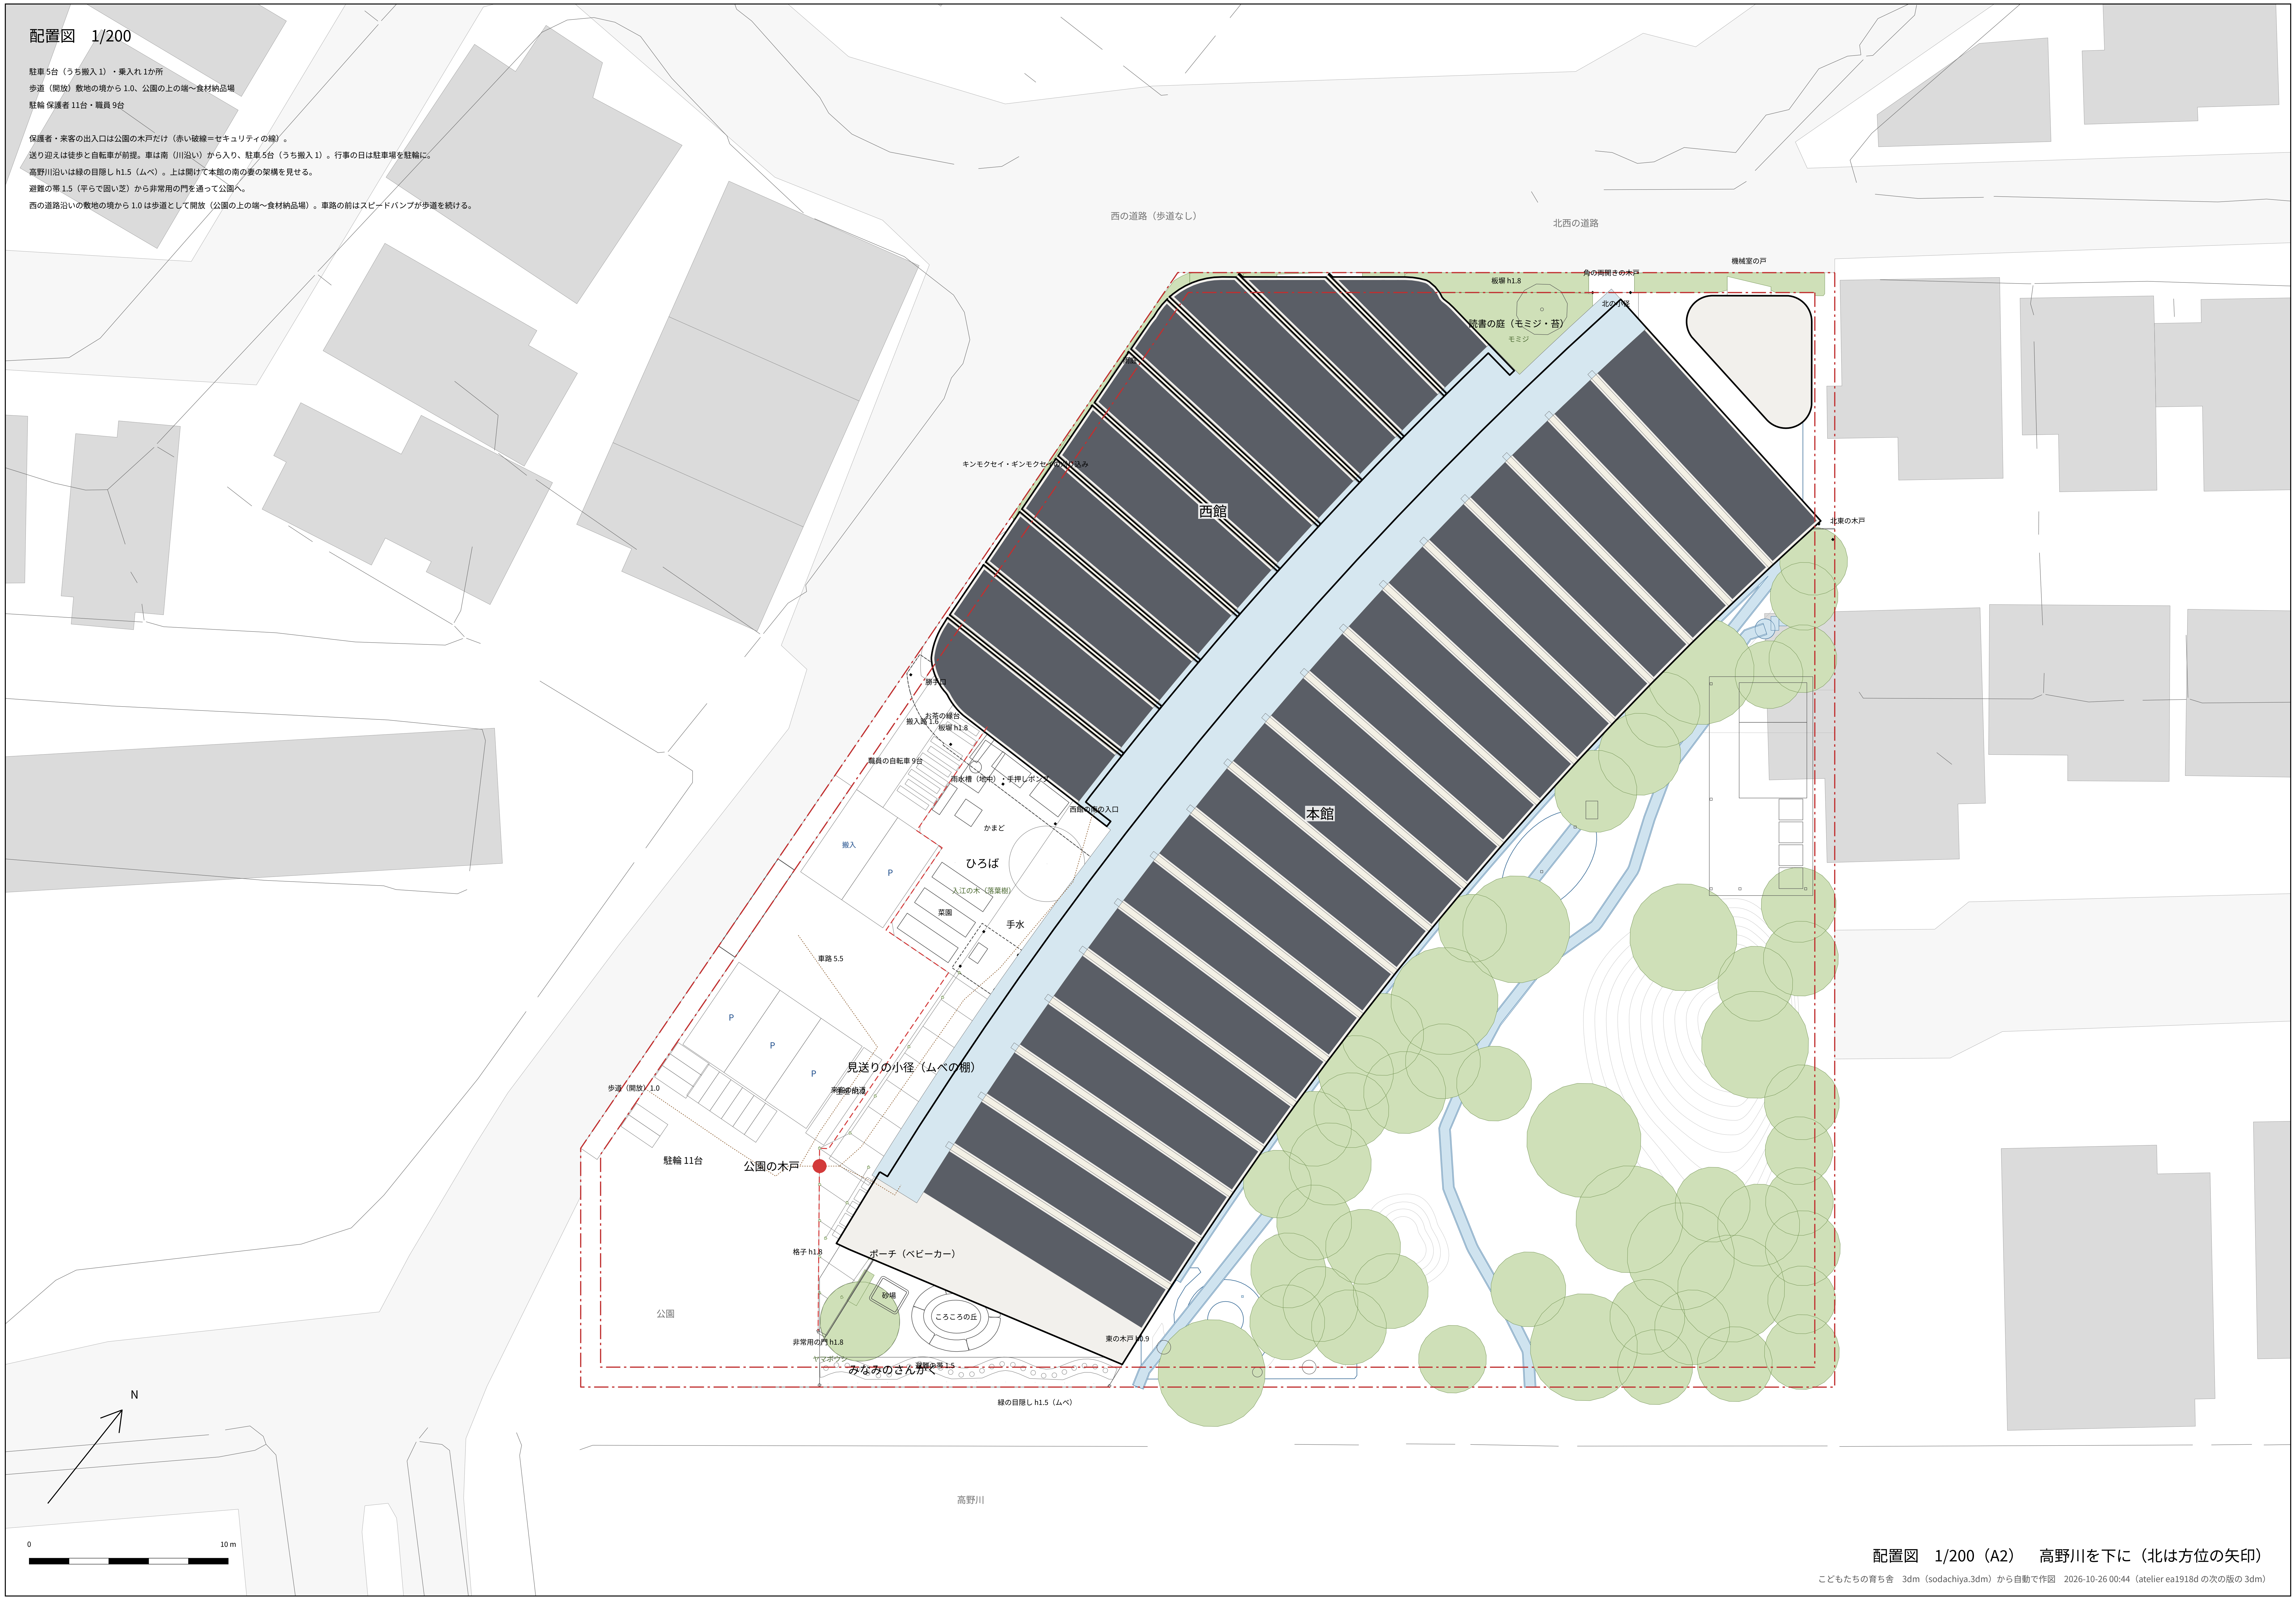
西の道路（歩道なし）
北西の道路
機械室の戸
角の両開きの木戸
板塀 h1.8
北の小径
読書の庭（モミジ・苔）
モミジ
雨庭
キンモクセイ・ギンモクセイの刈り込み
西館
本館
北東の木戸
勝手口
お茶の縁台
搬入路 1.6
板塀 h1.8
職員の自転車 9台
雨水槽（地中）・手押しポンプ
西館の南の入口
かまど
搬入
P
ひろば
入江の木（落葉樹）
菜園
手水
車路 5.5
P
P
P
見送りの小径（ムベの棚）
歩道（開放）1.0
来客の歩道
生垣 h1.2
駐輪 11台
公園の木戸
格子 h1.8
ポーチ（ベビーカー）
公園
砂場
ころころの丘
非常用の門 h1.8
ヤマボウシ
東の木戸 h0.9
避難の帯 1.5
みなみのさんかく
緑の目隠し h1.5（ムベ）
N
高野川
0
10 m

配置図　1/200（A2）　高野川を下に（北は方位の矢印）

こどもたちの育ち舎　3dm（sodachiya.3dm）から自動で作図　2026-10-26 00:44（atelier ea1918d の次の版の 3dm）