
平面図　1階　FL+1500 で切断／2階（西館）2FL+1000 で切断　1/100

高野川を下に（配置図と同じ向き）。2階は西の道路の外に同じ向きで置いた（遊戯室は吹き抜けから見下ろす）。一点鎖線は敷地の境。二点鎖線は切断より上にある物（屋根の外形・越屋根・2階の床の縁など）

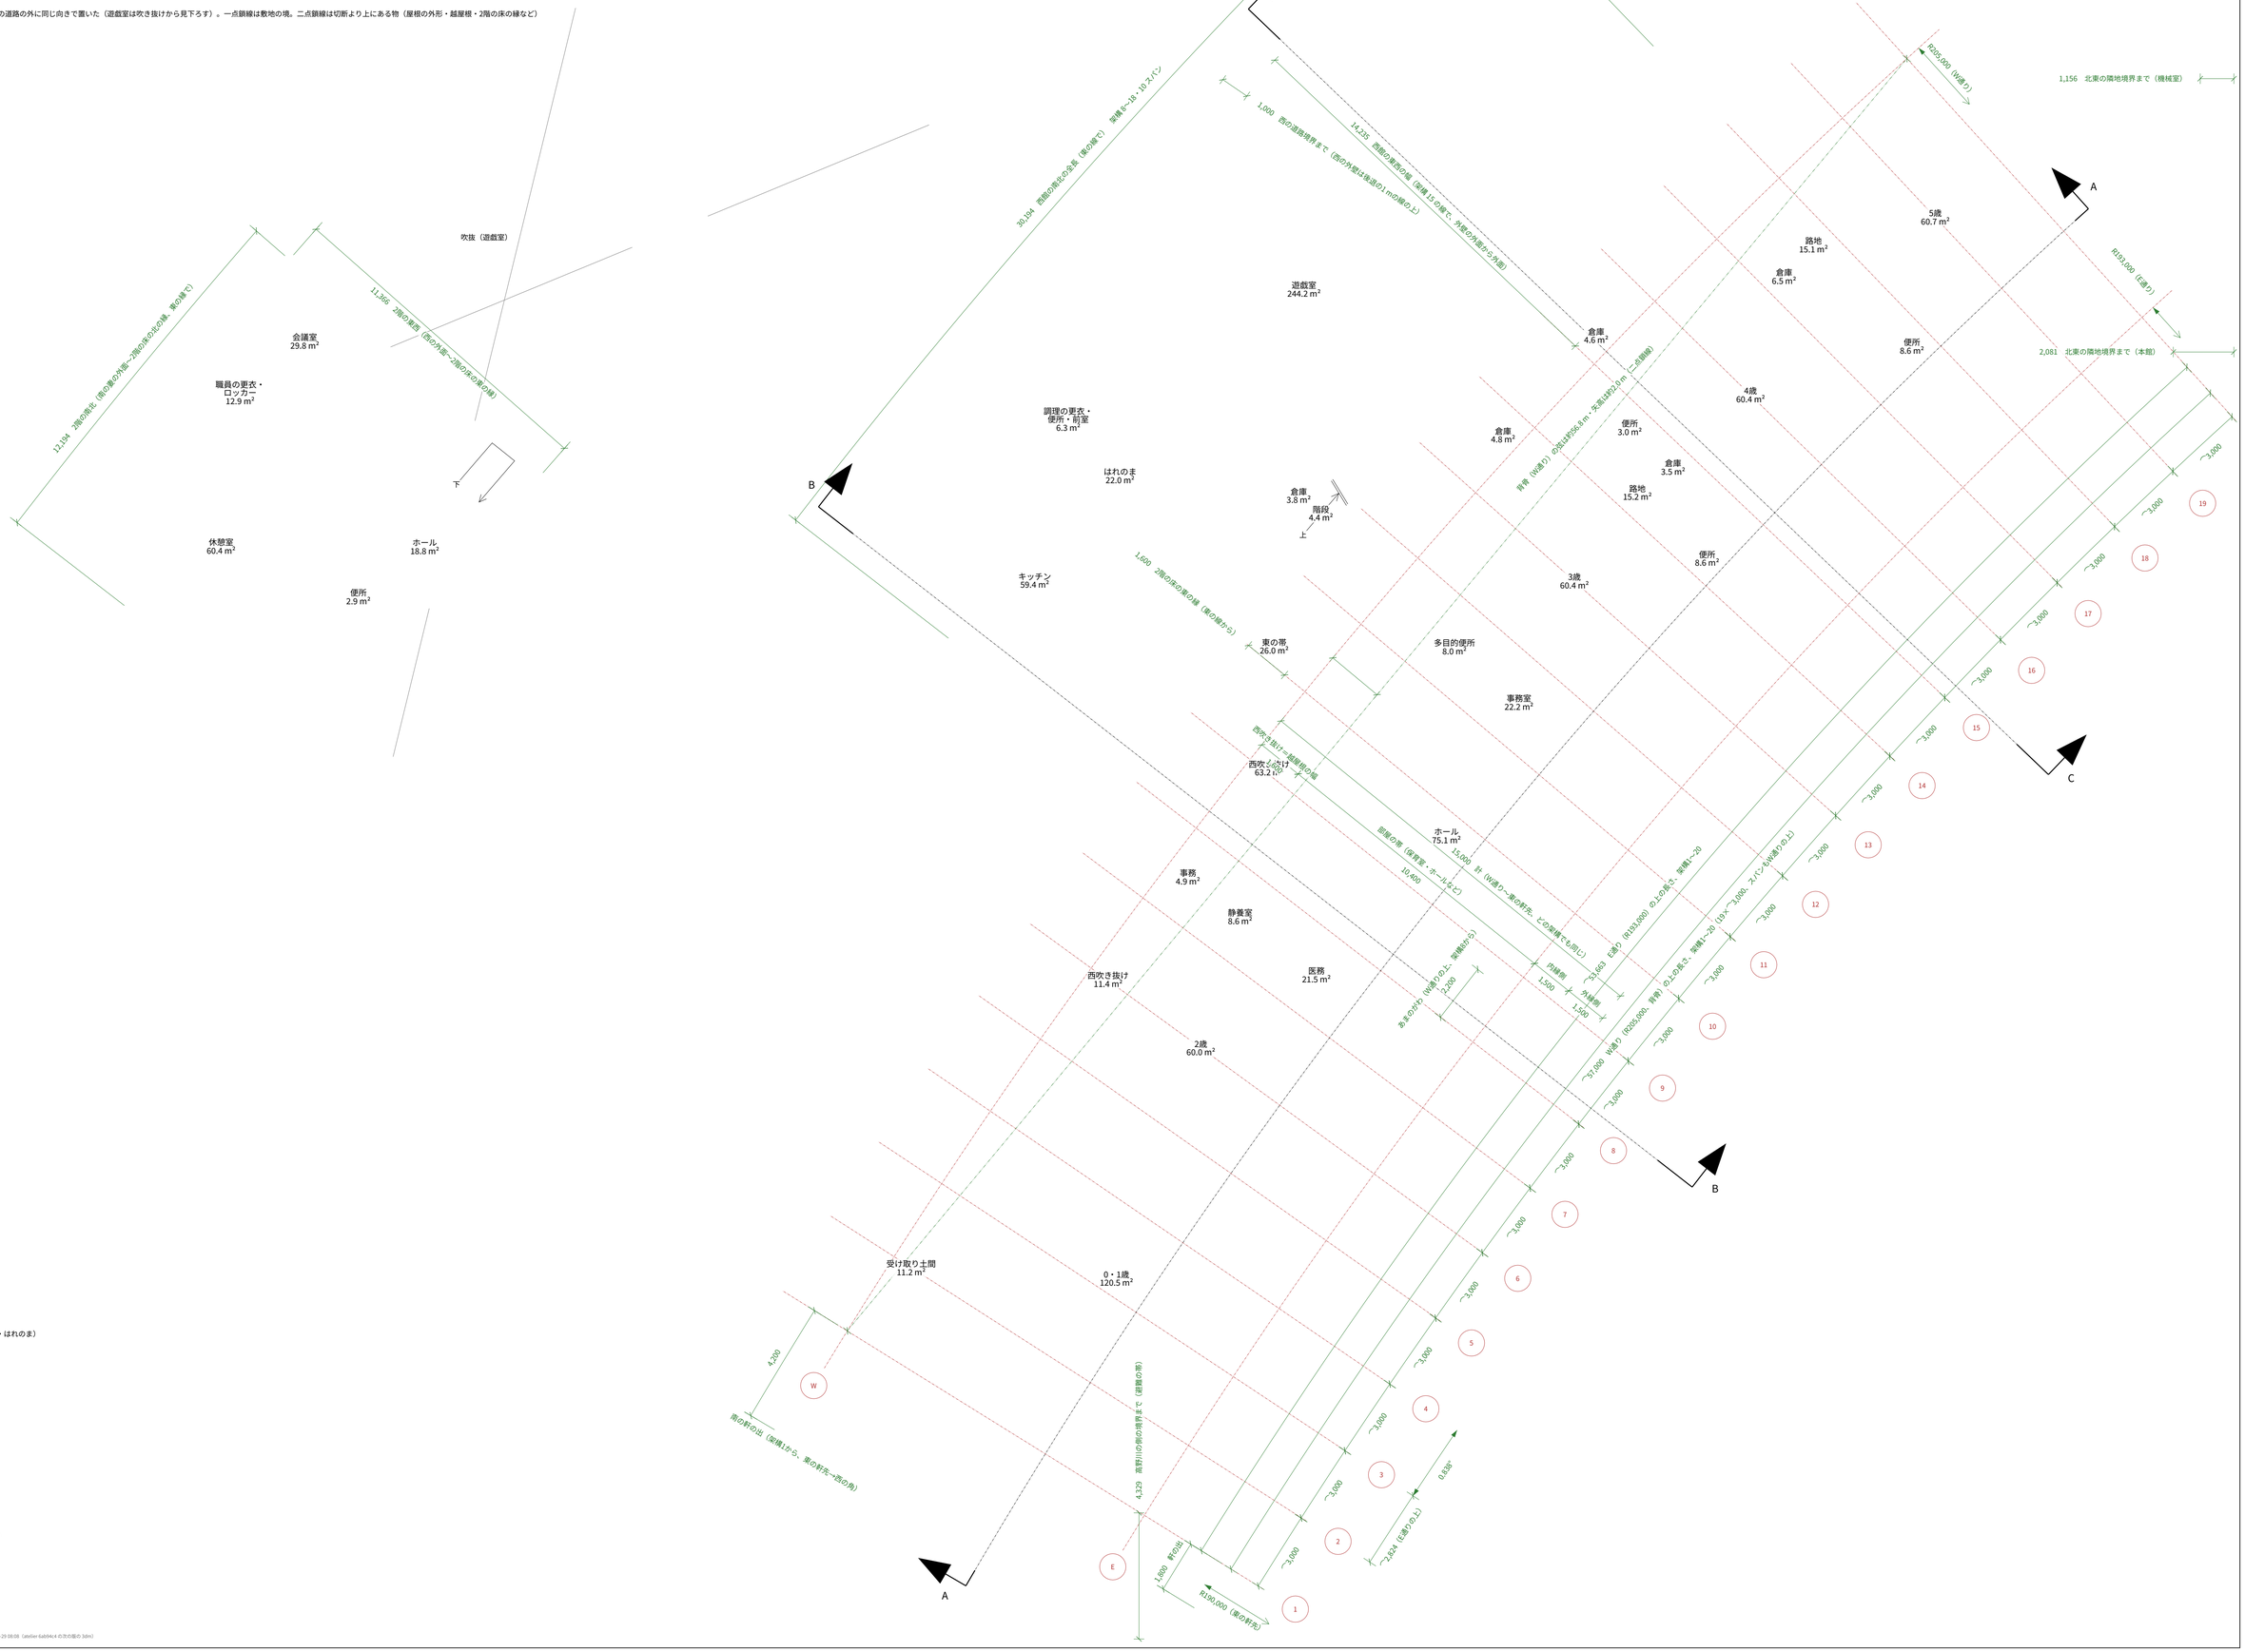

N

部屋の色

- 0・1歳〜5歳
- こどものみんなの場所（遊戯室・はれのま）
- 通り・つなぐ場所（はだし）
- 土足の床
- 大人の場所
- キッチン・調理の更衣
- 水まわり

0　5 m