平面図　1階　FL+1500 で切断／2階（西館）2FL+1000 で切断　1/100

高野川を下に（配置図と同じ向き）。2階は西の道路の外に同じ向きで置いた（遊戯室は吹き抜けから見下ろす）。一点鎖線は敷地の境。二点鎖線は切断より上にある物（屋根の外形・越屋根・2階の床の縁など）

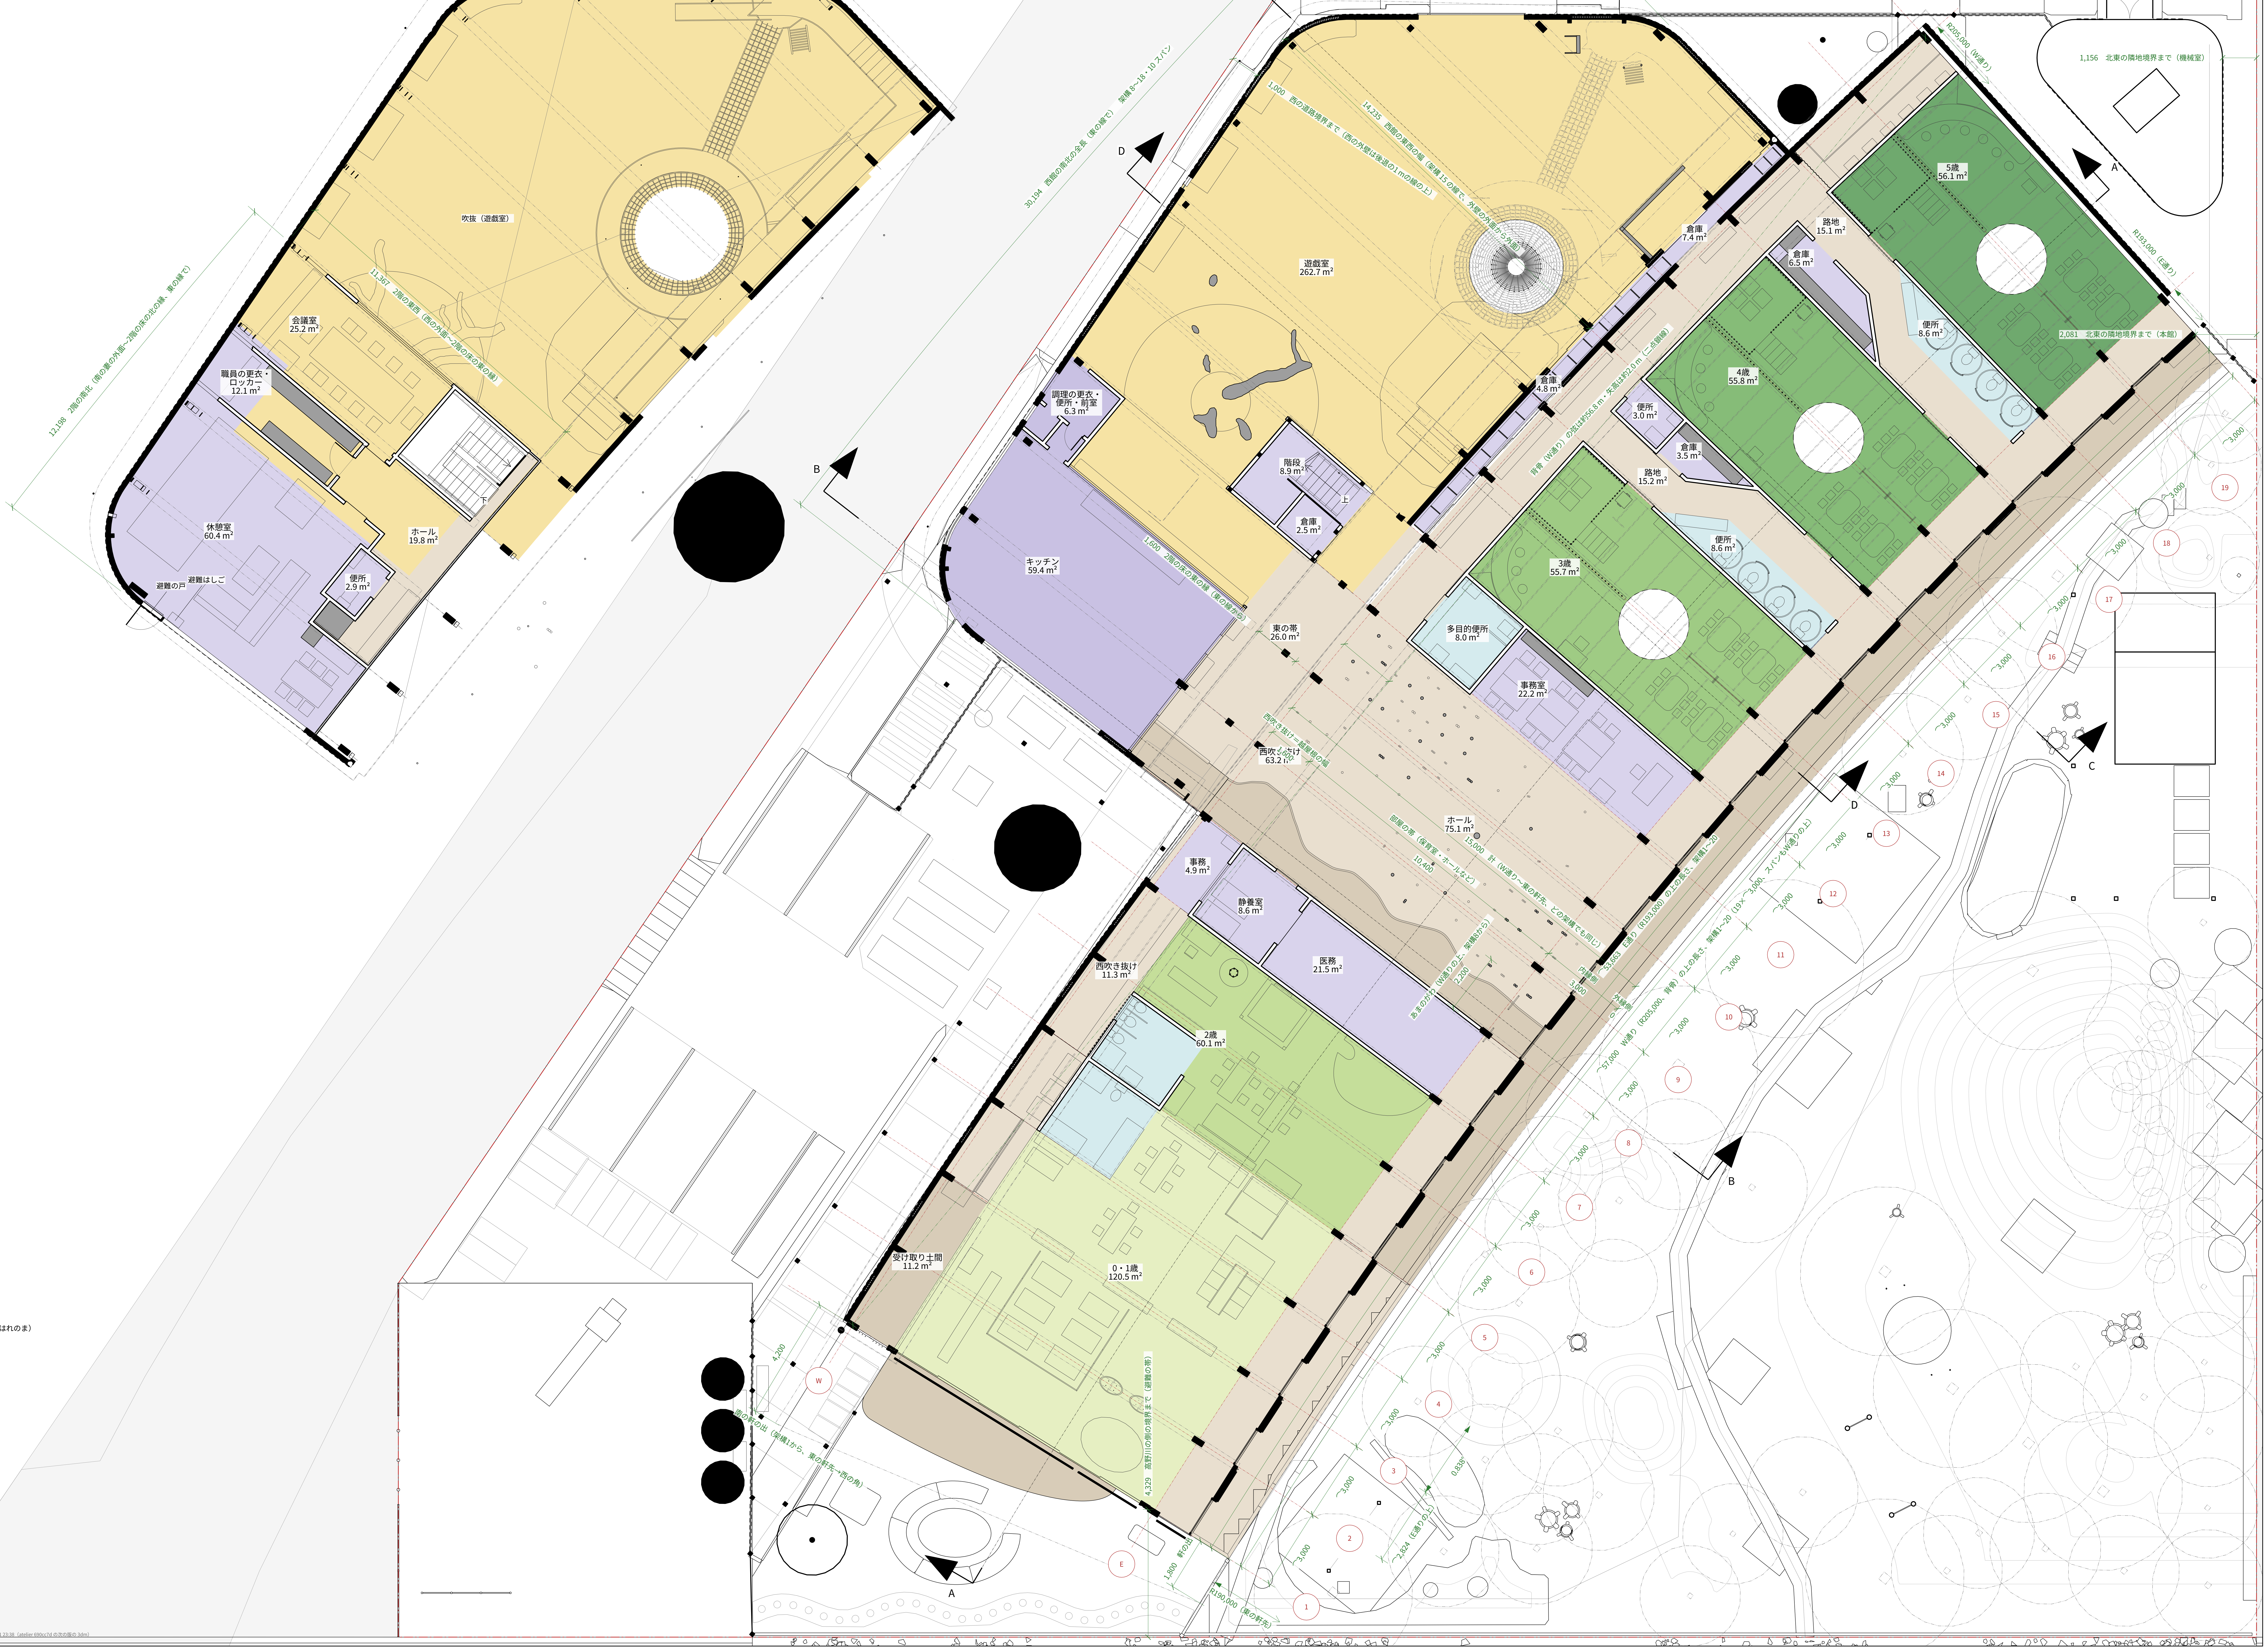
吹抜（遊戯室）
会議室 25.2 m²
職員の更衣・ロッカー 12.1 m²
休憩室 60.4 m²
ホール 19.8 m²
便所 2.9 m²
避難はしご
避難の戸
下
12,198　2階の南北（南の妻の外面〜2階の床の北の縁、東の縁で）
11,367　2階の東西（西の外面〜2階の床の東の縁）
30,194　西館の南北の全長（東の線で）　架構 8〜18・10 スパン
1,000　西の道路境界まで（西の外壁は後退の1 mの線の上）
14,235　西館の東西の幅（架構 15 の線で、外壁の外面から外面）
C
D
B
A
遊戯室 262.7 m²
調理の更衣・便所・前室 6.3 m²
キッチン 59.4 m²
階段 8.9 m²
上
倉庫 2.5 m²
倉庫 4.8 m²
倉庫 7.4 m²
1,600　2階の床の東の縁（東の線から）
東の帯 26.0 m²
西吹き抜け 63.2 m²
西吹き抜け＝越屋根の幅
1,600
ホール 75.1 m²
部屋の帯（保育室・ホールなど）
10,400
15,000　計（W通り〜東の軒先、どの架構でも同じ）
あまのがわ（W通りの上、架構8から）
2,200
3,000
内縁側
外縁側
⁓53,663　E通り（R193,000）の上の長さ、架構1〜20
⁓57,000　W通り（R205,000、背骨）の上の長さ、架構1〜20（19×⁓3,000、スパンもW通りの上）
背骨（W通り）の弦は約56.8 m・矢高は約2.0 m（二点鎖線）
多目的便所 8.0 m²
事務室 22.2 m²
3歳 55.7 m²
便所 8.6 m²
便所 3.0 m²
倉庫 3.5 m²
路地 15.2 m²
4歳 55.8 m²
倉庫 6.5 m²
路地 15.1 m²
便所 8.6 m²
5歳 56.1 m²
R205,000（W通り）
R193,000（E通り）
1,156　北東の隣地境界まで（機械室）
2,081　北東の隣地境界まで（本館）
事務 4.9 m²
静養室 8.6 m²
医務 21.5 m²
西吹き抜け 11.3 m²
2歳 60.1 m²
受け取り土間 11.2 m²
0・1歳 120.5 m²
4,329　高野川の側の境界まで（避難の帯）
1,800　軒の出
R190,000（東の軒先）
南の軒の出（架構1から、東の軒先→西の角）
4,200
2,824（E通りの上）
0.838°
⁓3,000
W
E
1
2
3
4
5
6
7
8
9
10
11
12
13
14
15
16
17
18
19
N

部屋の色

- 🟩 0・1歳〜5歳
- 🟨 こどものみんなの場所（遊戯室・はれのま）
- ▨ 通り・つなぐ場所（はだし）
- 🟫 土足の床
- 🟪 大人の場所
- 🟪 キッチン・調理の更衣
- 🟦 水まわり

0　5 m

こどもたちの育ち舎　3dm（sodachiya.3dm）から自動で作図　2026-11-01 23:38（atelier 690cc7d の次の版の 3dm）