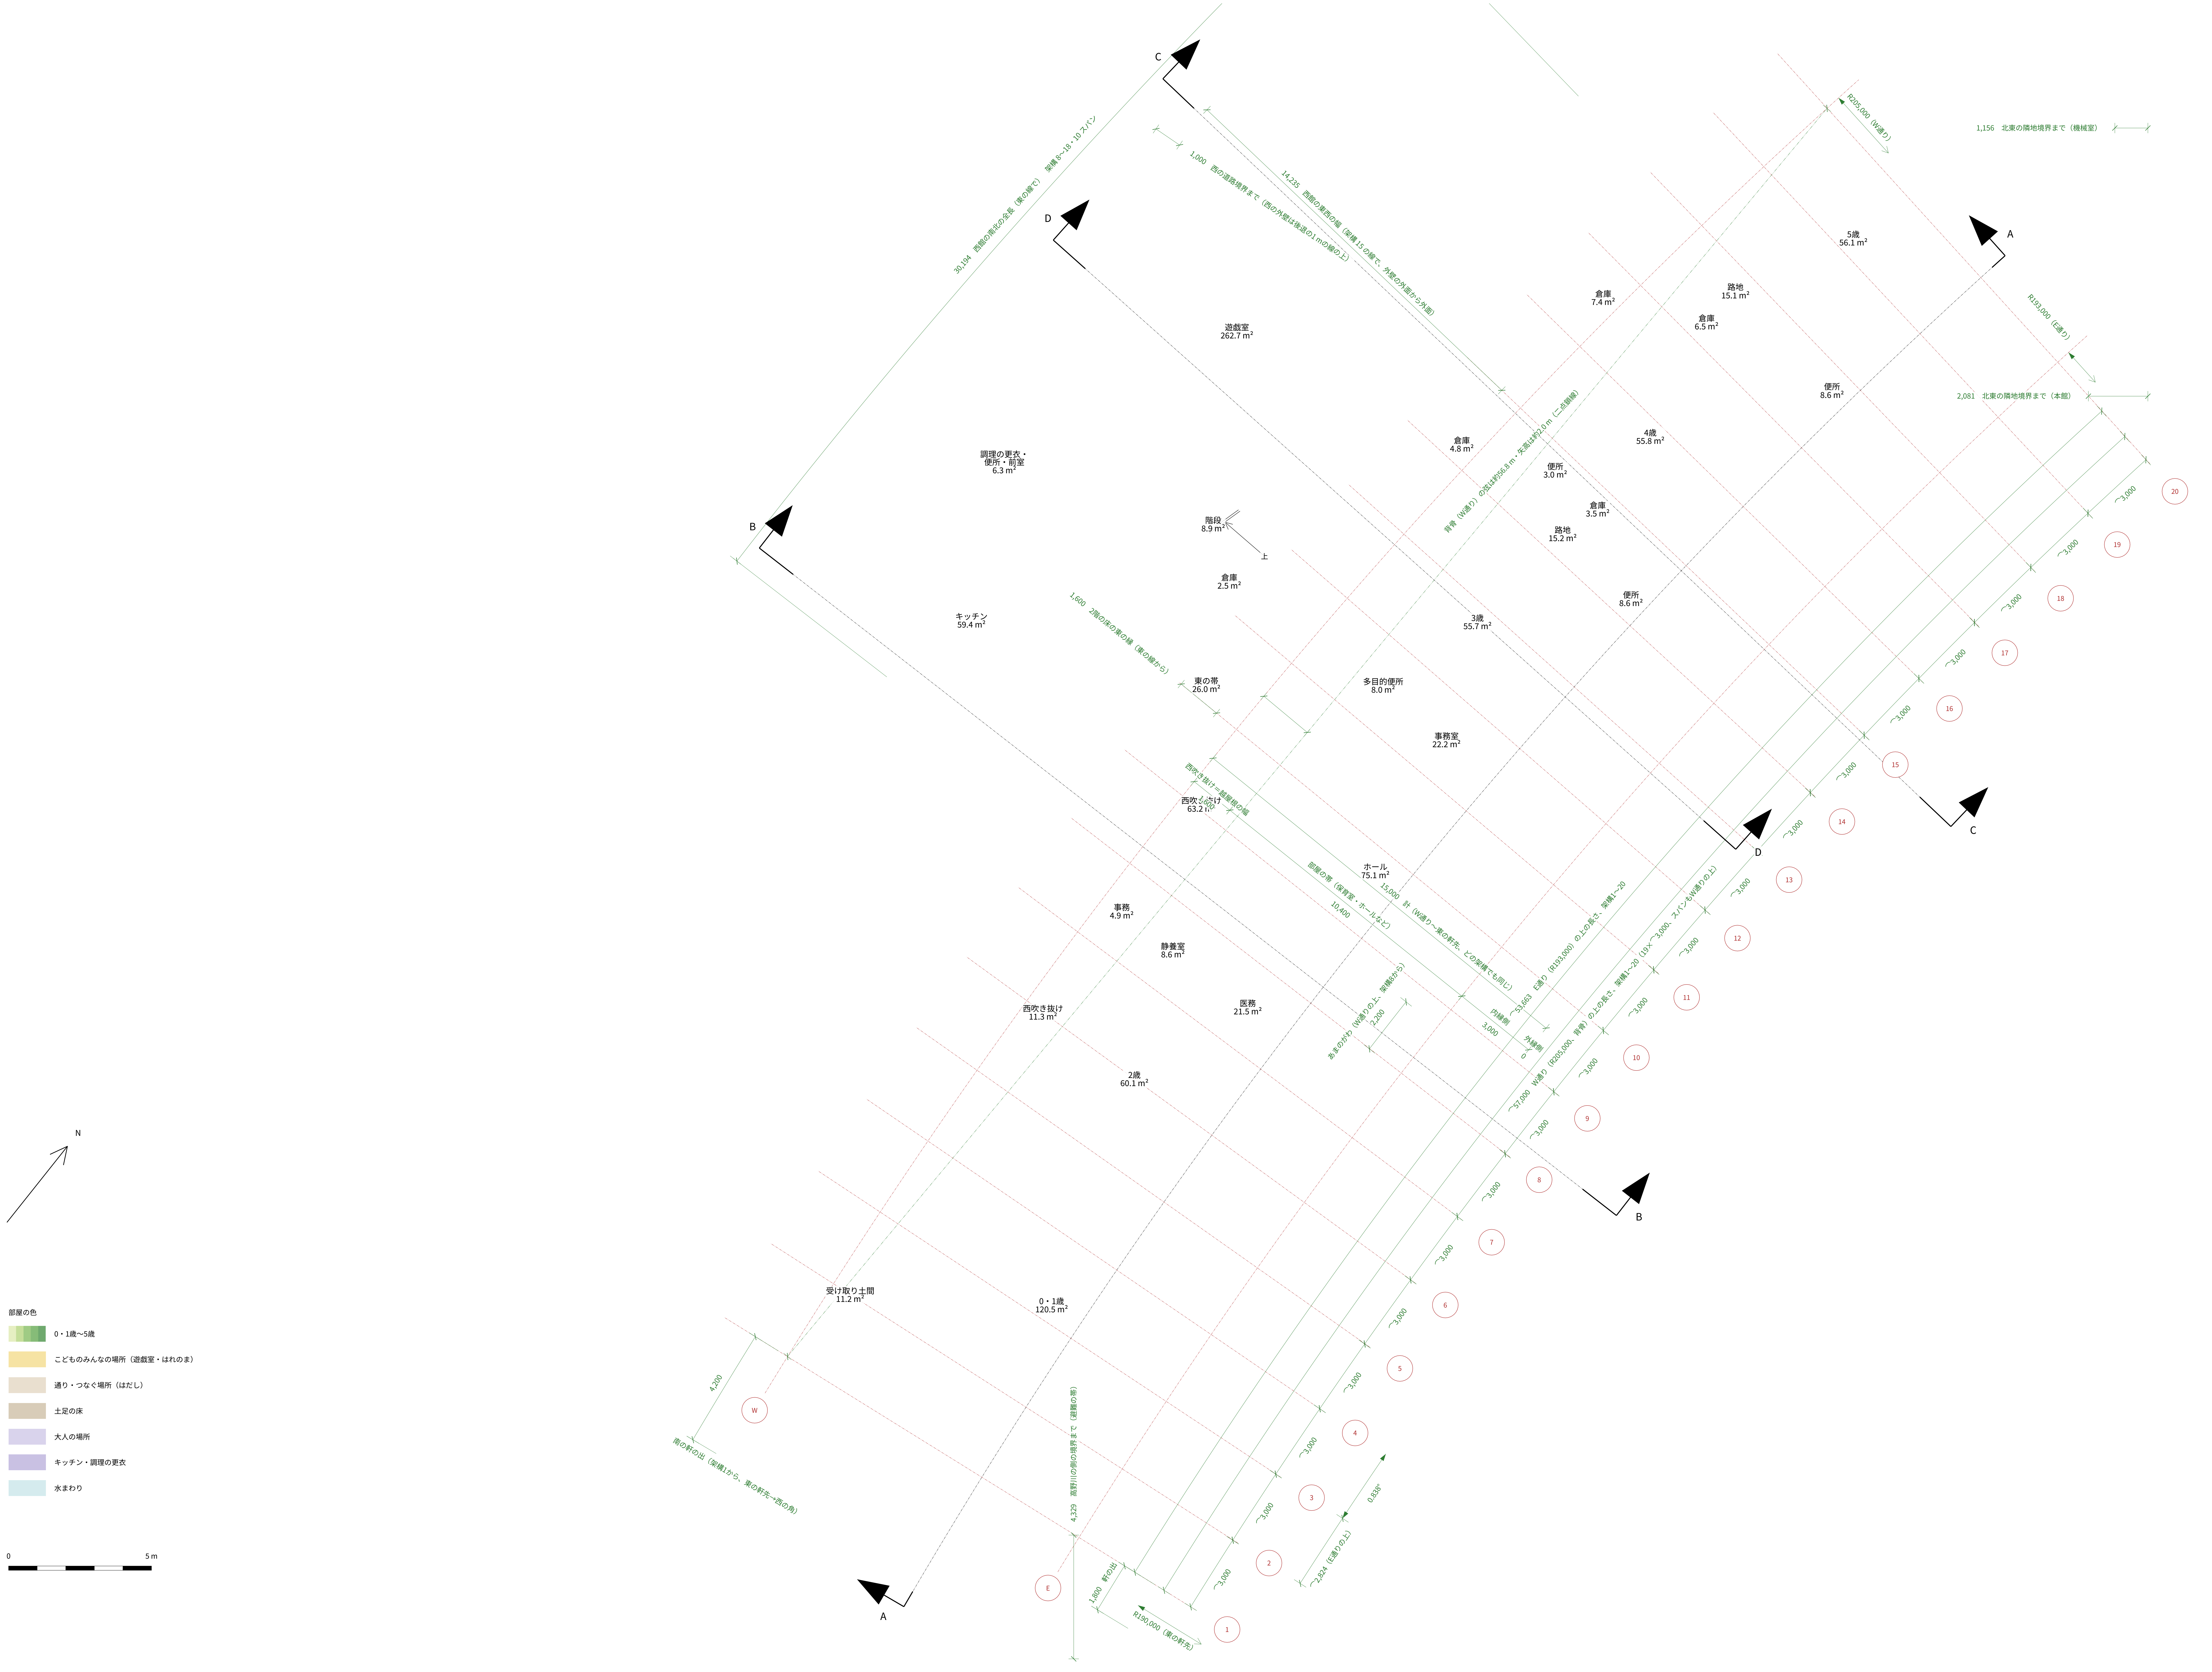
遊戯室 262.7 m²
調理の更衣・便所・前室 6.3 m²
キッチン 59.4 m²
階段 8.9 m²
上
倉庫 2.5 m²
東の帯 26.0 m²
西吹き抜け 63.2 m²
事務 4.9 m²
静養室 8.6 m²
西吹き抜け 11.3 m²
医務 21.5 m²
2歳 60.1 m²
受け取り土間 11.2 m²
0・1歳 120.5 m²
ホール 75.1 m²
多目的便所 8.0 m²
事務室 22.2 m²
3歳 55.7 m²
便所 8.6 m²
路地 15.2 m²
倉庫 3.5 m²
便所 3.0 m²
倉庫 4.8 m²
4歳 55.8 m²
便所 8.6 m²
倉庫 7.4 m²
倉庫 6.5 m²
路地 15.1 m²
5歳 56.1 m²
A
B
C
D
N
W
E
1
2
3
4
5
6
7
8
9
10
11
12
13
14
15
16
17
18
19
20
30,194　西館の南北の全長（東の線で）　架構 8〜18・10 スパン
1,000　西の道路境界まで（西の外壁は後退の1 mの線の上）
14,235　西館の東西の幅（架構 15 の線で、外壁の外面から外面）
R205,000（W通り）
1,156　北東の隣地境界まで（機械室）
R193,000（E通り）
2,081　北東の隣地境界まで（本館）
背骨（W通り）の弦は約56.8 m・矢高は約2.0 m（二点鎖線）
1,600　2階の床の東の縁（東の線から）
西吹き抜け＝越屋根の幅
1,600
部屋の帯（保育室・ホールなど）
10,400
15,000　計（W通り〜東の軒先、どの架構でも同じ）
内縁側
3,000
外縁側
0
あまのがわ（W通りの上、架構8から）
2,200
⌒53,663　E通り（R193,000）の上の長さ、架構1〜20
⌒57,000　W通り（R205,000、背骨）の上の長さ、架構1〜20（19×⌒3,000、スパンもW通りの上）
⌒3,000
4,200
南の軒の出（架構1から、東の軒先→西の角）
4,329　高野川の側の境界まで（避難の帯）
1,800　軒の出
R190,000（東の軒先）
⌒2,824（E通りの上）
0.838°
部屋の色
0・1歳〜5歳
こどものみんなの場所（遊戯室・はれのま）
通り・つなぐ場所（はだし）
土足の床
大人の場所
キッチン・調理の更衣
水まわり
0
5 m