


園庭の側の立面図　1/100　（円弧の中心の方向から、弧の真ん中に正対。西を見る、右が北）

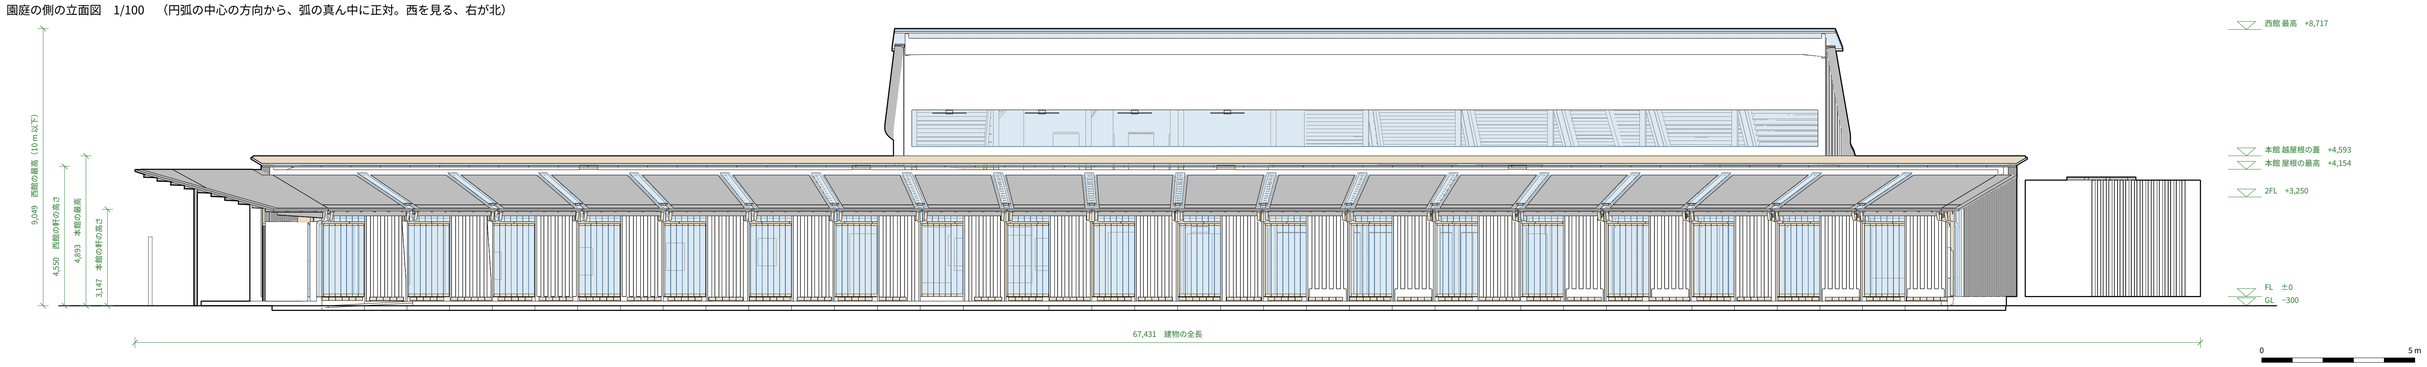

道路の側の立面図　1/100　（西の道路から、園庭の側の反対。東を見る、右が南）

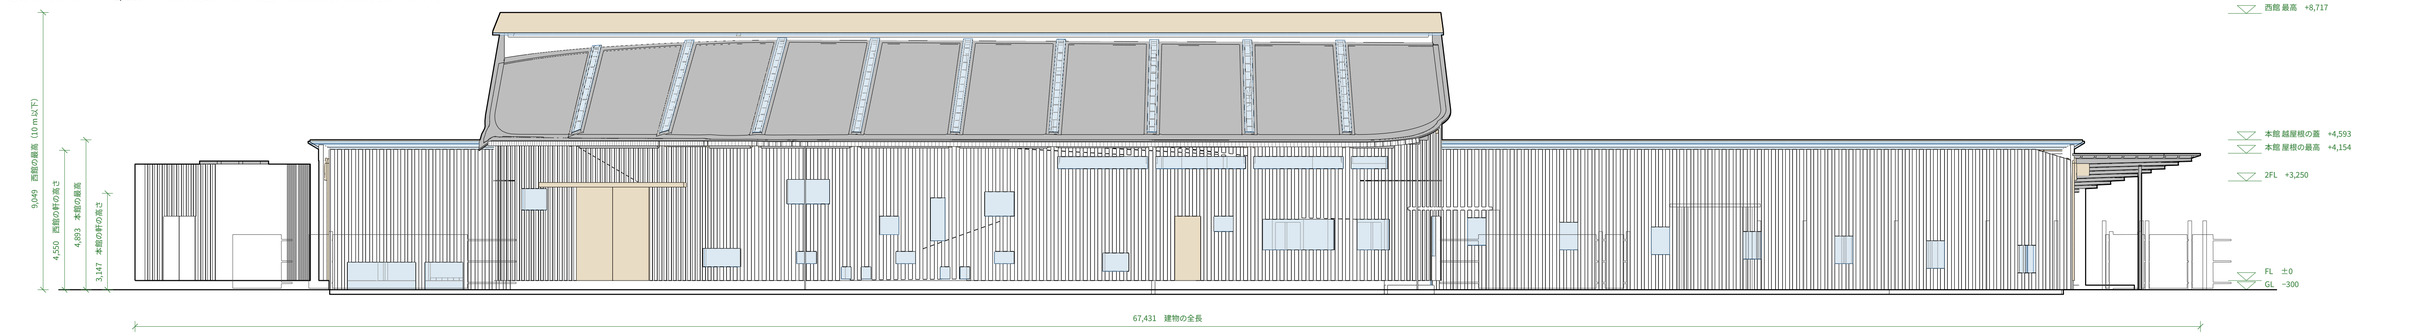

南の妻の立面図　1/100　（架構 1 に正対。北を見る、右が東）

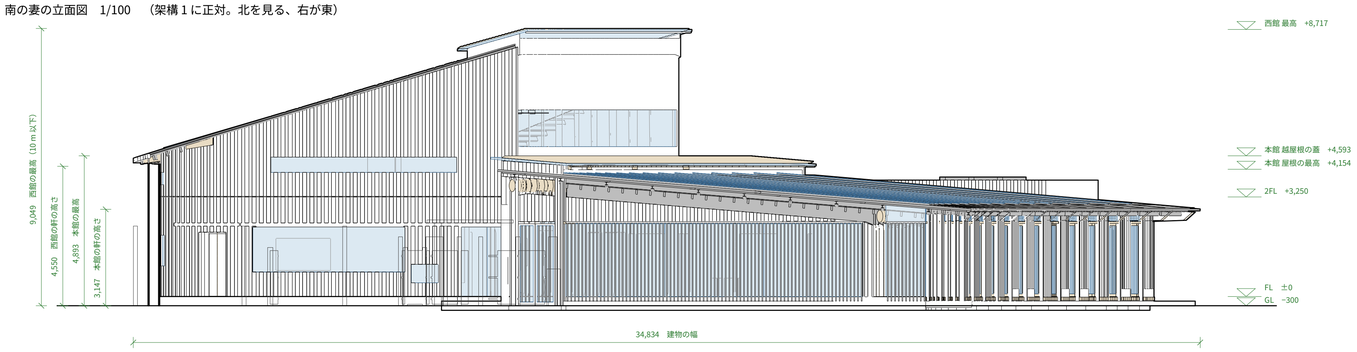

建物と、その手前の外構（塀・柵・木戸・棚・柱、細い線）。駐車・駐輪・室内の家具は省いた。灰色は屋根の面、薄い青はガラス（面は細い灰色の線で透けて見える）。建物の外形は太い線。
園庭の側と道路の側は本館の弧の真ん中に正対（平面と同じ向き、架構の番号は下の丸）。南の妻は架構 1 に正対。

立面図 1　園庭の側・道路の側・南の妻　1/100（A1）

こどもたちの育ち舎　3dm（sodachiya.3dm）から自動で作図　2026-10-28 11:01（atelier 2f84e7a の次の版の 3dm）