

高野川の側の立面図　1/100　（川の向こうから、川の辺に直角に。北西を見る、右が北東）

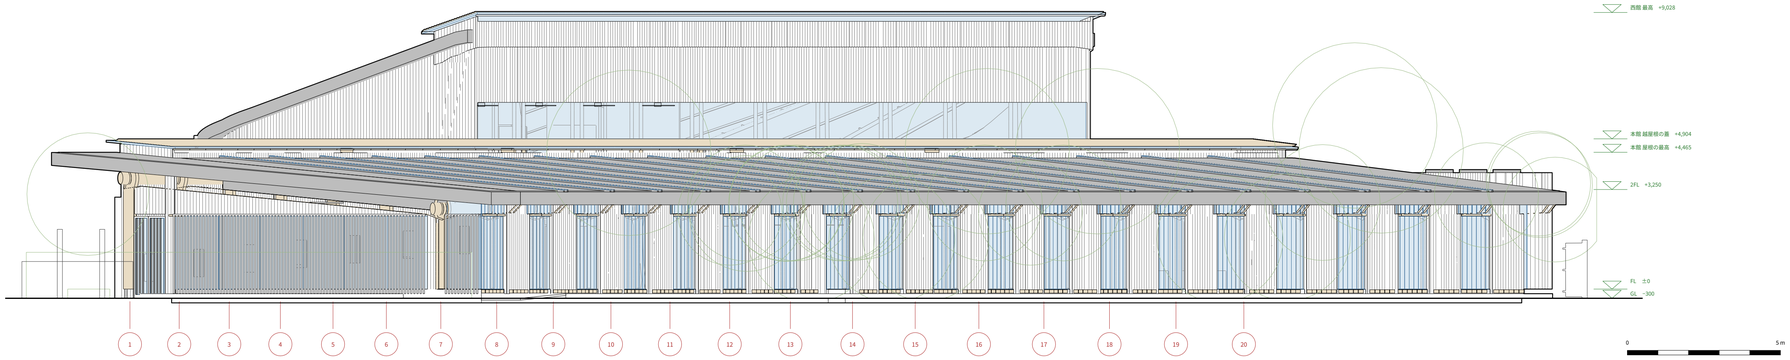


北の妻の立面図　1/100　（架構 20 に正対。南を見る、右が西）

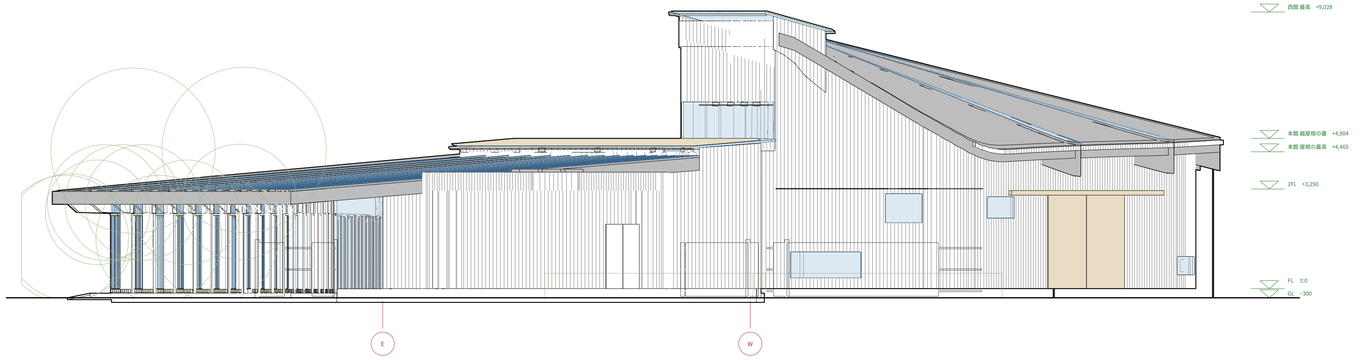


建物と、その手前の外構（塀・樋・木戸・棚・柱、細い線）・樹木（淡い緑の輪郭、手前 15 m まで）。駐車・駐輪・室内の家具は省いた。灰色は屋根の面、薄い青はガラス（奥は暗い灰色の線で透けて見える）。建物の外形は太い線。
高野川の側は川の向こうから川の辺に直角に。北の妻は架構 20 に正対。

**立面図 2　高野川の側・北の妻　1/100（A1）**

こどもたちの育ち舎　3dm（sodachiya.3dm）から自動で作図　2026-10-27 17:28（atelier ca62a90 の次の版の 3dm）