
平面図　2階（西館）　2FL+1000 で切断　1/100

高野川を下に（配置図と同じ向き）。1階の平面図と同じ位置・同じ縮尺（重ねると上下が合う）。西館の外（本館の屋根・園庭・周り）は上から見た見えがかり。二点鎖線は屋根の外形（軒の線）。部屋の幅は壁の芯から芯

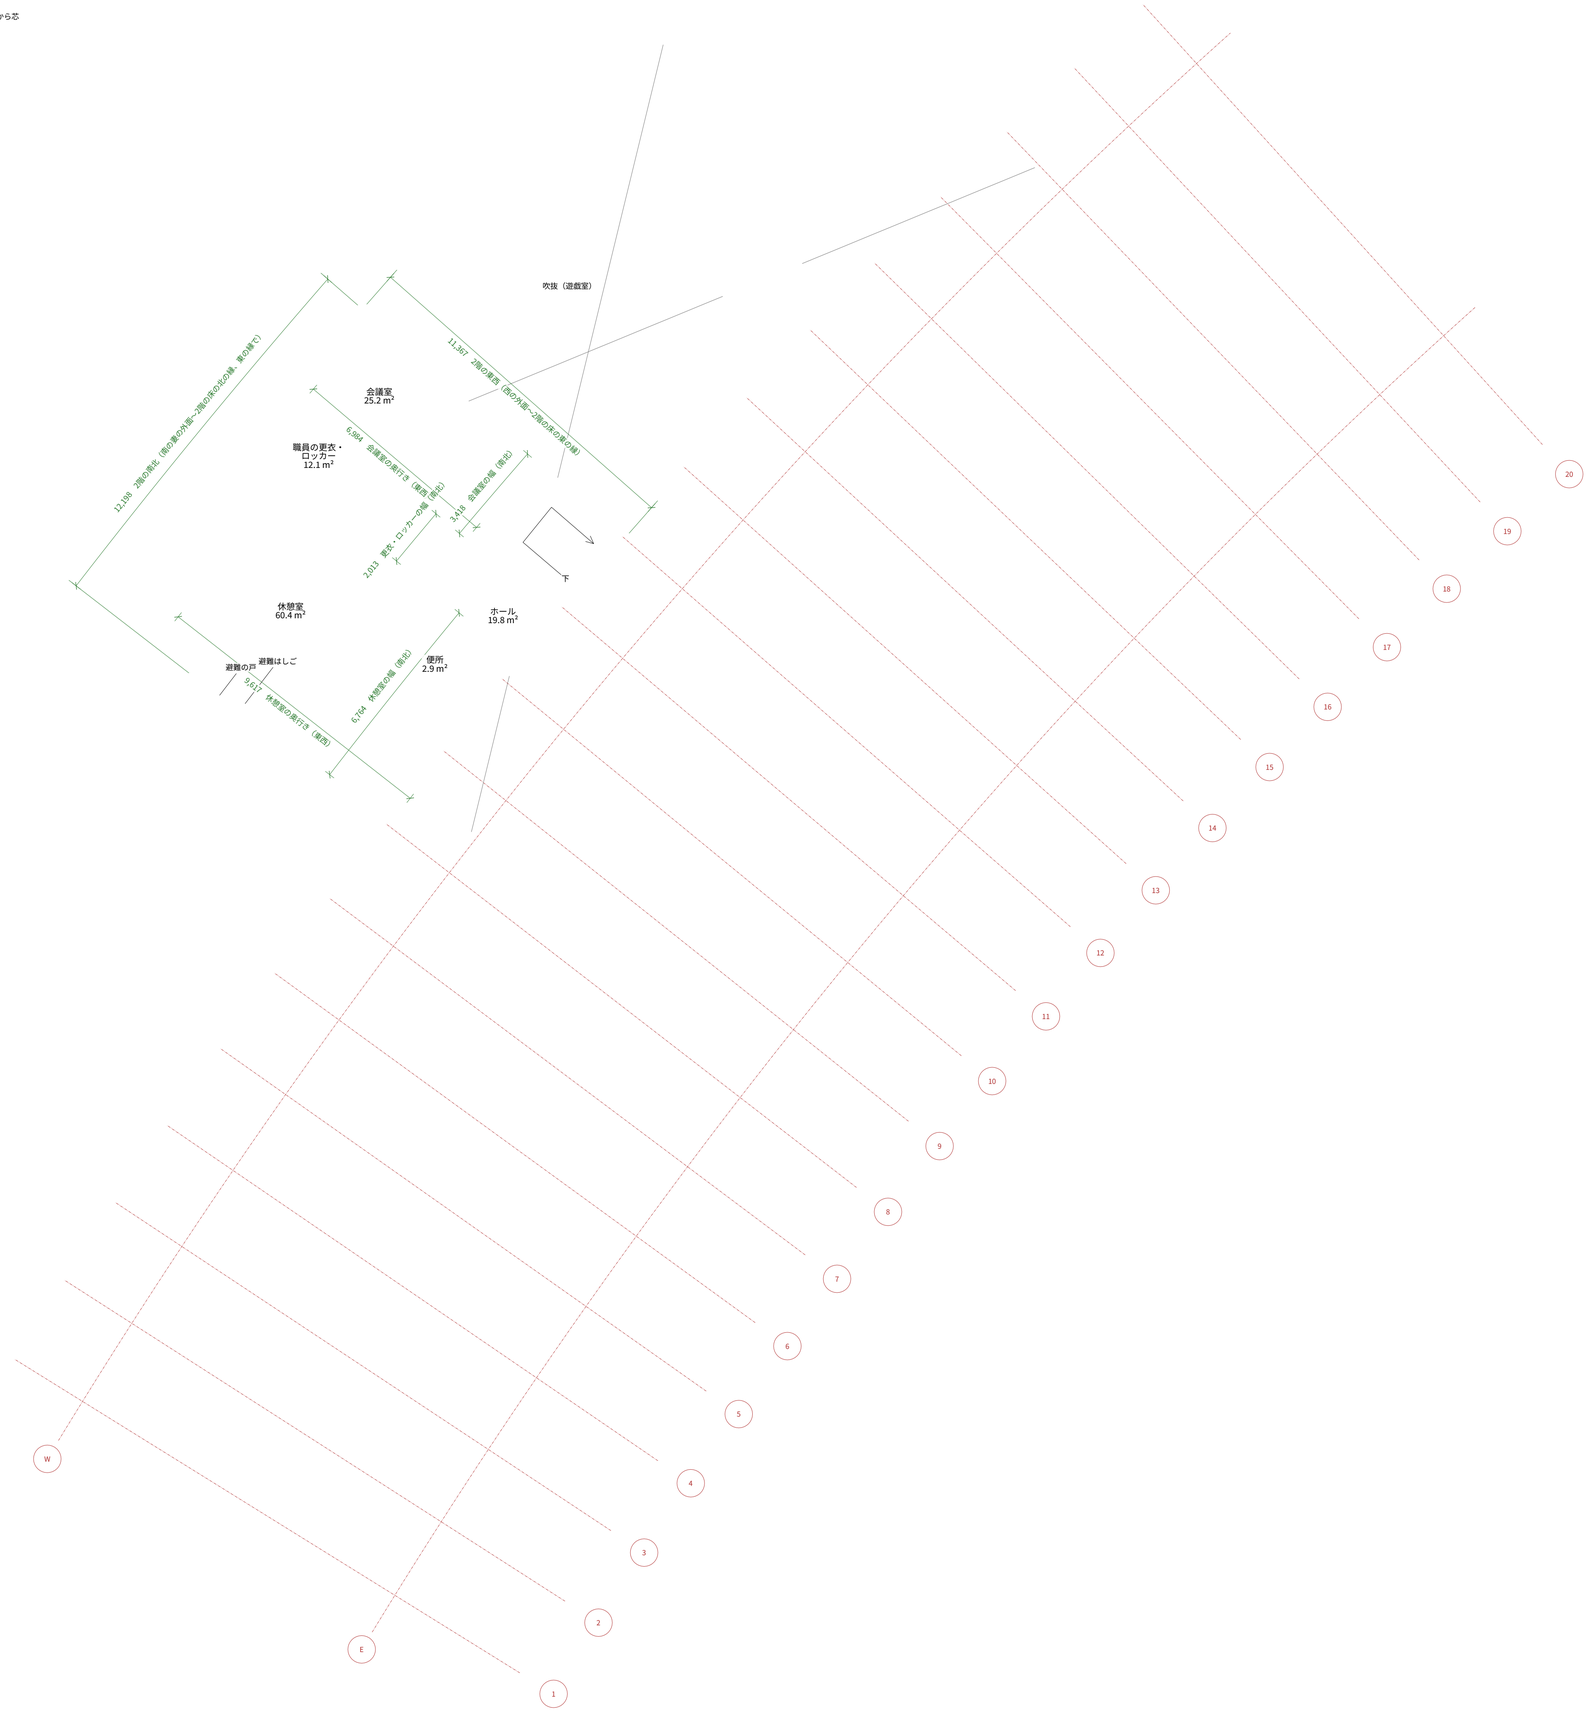

部屋の色

- 0・1歳〜5歳
- こどものみんなの場所（遊戯室・はれのま）
- 通り・つなぐ場所（はだし）
- 土足の床
- 大人の場所
- キッチン・調理の更衣
- 水まわり

0　5 m