# 平面図　1階　FL+1500 で切断　1/100

高野川を下に（配置図と同じ向き）。一点鎖線は敷地の境。二点鎖線は屋根の外形（軒の線）。周りの道・建物は細い線。スパンの寸法はスパン10の庭の側に重ねた5本（建物に近い順に、放射の線のあいだの角度／W通りの上の弧長／E通りの上の弧長／西館の東端の弧長／西館の西端の弧長）

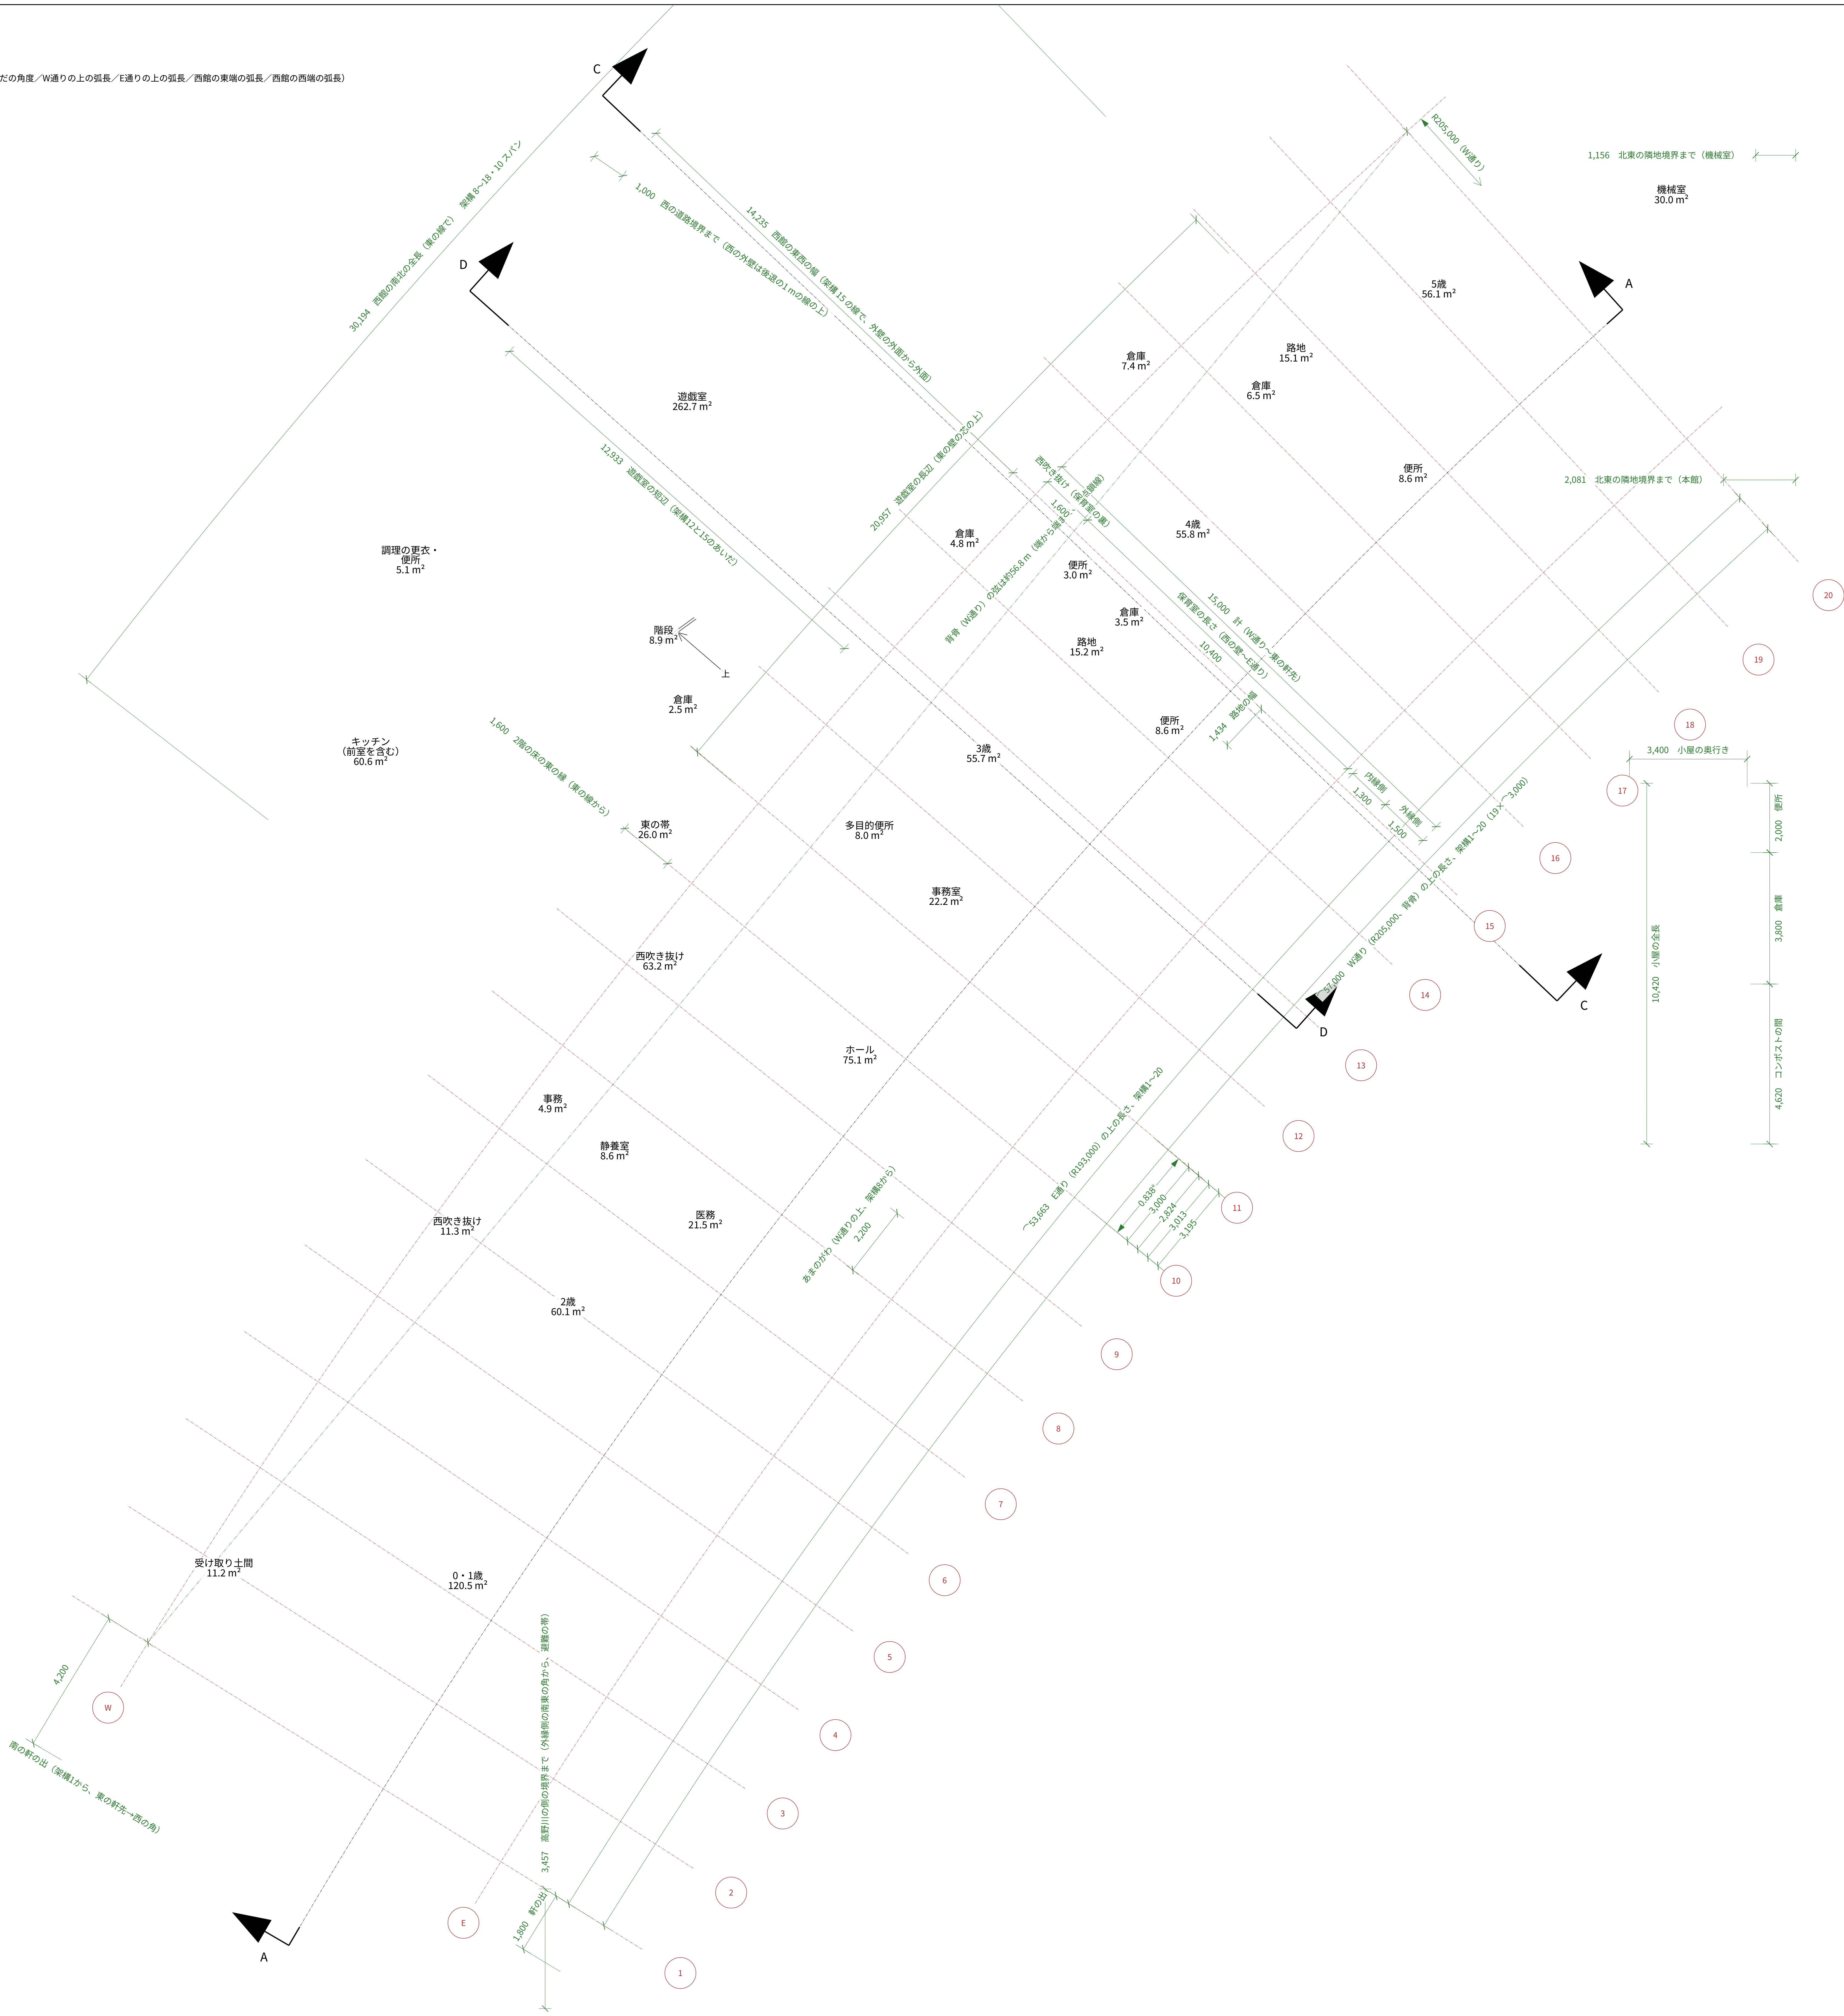
C
30,194　西館の南北の全長（東の線で）　架構 8〜18・10 スパン
1,000　西の道路境界まで（西の外壁は後退の1 mの線の上）
14,235　西館の東西の幅（架構 15 の線で、外壁の外面から外面）
R205,000（W通り）
1,156　北東の隣地境界まで（機械室）
機械室
30.0 m²
D
A
5歳
56.1 m²
倉庫
7.4 m²
路地
15.1 m²
倉庫
6.5 m²
遊戯室
262.7 m²
20,957　遊戯室の長辺（東の壁の芯の上）
12,933　遊戯室の短辺（架構12と15のあいだ）
便所
8.6 m²
2,081　北東の隣地境界まで（本館）
西吹き抜け（保育室の裏）
1,600
倉庫
4.8 m²
4歳
55.8 m²
背骨（W通り）の弦は約56.8 m（端から端まで）
便所
3.0 m²
調理の更衣・
便所
5.1 m²
倉庫
3.5 m²
15,000　計（W通り〜東の軒先）
保育室の長さ（西の壁〜E通り）
10,400
階段
8.9 m²
上
路地
15.2 m²
20
19
倉庫
2.5 m²
1,434　路地の幅
便所
8.6 m²
18
キッチン
（前室を含む）
60.6 m²
1,600　2階の床の東の縁（東の線から）
3歳
55.7 m²
3,400　小屋の奥行き
17
内縁側
1,300
外縁側
1,500
2,000　便所
東の帯
26.0 m²
多目的便所
8.0 m²
16
⌒57,000　W通り（R205,000、背骨）の上の長さ、架構1〜20（19×⌒3,000）
事務室
22.2 m²
15
3,800　倉庫
10,420　小屋の全長
西吹き抜け
63.2 m²
14
C
D
4,620　コンポストの間
ホール
75.1 m²
13
事務
4.9 m²
⌒53,663　E通り（R193,000）の上の長さ、架構1〜20
12
静養室
8.6 m²
0.838°
3,000
2,824
3,013
3,195
11
西吹き抜け
11.3 m²
医務
21.5 m²
あまのがわ（W通りの上、架構8から）
2,200
10
2歳
60.1 m²
9
8
7
6
受け取り土間
11.2 m²
0・1歳
120.5 m²
5
4,200
W
4
3,457　高野川の側の境界まで（外縁側の南東の角から、避難の帯）
3
南の軒の出（架構1から、東の軒先→西の角）
2
A
軒の出
1,800
E
1

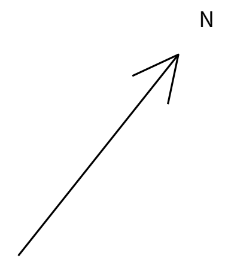

部屋の色

- 🟩 0・1歳〜5歳
- 🟨 こどものみんなの場所（遊戯室・はれのま）
- ▨ 通り・つなぐ場所（はだし）
- 🟫 土足の床
- 🟪 大人の場所
- 🟪 キッチン・調理の更衣
- 🟦 水まわり

0　5 m

こどもたちの育ち舎　3dm（sodachiya.3dm）から自動で作図　2026-11-03 09:19（atelier f0ad1ea の次の版の 3dm）