
育ち舎　2歳の部屋　家具配置（たたき台）

1/100（A3）　2026-10-27　架構5〜7（スパン5・6、南から）。破線は頭上（屋根板・軒・物干し・天袋）と午睡時のコット。

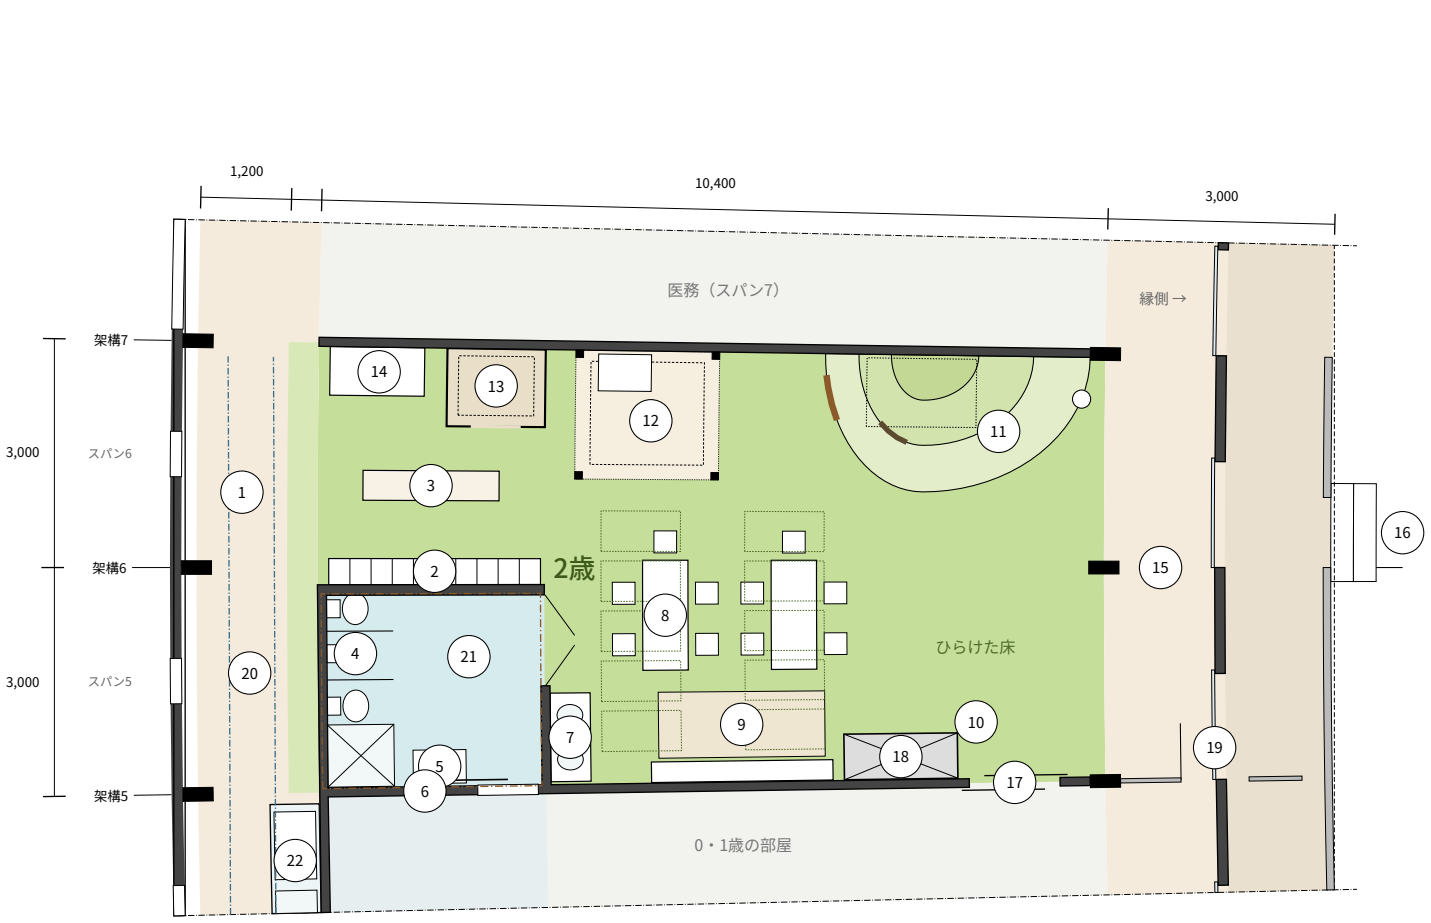

0　1　5　m

1　2歳の道（先生と歩いて登園する。幅 1.2、壁なし）
2　じぶんでの場所：個人棚・フック（10人分、h900）
3　ゆっくりのベンチ h250（着替え・靴下。座の下は引き出し）
4　トイレ：座る便器×3（低い仕切り h900）、シャワーパン
5　立ったままパンツを替える台
6　背伸びの戸（1歳が先生と来る）
7　手洗い×2 h500・鏡（トイレを出てすぐ、食事の前）
8　食卓 h400×2・椅子×10／午睡時はヒノキと帆布のコット×10（破線）
9　絵本の面陳棚 h600・ござ
10　ひらけた床（積み木・ブロック）
11　山：頂上 h900、南 約1:2・東 約1:2.5 の斜面、肩に崖 h350、中はかくれ家（入口は西、東に覗き穴）
12　ままごとの家（壁のない家：柱と低い屋根 h1400。先生の目が通る）
13　落ち着くくぼみ（自分から入る狭い所。先生から見える）
14　先生の記録台 h900（背は北の壁、部屋全体を見る）
15　縁側：内縁側 1.5（はだし）＋外縁側 1.5（土足 −150）。中ほどにスパンごとに杉の壁＋ガラスの片引き戸、外の端に格子の高欄 h900
16　高欄の戸・二段の縁
17　1歳⇔2歳の引き戸（朝夕の合同保育）
18　コットの収納（扉付き。上は先生の物の高い棚）
19　縁側の低い柵の戸（0・1歳／2歳の縁側の境）
20　物干し（昇降式の竹竿。西の吹き抜けの上、越屋根の下）
21　天袋（トイレの上）
22　洗濯（0・1歳の側、水まわりの配管壁沿い）

面積（芯々、概算）　2歳の保育室 77.1 m²（縁側を含む）　室内 60.3 m²（うちトイレ 8.0、トイレを除く 52.4）　道の残り（室に含める帯）2.4　2歳の道 7.2　縁側 16.8

危ないものと先生の物は扉の中か h1500 以上へ。それより低い所にあるものは全部さわってよい。