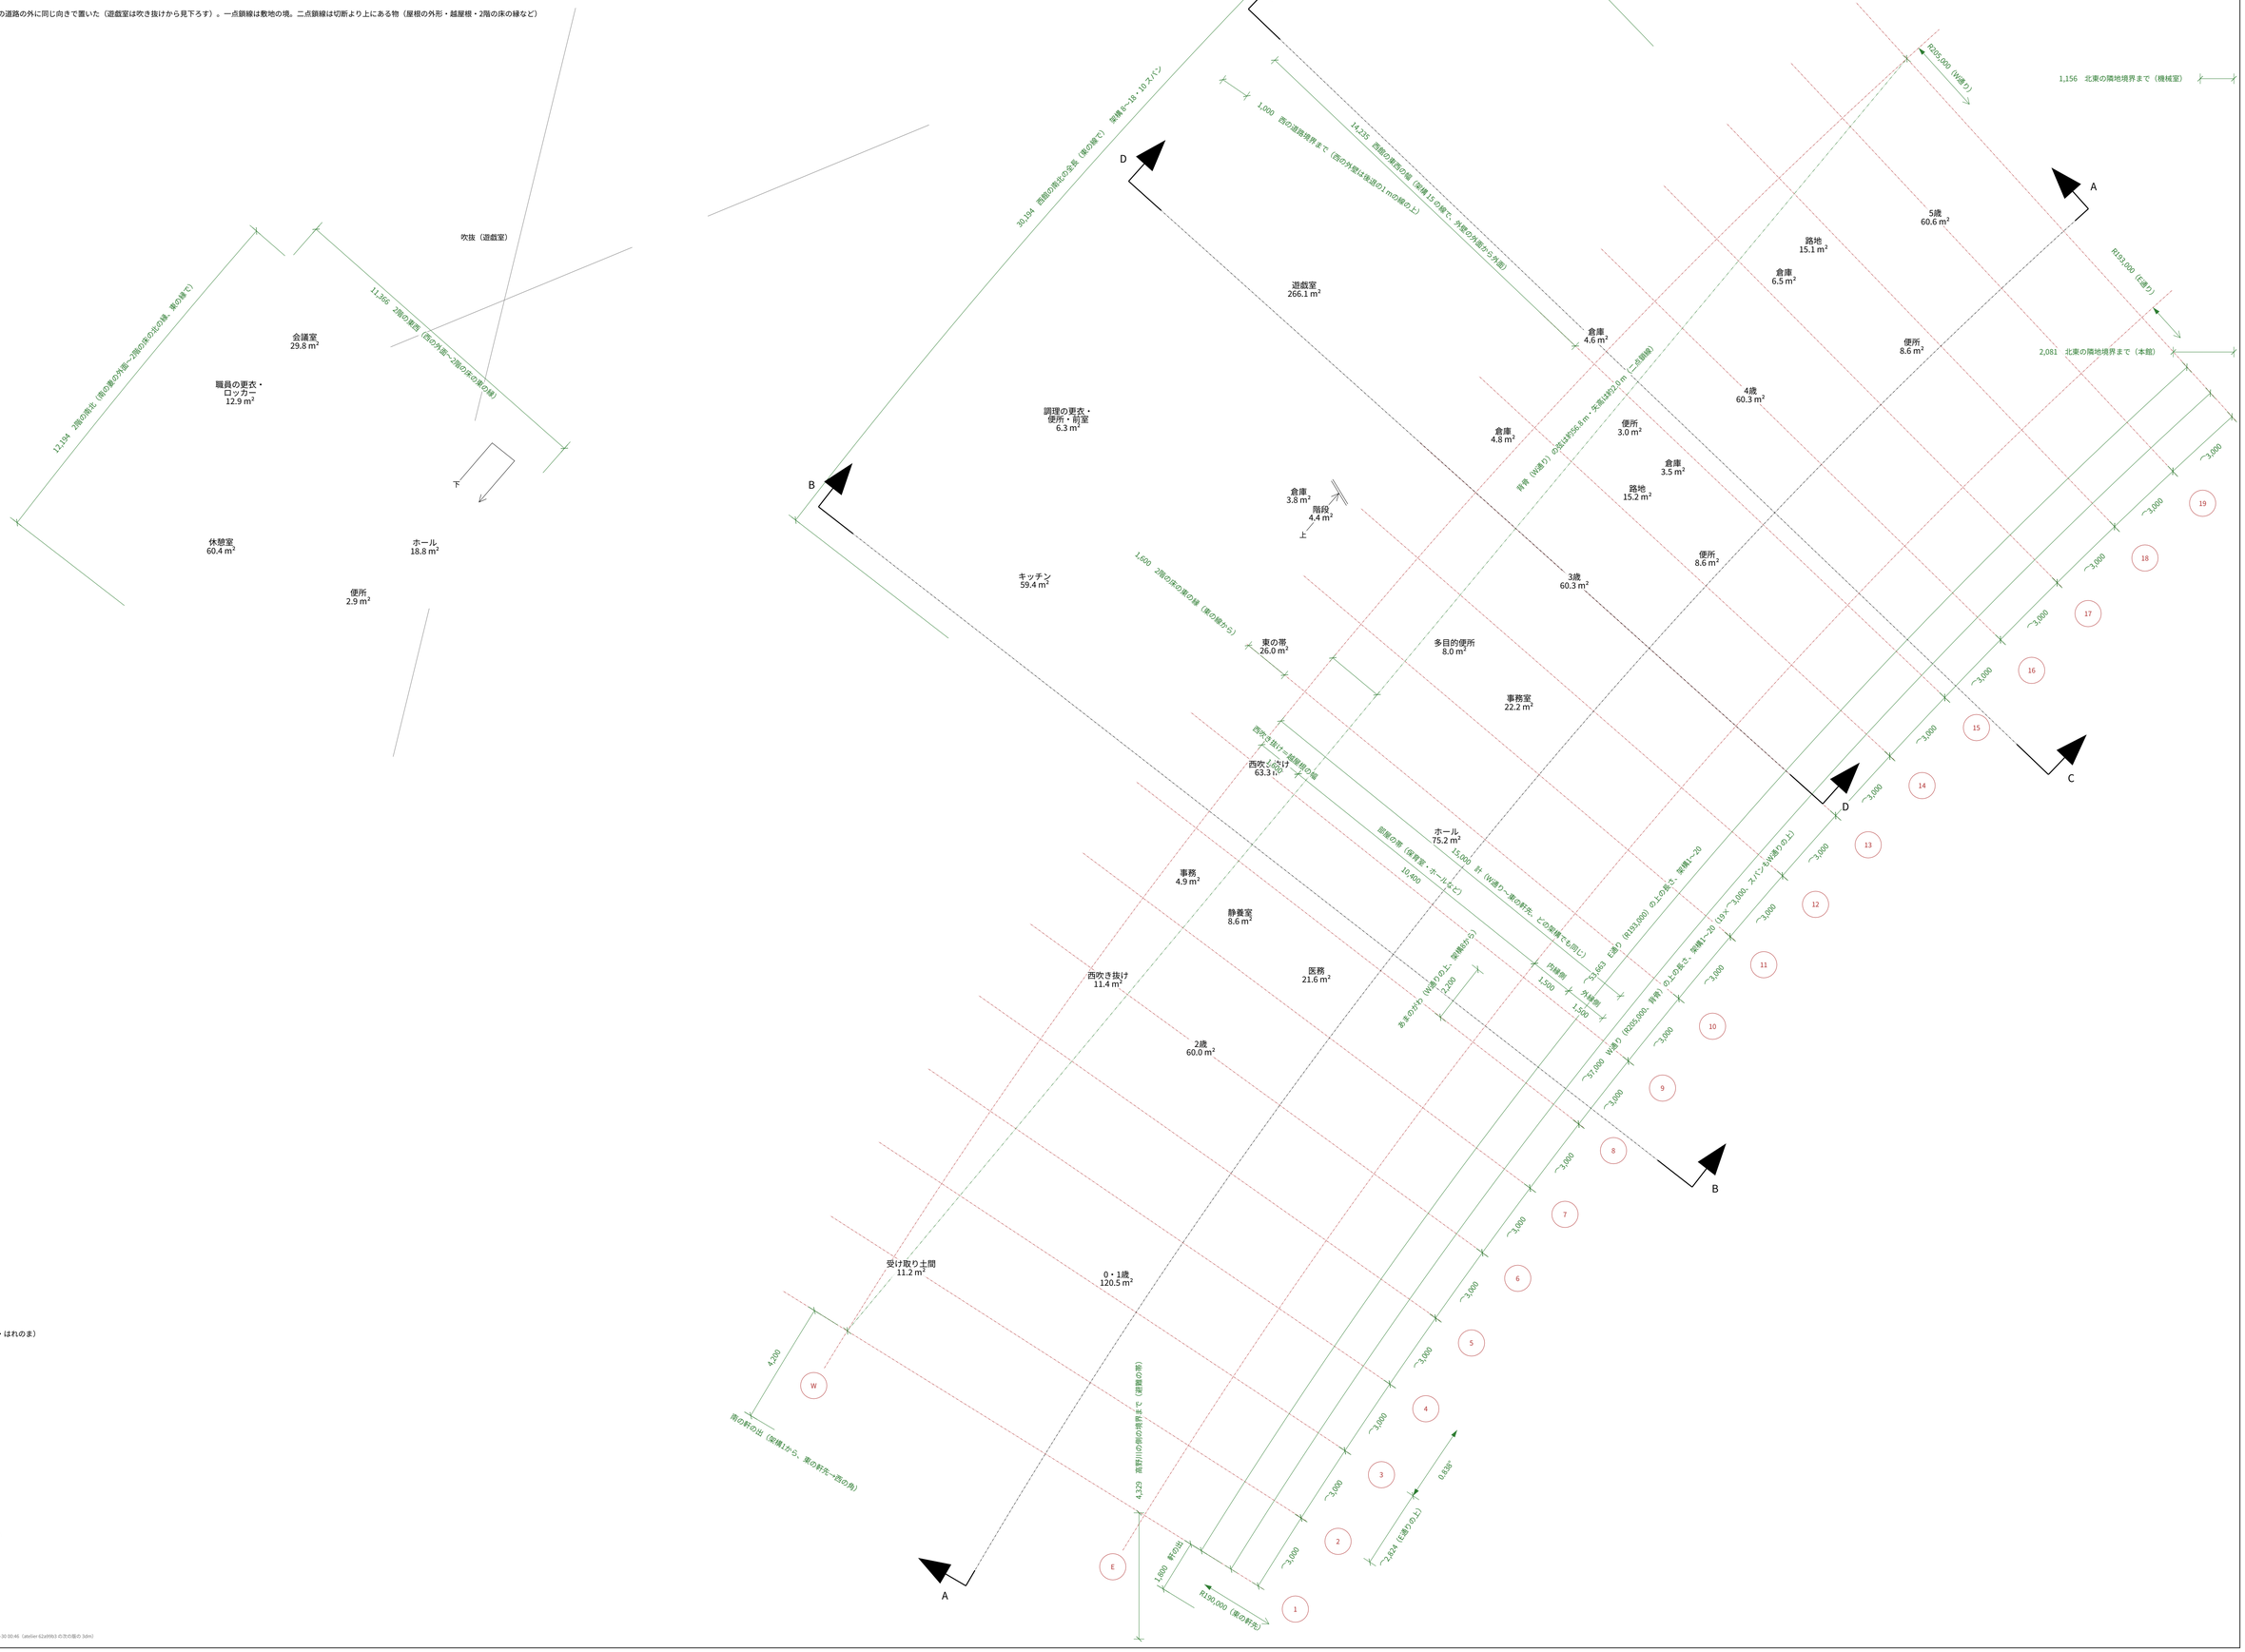
平面図　1階　FL+1500 で切断／2階（西館）2FL+1000 で切断　1/100

高野川を下に（配置図と同じ向き）。2階は西の道路の外に同じ向きで置いた（遊戯室は吹き抜けから見下ろす）。一点鎖線は敷地の境。二点鎖線は切断より上にある物（屋根の外形・越屋根・2階の床の縁など）


吹抜（遊戯室）
会議室
29.8 m²
職員の更衣・
ロッカー
12.9 m²
休憩室
60.4 m²
ホール
18.8 m²
便所
2.9 m²
下
12,194　2階の東北（西の東の方面～2階の北の端、東の縁で）
11,366　2階の東西（西の外面～2階の床の東の縁）
遊戯室
266.1 m²
調理の更衣・
便所・前室
6.3 m²
キッチン
59.4 m²
倉庫
3.8 m²
階段
4.4 m²
上
倉庫
4.8 m²
倉庫
4.6 m²
便所
3.0 m²
倉庫
3.5 m²
路地
15.2 m²
3歳
60.3 m²
便所
8.6 m²
4歳
60.3 m²
便所
8.6 m²
5歳
60.6 m²
路地
15.1 m²
倉庫
6.5 m²
東の帯
26.0 m²
多目的便所
8.0 m²
事務室
22.2 m²
西吹き抜け
63.3 m²
ホール
75.2 m²
事務
4.9 m²
静養室
8.6 m²
医務
21.6 m²
西吹き抜け
11.4 m²
2歳
60.0 m²
0・1歳
120.5 m²
受け取り土間
11.2 m²
30,104　西側の南北の全長（東の縁で）　勾配 4～18・10 スパン
14,235　西側の東西の幅（南棟 1スパンの縁で、外壁の外面から外面）
1,000　西の道路境界まで（西の外壁は敷地から1 m の縁の上）
1,600　2階の北の東の縁（東の壁から）
10,400
15,000　軒（W通り～東の軒先、どの勾配でも同じ）
西吹き抜け（保育室・ホールと）
面積の帯（保育室・ホールと）
西外3 抜け～越屋根の端
高野川の面の境界まで（図面の南）
4,229
1,800　軒の出
約90,000（東の軒先）
4,200
南の軒の出（架構1から、東の軒先→四の角）
W
E
A
B
C
D
R250,000（W通り）
1,156　北東の隣地境界まで（機械室）
R150,000（E通り）
2,081　北東の隣地境界まで（本館）
青青（W通り）の北は約56.8 m・交差は約2.9 m（二点鎖線）
~3,000
~3,600
~3,000
~3,000
~3,000
~3,000
~3,000
~3,000
~3,000
~3,000
~3,600
~3,000
~3,600
~3,000
~3,600
~3,000
~3,000
~3,000
~3,000
~3,000
~3,000
~3,000
~3,000