

**壁に貼ったとき　左：1〜3 を縦につなぐ（高さ約 1.8 m）　右：4・5 を縦につなぐ**

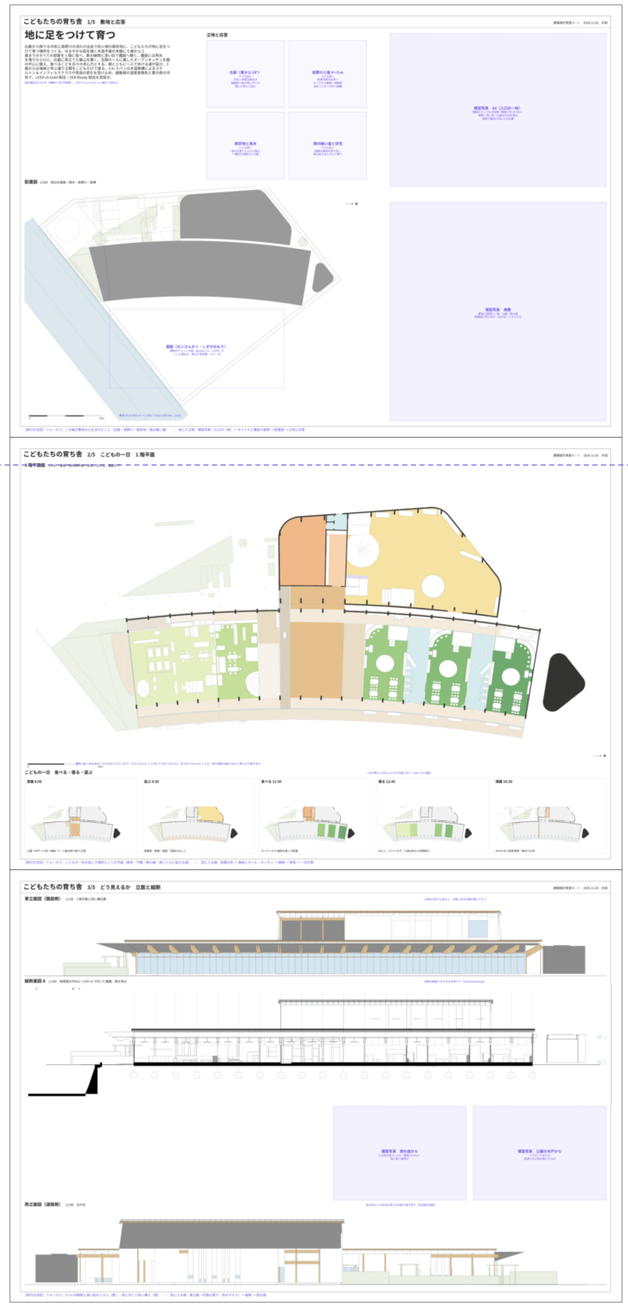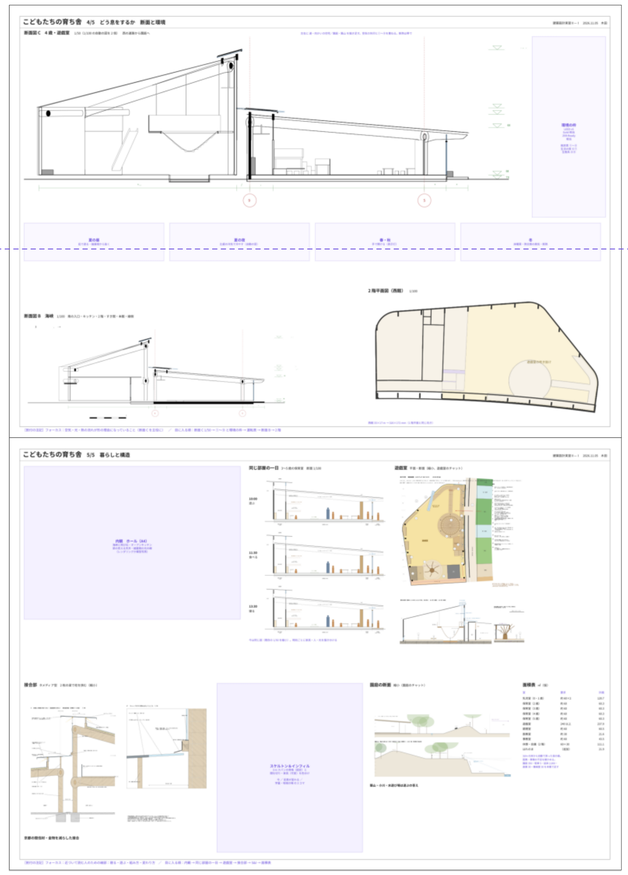


目の高さ 1.5 m

左の列は 配置 1/200 → 1 階平面 1/100 → 立面・縦断 1/100。

どれも北が右・園庭が下で、建物の位置が縦にそろう。

目の高さに来るのは 1 階平面（最も細かい図）と断面 C。

右の列は下端が約 0.6 m。暮らしと構造は近づいて読む。

製図台に置くなら 2＋2＋1（1・2／3・4／5）に切り分ける。

床

# 地に足をつけて育つ

比叡から降りる冷気と高野川の流れが出会う松ヶ崎の扇状地に、こどもたちが地に足をつけて育つ場所をつくる。ゆるやかな弧を描く木造平屋の本館に 0 歳から 5 歳までのすべての部屋を 1 階に並べ、東の縁側と深い庇で園庭へ開く。園庭には用水を借りた小川と、比叡に見立てた築山を置く。玄関ホールに面したオープンキッチンを園の中心に据え、食べることを日々の求心力とする。歳とともに一人で歩ける道が延び、3 歳からは海峡と呼ぶ通り土間をこどもだけで渡る。3 m スパンの木造架構によるスケルトン＆インフィルでクラスや用途の変化を受け止め、越屋根の温度差換気と夏の夜の冷気で、LEED v5 Gold 相当・ZEB Ready 相当を目指す。

設計趣旨 約 314 字（課題は 300 字程度）。文字 3.6 mm なら 1 m 離れて読める

## 立地と応答

**比叡（東から 24°）**
小さな図＋
冷気→本館は東向き
越屋根で夏の夜に冷やす
築山の頂から望む


**高野川と崖 4〜5 m**
小さな図＋
修景地域の右岸→
川へ下がる屋根・植栽帯
浸水 1.5 m→大学へ避難

**扇状地と用水**
小さな図＋
用水を借りた小川と築山
＝園内の高野川と比叡

**西の細い道と住宅**
小さな図＋
西館の屋根を西で低く
車は突き出た木より南で

**模型写真　A4（入口の一枚）**
園庭からこどもの目線（模型で約 10 mm）
縁側・深い庇・比叡の方向を見る
選抜で最初に目に入る位置

## 配置図　1/200　周辺の道路・樹木・高野川・駐車

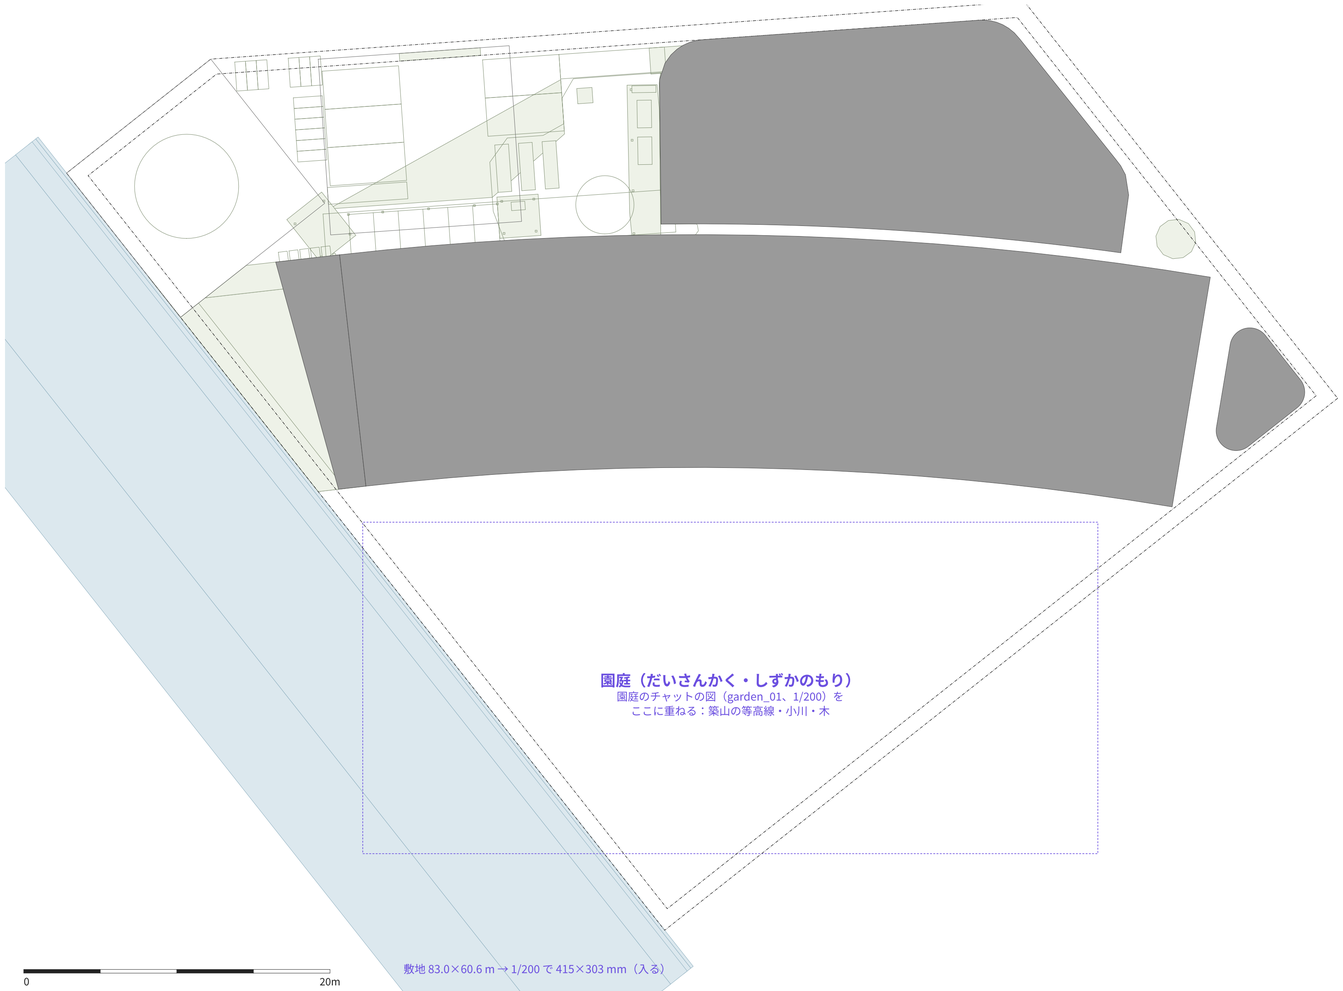



**模型写真　鳥瞰**
敷地と高野川・崖・公園・西の道
配置図と同じ向き（北が右）にそろえる

［割付の注記］フォーカス：この案が敷地から生まれたこと（比叡・高野川・扇状地・西の細い道）　／　目に入る順：模型写真（入口の一枚）→ タイトルと趣旨の冒頭 → 配置図 → 立地と応答

# こどもたちの育ち舎　2/5　こどもの一日　1 階平面



## 1 階平面図　1/100　道路・隣地境界線・家具。北が右、園庭が下

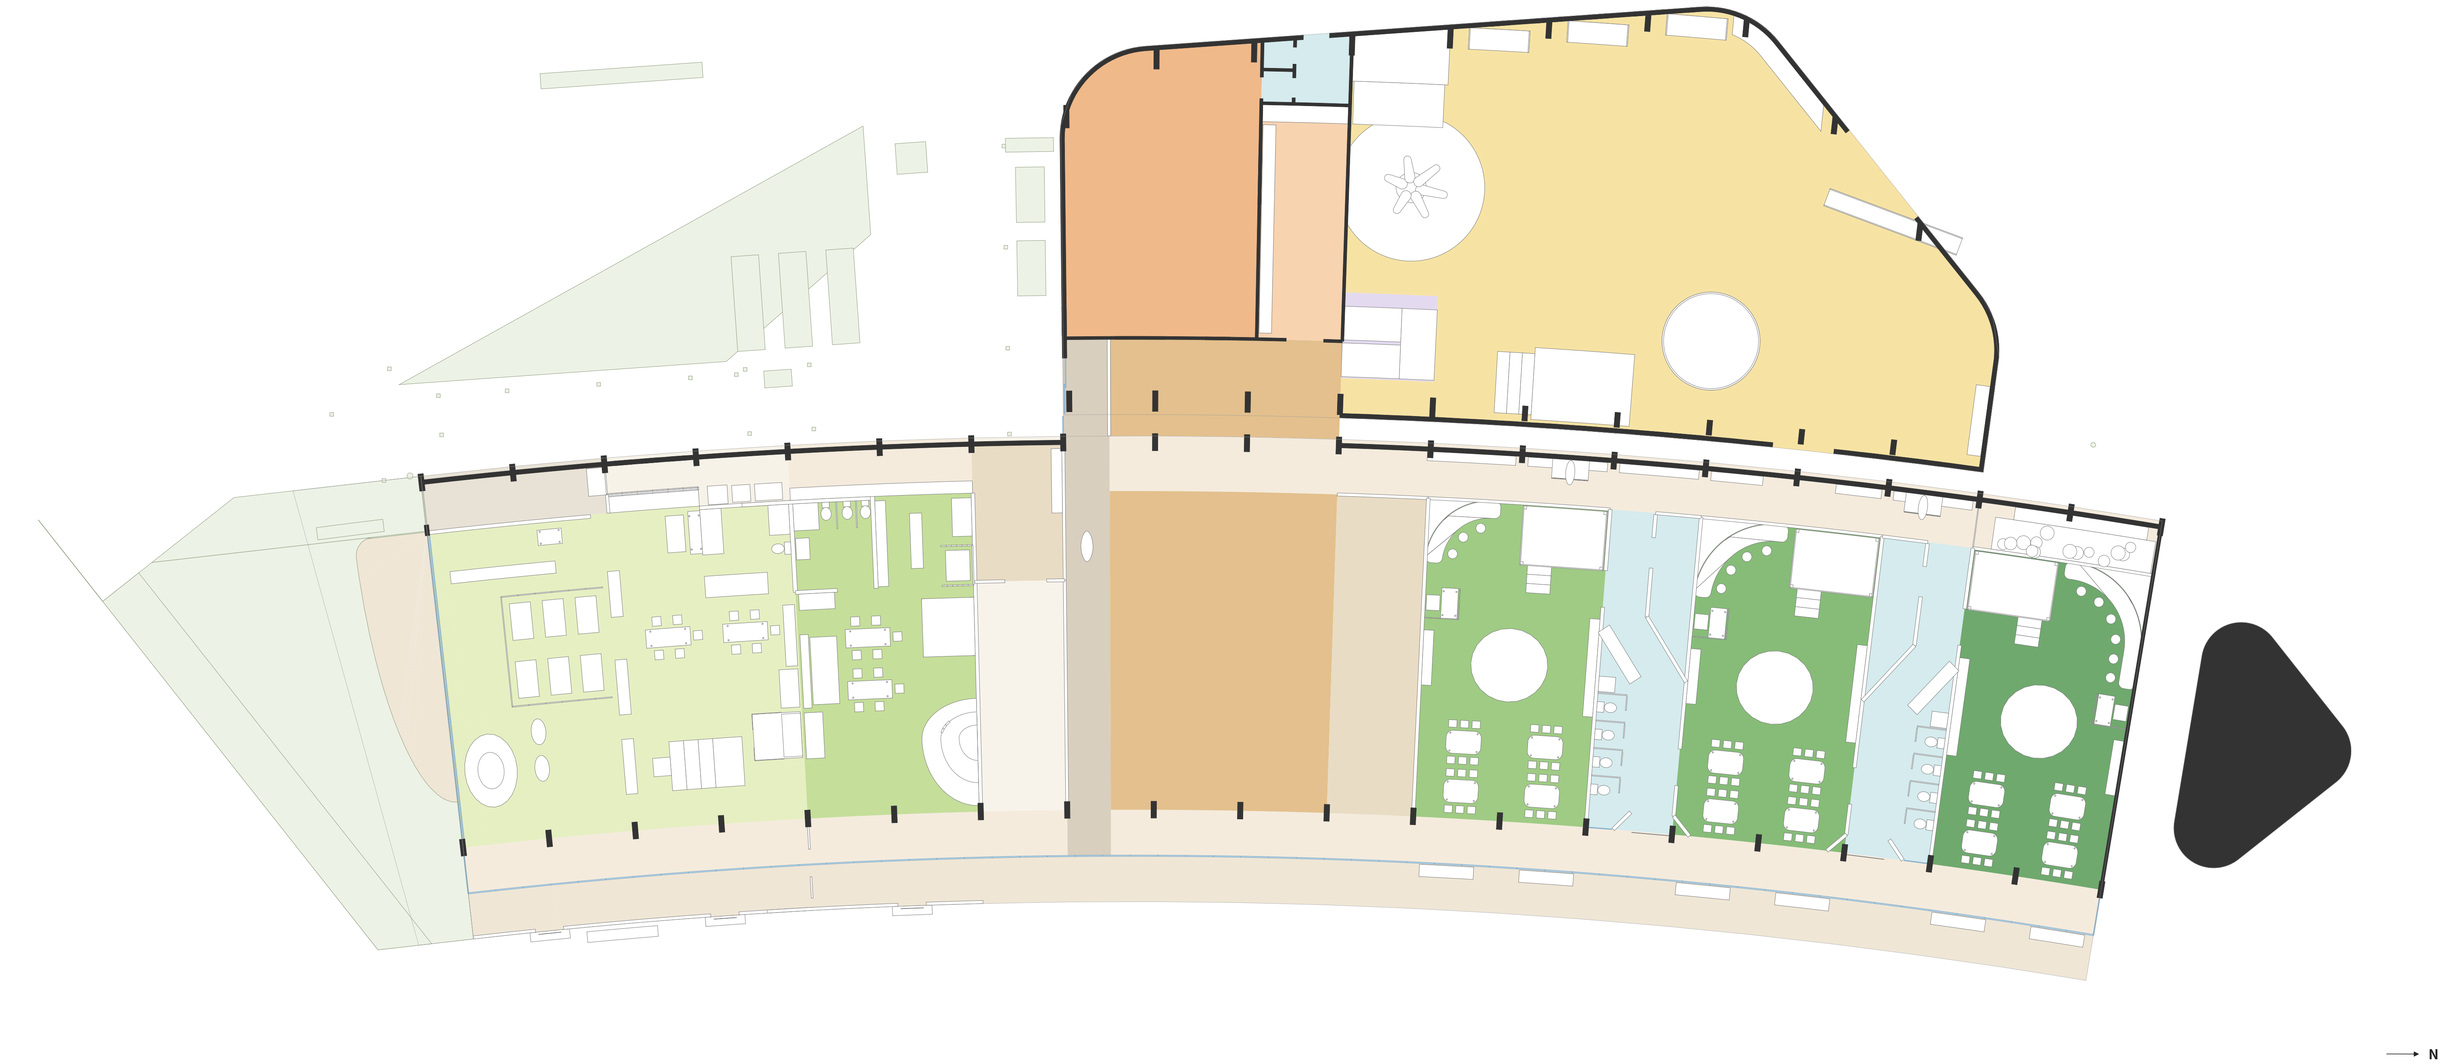



建物（庇・おむすび、みなみのさんかくまで）75.5×31.8 m → 1/100 で 755×318 mm。窓 799×410 mm に入る。西の道路の幅は 3dm に無いので描き足す

## こどもの一日　食べる・寝る・遊ぶ


一日の帯は 1/600 の小さな平面に色で（3dm から自動）

### 登園 8:00

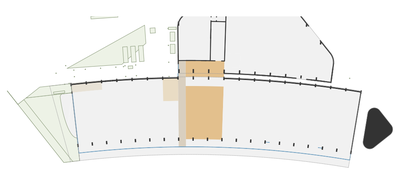


公園→木戸→小径→海峡／0・1 歳は受け取り土間

### 遊ぶ 9:30

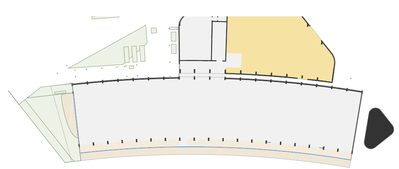


遊戯室・縁側・園庭・回遊のはしご

### 食べる 11:30

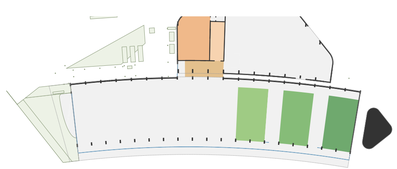


キッチンから海峡を通って配膳

### 寝る 12:45

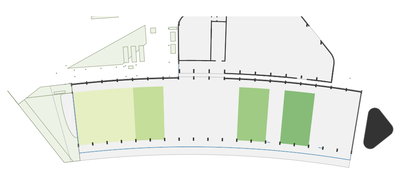

ねどこ・ロフトの下／5 歳は秋から段階的に

### 降園 16:30

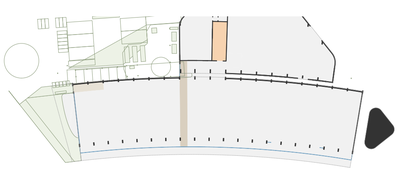

はれのまで延長保育／縁台でお茶


［割付の注記］フォーカス：こどもが一日を過ごす場所としての平面（家具・午睡・靴の線・歳とともに延びる道）　／　目に入る順：部屋の色 → 海峡とホール・キッチン → 縁側 → 家具 → 一日の帯

# こどもたちの育ち舎　3/5　どう見えるか　立面と縦断




## 東立面図（園庭側）　1/100　1階平面と同じ横位置

2枚目の真下に貼ると、平面と柱の位置が縦にそろう

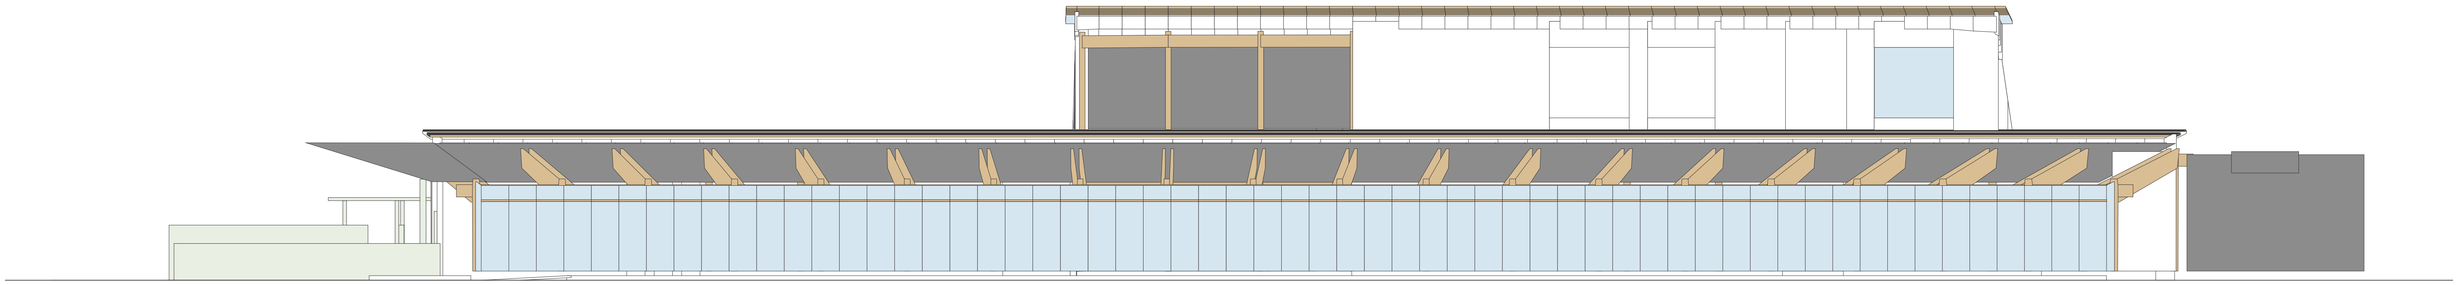

## 縦断面図 A　1/100　保育室の中ほど r=197 m で切って展開、西を見る

自動の断面Aをそのまま実寸で（model/drawings）

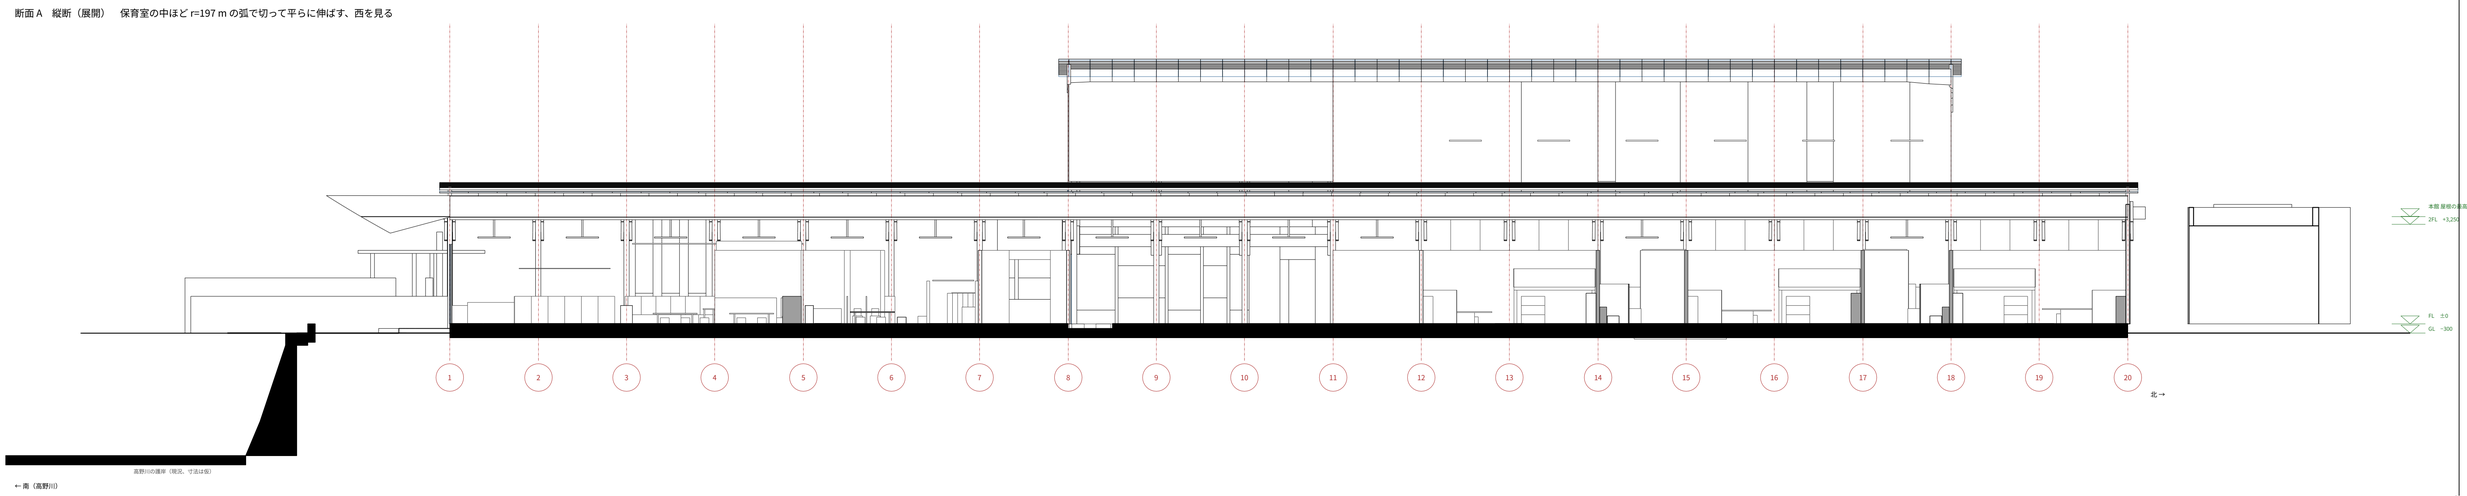



**模型写真　西の道から**
人の目の高さ 1.5 m（模型 15 mm）
低い軒と縦格子

**模型写真　公園の木戸から**
アプローチの入口
見送りの小径の奥にひろば

## 西立面図（道路側）　1/100　北が左

道の向かいの住宅の高さを点線で描き足す（圧迫感の説明）

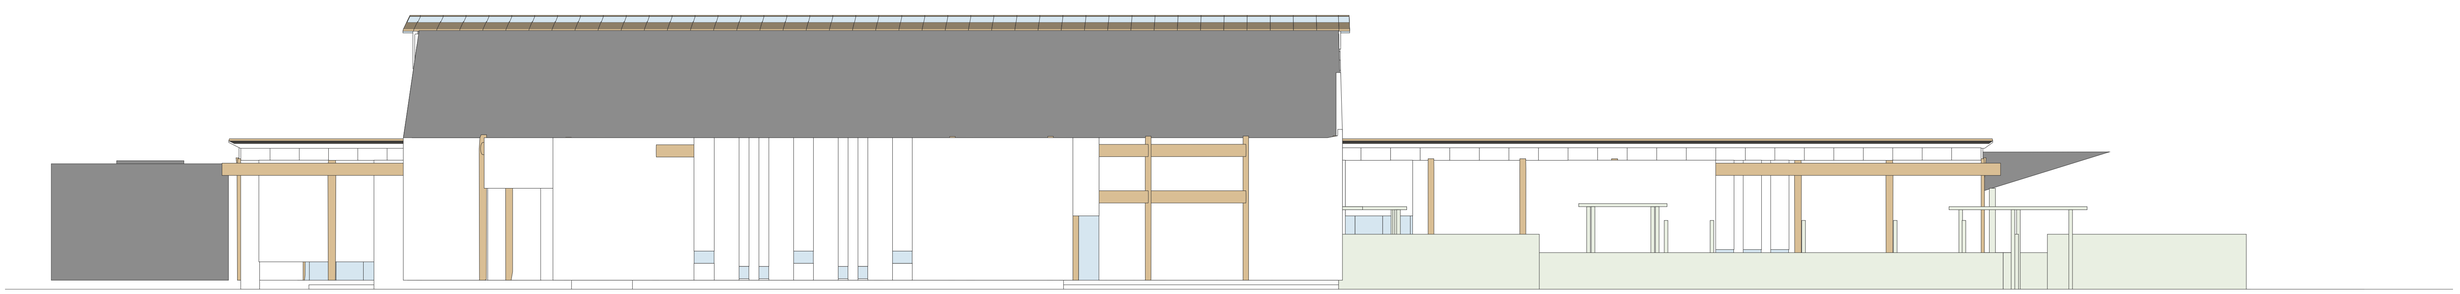


［割付の注記］フォーカス：57 m の縁側と深い庇のリズム（東）、街に対して低い構え（西）　／　目に入る順：東立面（平面の真下、柱がそろう）→ 縦断 → 西立面

# こどもたちの育ち舎　4/5　どう息をするか　断面と環境



## 断面図 C　4 歳・遊戯室　1/50（1/100 の自動の図を 2 倍）　西の道路から園庭へ

左右に 道・向かいの住宅／園庭・築山 を描き足す。空気の矢印と①〜⑨を重ねる。断熱は帯で

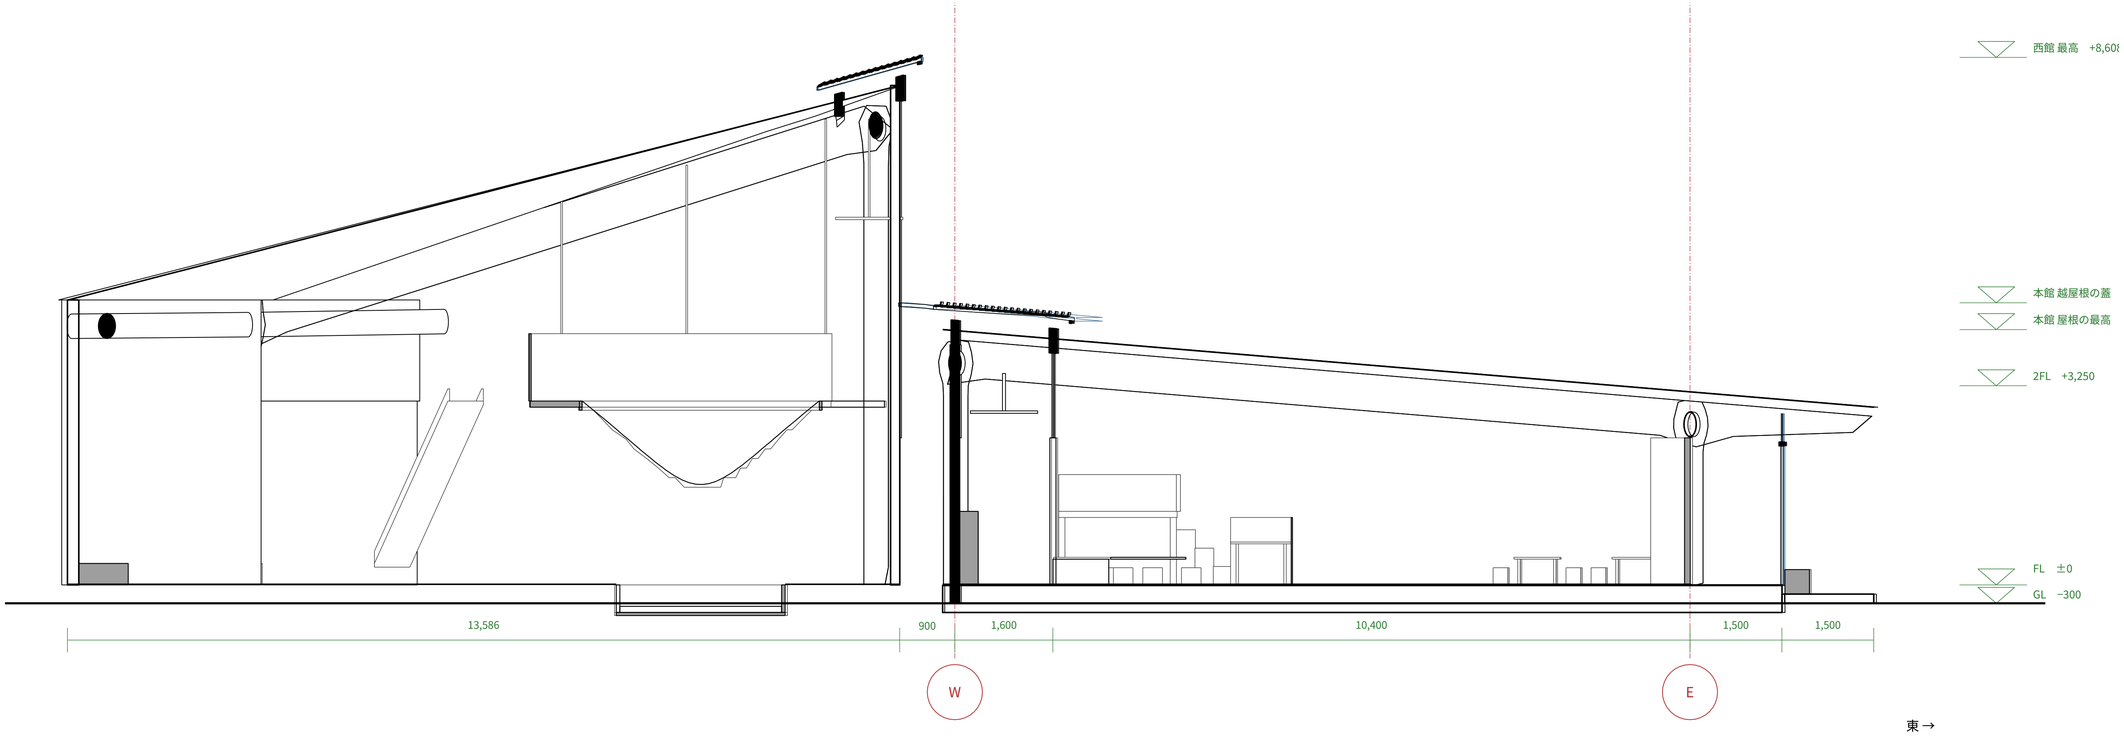


**環境の枠**
LEED v5
Gold 相当
ZEB Ready
相当

脱炭素 ①〜⑤
生活の質 ⑥⑦
生態系 ⑧⑨


### 夏の昼
庇で遮る・越屋根から抜く

### 夏の夜
比叡の冷気で冷やす（自動の窓）


### 春・秋
手で開ける（表示灯）

### 冬
床暖房・熱交換の換気・断熱

## 断面図 B　海峡　1/100　南の入口・キッチン・2 階・すき間・本館・縁側

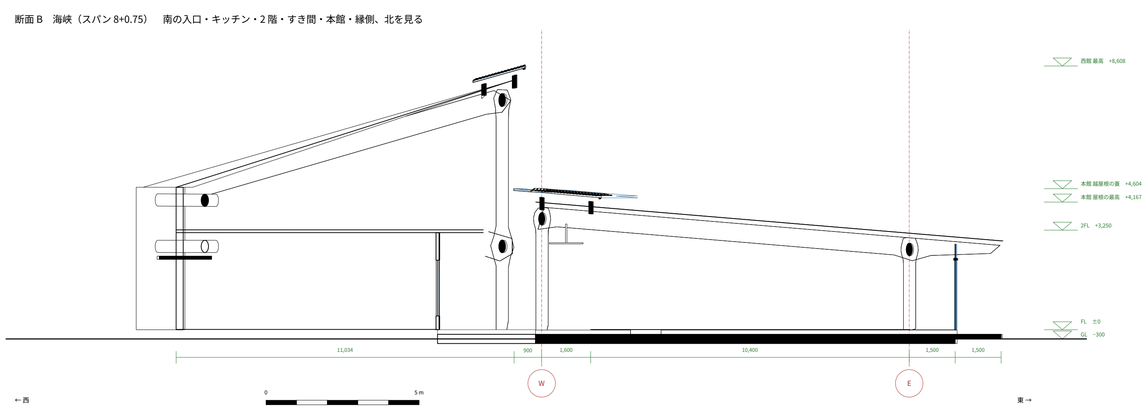


## 2 階平面図（西館）　1/100

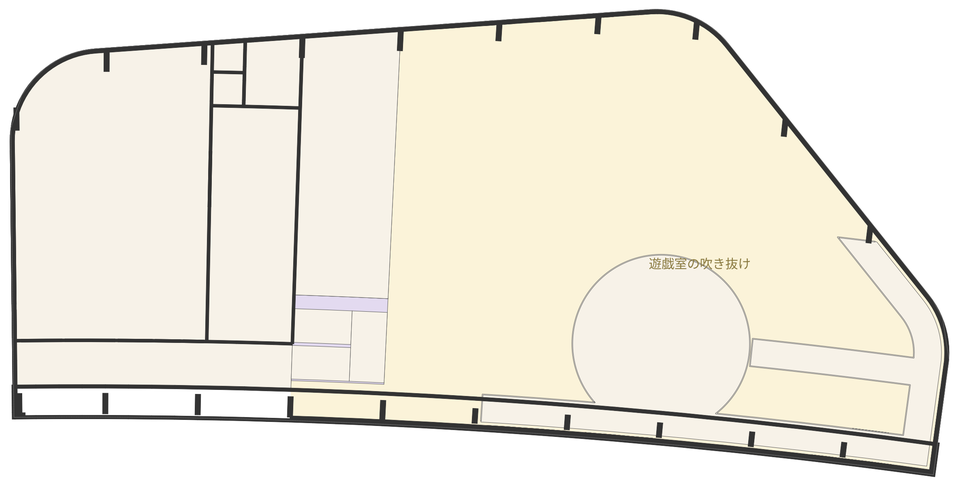


西館 33×17 m → 326×172 mm（1 階平面と同じ向き）

［割付の注記］フォーカス：空気・光・熱の流れが形の理由になっていること（断面 C を主役に）　／　目に入る順：断面 C 1/50 → ①〜⑨ と環境の枠 → 運転表 → 断面 B → 2 階


# こどもたちの育ち舎　5/5　暮らしと構造




**内観　ホール（A4）**
海峡と飛び石・オープンキッチン
梁の見える天井・越屋根の光の線
（レンダリングか模型写真）

## 同じ部屋の一日　3〜5 歳の保育室　断面 1/100


**10:00**
遊ぶ

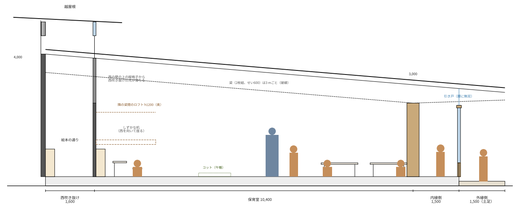

**11:30**
食べる

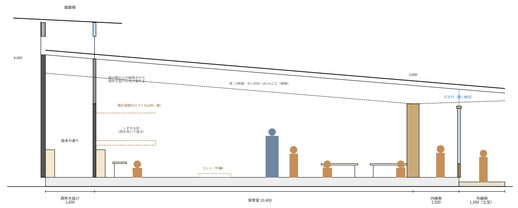



**13:30**
寝る

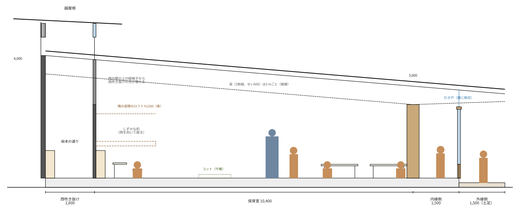

今は同じ図（既存の 1/50 を縮小）。時刻ごとに家具・人・光を描き分ける

## 遊戯室　平面・断面（縮小、遊戯室のチャット）

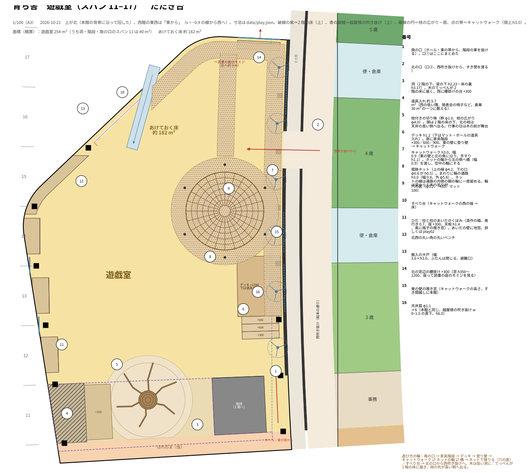


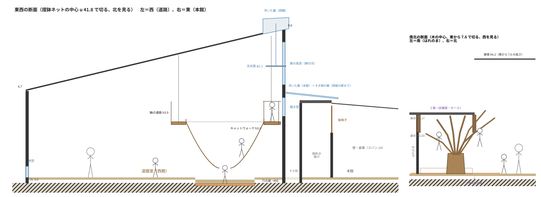







## 接合部　タメディア型　２枚の梁で柱を挟む（縮小）

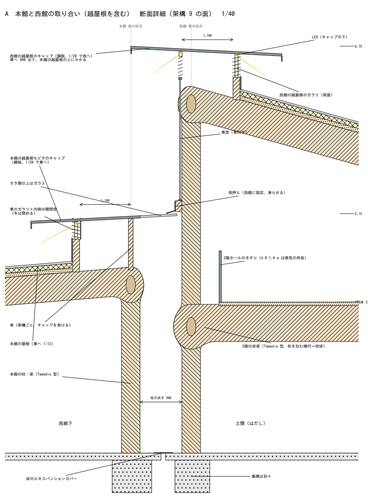

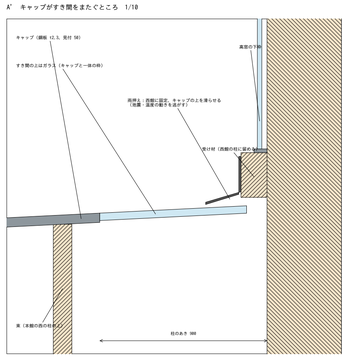

* 本館の越屋根は、西館と接する北寄りは西のガラスなので、キャップも西館の壁まで延ばして
すき間のよけガラスを取り付ける（すき間のよけガラス）。外から見る越屋根の形は変わらず見える。
内部では壁の中央で見えなくなる。雨仕舞は、キャップ上面に 2.3mm 銅板の水下を設けて本館の越屋根に重ねる。
（よけガラスの下端は、本館の柱・梁（Tamedia 型）を避けるため、西館の高窓の下端より 100 mm 上げる。
西館の 3 階床面（天から 3600 ほど、特注品の木製窓）に対して、無理なく取り付けられるようにした。

**京都の間伐材・金物を減らした接合**

**スケルトン＆インフィル**
３ｍスパンの骨格（固定）と
間仕切り・家具（可変）を色分け

今／定員が変わる／
学童・地域の場 の３コマ

## 園庭の断面　縮小（園庭のチャット）

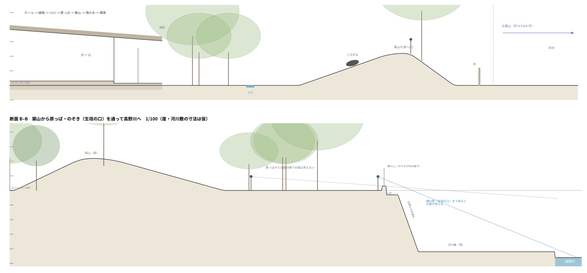

**築山・小川・水遊び場は遊ぶの答え**

## 面積表　㎡（仮）

| 室 | 要求 | 計画 |
|---|---|---|
| 乳児室（0・1 歳） | 約 60×2 | 120.7 |
| 保育室（2 歳） | 約 60 | 60.3 |
| 保育室（3 歳） | 約 60 | 60.3 |
| 保育室（4 歳） | 約 60 | 60.3 |
| 保育室（5 歳） | 約 60 | 60.3 |
| 遊戯室 | 240 以上 | 237.9 |
| 調理室 | 約 60 | 60.5 |
| 医務室 | 約 30 | 21.6 |
| 事務室 | 約 60 | 43.5 |
| 休憩・会議（2 階） | 60＋30 | 111.1 |
| はれのま | （追加） | 21.9 |

3dm の床から自動で測った仮の値。
医務・事務の不足を確かめる。
園庭 350・駐車 5・延床 2,000・
倉庫 30・機械室 30 を本番で足す

［割付の注記］フォーカス：近づいて読む人のための細部：寝る・遊ぶ・組み方・変わり方　／　目に入る順：内観 → 同じ部屋の一日 → 遊戯室 → 接合部 → S&I → 面積表