育ち舎　園庭（だいさんかく・しずかのもり）　たたき台8

配置 1/200　断面 1/100（A2）　2026-10-21　遊具を置かず、木と地形で遊ぶ庭。山・川・原っぱ・森、そのあいだにたくさんのニッチ。

地形は GL（＝FL−300）からの高さ。等高線 0.2 m ごと（1 m を太く）。築山の位置と形はこの図で決め直した（Keynote の位置は前提にしていない）。

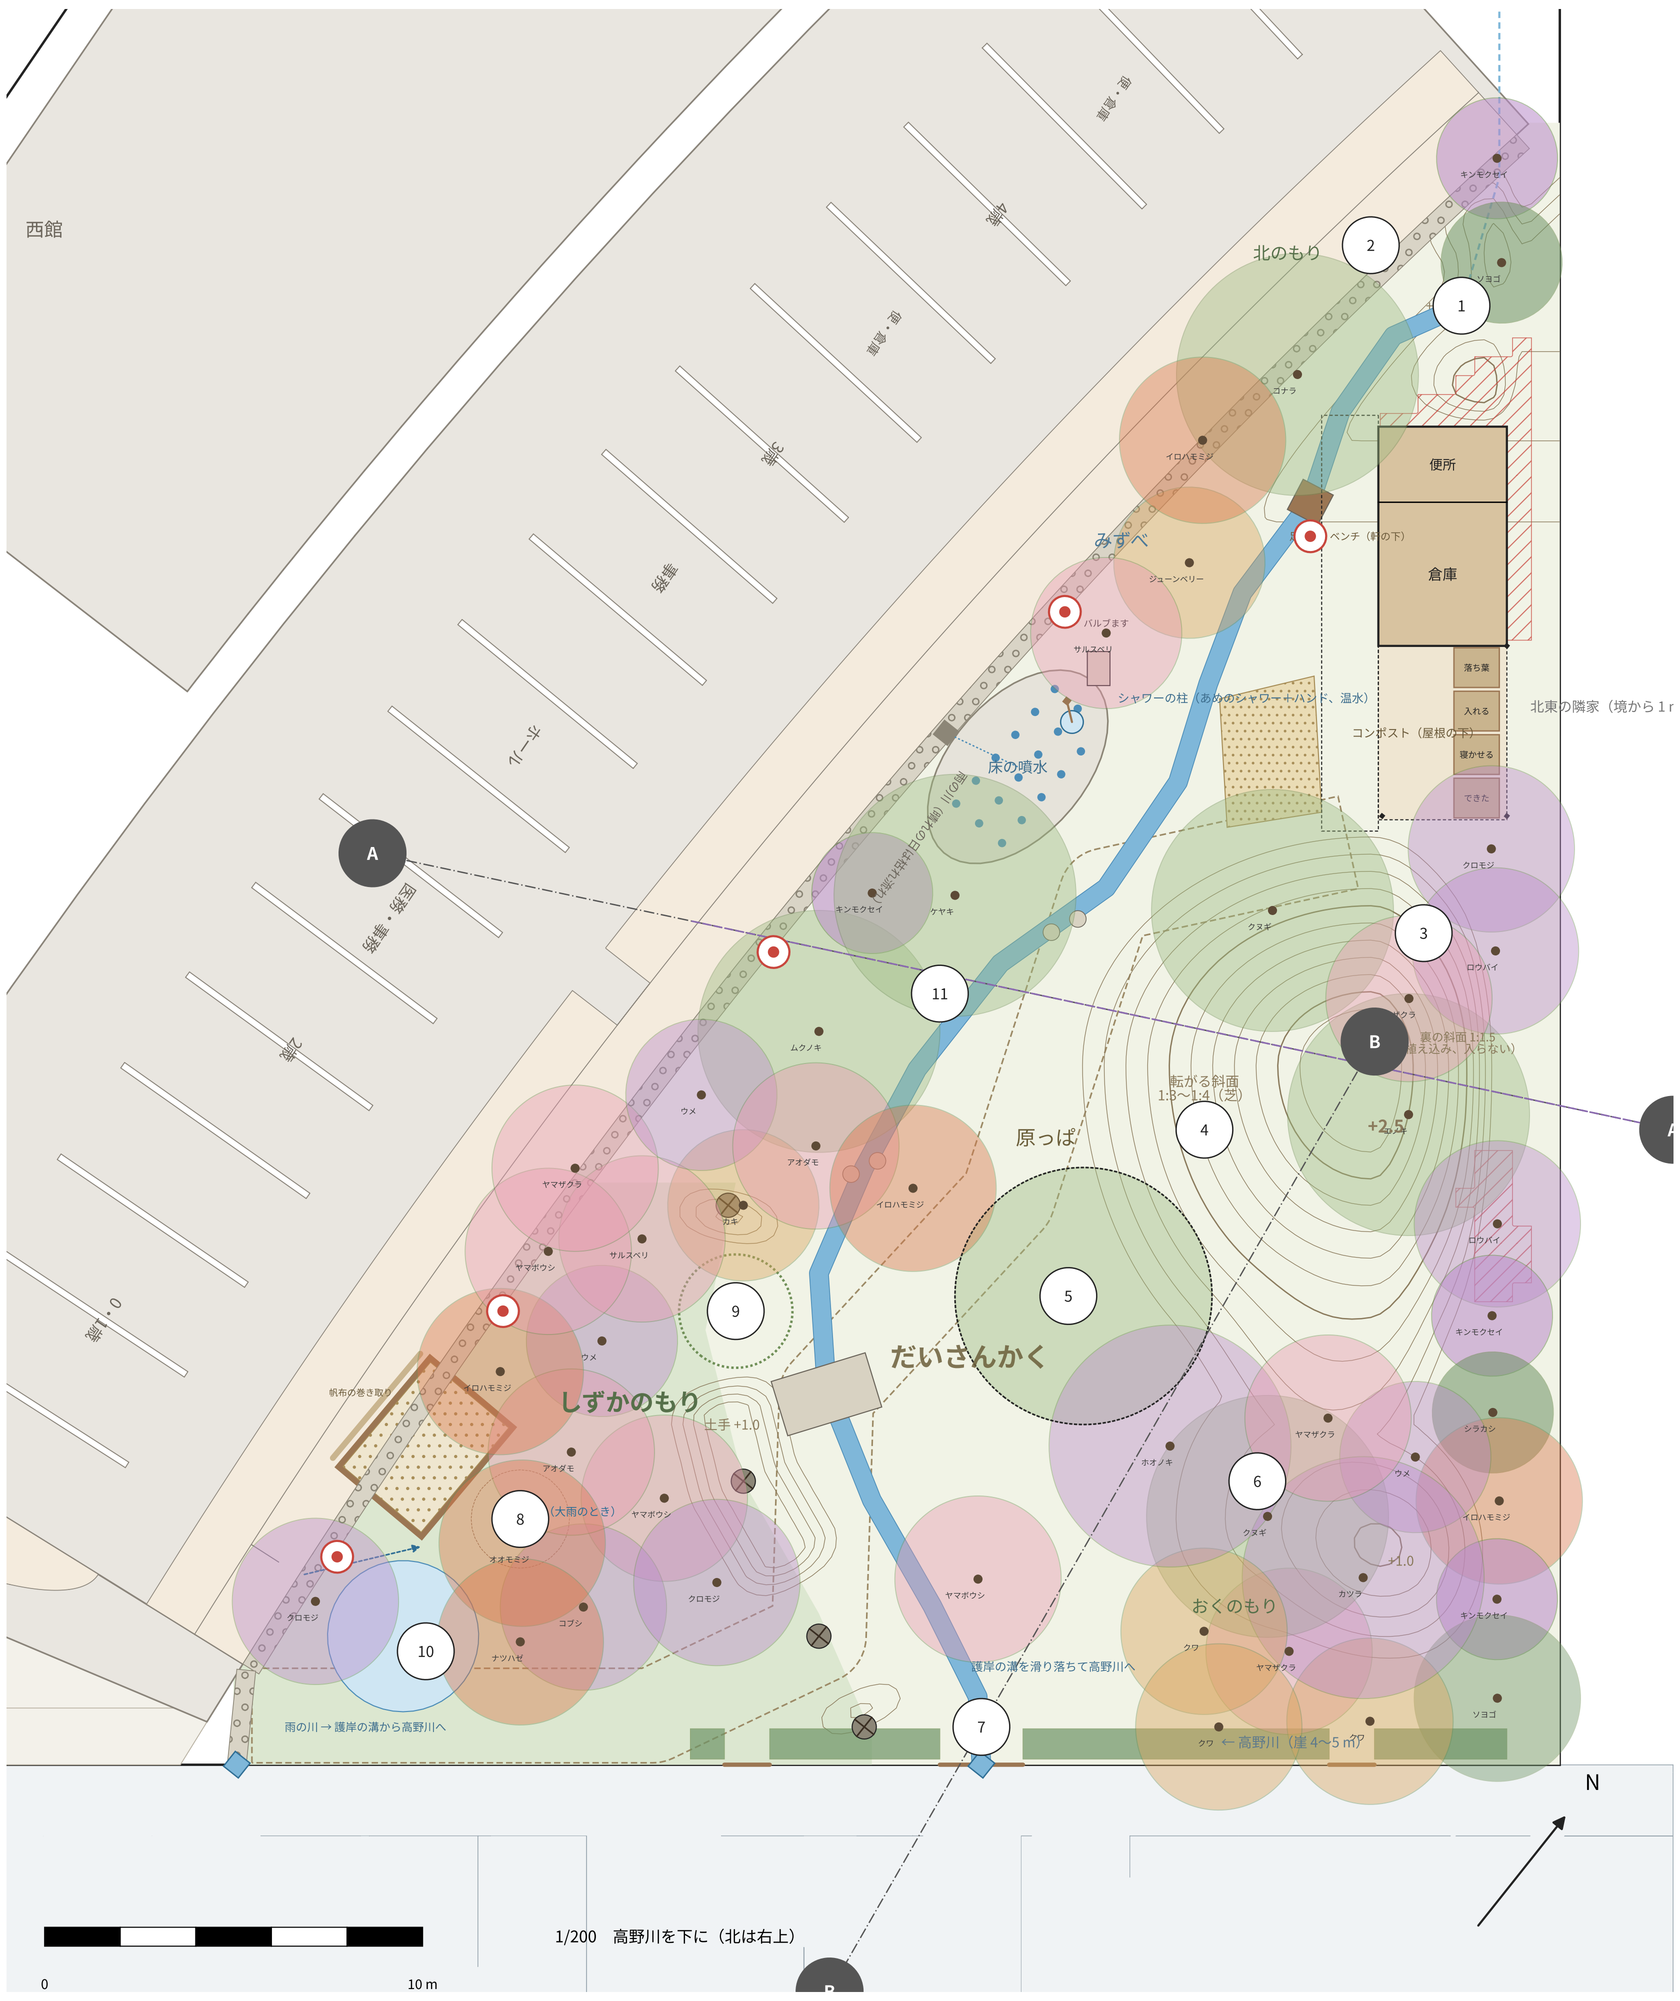
西館
便・倉庫
4歳
ホール
医務・事務
2歳
北のもり
みずべ
床の噴水
シャワーの柱（あめのシャワー＋ハンド、温水）
ベンチ（軒の下）
バルブます
便所
倉庫
落ち葉
入れる
寝かせる
できた
コンポスト（屋根の下）
北東の隣家（境から 1 r
転がる斜面 1:3〜1:4（芝）
裏の斜面 1:1.5（植え込み、入らない）
+2.5
原っぱ
だいさんかく
しずかのもり
帆布の巻き取り
土手 +1.0
(大雨のとき)
おくのもり
+1.0
雨の川 → 護岸の溝から高野川へ
護岸の溝を滑り落ちて高野川へ
← 高野川（崖 4〜5 m）
キンモクセイ
ソヨゴ
コナラ
イロハモミジ
ジューンベリー
サルスベリ
ケヤキ
ムクノキ
クヌギ
クロモジ
ロウバイ
ヤマザクラ
エノキ
ウメ
アオダモ
カキ
ヤマボウシ
オオモミジ
コブシ
ナツハゼ
ホオノキ
シラカシ
カツラ
クワ
A
B
N
0
10 m
1/200　高野川を下に（北は右上）

凡例

- ● 香り：ウメ 3・ロウバイ 2・クロモジ 3・キンモクセイ 4・カツラ 1・ホオノキ 1・コブシ 1
- ● 花：ヤマザクラ 4・サルスベリ 2・ヤマボウシ 3・アオダモ 2
- ● 紅葉：イロハモミジ 4・オオモミジ 1・ナツハゼ 1
- ● 実：カキ 1・ジューンベリー 1・クワ 3
- ● 常緑：ソヨゴ 2・シラカシ 1
- ● 木陰：エノキ 2・ケヤキ 1・ムクノキ 1・クヌギ 2・コナラ 1
- ○ 木登りの木（エノキ、下は木のチップ）
- ⊕ 関守石：しずかのもりの境。土手は低く越えられる。入口は柳の家をくぐる。「ここからはしずかに」と伝えて止める（ユーザー：物理的ではなく文化で）
- ▬ 小川（幅 0.5、岸は急、底は平らで浅い。終わりは護岸の溝を滑り落ちる、破線は暗渠）・水浴び場（円形 φ4.0、段なしの浅い皿）
- ▨ 床の噴水（水遊び場、上水をためずに一度だけ使う、排水は雨の川へ。ポンプなし、弁はシャワーの柱の隣のバルブます）
- ▨ 雨の川（雨落ちの溝、玉石。本館の雨は樋なしで落ち、南へ流れて護岸の溝から高野川へ。溢れたらすりばちが雨の池）
- ▨ 砂場・粒の遊び場（1〜2 mm、2.7×3.6 の木の縁、帆布を巻いた棒を転がして「おやすみね」とカバー）
- ― 等高線 0.2 m（太線 1.0 m）
- ⬚ 剪定・搬入の車の道（芝の保護材 幅 2.5、ふだんは庭）
- ◉ 先生のいる所（縁側の外の縁・小屋の軒、目の高さ GL+1.35）
- ▨ 死角：どの先生からも子どもの頭（地面+0.9）が見えない所

ニッチ（静かに遊べる・ひとりになれる所）

① みなもと：二つの丘のあいだから湧き出す石組み
② 丸太の輪：切り株の腰掛け（北のもり）
③ ほら：築山の北西の面の木の枠のくぼみ（3歳の縁側から見える向き）
④ 山の肩の平ら：腰掛ける段（丸太の土留め）
⑤ 木登りの木（エノキ）の根もと
⑥ おくのもり：低い起伏と倒木
⑦ のぞき：小川が護岸の溝を滑り落ちる所（生垣の口、柵ごしに高野川を覗き込む）
⑧ すりばち：小さなくぼ地（お話の輪）
⑨ 柳の家：小川のほとりの生きたヤナギのドーム、しずかのもりの入口
⑩ 水浴び場（0〜2 歳、上水）と粒の遊び場
⑪ 川辺の座り石

数字（この図から）

だいさんかく（しずかのもりを含む）約 886 m^2　うち しずかのもり 約 162 m^2（3〜5 歳 70 人で 1 人 10.3 m^2、基準は 3.3）

築山：頂 +2.5 m、裾の広さ 約 148 m^2、土 約 143 m^3。起伏・土手を足すと盛る土は 約 218 m^3

　→ 北のもりへの上り（最大 +0.7）・おくのもりの林床・土手 +1.0 も含めて締め固め 約 211 m^3。運び込まない。本館の床は床下空間（根切り GL−0.6、ユーザー）で、掘る土は 約 669 m^3（本館 約 539、西館ほか 約 85、園庭 約 41）

小川：地上の長さ 約 46 m、川床 +0.20 → −0.40（勾配 約 1/76）。水深 3〜5 cm で 約 4〜10 L/s（流れ 0.3〜0.4 m/s）。用水路の口の堰板で加減、大雨は水門を閉じる

木 47 本（24 種）。噴水の夏の日陰（7 月下旬）：9 時 55%、10〜13 時 約 41%（南東のケヤキ）、15 時 52%、16 時 95%（本館の影）。休むのは縁側の庇の下

床の噴水：約 17 m^2、噴き口 17 個（0.8 m ごと）＋シャワーの柱。上水、排水は雨の川へ。雨の川：屋根 約 880 m^2、100 mm/h で南の端 約 24 L/s、溝 0.5×0.2・1/200 で 約 50 L/s（目安）

小屋：便所 6.8＋倉庫 12.9＋コンポストの間 15.6 m^2（一つの屋根）。倉庫は教材庫×2（13.0）＋遊戯室の道具入れ（5.7）に足して 30 m^2 を超える

コンポスト：小屋の倉庫の南東、屋根の下の壁のない間に木枠 4 つ（落ち葉・入れる・寝かせる・できた、全体 約 4.6×1.2）。4・5 歳の当番がキッチンから野菜くずをもらい、落ち葉と重ね、できた土を入口の前の菜園へ運ぶ（ユーザー）

土の使い道（ユーザー：無理なく使える分だけ）：表土 約 147 m^3 は全部敷地に残す（築山の表面 0.2・木の下の林床 0.15 約 525 m^2・菜園）。下の土は築山の芯・土手・林床の盛り・西館の床の下へ。外へ出すのは下の土 約 301 m^3（近くの工事へ）

死角：約 33 m^2。築山の裏（隣家側）の植え込みと、北のもりの奥。植え込みは入らない所にする

断面 A–A　ホールから築山の頂を通って比叡山の向きへ　1/100

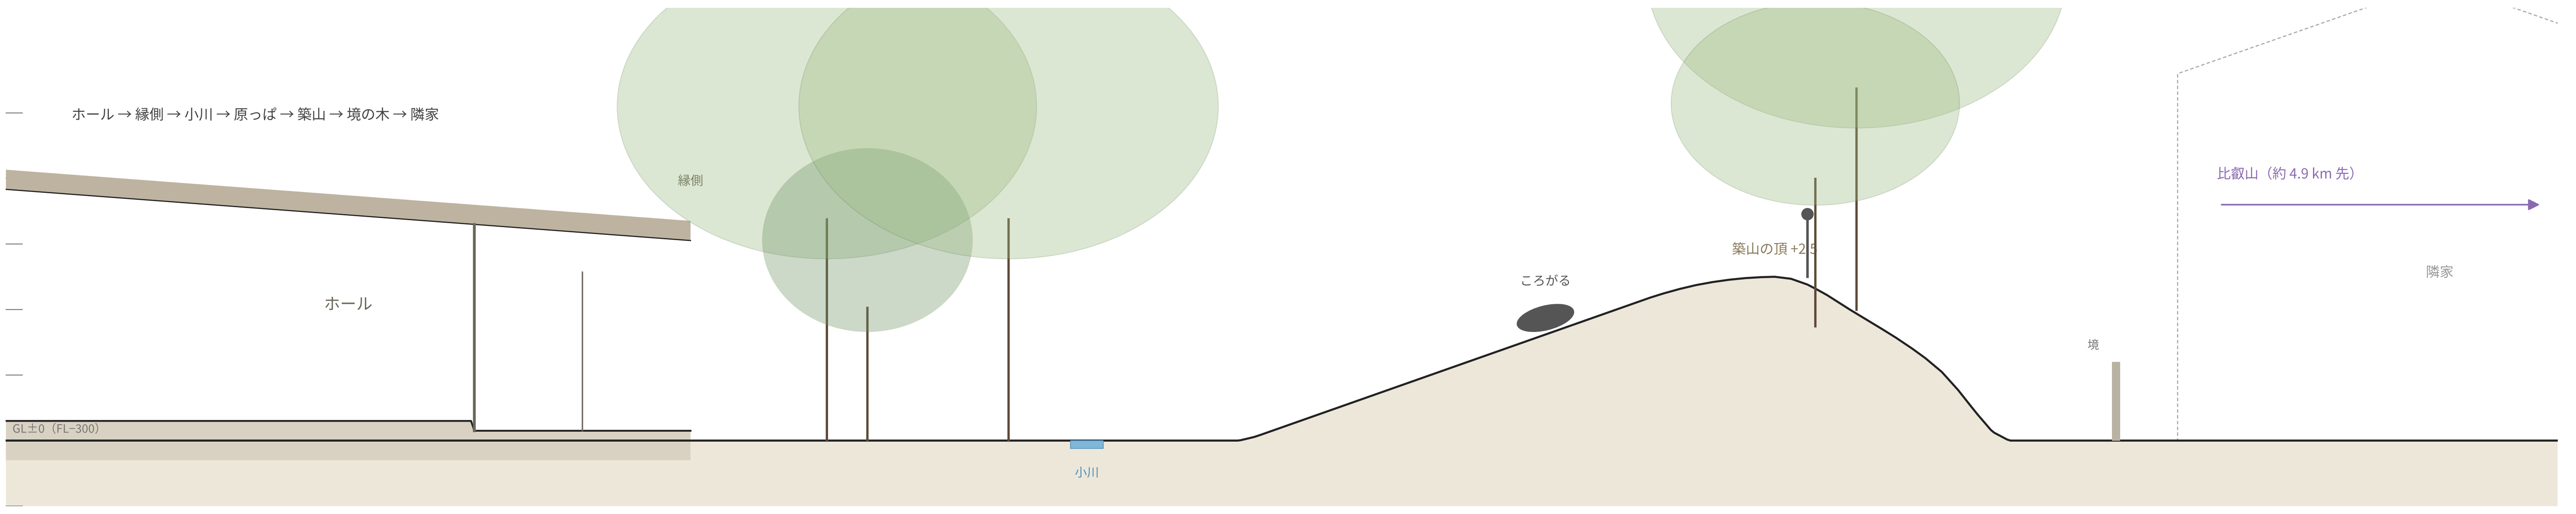
ホール → 縁側 → 小川 → 原っぱ → 築山 → 境の木 → 隣家
縁側
ホール
GL±0（FL−300）
小川
ころがる
築山の頂 +2.5
境
隣家
比叡山（約 4.9 km 先）

断面 B–B　築山から原っぱ・のぞき（生垣の口）を通って高野川へ　1/100（崖・河川敷の寸法は仮）

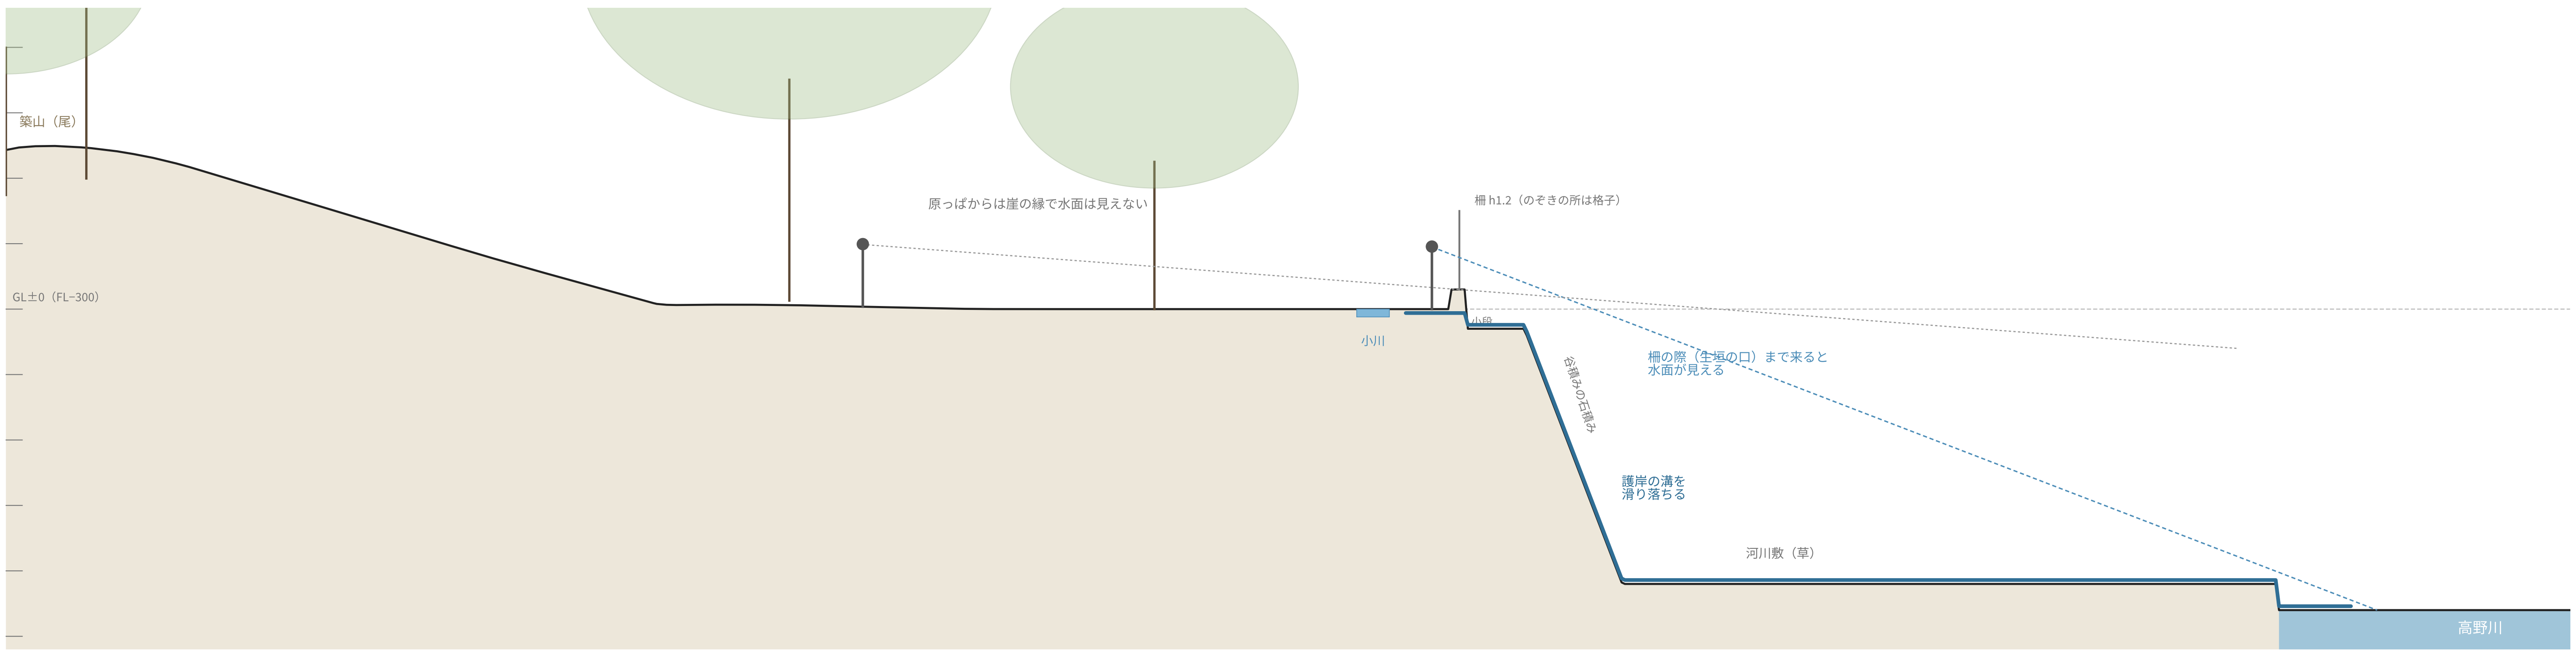
築山（尾）
GL±0（FL−300）
原っぱからは崖の縁で水面は見えない
柵 h1.2（のぞきの所は格子）
小川
小段
谷積みの石積み
柵の際（生垣の口）まで来ると水面が見える
護岸の溝を滑り落ちる
河川敷（草）
高野川

保母さんが困らないように（木と地形の約束）

- 高木は枝下 2 m 以上に仕立て、目の高さを見通す。低木は 60 cm 以下（大人は上から見える、子どもは隠れられる）。
- 縁側の外の縁と小屋の軒から全体が見える。見えない所（赤の斜線）は植え込みで入らない所にする。
- 毒・とげ・かぶれの木は使わない（キョウチクトウ・イチイ・アセビ・ピラカンサ・ハゼ・エゴノキ・ジンチョウゲ・ツツジ類 など）。ロウバイは種に毒があるので、築山の裏の入らない植え込みだけにし、花のあとに実を摘む。
- ツバキ・サザンカは植えない（チャドクガ）。落葉樹が中心、落ち葉は遊びに使い、掃くのは小径と縁側の前だけ。
- 木登りの木は決めておく（2 本まで）。下は剪定の枝でつくった木のチップ（剪定 → チップ → 根もと、を園の中で回す）。
- 水は浅く（小川 3〜5 cm）、床の噴水は水がたまらず外縁側のすぐ前（濡れたまま縁側へ、シャワーの柱）。子どもが手や口にふれる水は上水だけ（小川の水は飲まない、遊んだら足洗い場で洗う）。
- 縁側の前 1.5 m は木を植えない（出入りと見通し）。車の道の筋（幅 2.5）は木と起伏を置かない。

こどもたちの育ち舎　garden01.py（data/garden.json・sodachiya_exact_mesh.3dm から）