

A　本館と西館の取り合い（越屋根を含む）　断面詳細（架構 9 の面）　1/40

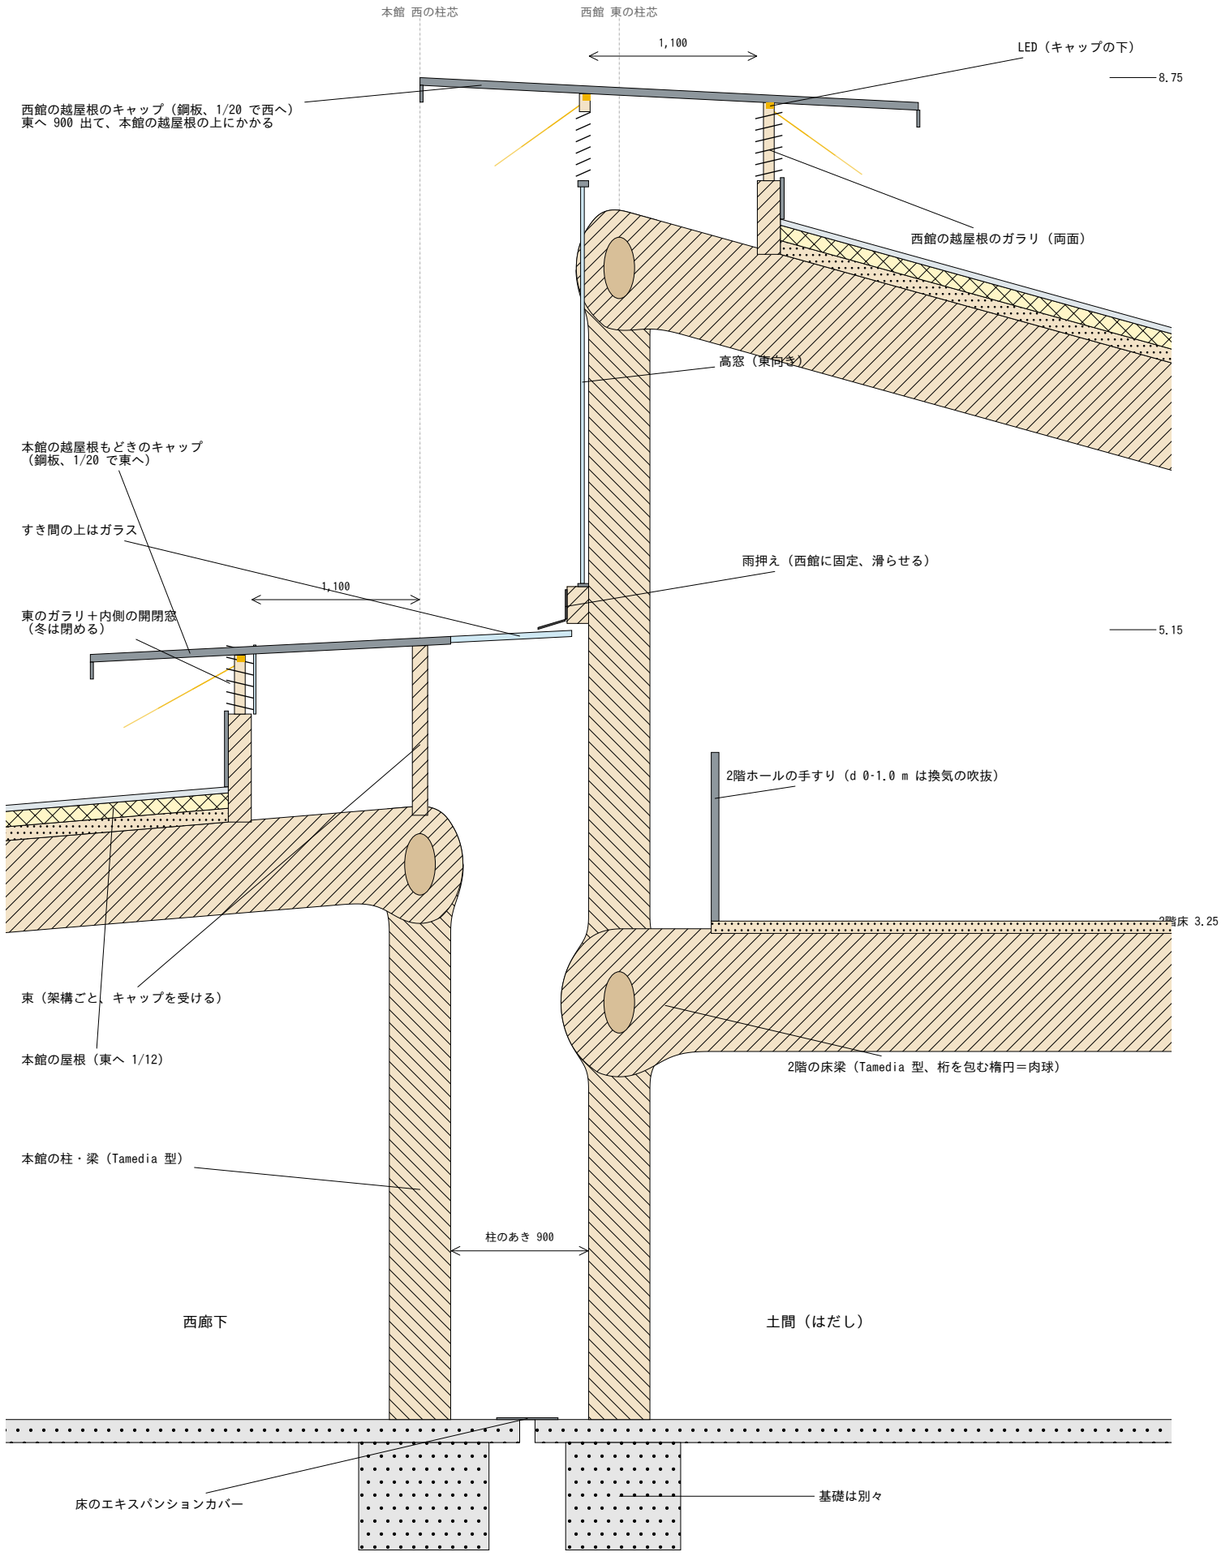


A’　キャップがすき間をまたぐところ　1/10

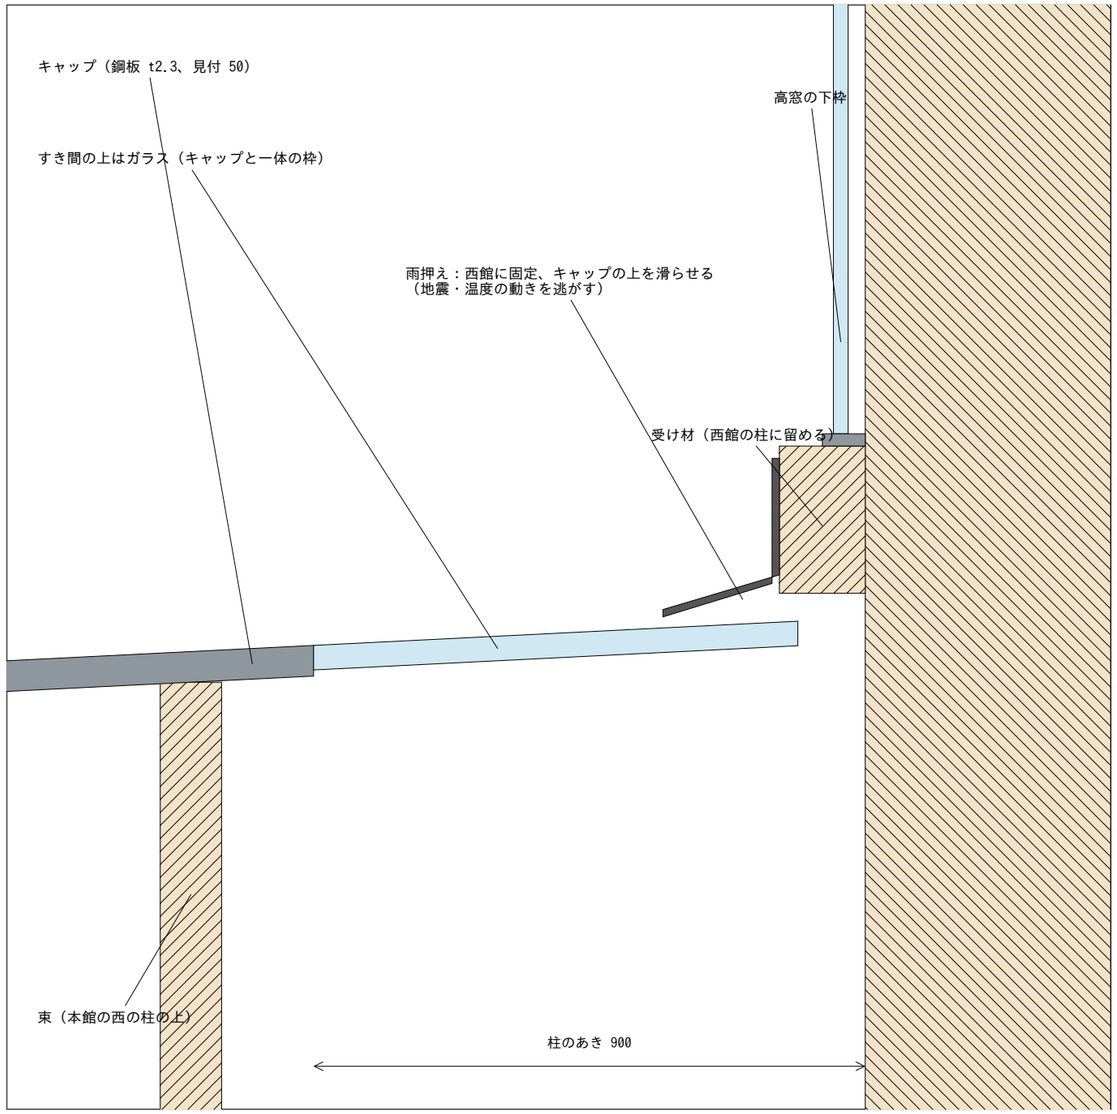

・本館の越屋根は、西館と接する区間では西のガラリをやめ、キャップを西館の壁まで延ばして
　すき間の屋根を兼ねる（すき間の上はガラス）。外から見る越屋根の形は端から端まで続く。
・西館の越屋根は屋根の頂点（東の縁）、換気の吹抜の真上。キャップは東へ 900 出て本館の越屋根に重なる。
・水はどちらのキャップも外へ流れ（本館は東、西館は西）、すき間には落ちない。
・LED はキャップの下。夜は低く長い線（本館）と高く短い線（西館）の二段の光になる。
・西館の 2 階床梁（せい 800）は、桁を包む木を厚く（280）して、楕円が梁の下に出るようにした。

B　南端の取り合い　平面詳細　1/50

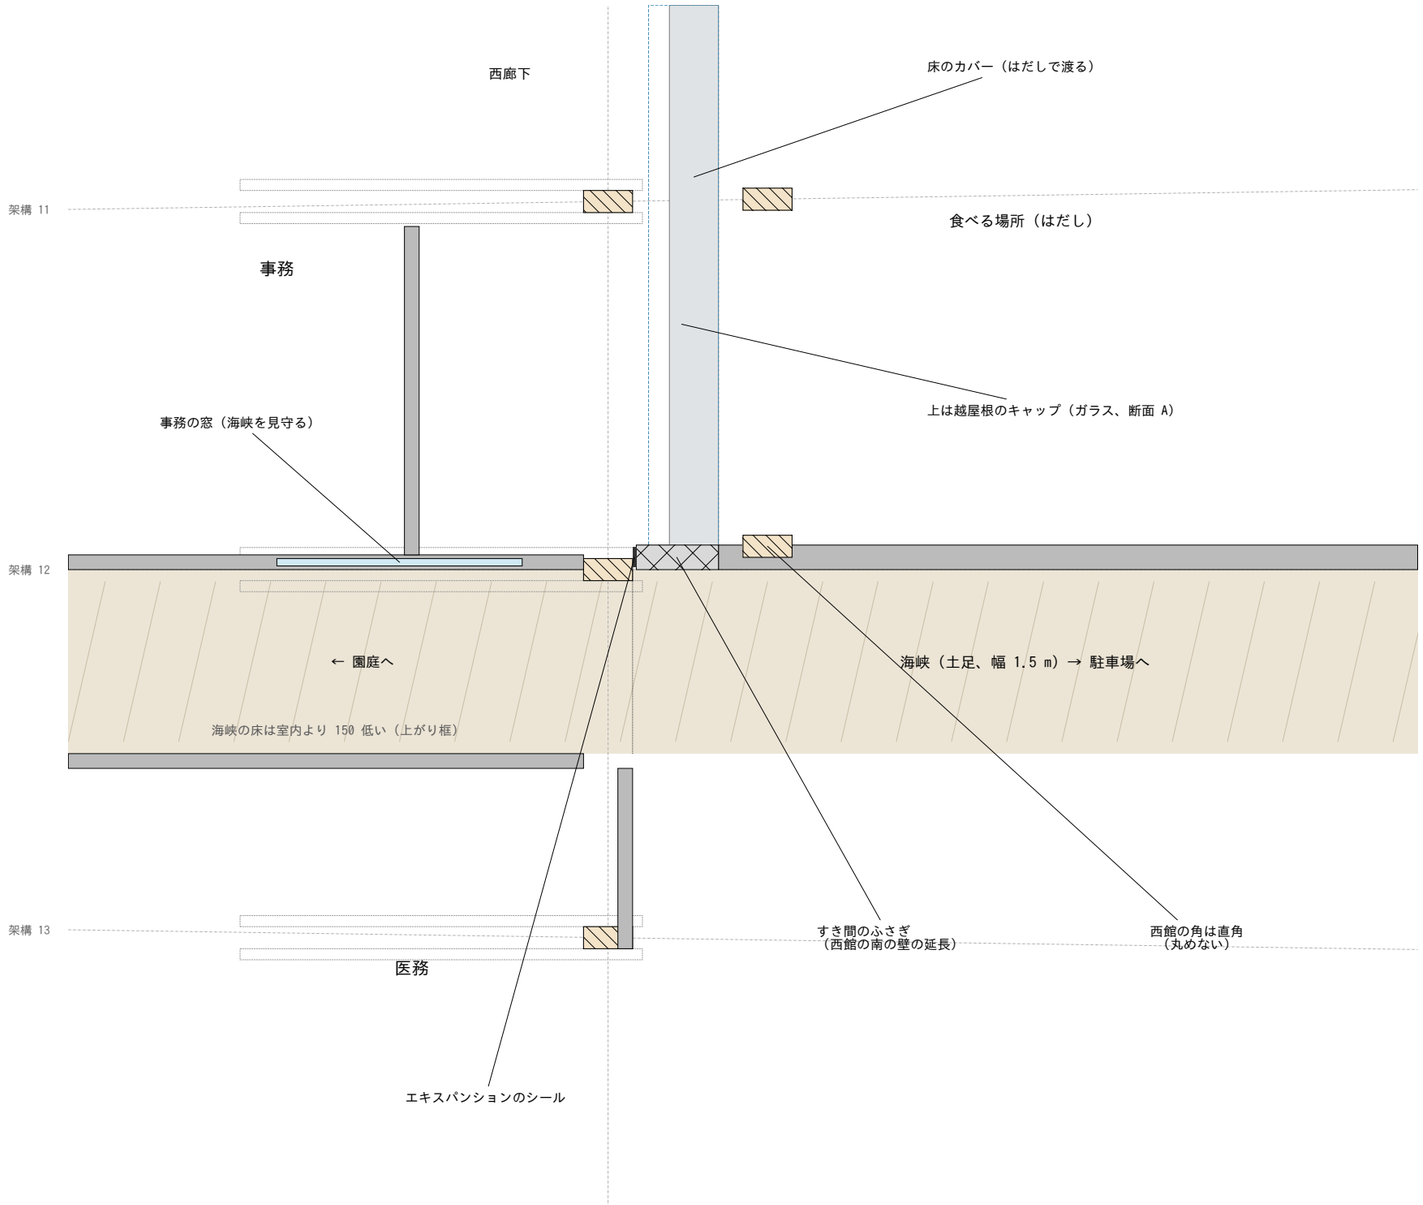

・円弧は短い区間なので直線で近似して描いている（3 m で 5 mm のずれ）。
・海峡の 1.5 m を医務と事務のどちらから取るかは未定。図では医務の側から取っている。
・北端の取り合いも同じ考え方（西館の北の妻の壁を架構 2 の線にそろえ、すき間をふさぐ）。