
育ち舎　0・1歳の部屋　家具配置（たたき台）

1/100（A3）　2026-10-19　西の背骨（r=205）を上下に、北を上寄りに描く。破線は頭上（軒・天蓋・物干し・天袋）と午睡時のコット。

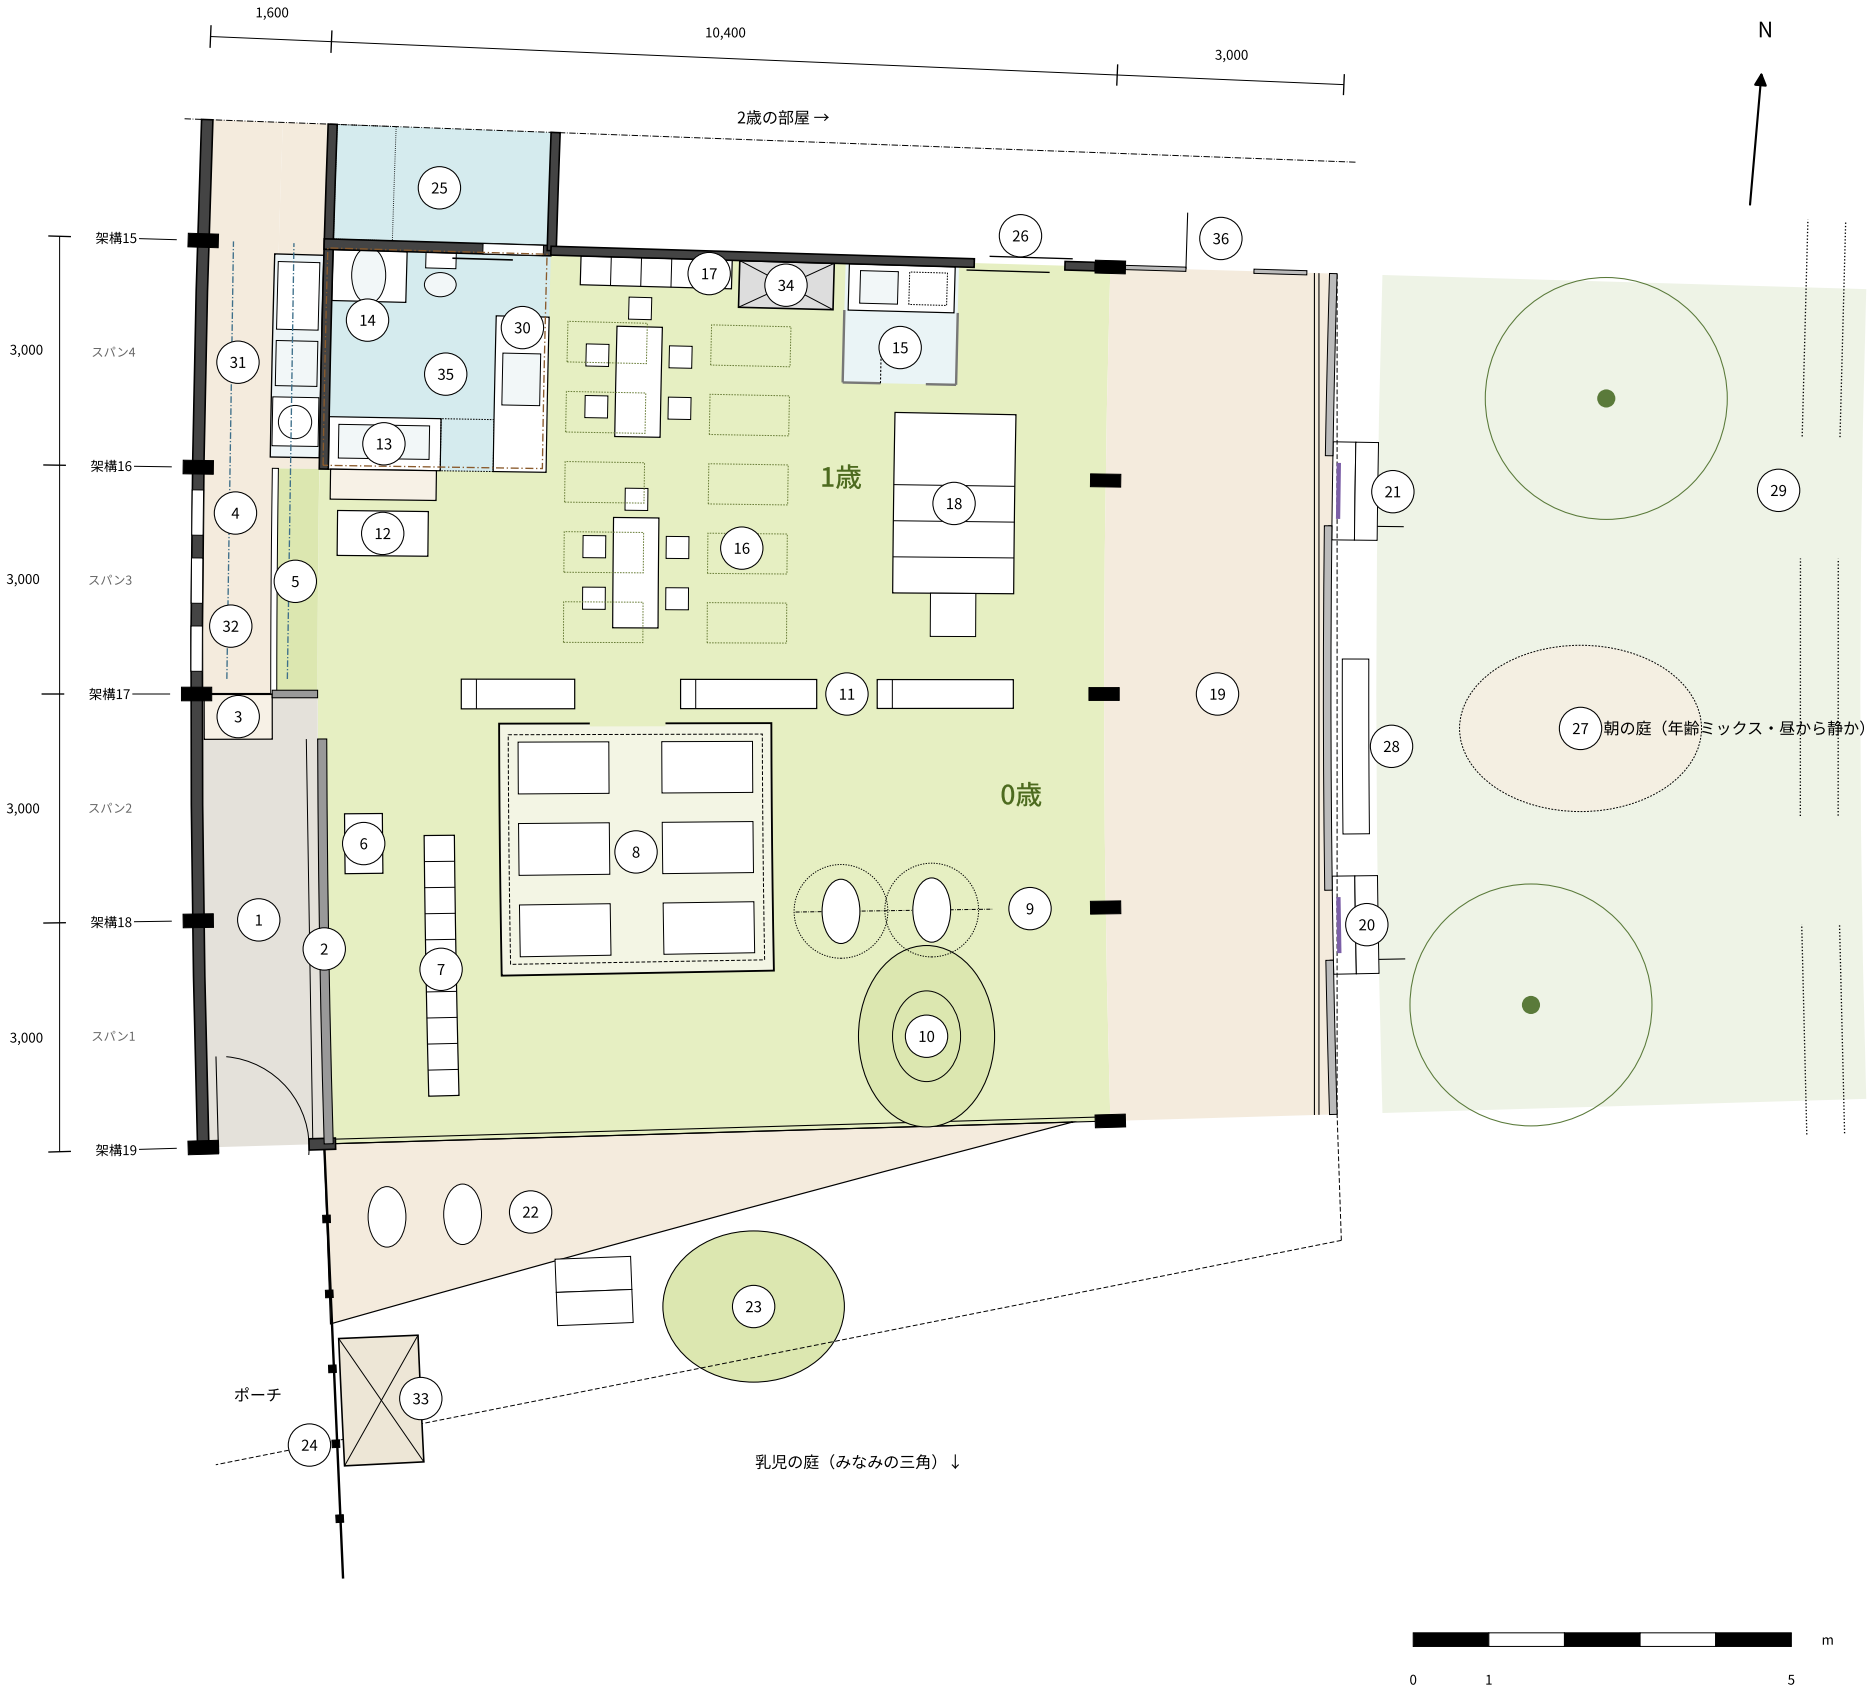

1　受け取り土間（GL＝FL−300）。南の妻の扉・くぐり戸・背くらべの柱

2　框＋腰壁 h600（受け渡しのカウンター）

3　式台 150＋木戸（2歳はここで靴を脱ぐ。木戸は先生が開ける）

4　2歳の道（幅 1.0、西の外壁沿い）

5　窓辺の小上がり h300＋格子の手すり h600。覗き窓は西の外壁。中は引き出し

6　受け入れ（検温・連絡帳の小机）

7　0歳の個人棚 h700（10人分）

8　ねどこ：ベビーベッド×6（ほかは床に布団）、囲い h900、布の天蓋

9　吊りかご×2（寝かしつけ用。架構18 の梁から4点吊り、破線は振れの範囲）

10　ほふくの丘（h200 のゆるい起伏）

11　動かせる低い棚 h600（0歳／1歳の境。寄せれば閉じる）

12　先生の腰掛ける机（座 h300・天板 h500、背はおむつ台の腰壁、座の下は収納）

13　おむつ替え台 h850（先生は北に立ち、部屋を向く）

14　沐浴槽・1歳の小さな便器・2歳トイレへの戸（背伸びの戸）

15　調乳コーナー（おむつと完全に分ける。シンク・冷蔵庫、柵 h900＋戸）

16　1歳の食卓 h350×2・椅子×10／午睡時はヒノキと帆布のコット×10（破線）

17　1歳の個人棚（二段、北の間仕切り沿い）

18　上り下りの段々（150×3）と短いすべり台

19　縁側（教室の一部）：引き込みのガラス戸＋格子の高欄 h900

20　高欄の戸（先生が開ける）と二段の縁（150×2）

21　「おひるね中」の暖簾（戸の上の軒先に掛ける）

22　南の縁側：外気浴（深い軒の下）

23　這い出せる一点（築山が縁側の高さまで上がる）と二段の縁

24　柵 h1.2（一本の線の延長）→ 非常用の門。西はポーチ

25　2歳のトイレ（参考、入口は東向き）

26　1歳⇔2歳の引き戸（朝夕の合同保育）

27　1–2 mm の粒の遊び場（夕方は「おやすみの布」）

28　大きい子の縁台 h300（高欄越しに目が合う）

29　土手＋生垣（切れ目から入る。奥行きは配置図で決める）

30　手洗い・おむつの棚 h850（水まわりの東の縁、腰壁を兼ねる）

31　洗濯：洗濯乾燥機・予洗いのシンク・たたむ棚（水まわりの配管壁に沿う）

32　物干し（昇降式の竹竿。西の吹き抜けの上、越屋根の下で乾かす）

33　外の物置（散歩車・砂場の道具。柵と一体、南の軒の下）

34　1歳のコットの収納（重ねて 10台）

35　天袋（水まわりの上。季節のもの・おむつの在庫・予備の寝具）

36　縁側の低い柵の戸（0・1歳／2歳の縁側の境）

面積（芯々、概算）　0・1歳の保育室 154.3 m²（縁側 33.6 を含む）　室内 120.7 m²（うち 0歳側 60.3、1歳側 49.0、水まわり 8.9、調乳 2.4）　窓辺 1.8　土間 9.6

基準の目安：ほふく室 3.3 m²/人 × 20人 = 66 m²。柱 400×180（黒）。室と縁側のあいだ（架構の東の柱の列）は開け放し。縁側の外のガラス戸が外壁。