こどもたちの育ち舎　1/5　敷地と園庭

地に足をつけて育つ

比叡から降りる冷気と高野川の流れが出会う松ヶ崎の扇状地に、こどもたちが地に足をつけて育つ場所をつくる。画面の中の疑似体験ではなく、木に抱きつき、土の中のミミズに驚き、生き物の生と死を間近に見る。弧を描く木造平屋の本館に 0 歳から 5 歳のすべての部屋を並べ、東の縁側と深い庇で園庭へ開く。園庭には用水を借りた小川と、比叡に見立てた築山を置く。玄関ホールに面したオープンキッチンを園の中心に据えて食べることを日々の求心力とし、野菜くずはこどもの手で土に還す。命に関わる危険だけを取り除き、自分の手と舌で世界を確かめる余地を残す。3 m スパンの木造架構によるスケルトン＆インフィルで用途の変化を受け止め、越屋根の温度差換気と夏の夜の冷気で、LEED v5 Gold 相当を目指す。

設計趣旨 約 331 字（課題は 300 字程度）。文字 3.6 mm なら 1 m 離れて読める

立地と応答

比叡（東から 24°）
小さな図＋
冷気→本館は東向き
越屋根で夏の夜に冷やす

高野川と崖 4〜5 m
小さな図＋
川へ下がる屋根・植栽帯
浸水 1.5 m→大学へ避難

扇状地と用水
小さな図＋
用水を借りた小川と築山
＝園内の高野川と比叡

西の細い道と住宅
小さな図＋
西館の屋根を西で低く
車は突き出た木より南で

模型写真　A4（入口の一枚）
園庭からこどもの目線（模型で約 10 mm）
縁側・深い庇・築山の向こうに比叡の方向
選抜で最初に目に入る位置

配置図　1/200　高野川を下に（川向こうから見る向き、北は右上）

点線の枠＝園庭のチャットの配置 1/200（garden01）を実寸で重ねた。本番は一枚に描き直す

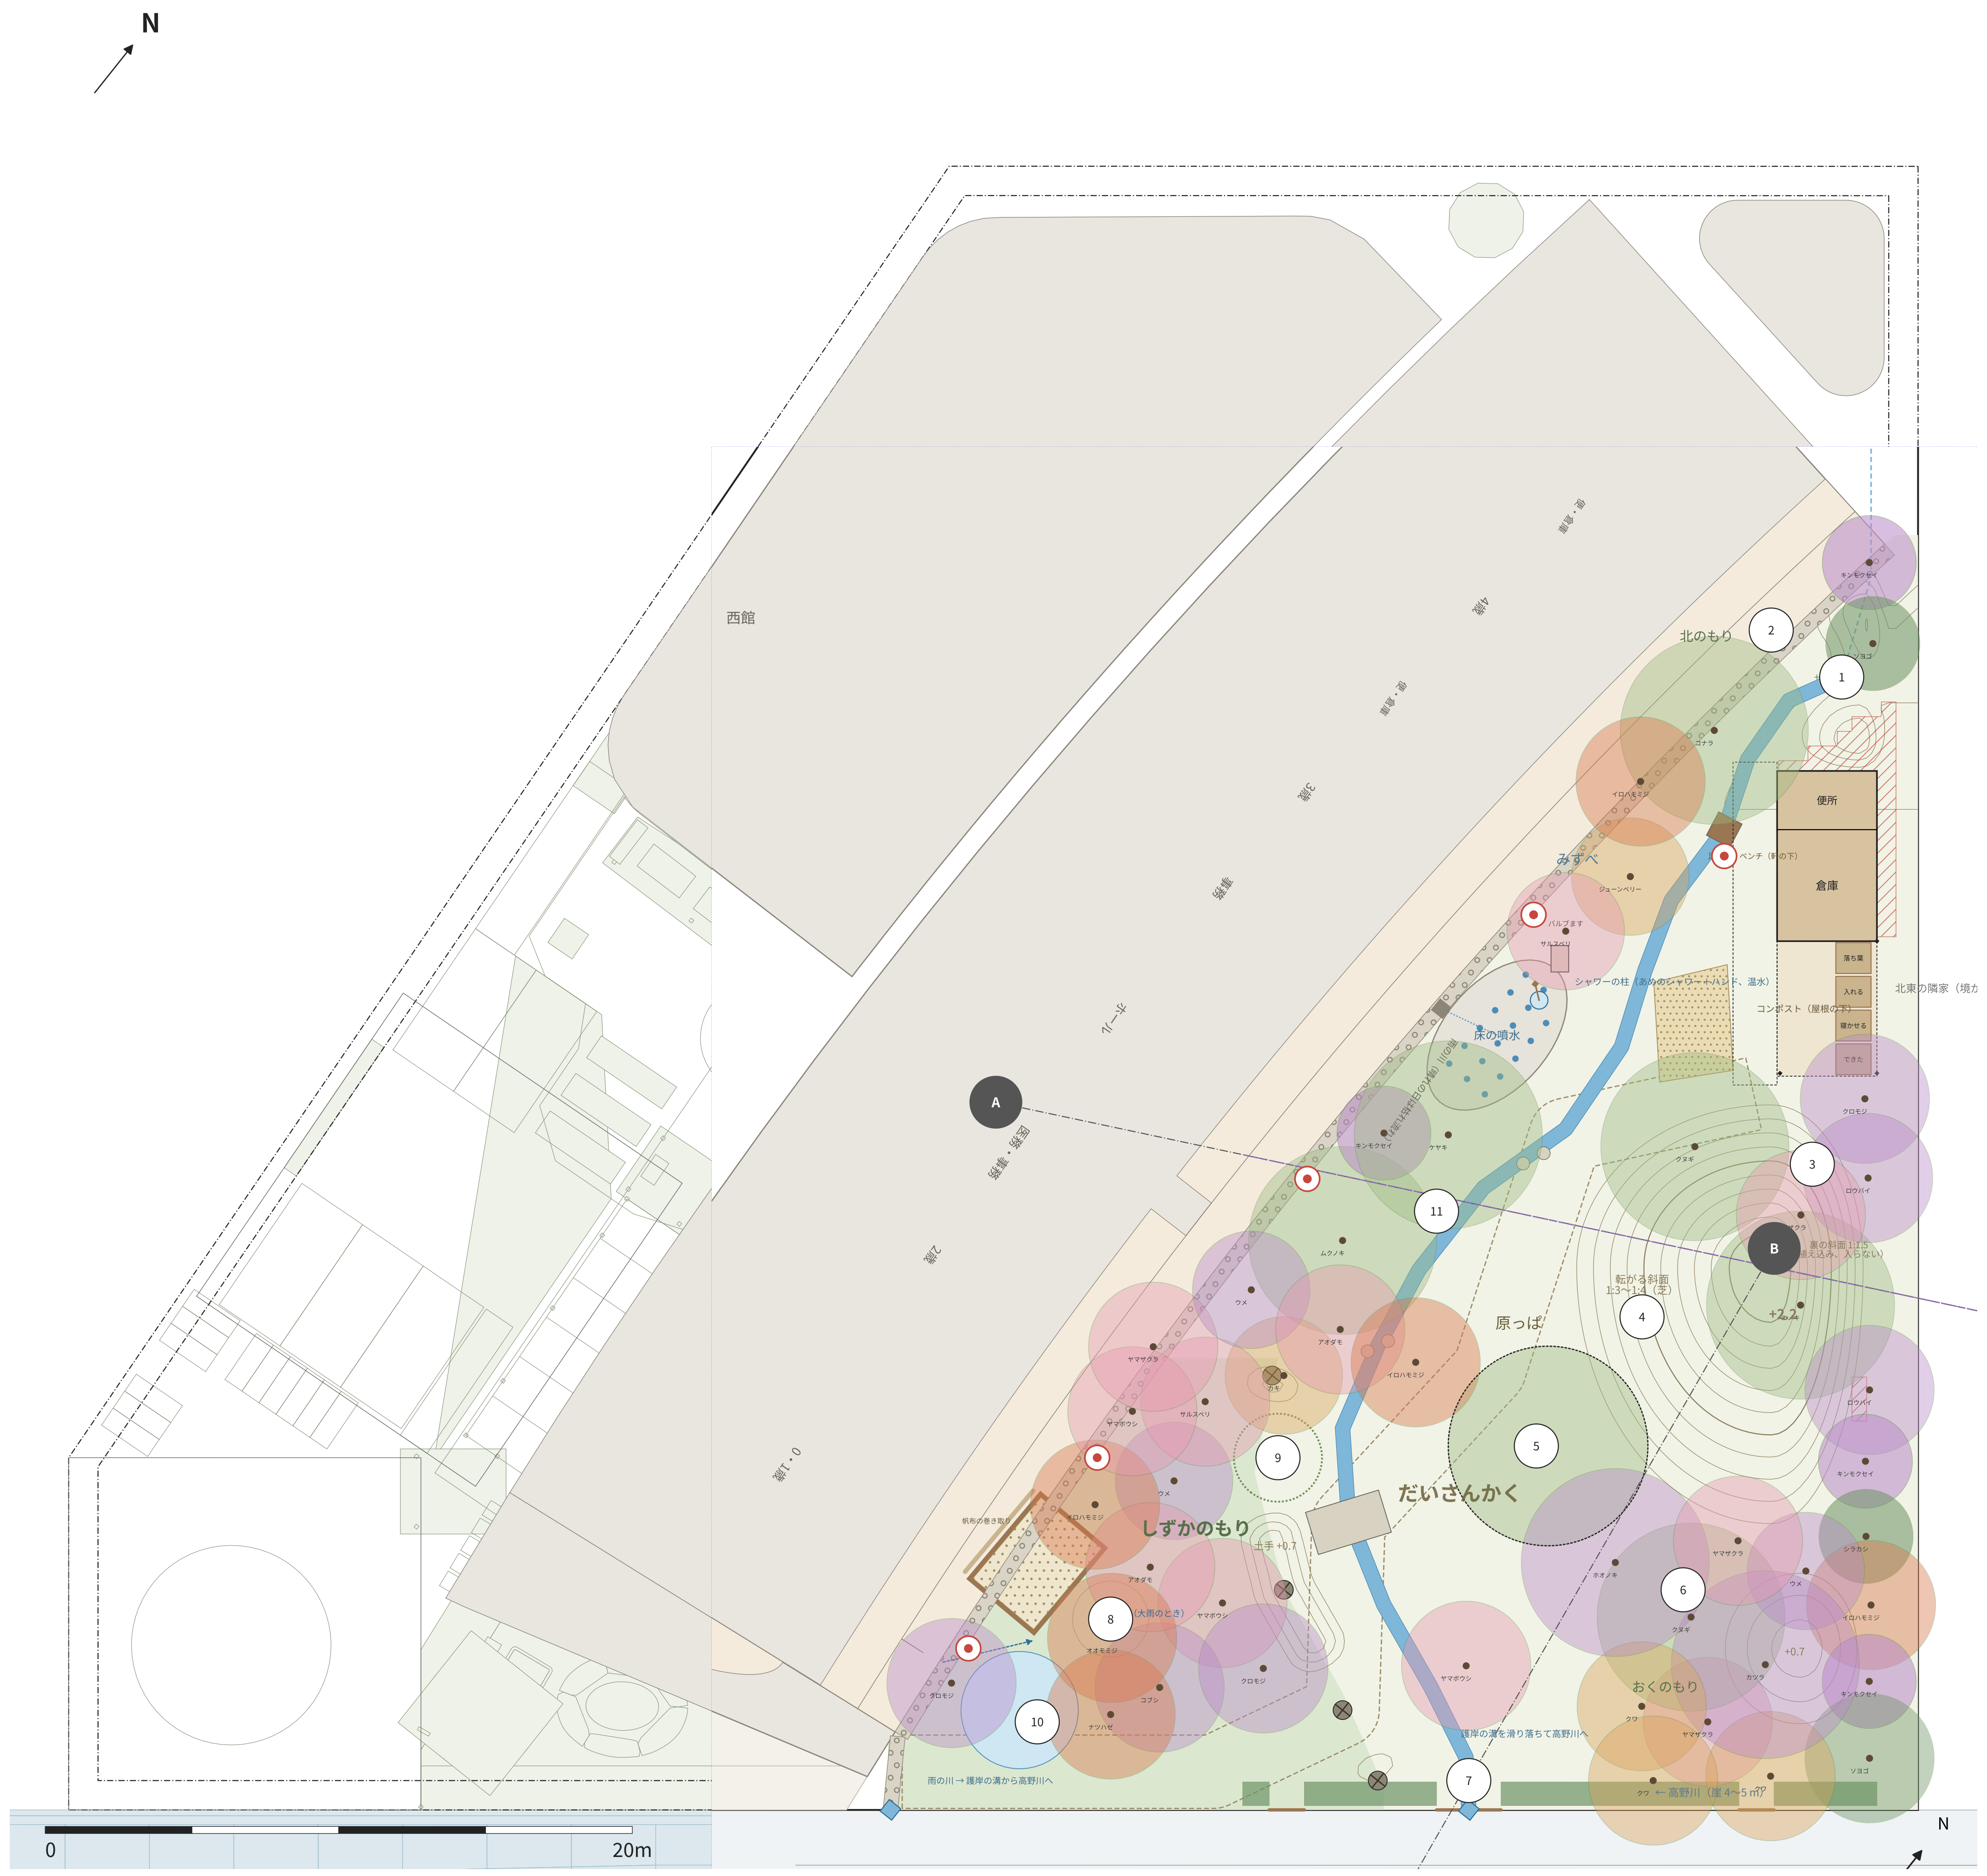

園庭　本物に触れて遊ぶ

見立て　築山＝比叡、小川＝高野川
小さな図＋
ホールから頂の向こうに比叡
足もとを掘った土で盛る
遊具を置かず、地形と木で遊ぶ

水の行方を隠さない
小さな図＋
用水→みなもと→小川→護岸の溝→高野川
雨は樋なしで屋根から落ち、雨の川へ
溢れたらすりばちが雨の池に

土と世代のめぐり
小さな図＋
キッチンの野菜くず→コンポスト（4・5 歳の当番）
→入口前の菜園→給食、余りは農家へ
柳の家は上の子が小さい子のために編む

静かな場所と先生の目
小さな図＋
南のしずかのもり（寝ている 0〜2 歳の前）
ニッチ 11 か所、死角は植え込みだけ
取り除くのは命に関わる危険だけ

模型写真　鳥瞰
敷地と高野川・崖・公園・西の道・園庭
配置図と同じ向き（高野川を手前）にそろえる

［割付の注記］フォーカス：この案が敷地から生まれたこと（比叡・高野川・扇状地・西の細い道）と、主題の舞台としての園庭　／　目に入る順：模型写真（入口の一枚）→ タイトルと趣旨の冒頭 → 配置図と園庭 → 園庭の筋 → 立地と応答

こどもたちの育ち舎　2/5　こどもの一日　1 階平面

建築設計実習 II — I　2026.11.05　木田

1 階平面図　1/100　道路・隣地境界線・家具。北が右、園庭が下（縁側の前の園庭まで）

建物（庇・おむすび・みなみのさんかくまで）75.5×31.8 m → 1/100 で 755×318 mm。窓 799×392 mm に入る。西の道路の幅は 3dm に無いので描き足す

こどもの一日　園庭と部屋を行き来して　食べる・遊ぶ・寝る・当番

一日の帯は 1/700 の小さな配置（建物＋園庭、3dm と garden.json から自動）。北が右・園庭が下

登園 8:00

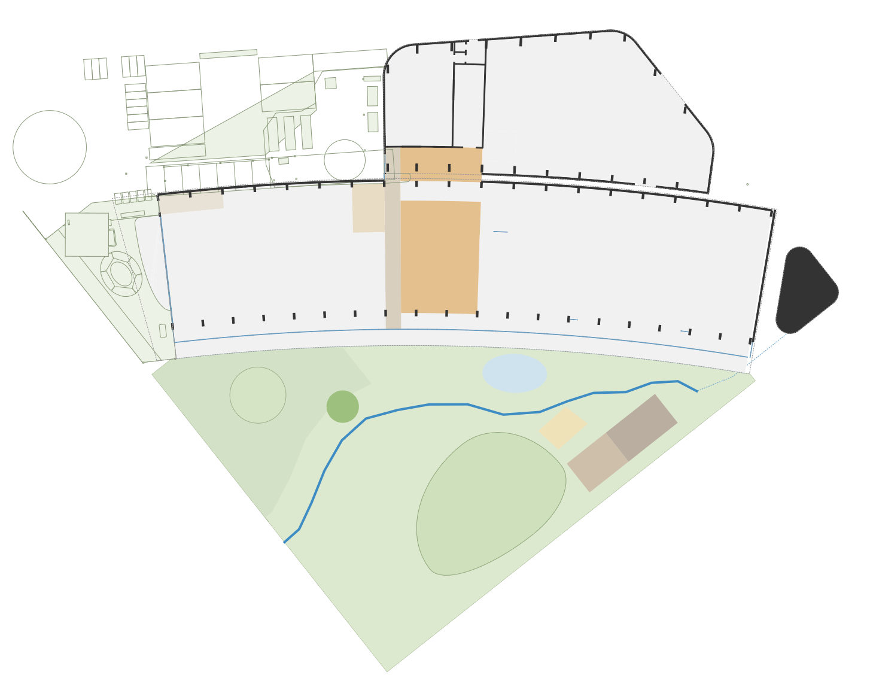

公園→木戸→小径→海峡／0・1 歳は受け取り土間

外で遊ぶ 9:30

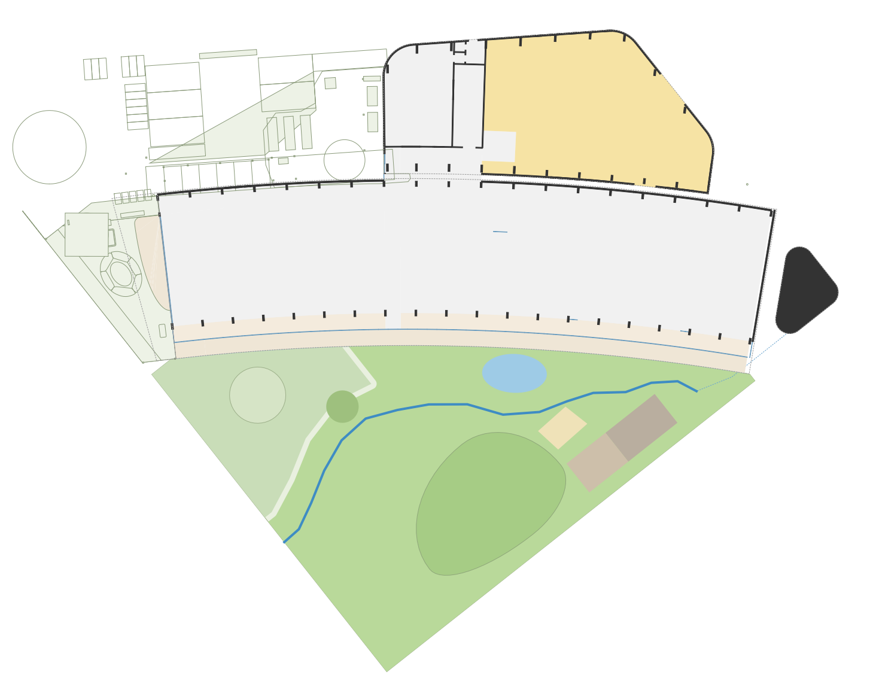

3〜5 歳はだいさんかく（築山・小川・もり、夏は床の噴水）
0〜2 歳はしずかのもり／雨の日は遊戯室

食べる 11:30

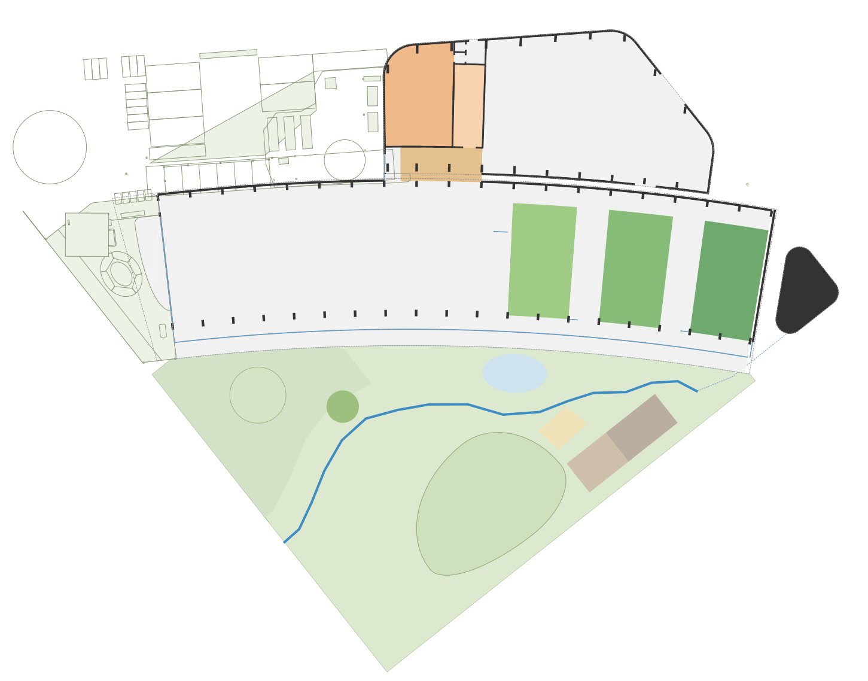

キッチンから海峡を通って配膳
縁側から見える台所

寝る 12:45

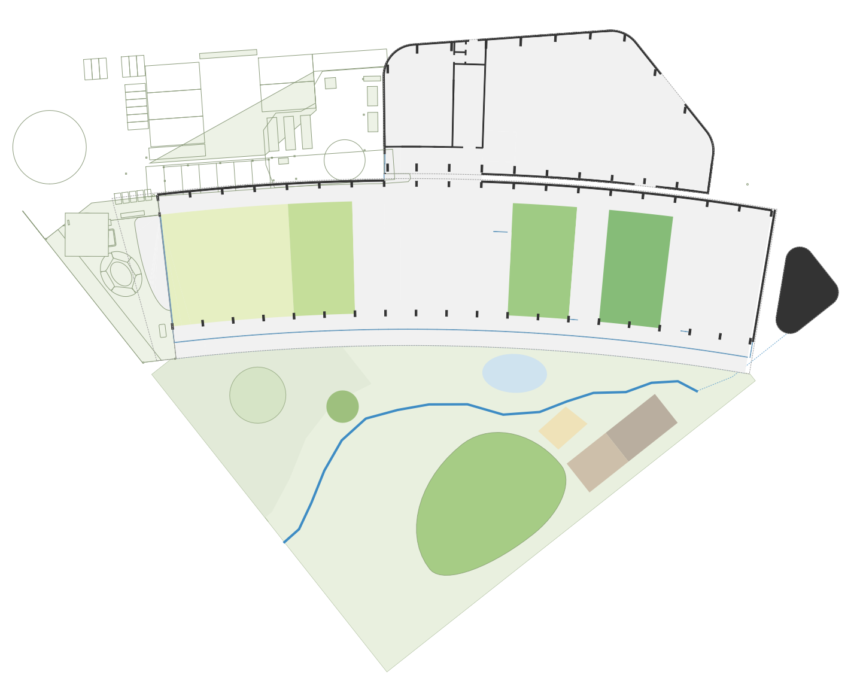

ねどこ・ロフトの下／南のしずかのもりは静かに
起きている 5 歳は北の築山・遊戯室で

当番 15:00

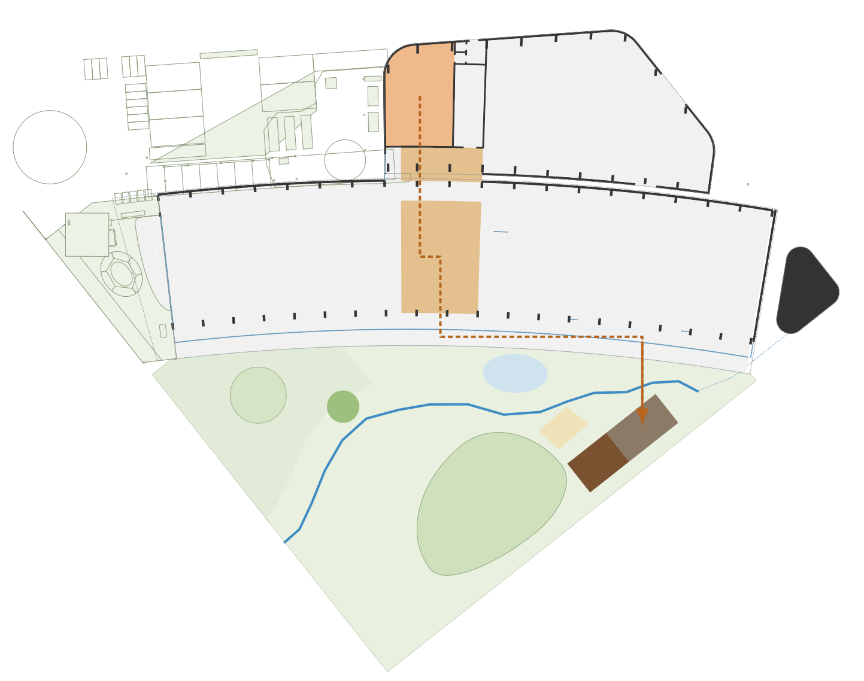

4・5 歳のコンポスト当番：キッチンの野菜くず→小屋
できた土は入口前の菜園へ（余りは農家へ）

降園 16:30

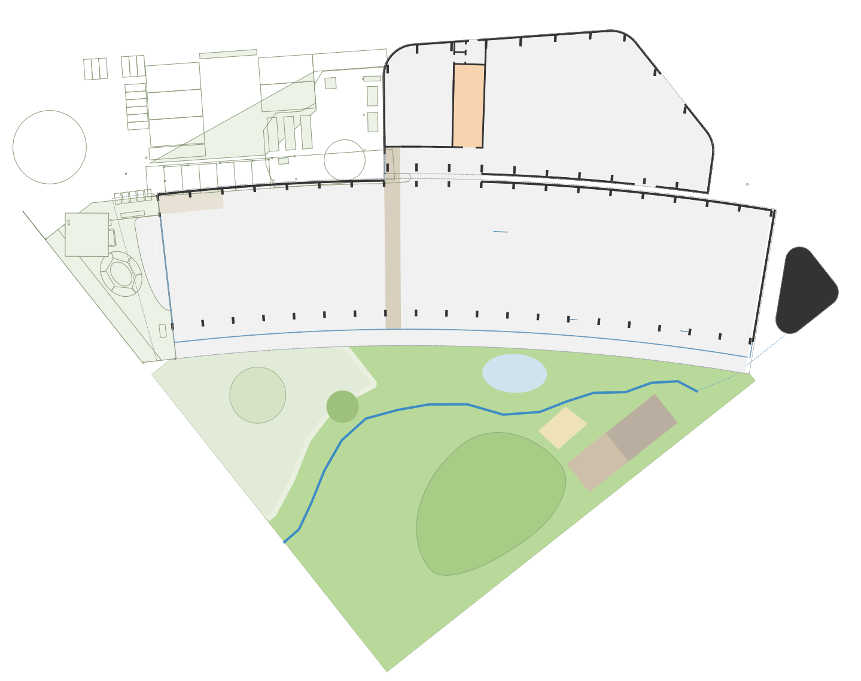

はれのまで延長保育／縁台でお茶
迎えを待つあいだ夕方の園庭

［割付の注記］フォーカス：こどもが一日を過ごす場所としての平面（家具・午睡・靴の線・歳とともに延びる道）　／　目に入る順：部屋の色 → 海峡とホール・キッチン → 縁側 → 家具 → 一日の帯（部屋と園庭）

こどもたちの育ち舎　3/5　どう見えるか　立面と縦断

建築設計実習 II — I　2026.11.05　木田

東立面図（園庭側）　1/100　1 階平面と同じ横位置

2 枚目の真下に貼ると、平面と柱の位置が縦にそろう

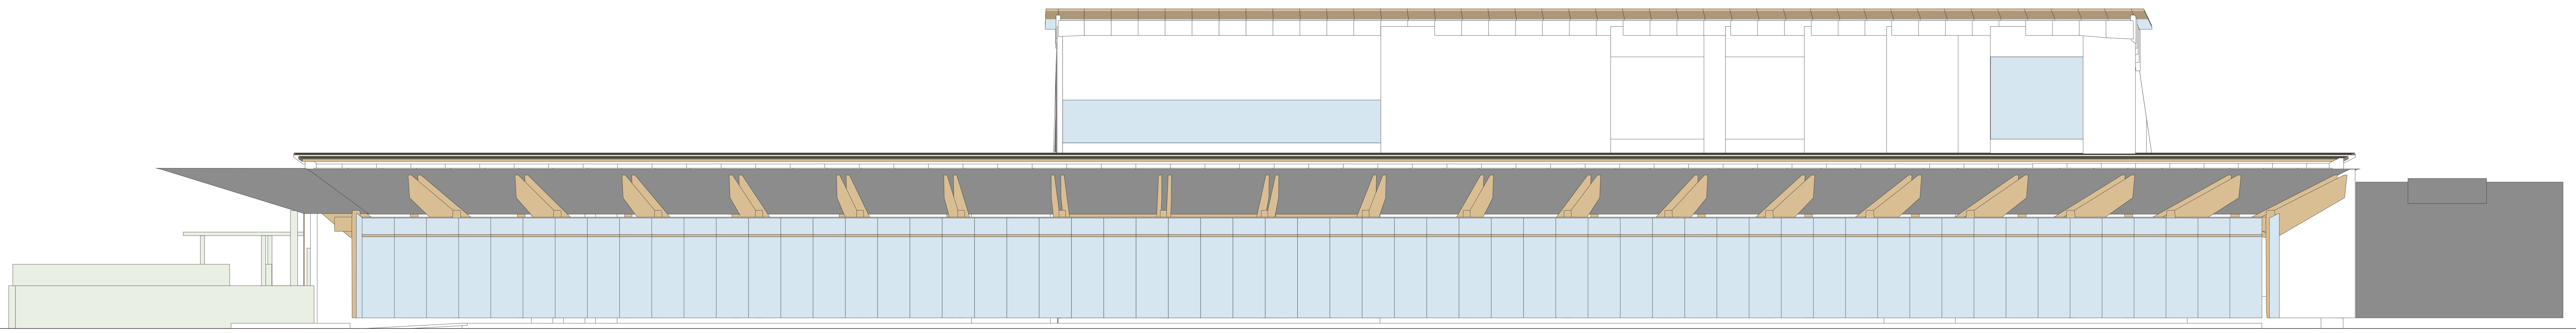

縦断面図 A　1/100　保育室の中ほど r=197 m で切って展開、西を見る

自動の断面 A をそのまま実寸で（model/drawings）

断面 A　縦断（展開）　保育室の中ほど r=197 m の弧で切って平らに伸ばす、西を見る

模型写真　西の道から
人の目の高さ 1.5 m（模型 15 mm）
低い軒と縦格子

模型写真　公園の木戸から
アプローチの入口
見送りの小径の奥にひろば

西立面図（道路側）　1/100　北が左

道の向かいの住宅の高さを点線で描き足す（圧迫感の説明）

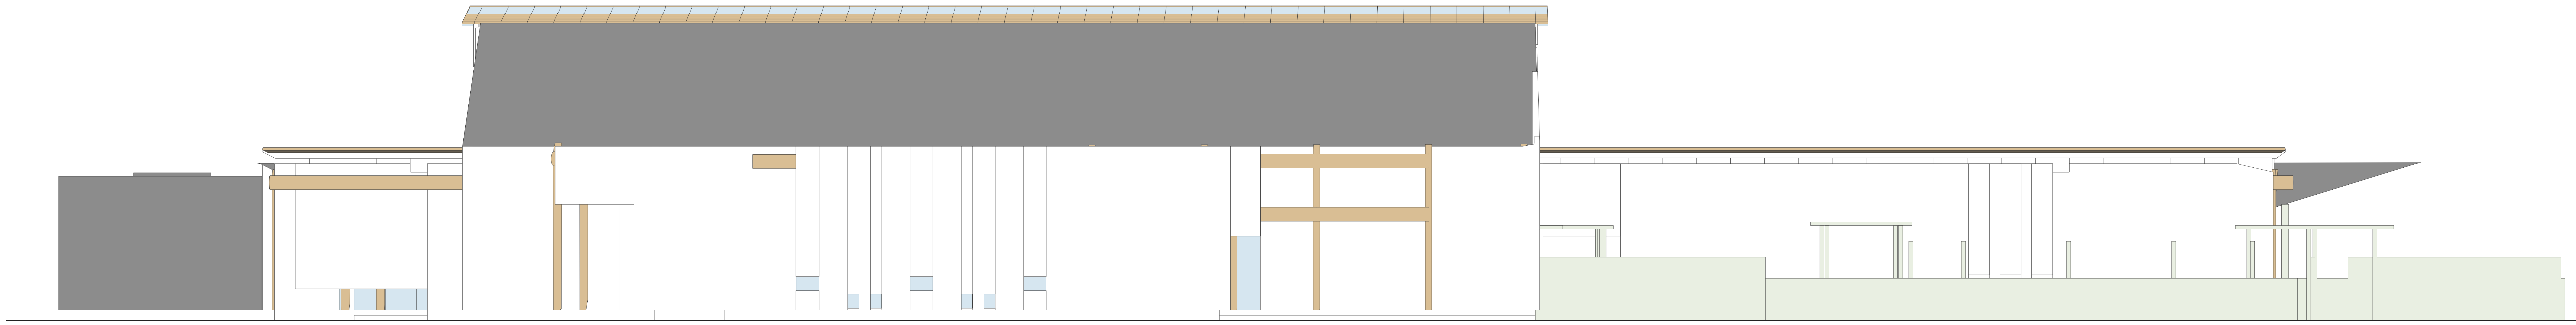

［割付の注記］フォーカス：57 m の縁側と深い庇のリズム（東）、街に対して低い構え（西）　／　目に入る順：東立面（平面の真下、柱がそろう）→ 縦断 → 西立面

こどもたちの育ち舎　4/5　どう息をするか　断面と環境

建築設計実習 II — I　2026.11.05　木田

断面図 C　4 歳・遊戯室　1/50（1/100 の自動の図を 2 倍）　西の道路から園庭へ

左右に 道・向かいの住宅／園庭・築山 を描き足す。空気の矢印と①〜⑨を重ねる。断熱は帯で

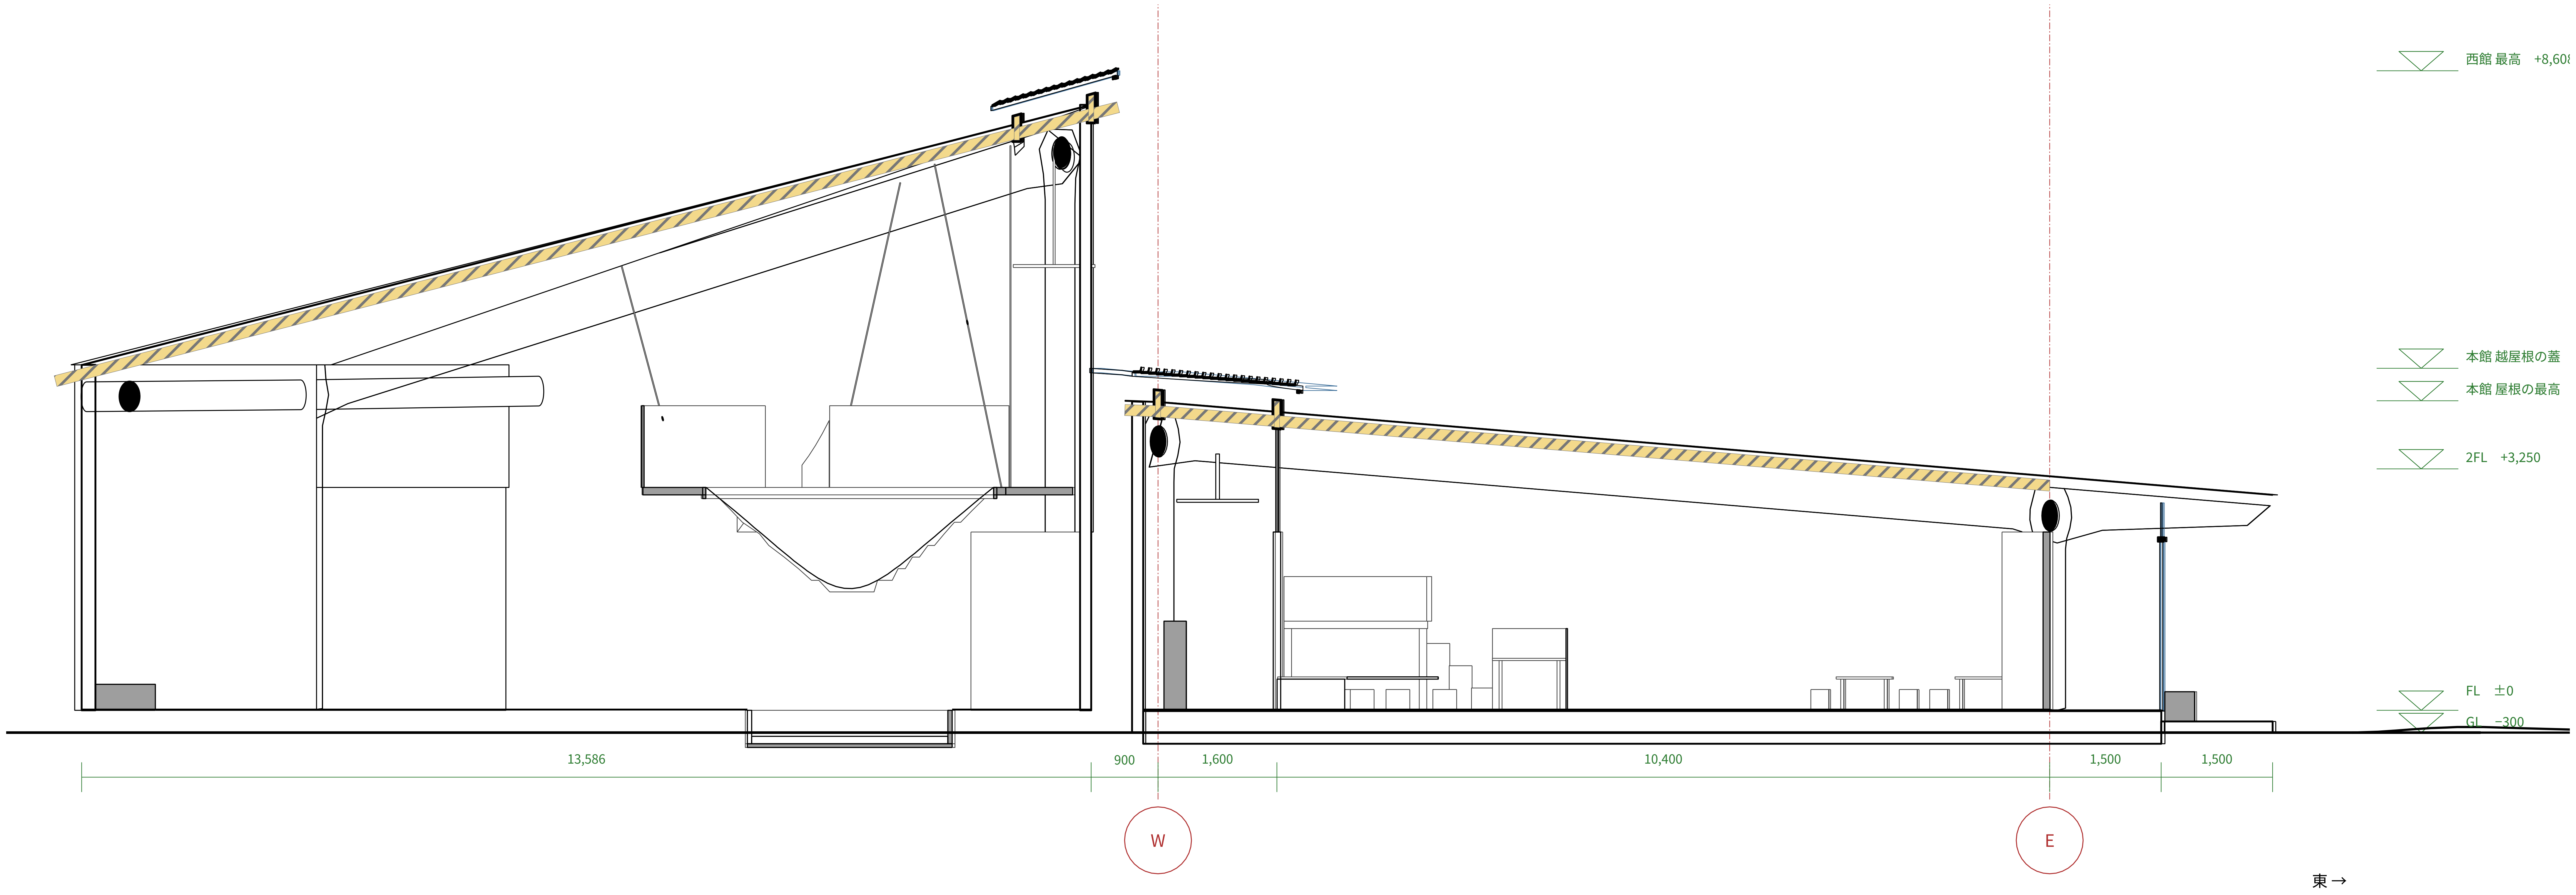

環境の枠
LEED v5
Gold 相当

脱炭素 ①〜⑤
生活の質 ⑥⑦
生態系 ⑧⑨

夏の昼
庇で遮る・越屋根から抜く

夏の夜
比叡の冷気で冷やす（自動の窓）

春・秋
手で開ける（表示灯）

冬
床暖房・熱交換の換気・断熱

断面図 B　海峡　1/100　南の入口・キッチン・2 階・すき間・本館・縁側

断面 B　海峡（スパン 8+0.75）　南の入口・キッチン・2 階・すき間・本館・縁側、北を見る

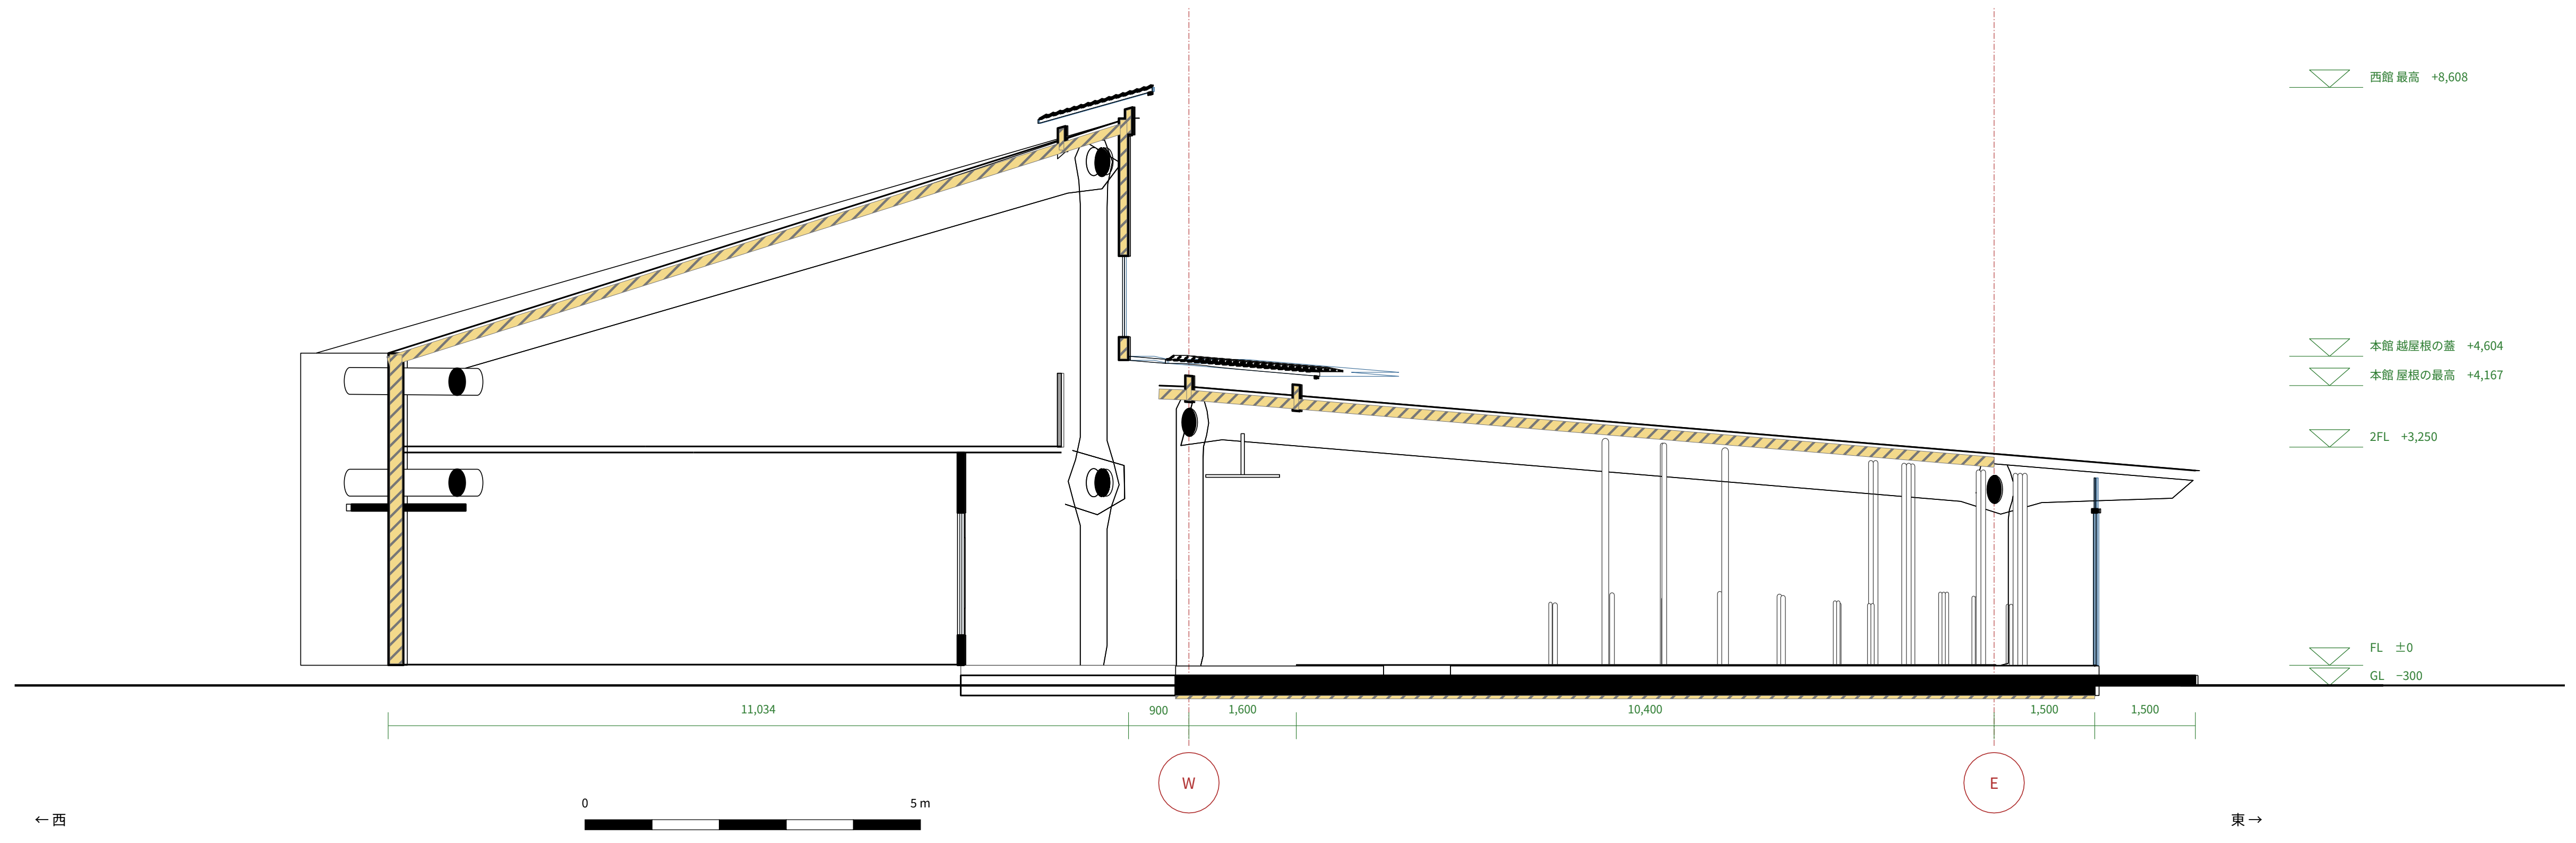

2 階平面図（西館）　1/100

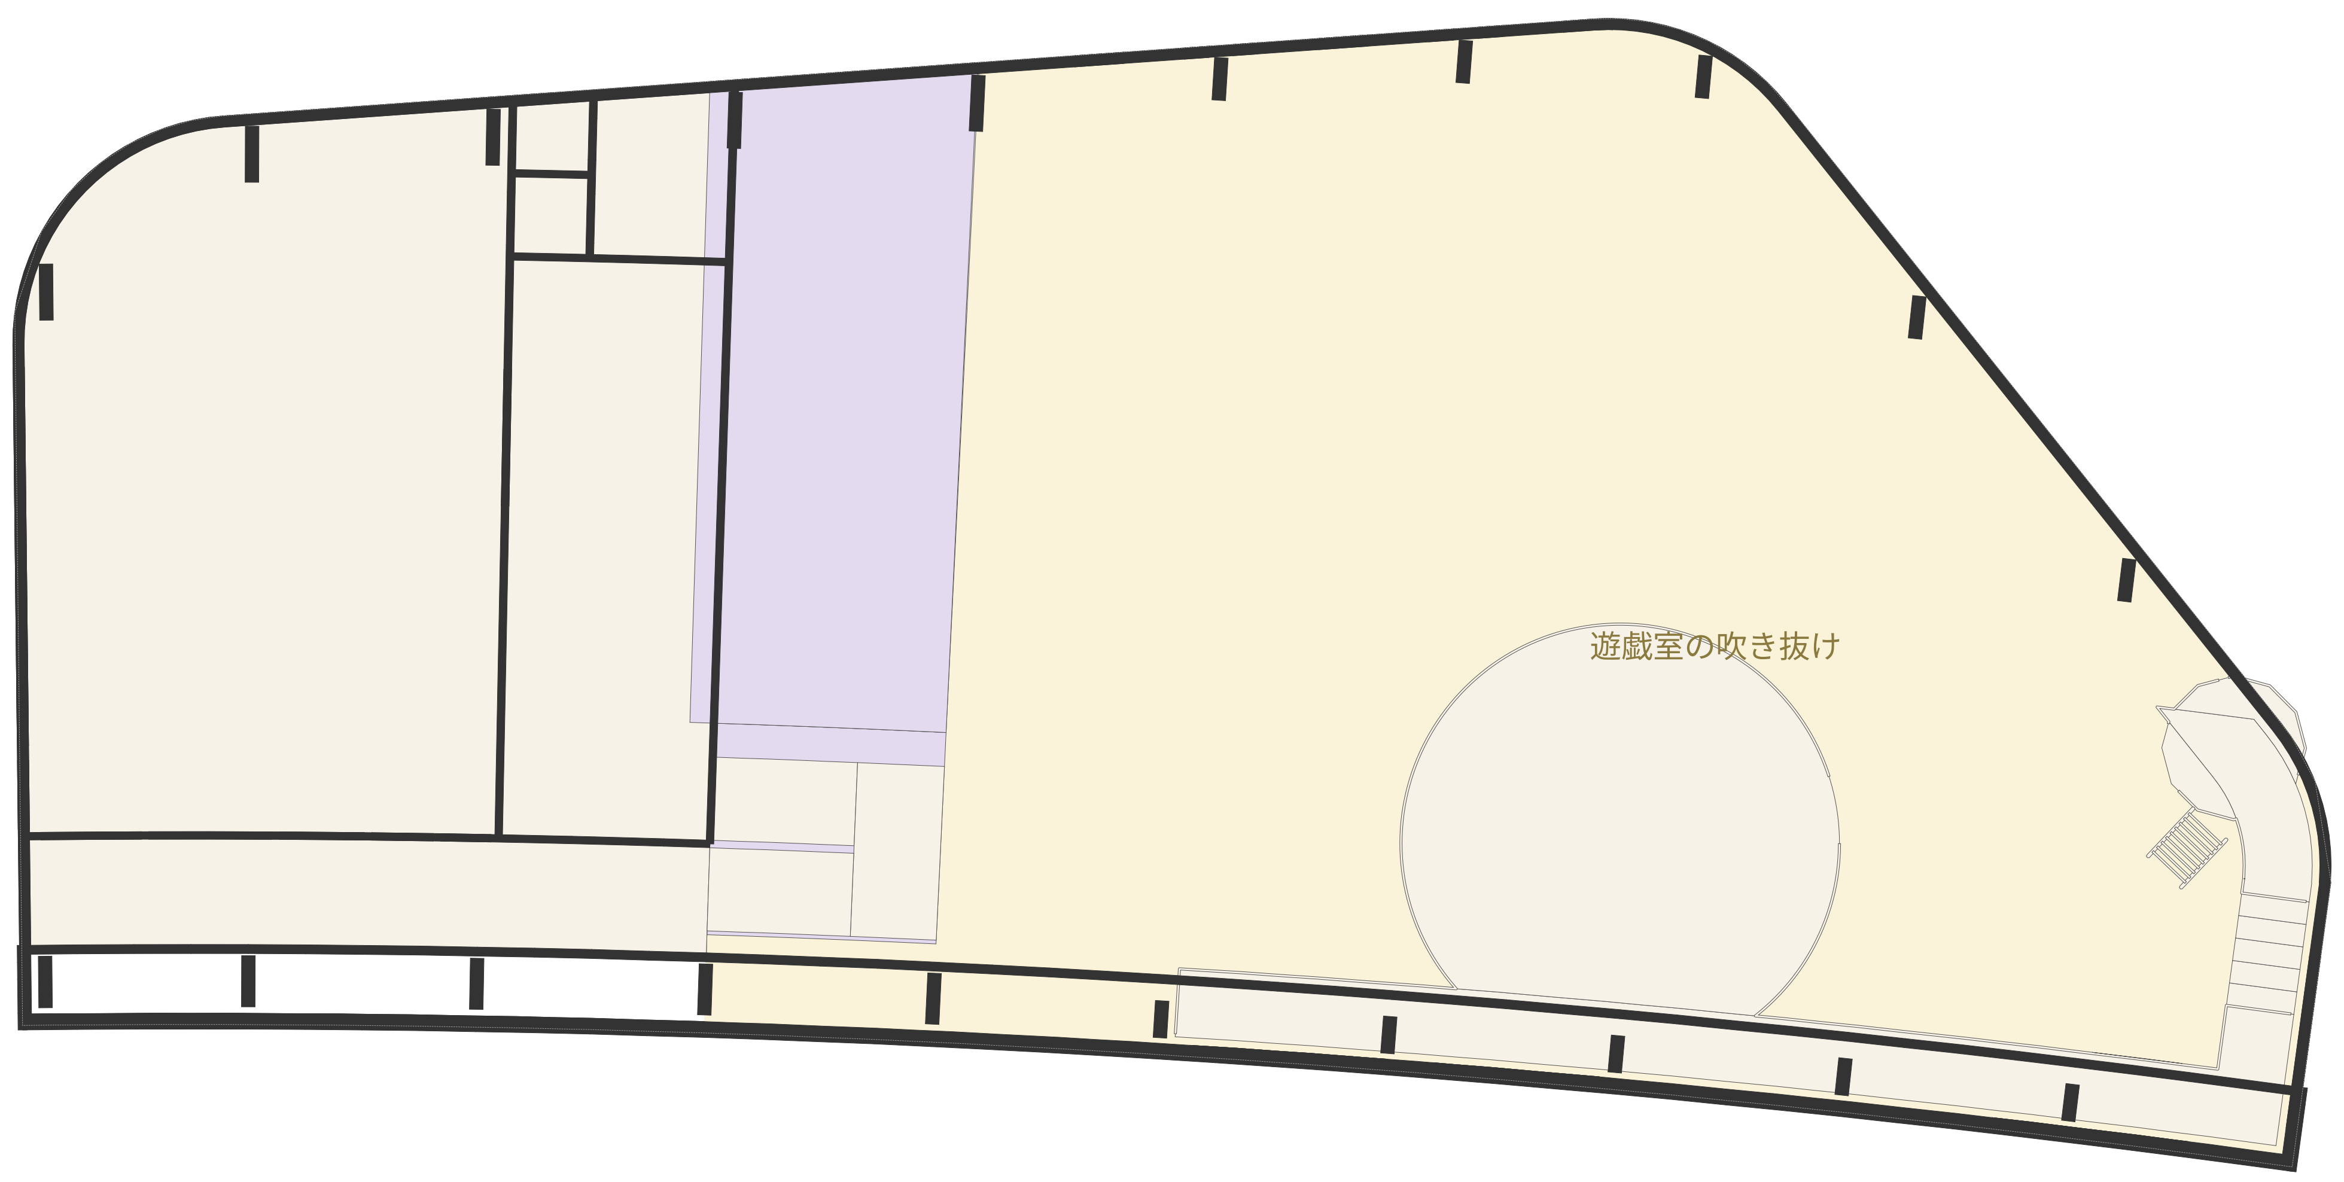

西館 33×17 m → 326×172 mm（1 階平面図と同じ向き）

［割付の注記］フォーカス：空気・光・熱の流れが形の理由になっていること（断面 C を主役に）　／　目に入る順：断面 C 1/50 → ①〜⑨ と環境の枠 → 運転表 → 断面 B → 2 階

こどもたちの育ち舎　5/5　暮らしと構造

建築設計実習 II — I　2026.11.05　木田

内観　ホール（A4）
海峡と飛び石・オープンキッチン
梁の見える天井・越屋根の光の線
（レンダリングか模型写真）

同じ部屋の一日　3〜5 歳の保育室　断面 1/100

10:00
遊ぶ

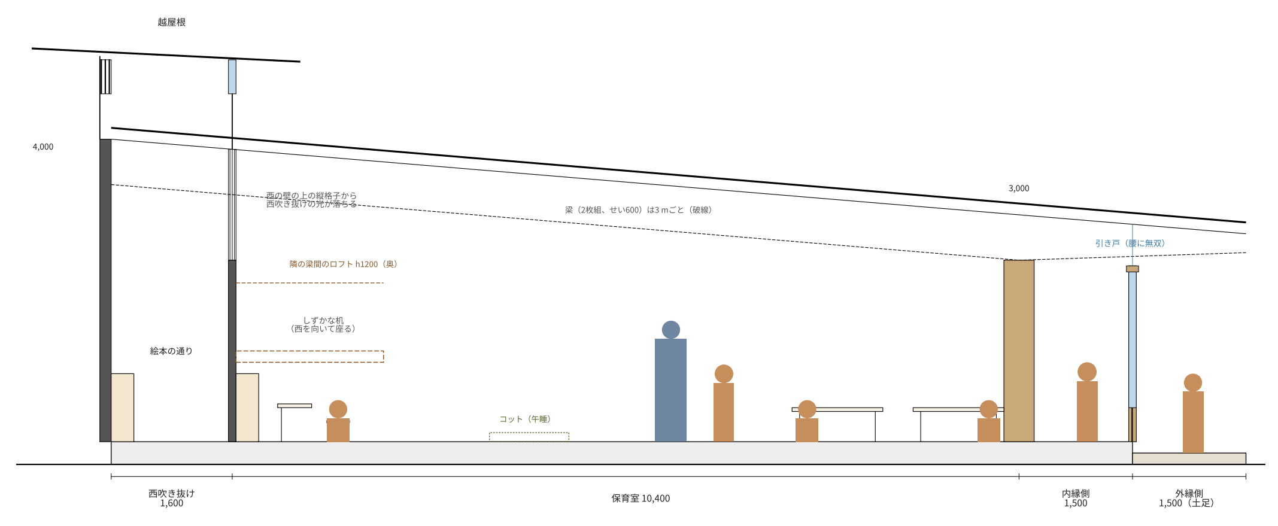

11:30
食べる

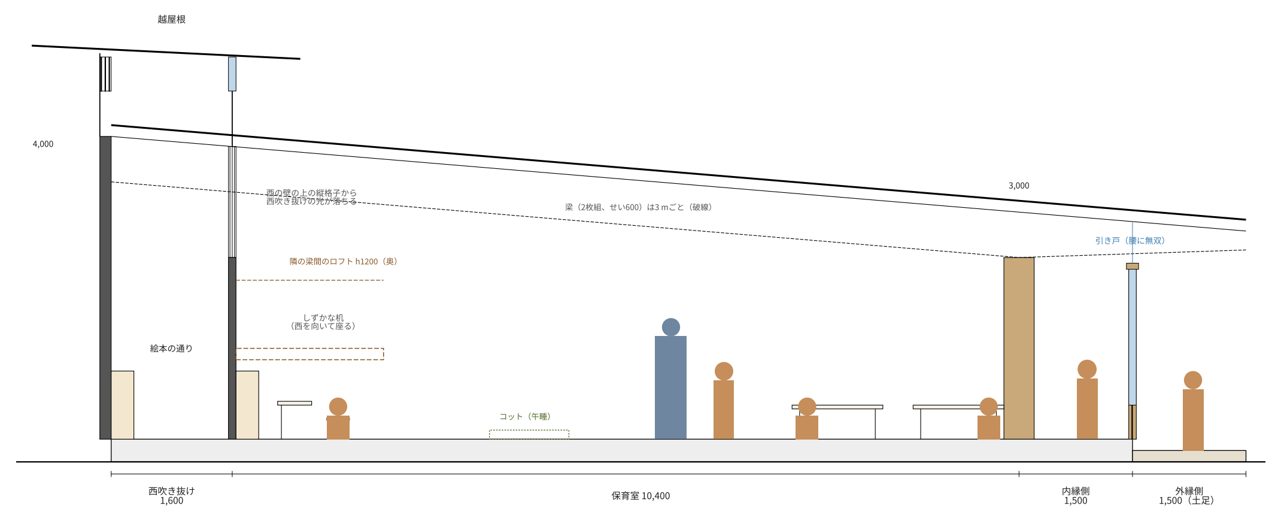

13:30
寝る

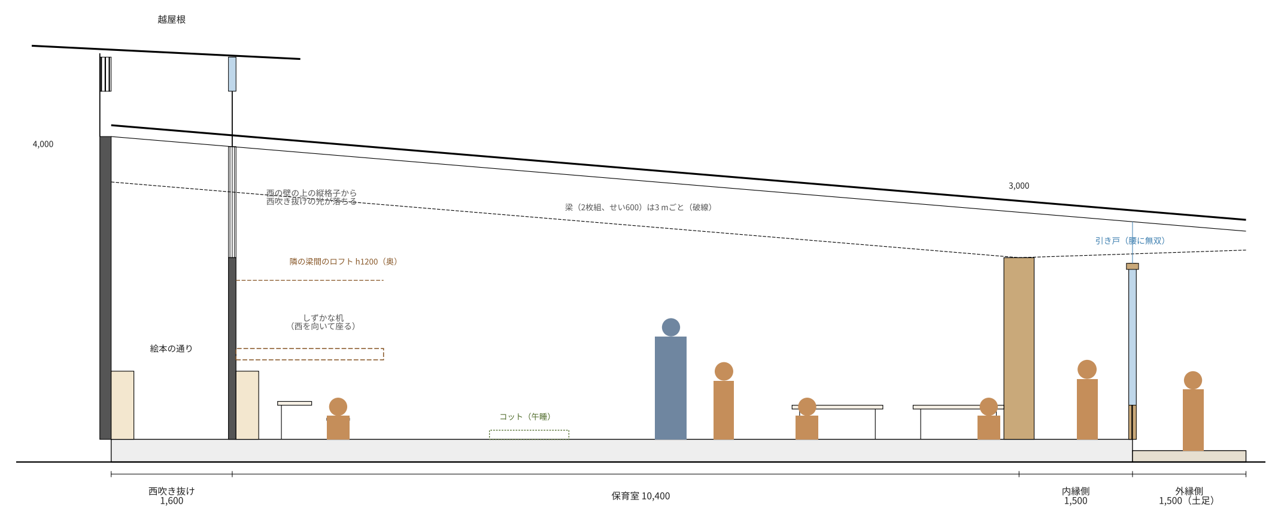

今は同じ図（既存の 1/50 を縮小）。時刻ごとに家具・人・光を描き分ける

遊戯室　平面・断面（縮小、遊戯室のチャット）

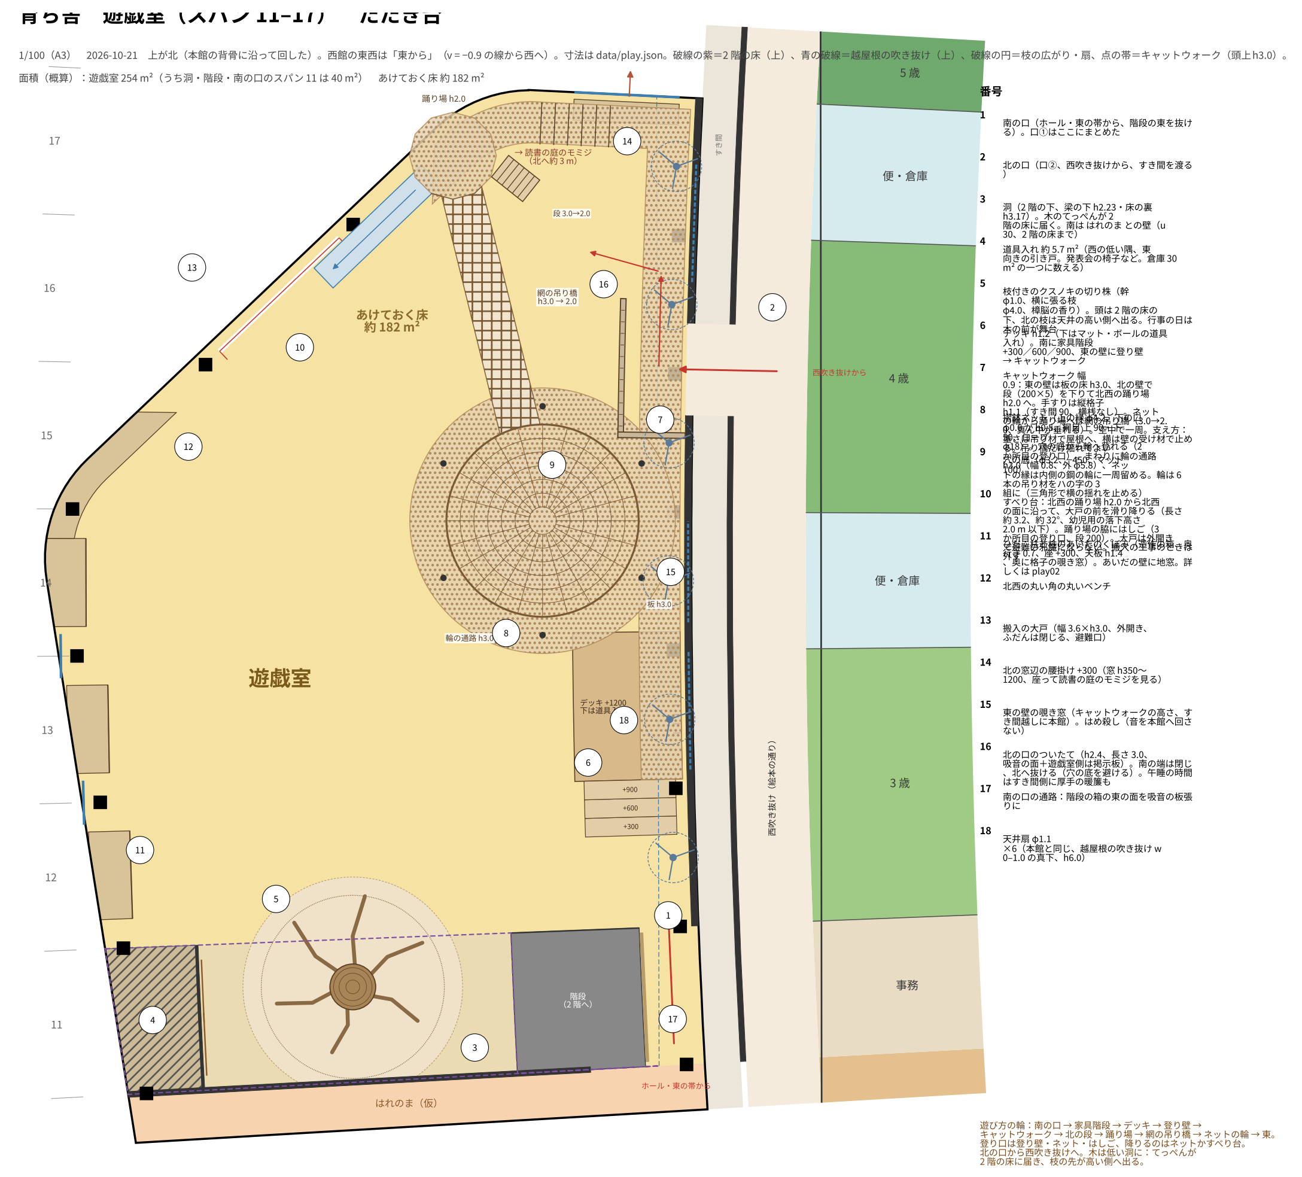

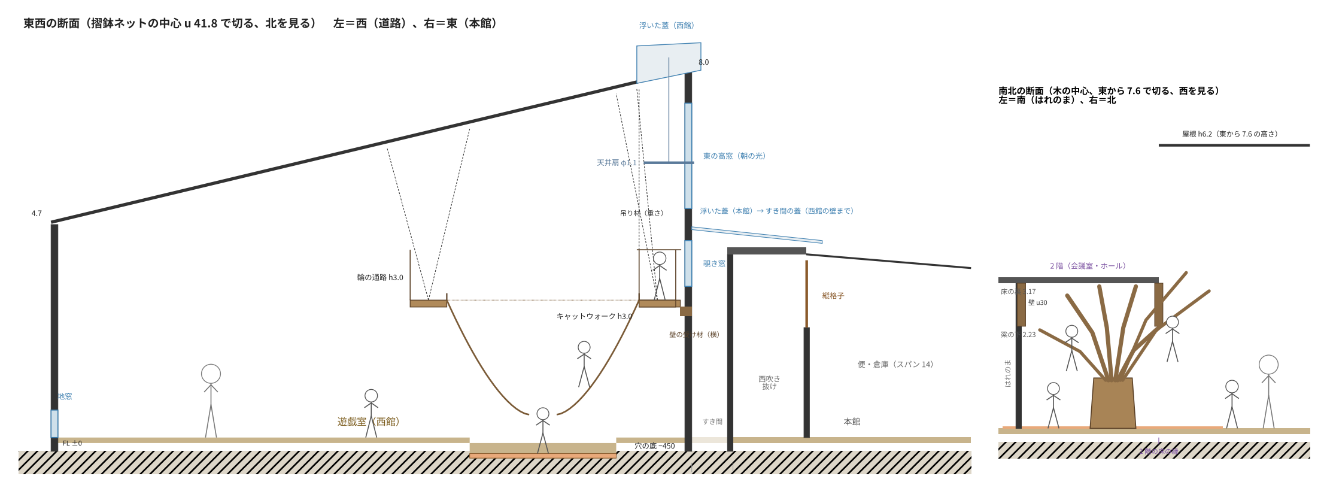

接合部　タメディア型　2 枚の梁で柱を挟む（縮小）

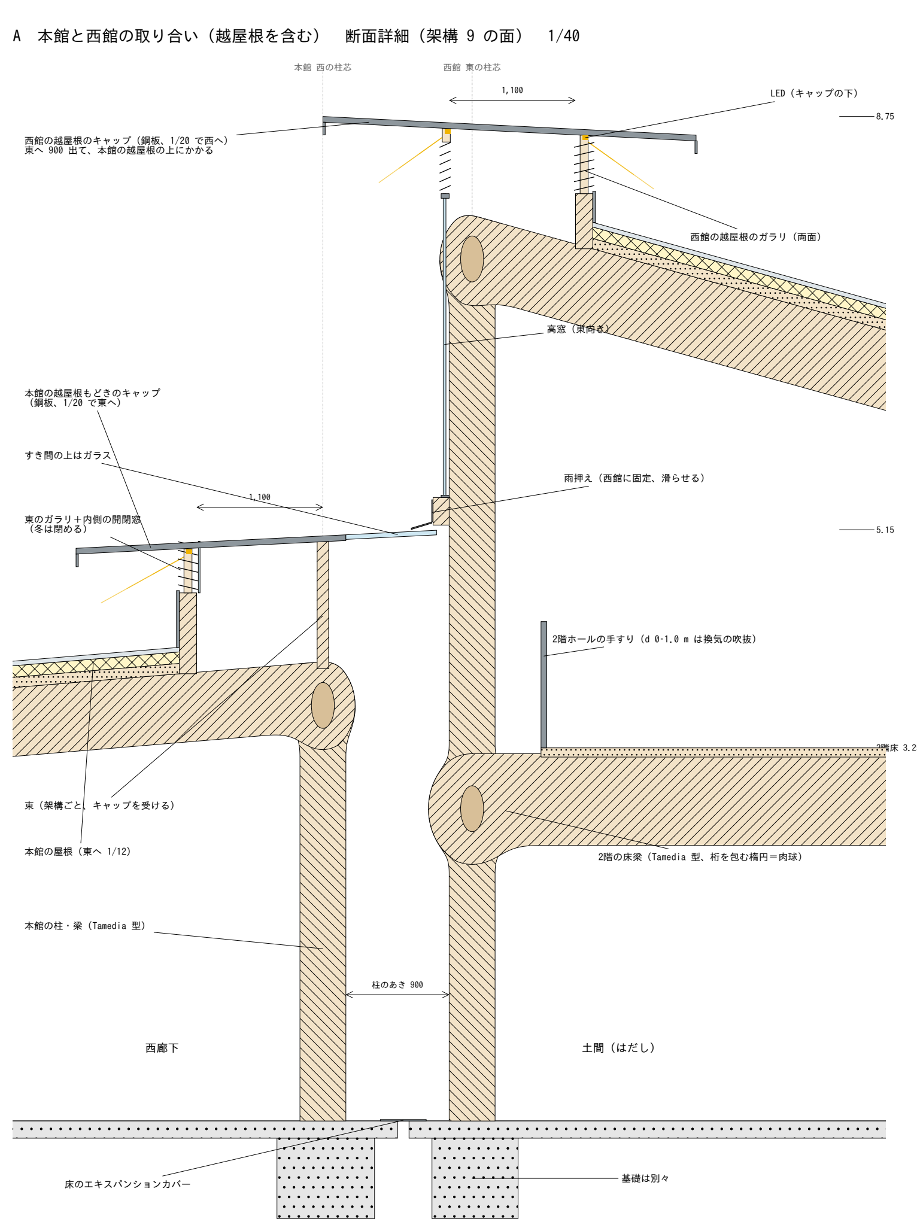

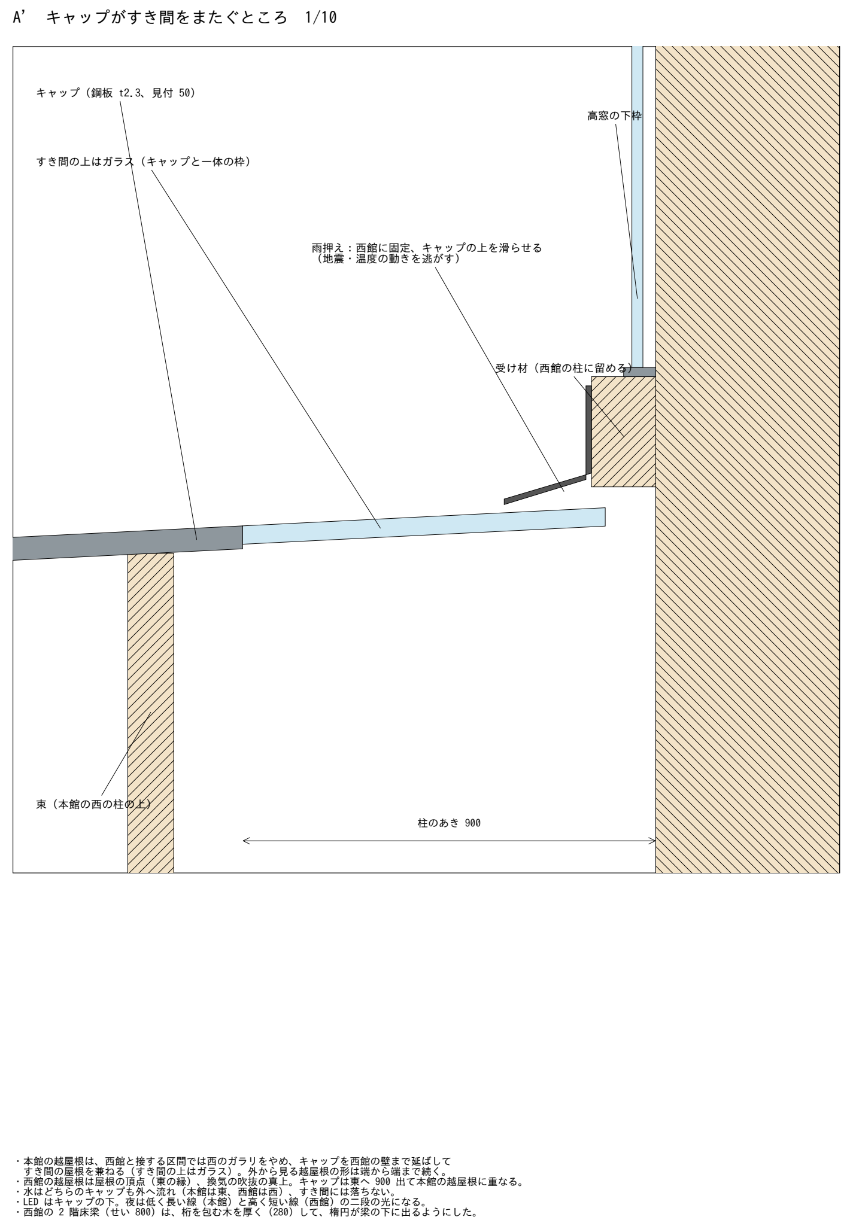

京都の間伐材・金物を減らした接合

スケルトン＆インフィル
3 m スパンの骨格（固定）と
間仕切り・家具（可変）を色分け

今／定員が変わる／
学童・地域の場 の 3 コマ

園庭の断面　縮小（園庭のチャット）

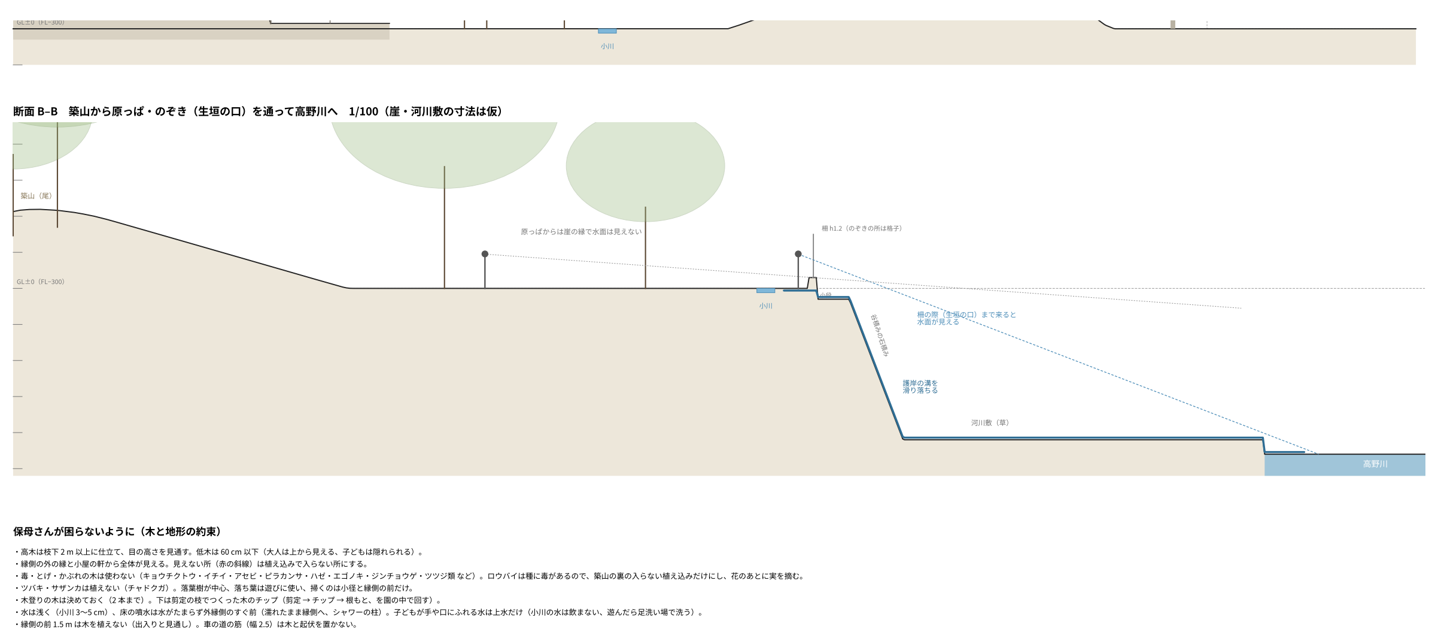

築山・小川・水遊び場は遊ぶの答え

面積表　m²（仮）

室	要求	計画
乳児室（0・1 歳）	約 60×2	120.7
保育室（2 歳）	約 60	60.3
保育室（3 歳）	約 60	60.3
保育室（4 歳）	約 60	60.3
保育室（5 歳）	約 60	60.3
遊戯室	240 以上	237.9
調理室	約 60	60.5
医務室	約 30	21.6
事務室	約 60	23.0
休憩・会議（2 階）	60＋30	94.1
はれのま	（追加）	21.9

3dm の床から自動で測った仮の値。
医務・事務の不足を確かめる。
園庭 350・駐車 5・延床 2,000・
倉庫 30・機械室 30 を本番で足す

inspired by

Asilo Nido Iride　Mario Cucinella Architects・Guastalla・2015
→ 梁の列が並ぶ長細い本館と、外に付く付属の建物

Tamedia　坂茂・Zürich・2013
→ 梁の端の楕円の頭と、それを貫く楕円の桁

レイモンド斑鳩こども園　キノアーキテクツ・斑鳩・2026
→ 室内に木を立てる（ホールの北山杉）

KAIT 工房　石上純也・厚木・2008
→ 柱の配列：見る向きで景色が変わる並び

認定こども園らみどり　はりゅうウッドスタジオ・須賀川・2026
→ 内と外の二重の縁側、遊具を置かない地形の園庭

仙田満の園舎　環境デザイン研究所
→ 擂鉢のネット、キャットウォーク、ニッチ

Waldorf School of the Peninsula　California
→ 遊戯室の切り株

［割付の注記］フォーカス：近づいて読む人のための細部：寝る・遊ぶ・組み方・変わり方　／　目に入る順：内観 → 同じ部屋の一日 → 遊戯室 → 接合部 → S&I → 面積表 → inspired by