
壁に貼ったとき　左：1〜3を縦につなぐ（高さ約1.8 m）　右：4・5を縦につなぐ

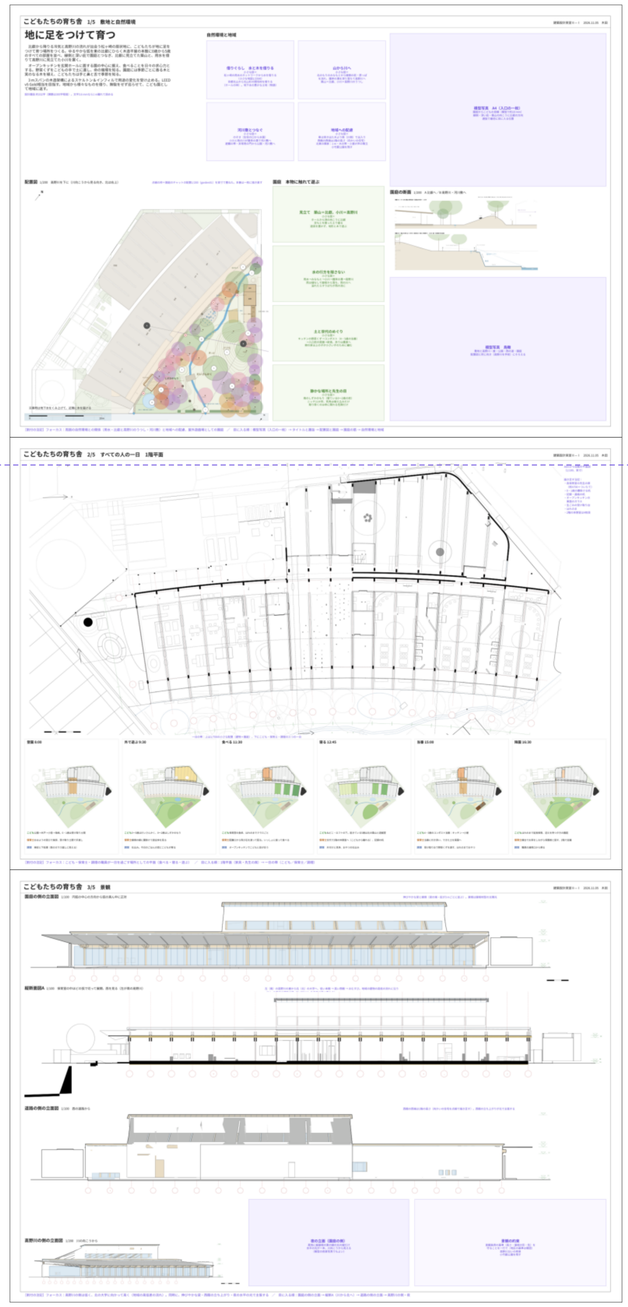

目の高さ1.5 m

課題の言葉の順：1 敷地と自然環境 → 2 すべての人の一日 → 3 景観。

右の列：4 環境 → 5 こどもたちへの環境。

目の高さに来るのは1階平面（最も細かい図）と断面C。

2〜4枚目の平面・立面・断面は3dmから自動の図を実寸で貼る。

製図台に置くなら2+2+1（1・2／3・4／5）に切り分ける。

床

地に足をつけて育つ

　比叡から降りる冷気と高野川の流れが出会う松ヶ崎の扇状地に、こどもたちが地に足をつけて育つ場所をつくる。ゆるやかな弧を東の比叡にひらく木造平屋の本館に0歳から5歳のすべての部屋を並べ、縁側と深い庇で園庭とつなぎ、比叡に見立てた築山と、用水を借りて高野川に見立てた小川を置く。

　オープンキッチンを玄関ホールに面する園の中心に据え、食べることを日々の求心力とする。野菜くずをこどもの手で土に還し、命の循環を知る。園庭には季節ごとに香る木と実のなる木を植え、こどもたちは手と鼻と舌で季節を知る。

　3 mスパンの木造架構によるスケルトン＆インフィルで用途の変化を受け止める。LEED v5 Gold相当を目指す。地域から様々なものを借り、無駄をせず巡らせて、こども園として地域に返す。

設計趣旨 約332字（課題は300字程度）。文字3.6 mmなら1 m離れて読める

自然環境と地域

借りぐらし　水と木を借りる
小さな図＋
松ヶ崎の用水のネットワークから水を借りる
（小さな地図1/2500）
京都北山から北山杉の間伐材を借りる
（ホールの林）。地下水の豊かな土地（物語）

山から川へ
小さな図＋
北のもりのみなもとから縁側の前・原っぱ
を流れ、護岸の溝を滑り落ちて高野川へ
築山＝比叡、小川＝高野川のうつし

河川敷とつなぐ
小さな図＋
のぞき（生垣の口から水面）
小川と雨の川が護岸の溝で河川敷へ
避難の帯・非常用の門から公園・河川敷へ

地域への配慮
小さな図＋
車は突き出た木より南（川側）で出入り
西館の西端は1階の高さ（向かいの住宅）
北東の隣家：1 m・木の帯・小屋が声の衝立
小竹藪公園を残す

模型写真　A4（入口の一枚）
園庭からこどもの目線（模型で約10 mm）
縁側・深い庇・築山の向こうに比叡の方向
選抜で最初に目に入る位置

配置図 1/200　高野川を下に（川向こうから見る向き、北は右上）

点線の枠＝園庭のチャットの配置1/200（garden01）を実寸で重ねた。本番は一枚に描き直す



園庭　本物に触れて遊ぶ


見立て　築山＝比叡、小川＝高野川
小さな図＋
ホールから頂の向こうに比叡
足もとを掘った土で盛る
遊具を置かず、地形と木で遊ぶ

水の行方を隠さない
小さな図＋
用水→みなもと→小川→護岸の溝→高野川
雨は樋なしで屋根から落ち、雨の川へ
溢れたらすりばちが雨の池に

土と世代のめぐり
小さな図＋
キッチンの野菜くず→コンポスト（4・5歳の当番）
→入口前の菜園→給食、余りは農家へ
柳の家は上の子が小さい子のために編む

静かな場所と先生の目
小さな図＋
南のしずかのもり（寝ている0〜2歳の前）
ニッチ11か所、死角は植え込みだけ
取り除くのは命に関わる危険だけ

園庭の断面 1/200　A 比叡へ／B 高野川・河川敷へ

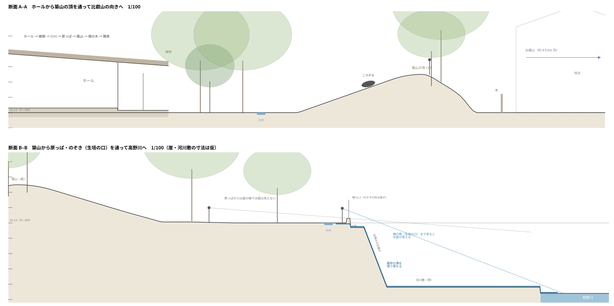

模型写真　鳥瞰
敷地と高野川・崖・公園・西の道・園庭
配置図と同じ向き（高野川を手前）にそろえる

［割付の注記］フォーカス：周囲の自然環境との関係（用水・比叡と高野川のうつし・河川敷）と地域への配慮、屋外遊戯場としての園庭　／　目に入る順：模型写真（入口の一枚）→ タイトルと趣旨 → 配置図と園庭 → 園庭の筋 → 自然環境と地域

こどもたちの育ち舎　2/5　すべての人の一日　1階平面

建築設計実習Ⅱ－Ⅰ　2026.11.05　木田

1 階平面図　FL+1200 で切断　1/100　（右が北の端、下が園庭）




3dmから自動の平面図（1/100、実寸）

描き足す注記：
- 各保育室の先生の席（机h700＋ついたて）
- 0・1歳の腰掛ける机
- 記録・連絡の机
- オープンキッチンの東面のガラス
- 生ごみの受け取り台
- はれのま
- 2階の休憩室は4枚目

一日の帯：上は1/700の小さな配置（建物＋園庭）、下にこども・保育士・調理の三つの一日

登園 8:00

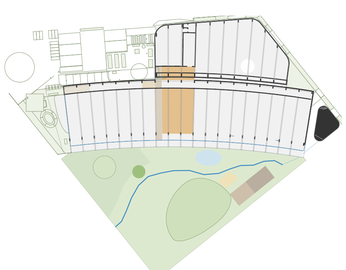


こども公園→木戸→小径→海峡。0・1歳は受け取り土間

保育士おはようの窓口で挨拶、受け取り土間で手渡し

調理　検収と下処理（南のガラス越しに見える）

外で遊ぶ 9:30

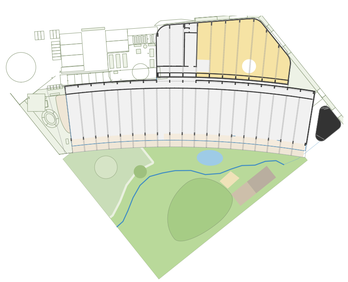


こども3〜5歳はだいさんかく、0〜2歳はしずかのもり

保育士縁側の縁に腰掛けて庭全体を見る

調理　仕込み。今日のごはんの窓にこどもが寄る

食べる 11:30

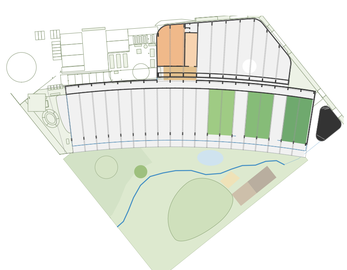


こども保育室の食卓、はれのまでクラスごと

保育士配膳口から飛び石を渡って配る。いっしょに座って食べる

調理　オープンキッチンでこどもと目が合う

寝る 12:45

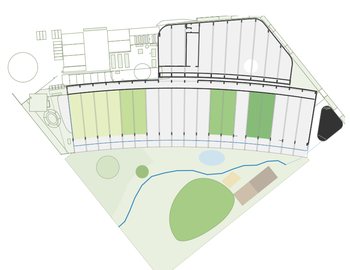


こどもねどこ・ロフトの下。起きている5歳は北の築山と遊戯室

保育士交代で2階の休憩室へ（こどもから離れる）、記録の机

調理　片付けと洗浄、おやつの仕込み

当番 15:00

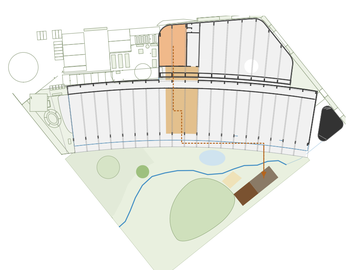


こども4・5歳のコンポスト当番：キッチン→小屋

保育士当番に付き添い、できた土を菜園へ

調理　受け取り台で野菜くずを渡す、はれのまでおやつ

降園 16:30

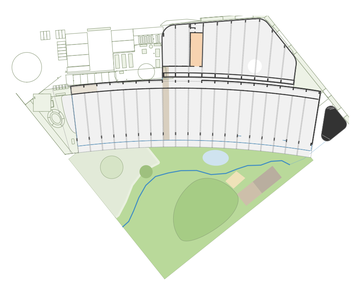

こどもはれのまで延長保育、迎えを待つ夕方の園庭

保育士縁台でお茶をしながら保護者と話す、2階で会議


調理　職員の通用口から帰る

［割付の注記］フォーカス：こども・保育士・調理の職員が一日を過ごす場所としての平面（食べる・寝る・遊ぶ）　／　目に入る順：1階平面（家具・先生の席）→一日の帯（こども／保育士／調理）

こどもたちの育ち舎　3/5　景観


園庭の側の立面図　1/100　円弧の中心の方向から弧の真ん中に正対

伸びやかな梁と縁側（梁の端・庇が3ｍごとに並ぶ）。屋根は屋根材型の太陽光

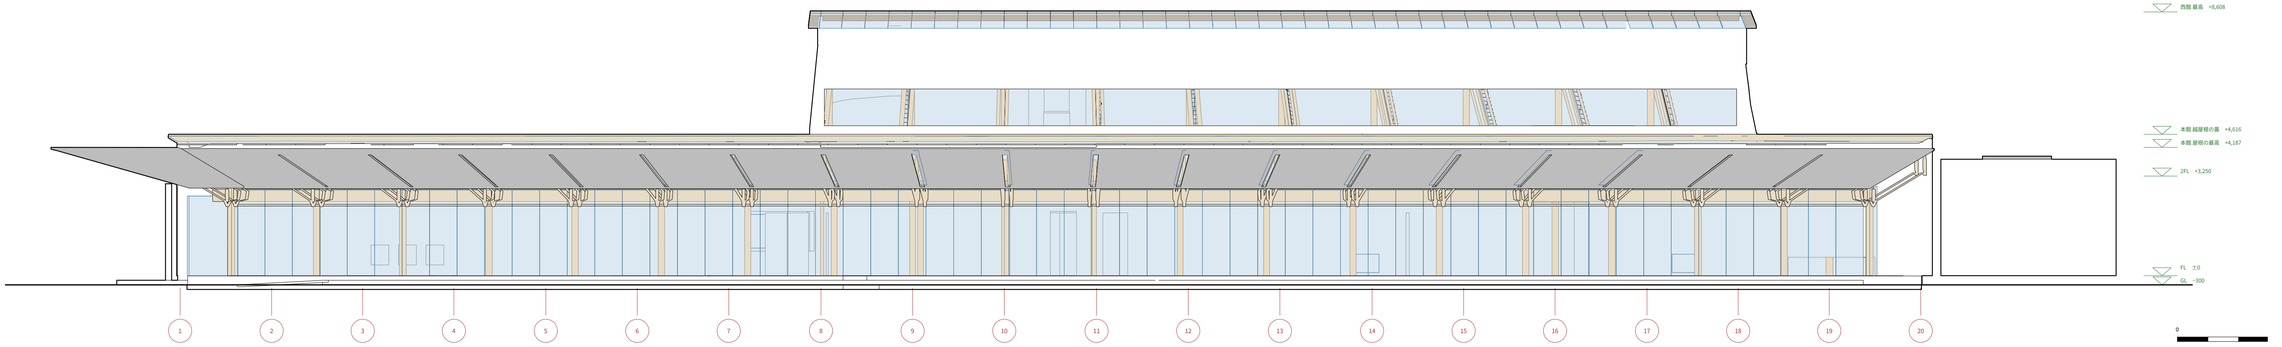


縦断面図A　1/100　保育室の中ほどの弧で切って展開、西を見る（左が南の高野川）

左（南）の高野川の崖から右（北）の大学へ、低い本館 → 高い西館 → おむすび。地域の建物の高低の流れに沿う

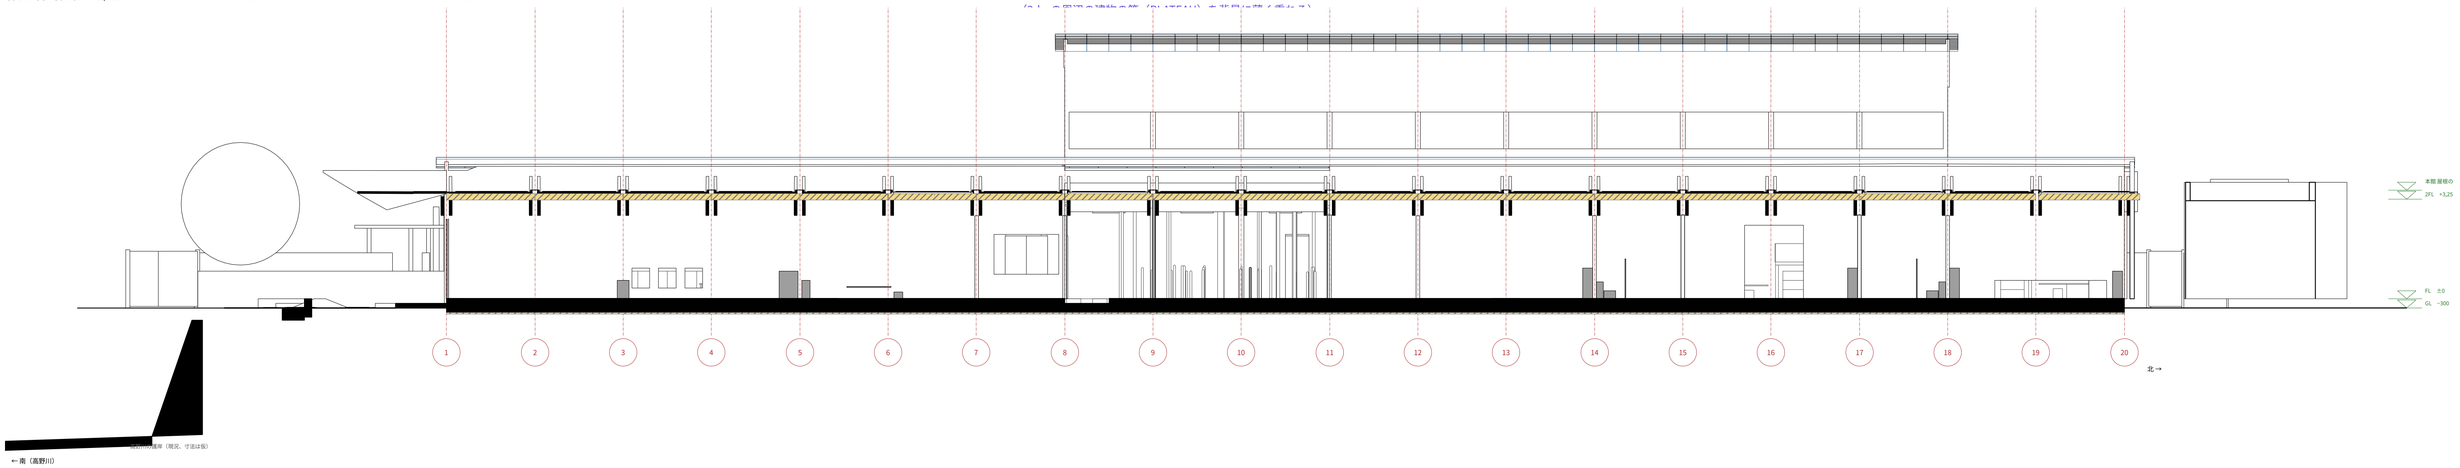


道路の側の立面図　1/100　西の道路から

西館の西端は1階の高さ（向かいの住宅を点線で描き足す）。西館の立ち上がりが北で主張する

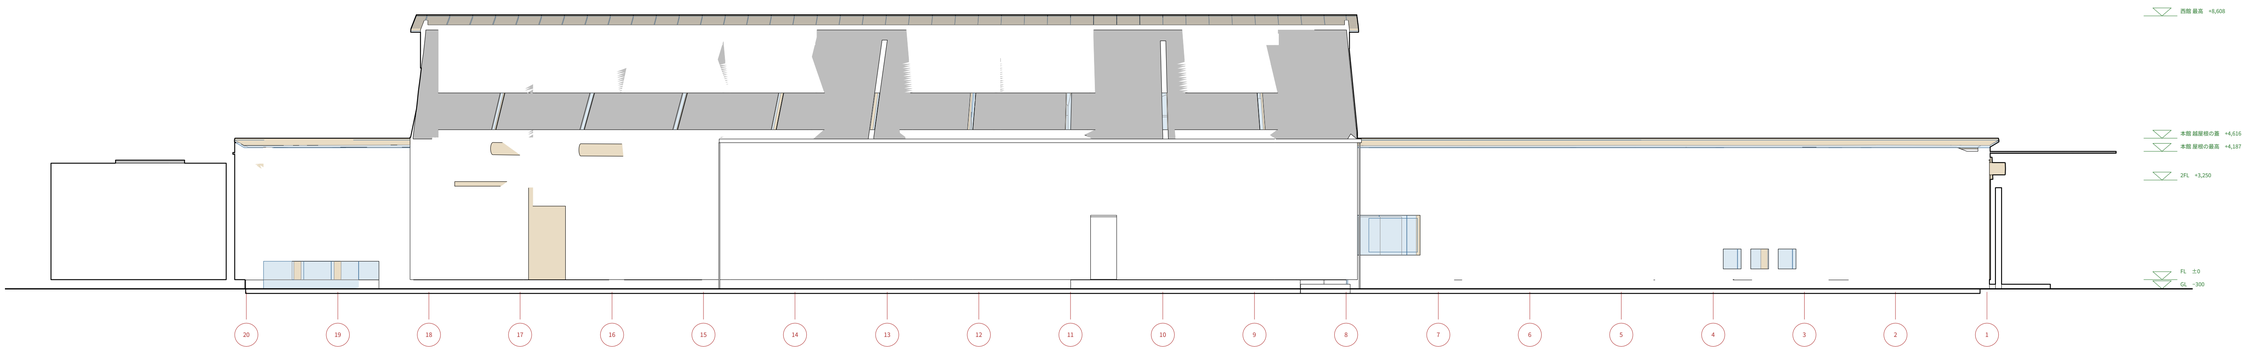

高野川の側の立面図　1/200　川の向こうから

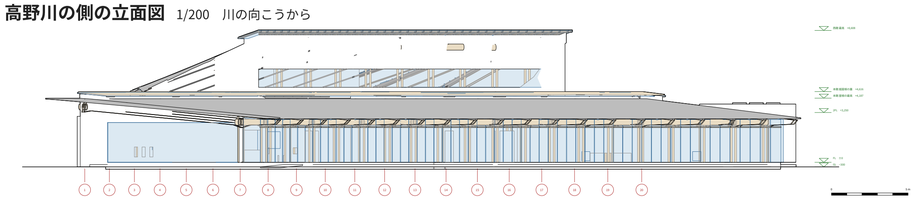

夜の立面（園庭の側）

黒地に越屋根の東の縁の光の線だけ
水平の光が一本、川向こうから見える
（模型の夜景写真でもよい）

景観の約束


景観条例の基準（高さ・屋根の形・色）を
守ることを一行で（地区の基準は確認）
高野川沿いの修景
小竹薮公園を残す

［割付の注記］フォーカス：高野川の側は低く、北の大学に向かって高く（地域の高低差の流れ）。同時に、伸びやかな梁・西館の立ち上がり・夜の水平の光で主張する　／　目に入る順：園庭の側の立面 → 縦断A（川から北へ）→ 道路の側の立面 → 高野川の側・夜

こどもたちの育ち舎　4/5　環境

断面図C　4歳・遊戯室の摺鉢ネット　1/50（1/100の自動の図を2倍）　西の道路から園庭へ

矢印：昼の道（青）と夏の夜の道（紺）。床下の底板t200と断熱の帯。光の筋の光

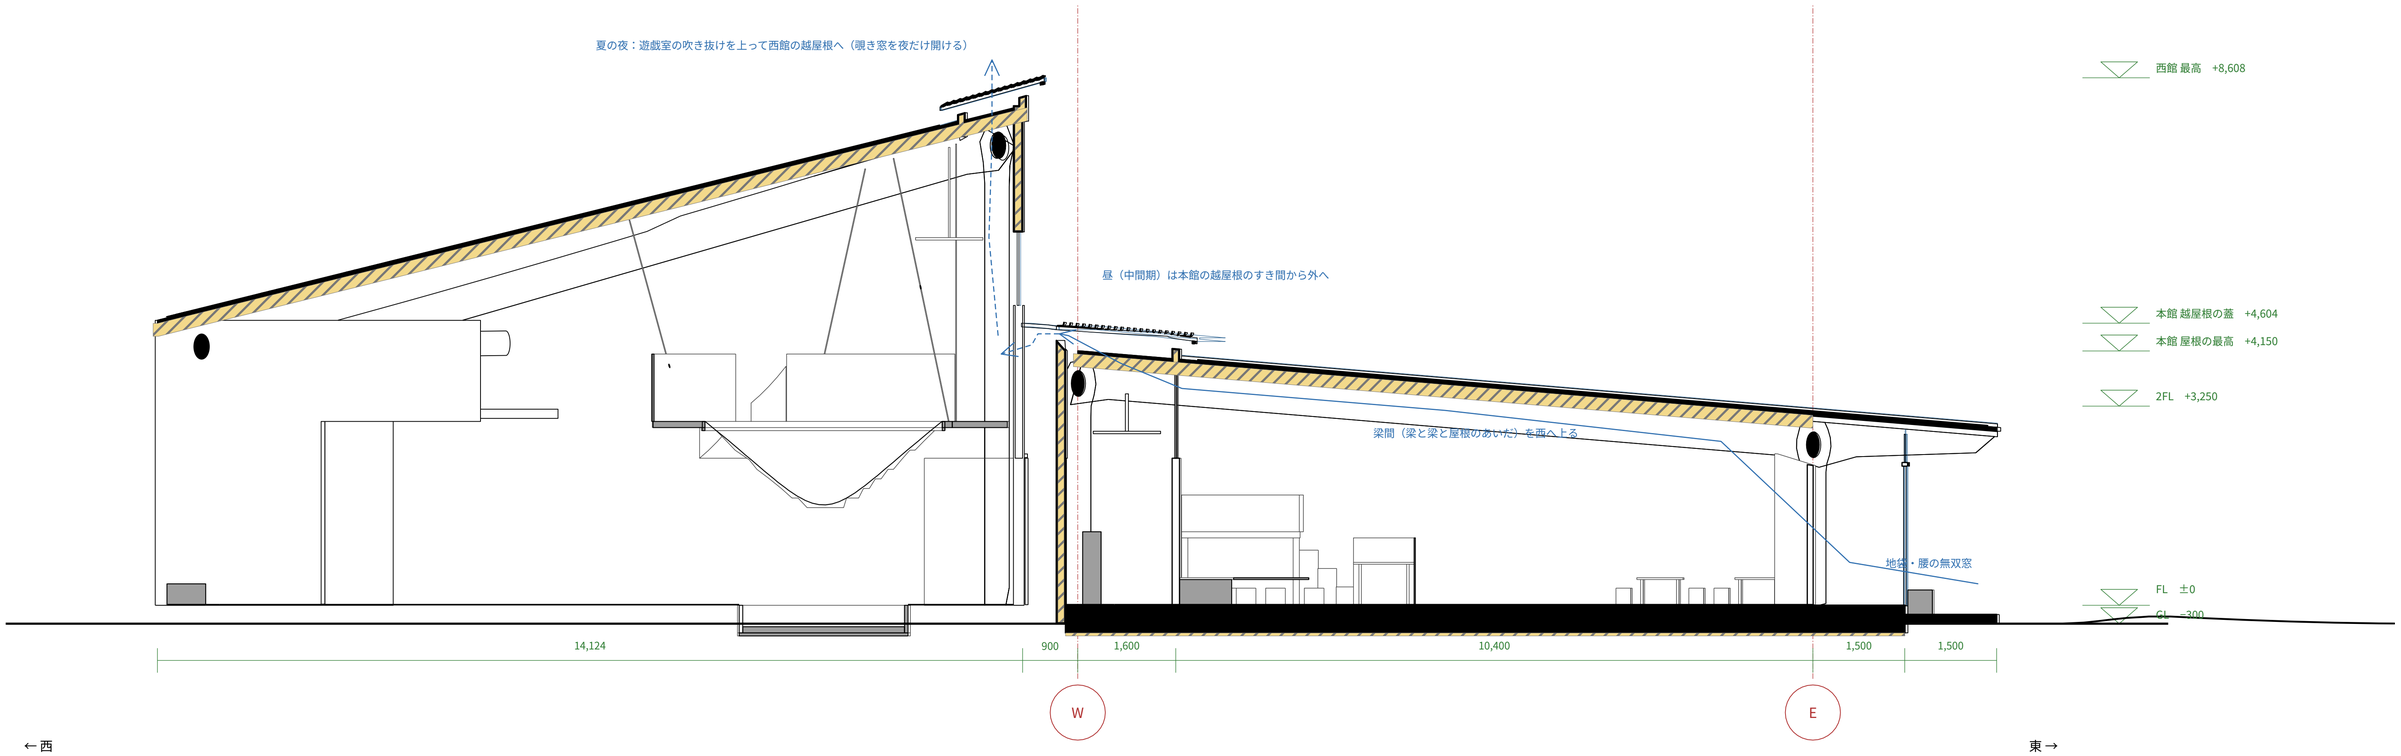

運転表

夏の昼
庇で遮る・天井扇
床下空調（底板の冷え）

夏の夜
縁側の段のガラリ→床下→梁間
→越屋根・遊戯室の吹き抜け

春・秋
越屋根の換気口を開ける
縁側を開け放す

冬
換気口を閉じる・熱交換
基礎断熱・屋根の断熱

環境への配慮（LEED v5 Gold相当を目指す）


パッシブ
床下に冷えをためる
越屋根の通風、光の筋の昼光

エネルギー
屋根材型の太陽光
蓄電池（災害時の拠点）

資源
北山杉の間伐材（山の手入れを支える）
地域のスギ、土・雨・生ごみを敷地で回す


時間
スケルトン＆インフィル
水まわりはどのスパンにも

断面図B　海峡　1/100　南の入口・キッチン・2階・すき間・本館・縁側

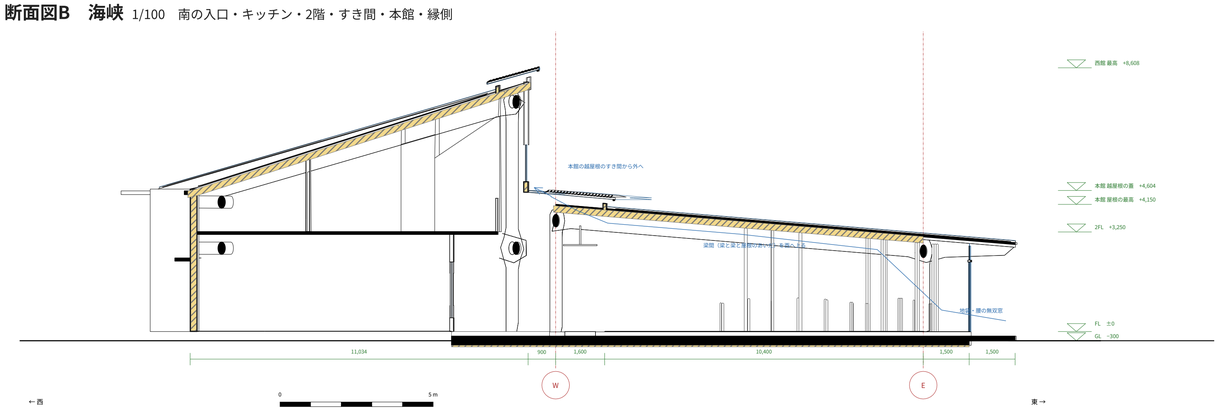

西館2階＝職員の側（休憩室・ぐったり休憩・会議室・更衣）。こどもから離れて休む

西館2階平面図　1/100　職員の側

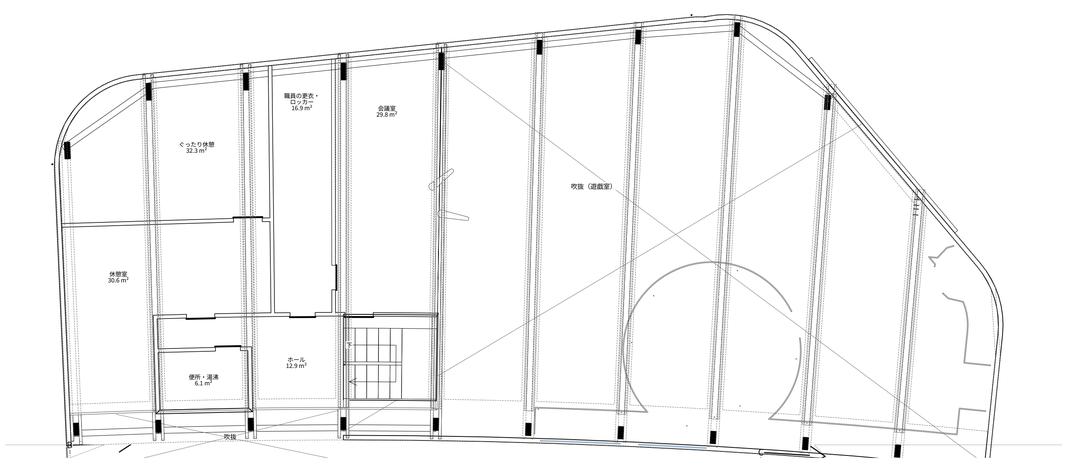

［割付の注記］フォーカス：木造・パッシブ（床下・越屋根・光の筋）で空調を補う。エネルギー・資源・時間（S&I）まで　／　目に入る順：断面C 1/50（昼と夏の夜の風、光の筋、床下）→ 運転表と4つの配慮 → 断面B → 2階（職員の側）


こどもたちの育ち舎　5/5　こどもたちへの環境

建築設計実習Ⅱ－Ⅰ　2026.11.05　木田


内観　ホール（A4）
北山杉の林・海峡と飛び石・オープンキッチン
梁の見える天井・光の筋・越屋根の光の線
（レンダリングか模型写真）

同じ部屋の一日　3〜5歳の保育室　断面


10:00
遊ぶ

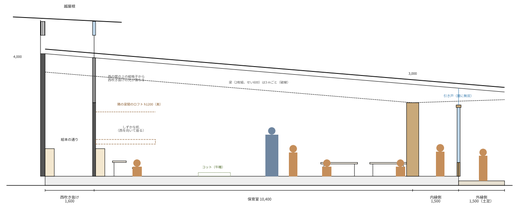


11:30
食べる

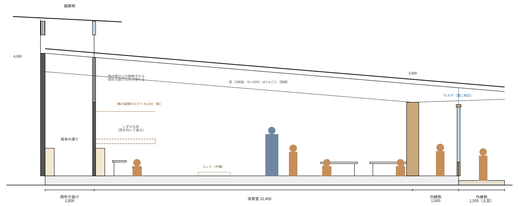

13:30
寝る

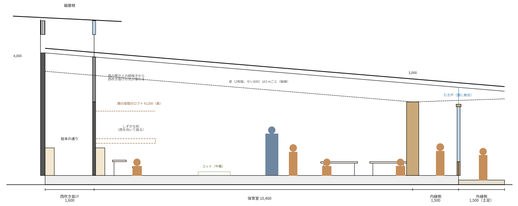

今は同じ図。部屋の分け方と天井の高低が決まったら描き分ける

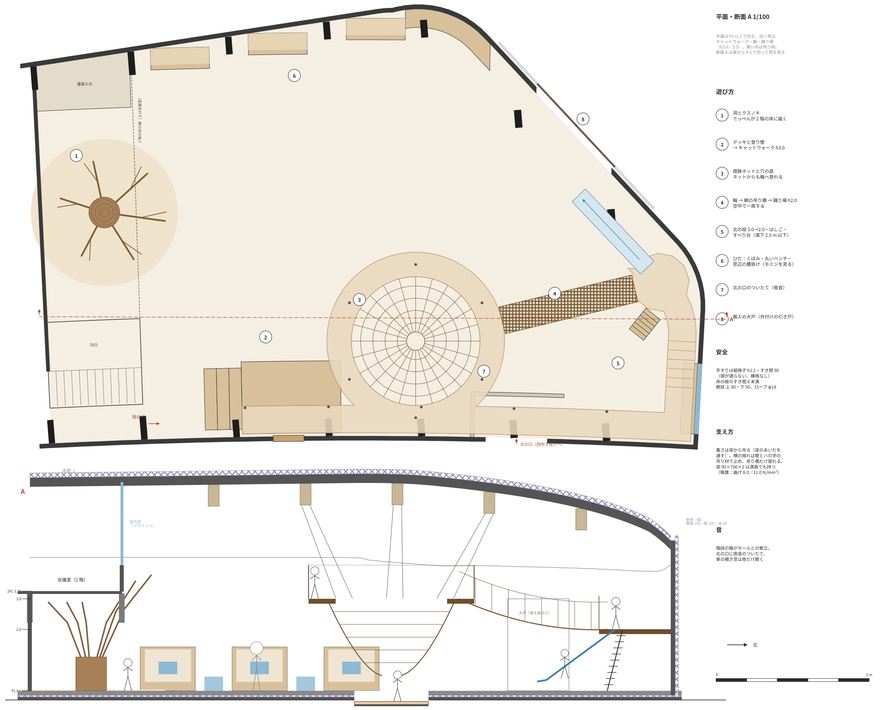
平面・断面 A 1/100
遊び方
1 ぼこスノメ
ちっちんぴょ 巻の床に敷く
2 デッキと登り壁
→ キャットウォーク 53.0
3 壁掛ネットと穴の底
ネットから along へ登れる
4 幅 一 鏡の高さ横 一 踊り場 52.0
空中で一周する
5 北の段 10〜20・ぼし ご・
すべり台（高さ 2.0 m 以下）
6 ひだ ・ くぼみ・丸いベンチ・
窓辺の腰掛け（をとコを見る）
7 北のひのついたて（地巻）
8 導入の大戸（内付けの引き戸）
安全
手すりは縦格子 ＆ L ＝ すき間 90
（頭が通らない 横格もよ）
床の段ですき間 ＆ 来落
絨毯 上 50・下 50、ロープ止め
変え方
重さは変から見る（窓のあいだを
ホールの北山杉の林 こどもの目の高さ（0.9 m）から
ホールの北山杉の林　こどもの目の高さ（0.9 m）から見た景色　（たたき台・6 版：すべて自立）
A　海峡から北を見る（世面のこども）
B　外縁部から西を見る（園庭から入ってくる）
A　本棚と西面の取り合い（越屋根を含む）　断面詳細（架構 9 の面）　1/40
A'　キャップがすき間をまたぐところ　1/10
洞のクスノキ　断面パース（遊戯室のチャット）
洞のクスノキ
2 階の床の下の低い洞（梁の下 2.23）。クスノキの枝の先が天井に触れ、木が 2 階を支えているように見える。
北の枝は床の線の下をくぐって遊戯室の高い側へ（この図では切断面で切れている）。
光の筋と架構　1/20
2枚の梁のあいだ180の上に
乳白ガラスの光の筋
垂木・楕円の桁と一枚で（作成）
スケルトン＆インフィル
３ｍスパンの架構（固定）と
間仕切りA・B・C、家具（可変）を色分け
どのスパンにも上水・下水の口
今 ／ 定員が変わる ／ 学童・地域の場
の3コマ
面積表　m²（壁芯、3dmから自動）
室 | 要求 | 計画
乳児室（0〜1歳） | 約60×2 | 120.5
保育室（2歳） | 約60 | 60.0
保育室（3〜5歳） | 約60×3 | 181.3
遊戯室 | 240以上 | 243.5
便所 | 適宜 | 57.3
食堂 | 必要に応じて | 21.9
園庭 | 350以上 | 982.2
事務室 | 約60 | 73.8
休憩室 | 約60 | 62.9
医務室 | 約30 | 30.1
調理室 | 約60 | 65.7
便所（大人用） | 適宜 | 17.1
機械室 | 約30 | 30.0
駐車場 | 5台以上 | ○
延床（2,000以内） | | 1,286.5
inspired by
Asilo Nido Iride
Mario Cucinella Architects・Guastalla・2015
→ 梁の列が並ぶ長細い本館と、外に付く付属の建物
Tamedia
坂茂・Zürich・2013
→ 梁の端の楕円の頭と、それを貫く楕円の桁
レイモンド斑鳩こども園
キノアール テクツ・斑鳩・2026
→ 室内に木を立てる（ホールの北山杉）
KAIT工房
石上純也・厚木・2008
→ 柱の配列：見る向きで景色が変わる並び
認定こども園らみどり
はりゅうウッドスタジオ・須賀川・2026
→ 内と外の二重の縁側、遊具を置かない地形の園庭
仙田満の園舎
環境デザイン研究所
→ 揺動のネット、キャットウォーク、ニッチ
Waldorf School of the Peninsula
California
→ 遊戯室の切り株

［割付の注記］フォーカス：娘にこんな環境を与えたい、という空間：遊戯室・切り株・北山杉の林・組み方・変わり方　／　目に入る順：内観 → 遊戯室 → 同じ部屋の一日 → 林・洞 → 接合部 → S&I → 面積表 → inspired by