平面図　1階　FL+1500 で切断　1/100

高野川を下に（配置図と同じ向き）。一点鎖線は敷地の境。二点鎖線は屋根の外形（軒の線）。周りの道・建物は細い線。スパンの寸法はスパン10の庭の側に重ねた5本（建物に近い順に、放射の線のあいだの角度／W通りの上の弧長／E通りの上の弧長／西館の東端の弧長／西館の西端の弧長）
長手の全体は外がW通り（背骨）、内がE通りの上の弧長。二点鎖線の寸法は背骨（W通り）の弦。寸法はmm

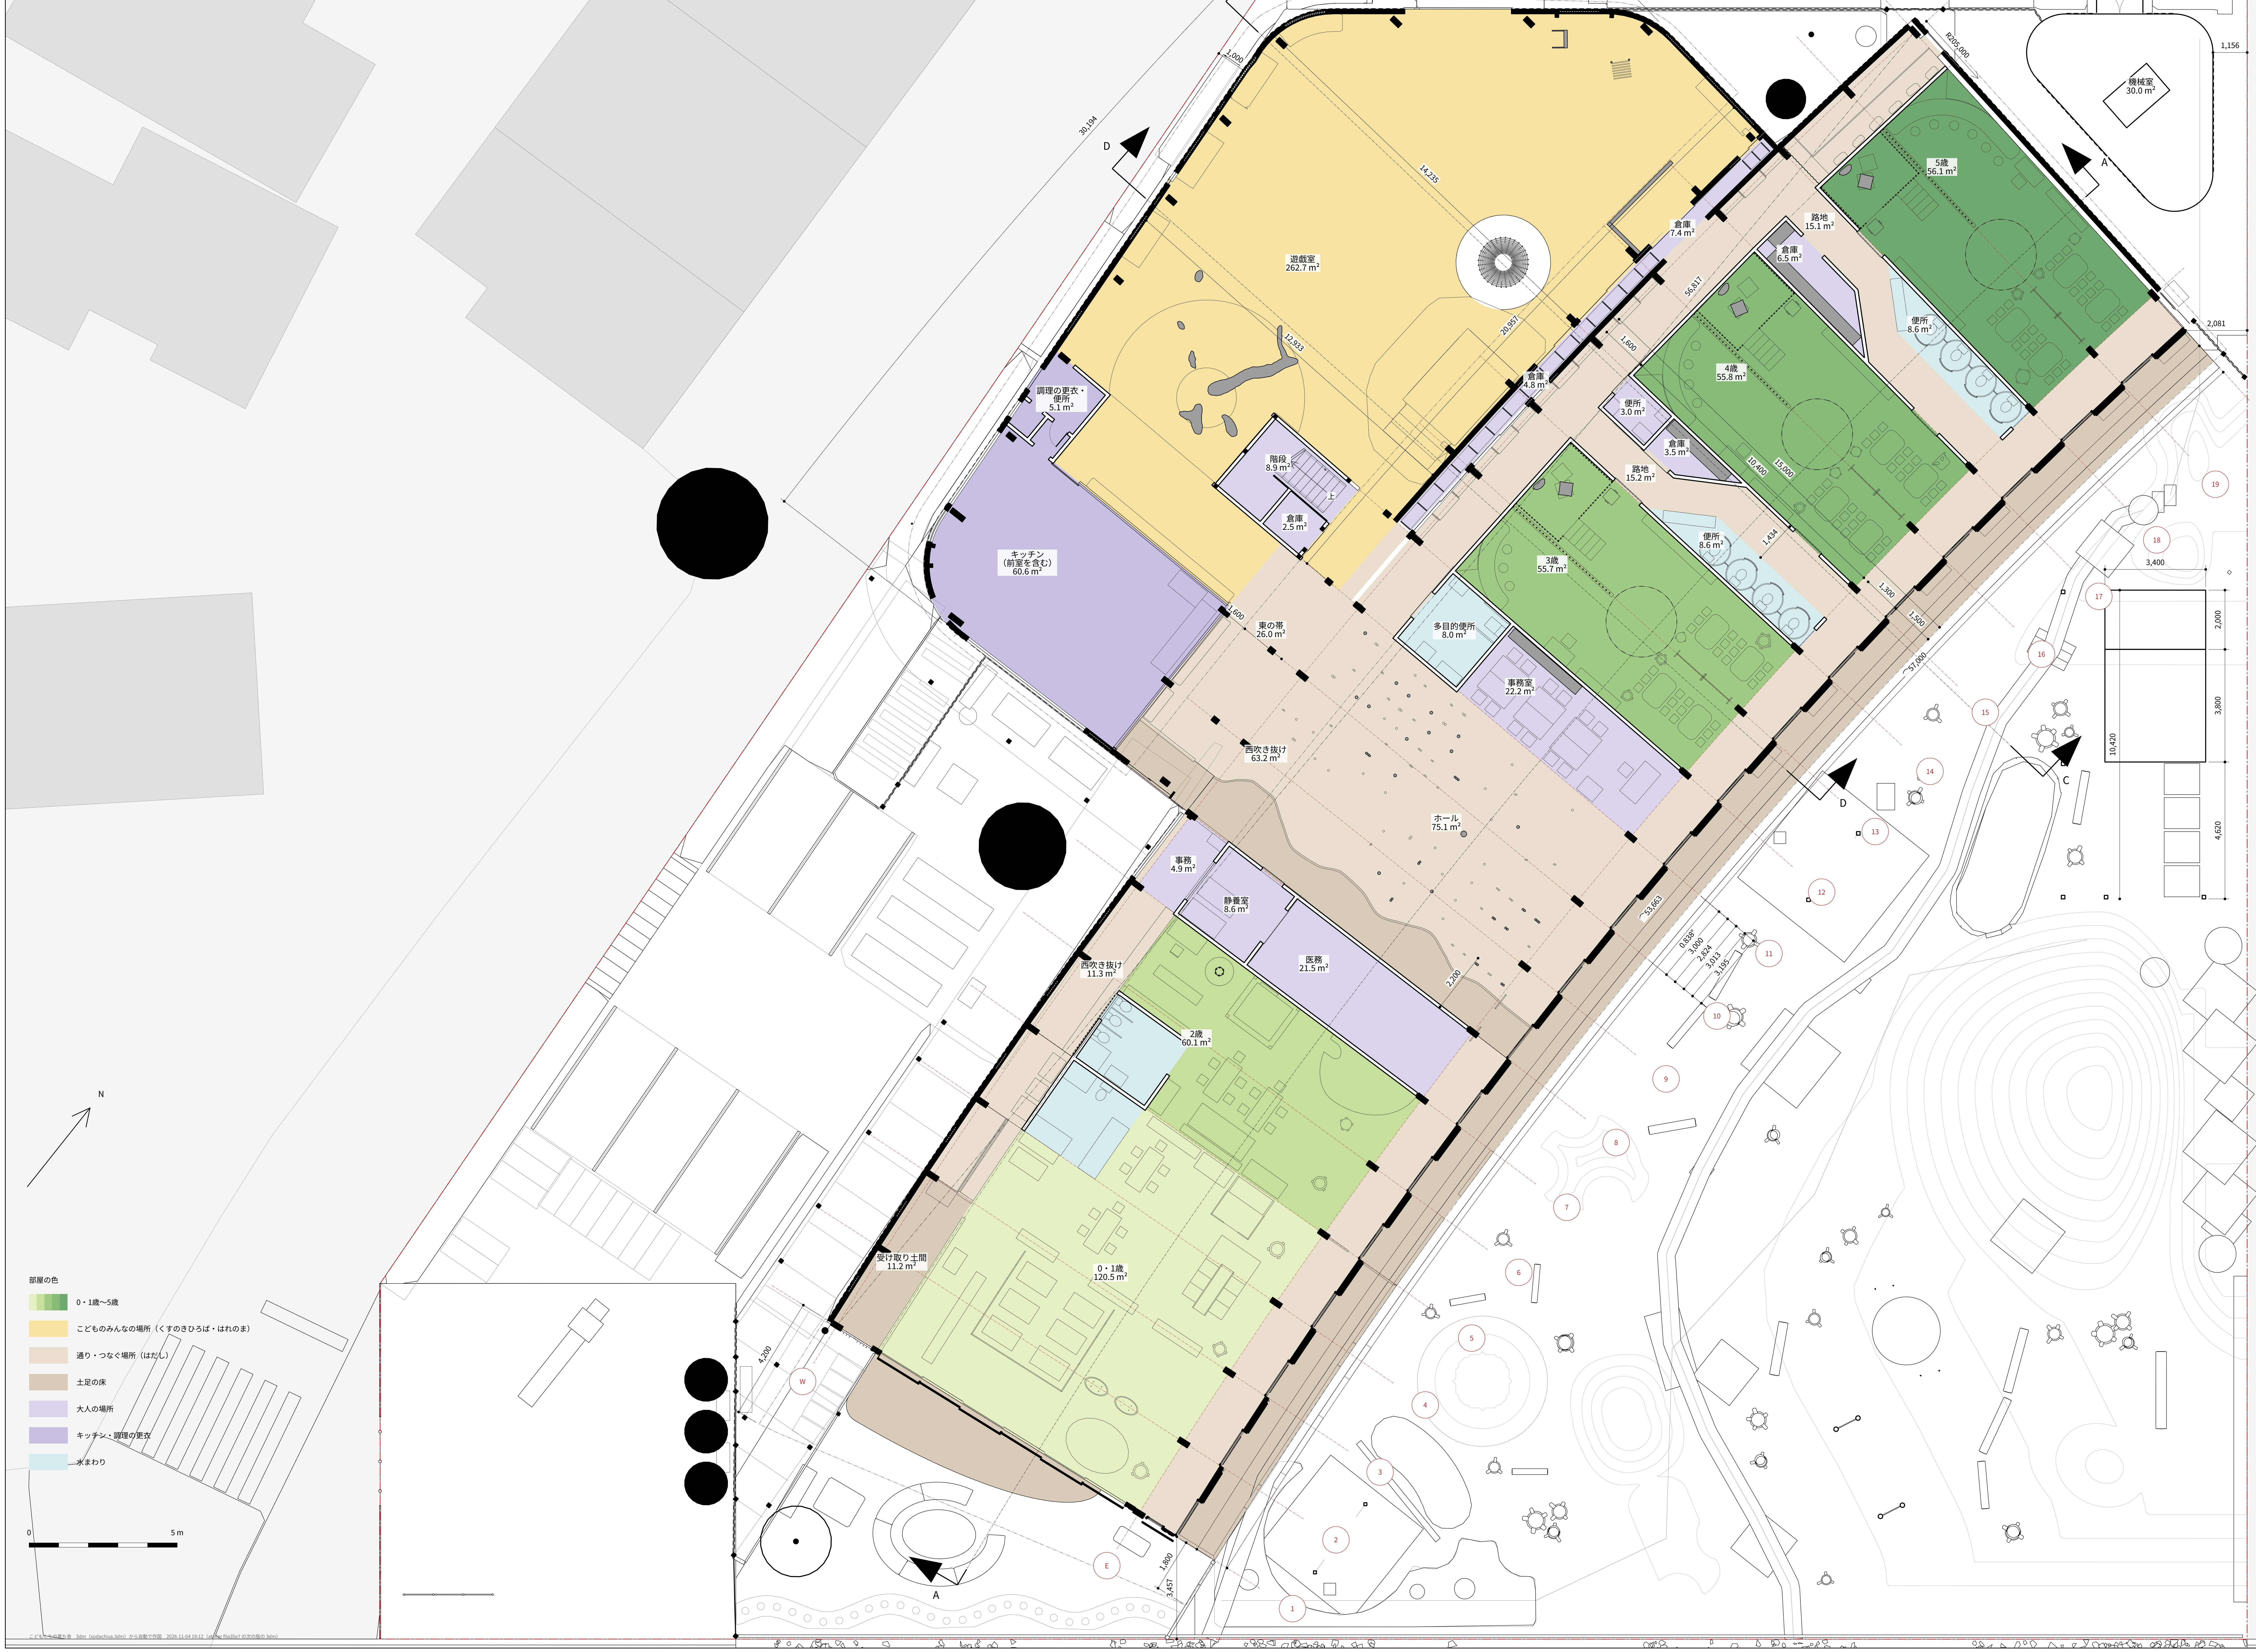

部屋の色

- 🟩 0・1歳〜5歳
- 🟨 こどものみんなの場所（くすのきひろば・はれのま）
- ▨ 通り・つなぐ場所（はだし）
- 🟫 土足の床
- 🟪 大人の場所
- 🟪 キッチン・調理の更衣
- 🟦 水まわり

0　5 m

こどもたちの育ち舎　3dm（sodachiya.3dm）から自動で作図　2026-11-04 19:12（atelier f0a35e7 の次の版の 3dm）