
壁に貼ったとき　左：1〜3 を縦につなぐ（高さ約 1.8 m）　右：4・5 を縦につなぐ

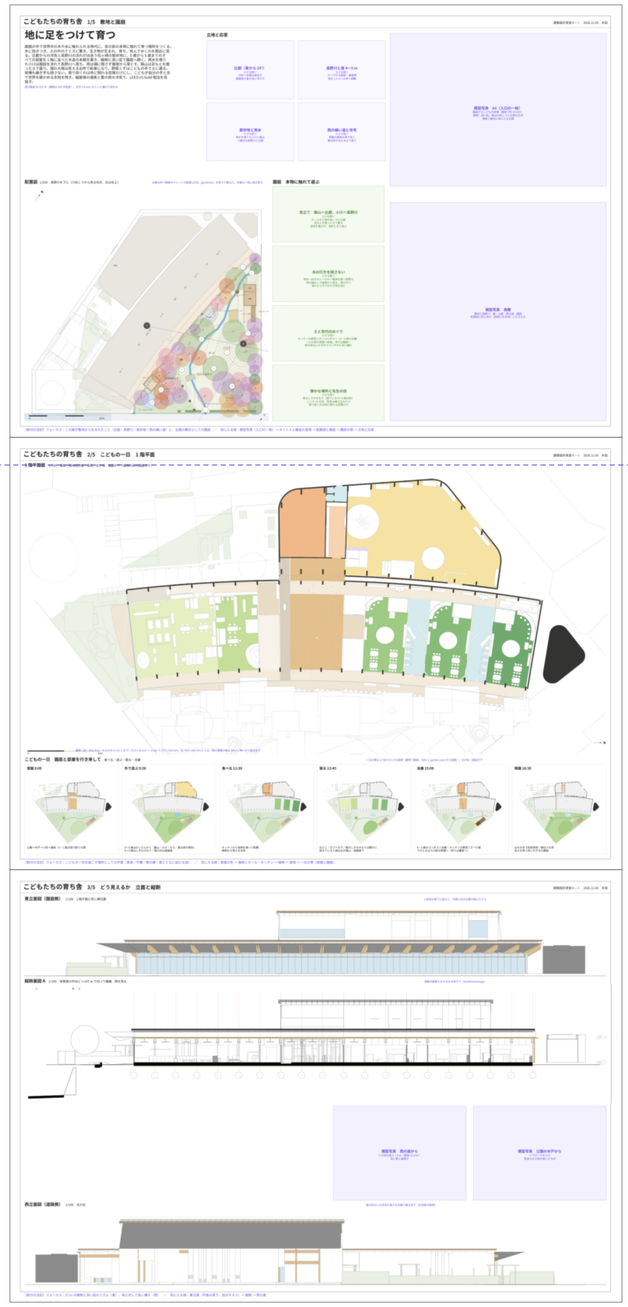

目の高さ 1.5 m

左の列は 配置 1/200 → 1 階平面 1/100 → 立面・縦断 1/100。

2・3 は北が右・園庭が下で柱が縦にそろう。1 の配置は高野川が下（北は右上）。

目の高さに来るのは 1 階平面（最も細かい図）と断面 C。

右の列は下端が約 0.6 m。暮らしと構造は近づいて読む。

製図台に置くなら 2＋2＋1（1・2／3・4／5）に切り分ける。

床

地に足をつけて育つ

画面の中で世界中の木や水に触れられる時代に、目の前の本物に触れて育つ場所をつくる。木に抱きつき、土の中のミミズに驚き、生き物が生まれ、育ち、死んでゆくのを間近に見る。比叡からの冷気と高野川の流れが出会う松ヶ崎の扇状地に、0 歳から 5 歳までのすべての部屋を 1 階に並べた木造の本館を置き、縁側と深い庇で園庭へ開く。用水を借りた小川は園庭を流れて高野川へ落ち、雨は樋に隠さず屋根から落とす。築山は足もとを掘った土で盛り、畑の大根は見える台所で給食になり、野菜くずはこどもの手で土に還る。架構も継ぎ手も隠さない。取り除くのは命に関わる危険だけにし、こどもが自分の手と舌で世界を確かめる余地を残す。越屋根の通風と夏の夜の冷気で、LEED v5 Gold 相当を目指す。

設計趣旨 約 325 字（課題は 300 字程度）。文字 3.6 mm なら 1 m 離れて読める

立地と応答

比叡（東から 24°）
小さな図＋
冷気→本館は東向き
越屋根で夏の夜に冷やす

高野川と崖 4〜5 m
小さな図＋
川へ下がる屋根・植栽帯
浸水 1.5 m→大学へ避難


扇状地と用水
小さな図＋
用水を借りた小川と築山
＝園内の高野川と比叡

西の細い道と住宅
小さな図＋
西館の屋根を西で低く
車は突き出た木より南で

模型写真　A4（入口の一枚）
園庭からこどもの目線（模型で約 10 mm）
縁側・深い庇・築山の向こうに比叡の方向
選抜で最初に目に入る位置

配置図　1/200　高野川を下に（川向こうから見る向き、北は右上）

点線の枠＝園庭のチャットの配置 1/200（garden01）を実寸で重ねた。本番は一枚に描き直す

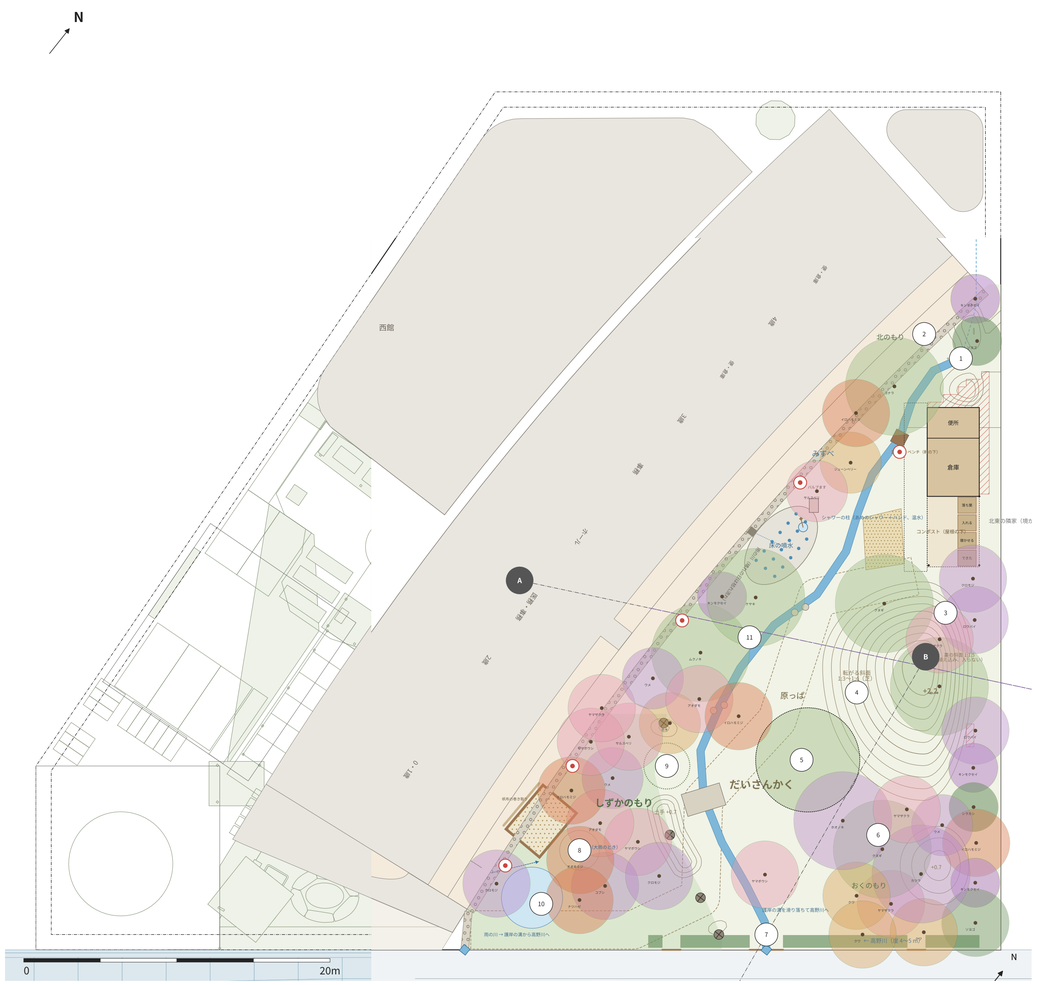

園庭　本物に触れて遊ぶ

見立て　築山＝比叡、小川＝高野川
小さな図＋
ホールから頂の向こうに比叡
足もとを掘った土で盛る
遊具を置かず、地形と木で遊ぶ

水の行方を隠さない
小さな図＋
用水→みなもと→小川→護岸の溝→高野川
雨は樋なしで屋根から落ち、雨の川へ
溢れたらすりばちが雨の池に

土と世代のめぐり
小さな図＋
キッチンの野菜くず→コンポスト（4・5 歳の当番）
→入口前の菜園→給食、余りは農家へ
柳の家は上の子が小さい子のために編む


静かな場所と先生の目
小さな図＋
南のしずかのもり（寝ている 0〜2 歳の前）
ニッチ 11 か所、死角は植え込みだけ
取り除くのは命に関わる危険だけ

模型写真　鳥瞰
敷地と高野川・崖・公園・西の道・園庭
配置図と同じ向き（高野川を手前）にそろえる

［割付の注記］フォーカス：この案が敷地から生まれたこと（比叡・高野川・扇状地・西の細い道）と、主題の舞台としての園庭　／　目に入る順：模型写真（入口の一枚）→ タイトルと趣旨の冒頭 → 配置図と園庭 → 園庭の筋 → 立地と応答

こどもたちの育ち舎　2/5　こどもの一日　1 階平面

1 階平面図　1/100　道路・隣地境界線・家具。北が右、園庭が下（縁側の前の園庭まで）

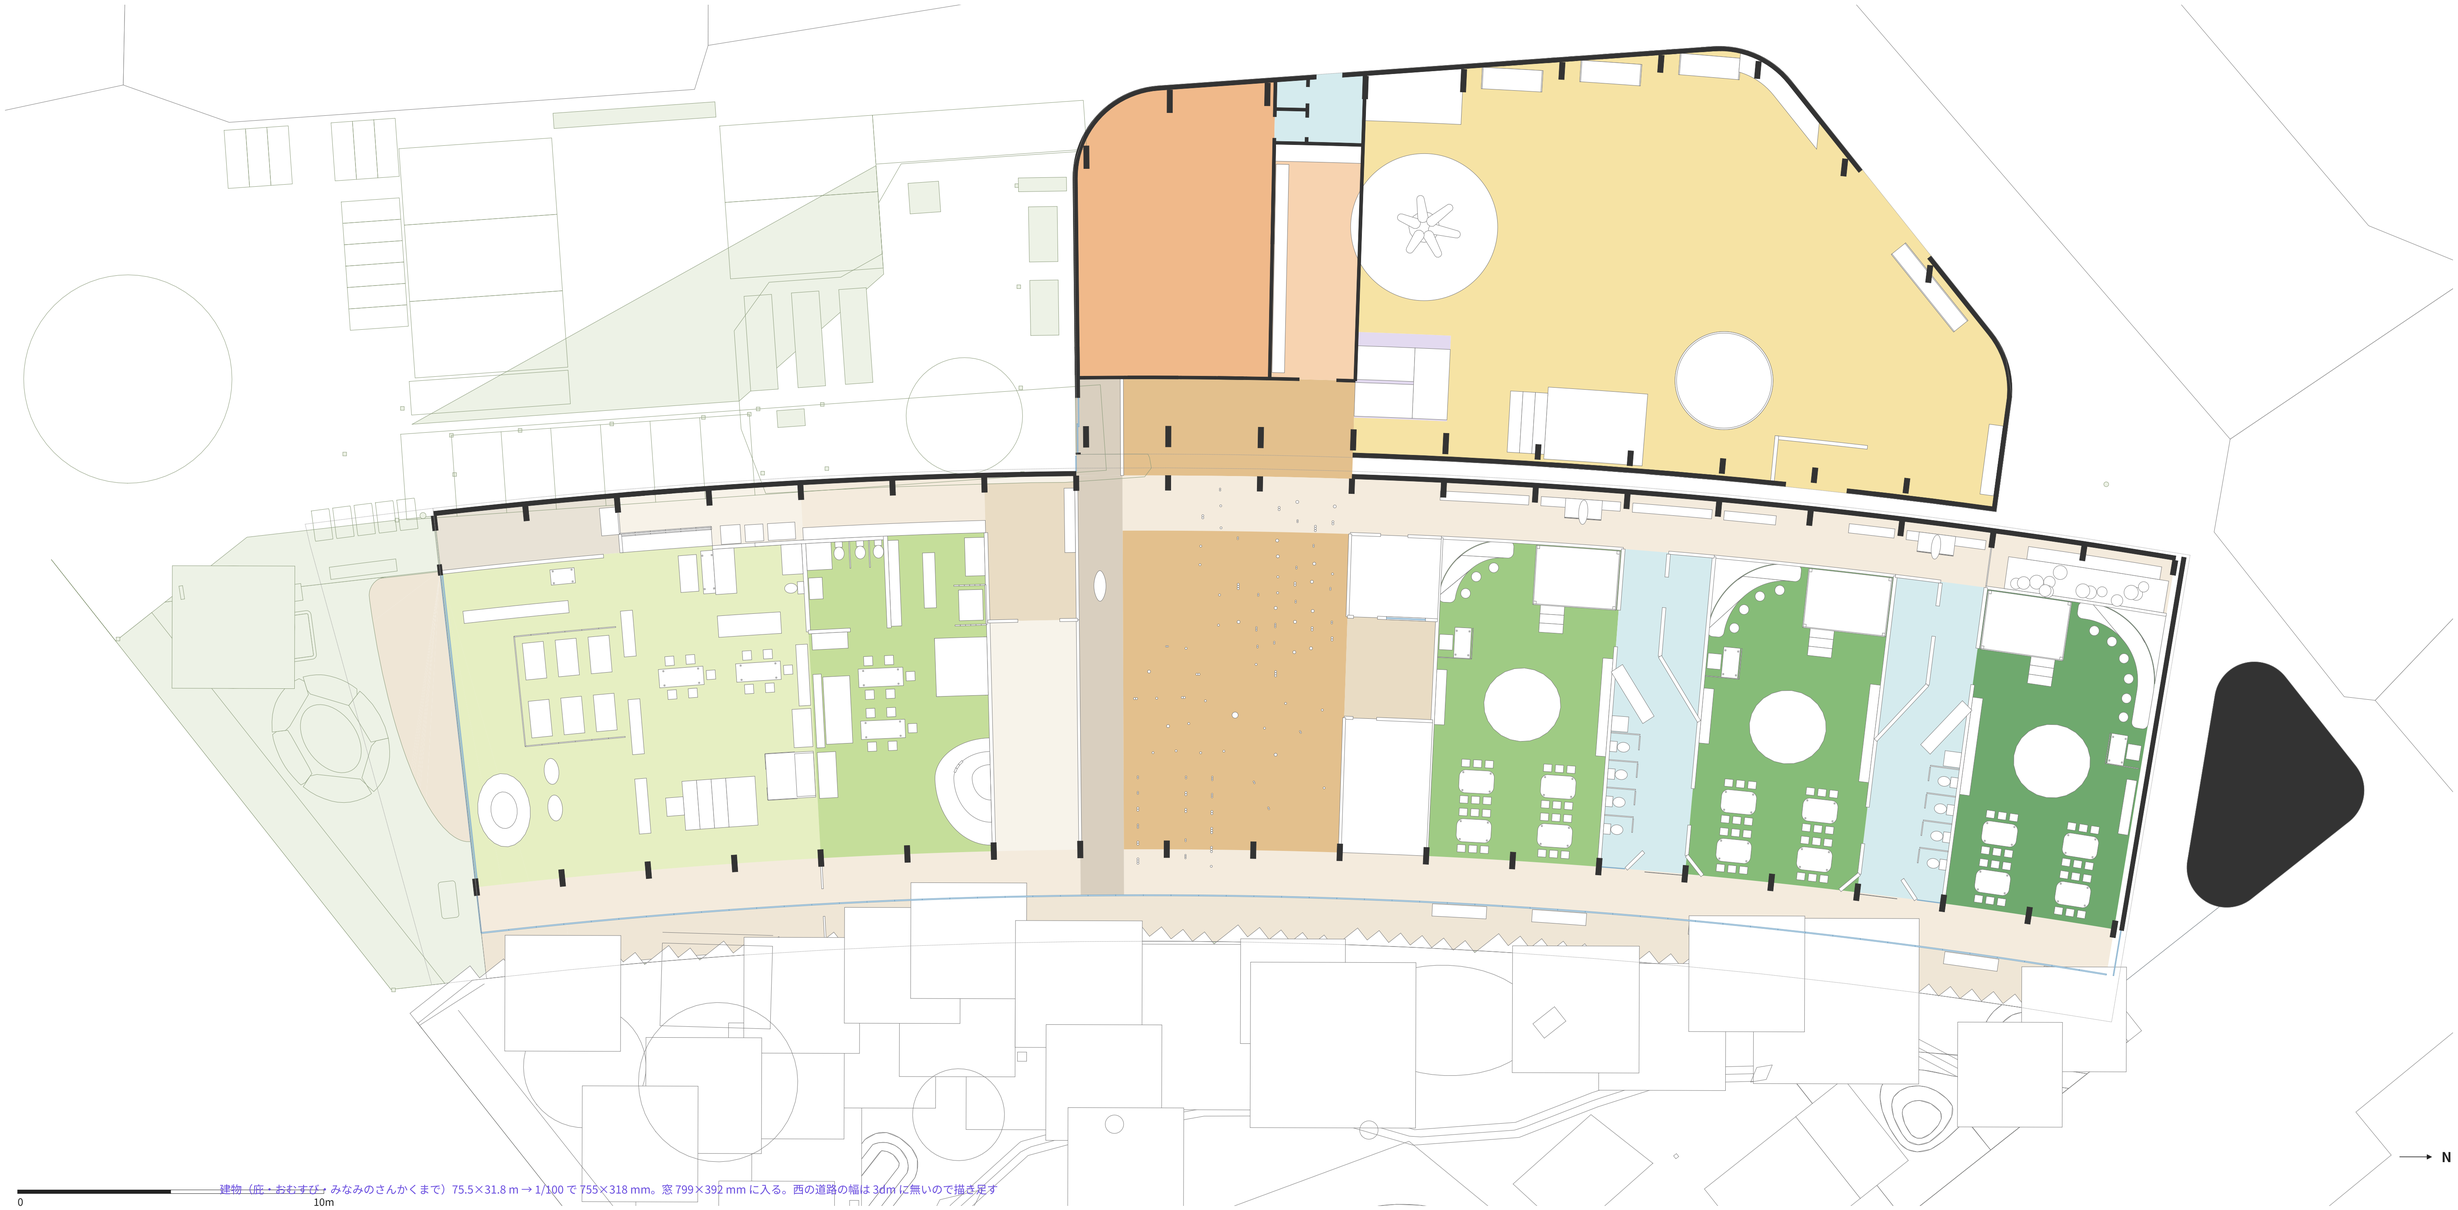


建物（低・おむすび・みなみのさんかくまで）75.5×31.8 m → 1/100 で 755×318 mm。窓 799×392 mm に入る。西の道路の幅は 3dm に無いので描き足す

こどもの一日　園庭と部屋を行き来して　食べる・遊ぶ・寝る・当番


一日の帯は 1/700 の小さな配置（建物＋園庭、3dm と garden.json から自動）。北が右・園庭が下

登園 8:00

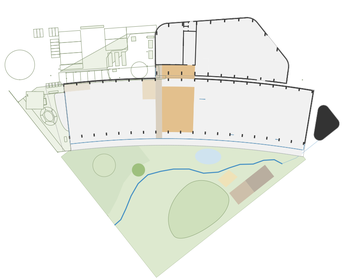

公園→木戸→小径→海峡／0・1 歳は受け取り土間

外で遊ぶ 9:30

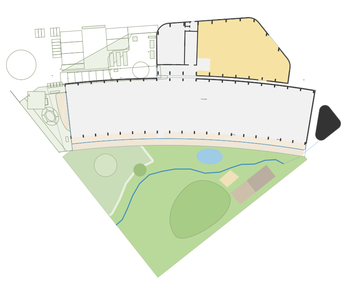

3〜5 歳はだいさんかく（築山・小川・もり、夏は床の噴水）
0〜2 歳はしずかのもり／雨の日は遊戯室

食べる 11:30




キッチンから海峡を通って配膳
縁側から見える台所

寝る 12:45




ねどこ・ロフトの下／南のしずかのもりは静かに
起きている 5 歳は北の築山・遊戯室で

当番 15:00

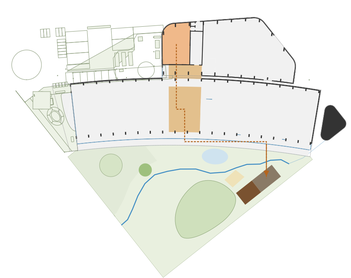

4・5 歳のコンポスト当番：キッチンの野菜くず→小屋
できた土は入口前の菜園へ（余りは農家へ）

降園 16:30

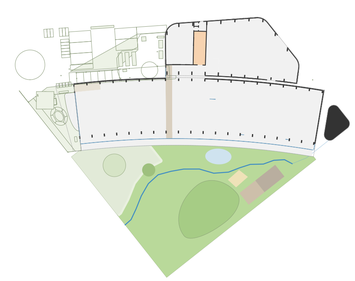

はれのまで延長保育／縁台でお茶
迎えを待つあいだ夕方の園庭


［割付の注記］フォーカス：こどもが一日を過ごす場所としての平面（家具・午睡・靴の線・歳とともに延びる道）　／　目に入る順：部屋の色 → 海峡とホール・キッチン → 縁側 → 家具 → 一日の帯（部屋と園庭）

こどもたちの育ち舎　3/5　どう見えるか　立面と縦断

建築設計実習Ⅱ―Ⅰ　2026.11.05　木田

東立面図（園庭側）　1/100　1階平面と同じ横位置


2枚目の真下に貼ると、平面と柱の位置が縦にそろう

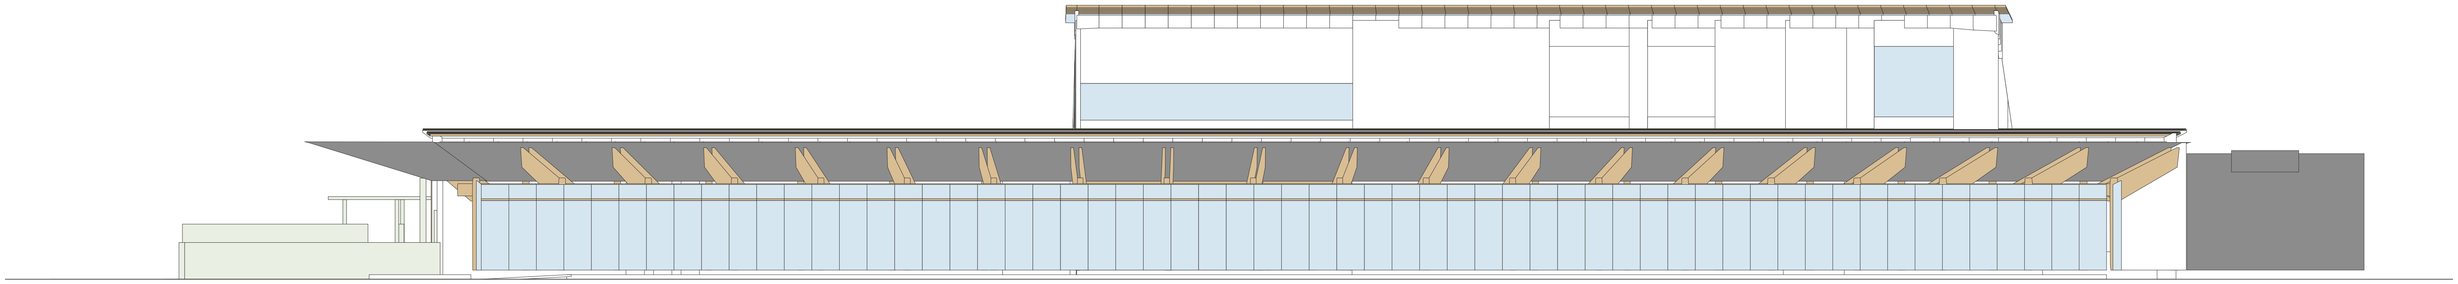

縦断面図 A　1/100　保育室の中ほど r=197 m で切って展開、西を見る

自動の断面Aをそのまま実寸で（model/drawings）

断面 A　縦断（展開）　保育室の中ほど r=197 m の弧で切って平らに伸ばす、西を見る

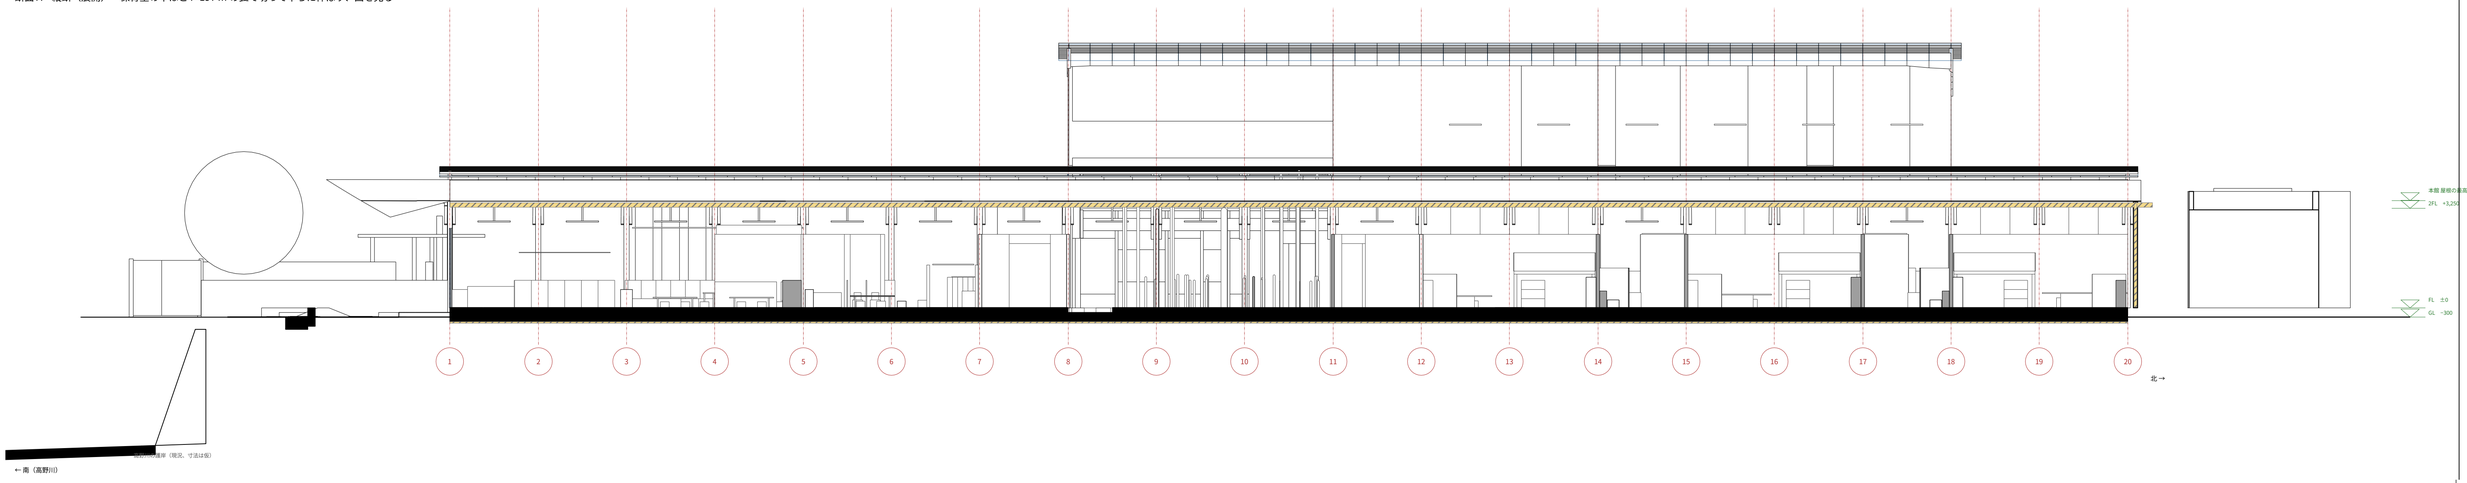


模型写真　西の道から
人の目の高さ 1.5 m（模型 15 mm）
低い軒と縦格子

模型写真　公園の木戸から
アプローチの入口
見送りの小径の奥にひろば

西立面図（道路側）　1/100　北が左

道の向かいの住宅の高さを点線で描き足す（圧迫感の説明）

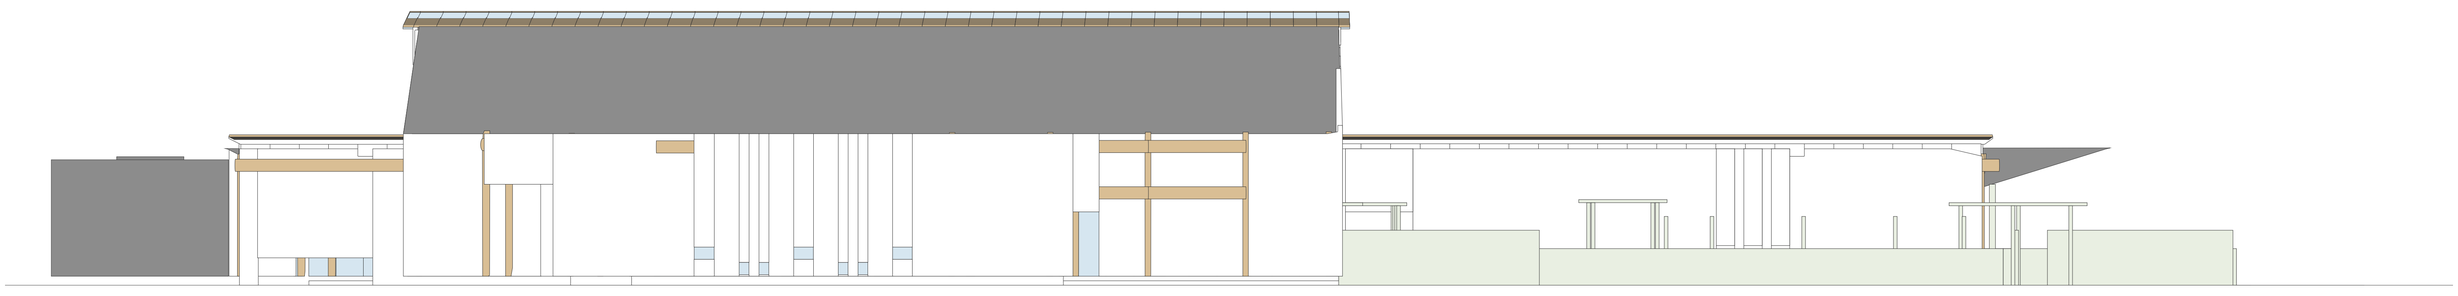


［割付の注記］フォーカス：57 m の縁側と深い庇のリズム（東）、街に対して低い構え（西）　／　目に入る順：東立面（平面の真下、柱がそろう）→ 縦断 → 西立面

こどもたちの育ち舎　4/5　どう息をするか　断面と環境

断面図 C　4 歳・遊戯室　1/50（1/100 の自動の図を 2 倍）　西の道路から園庭へ

左右に 道・向かいの住宅／園庭・築山 を描き足す。空気の矢印と①〜⑨を重ねる。断熱は帯で

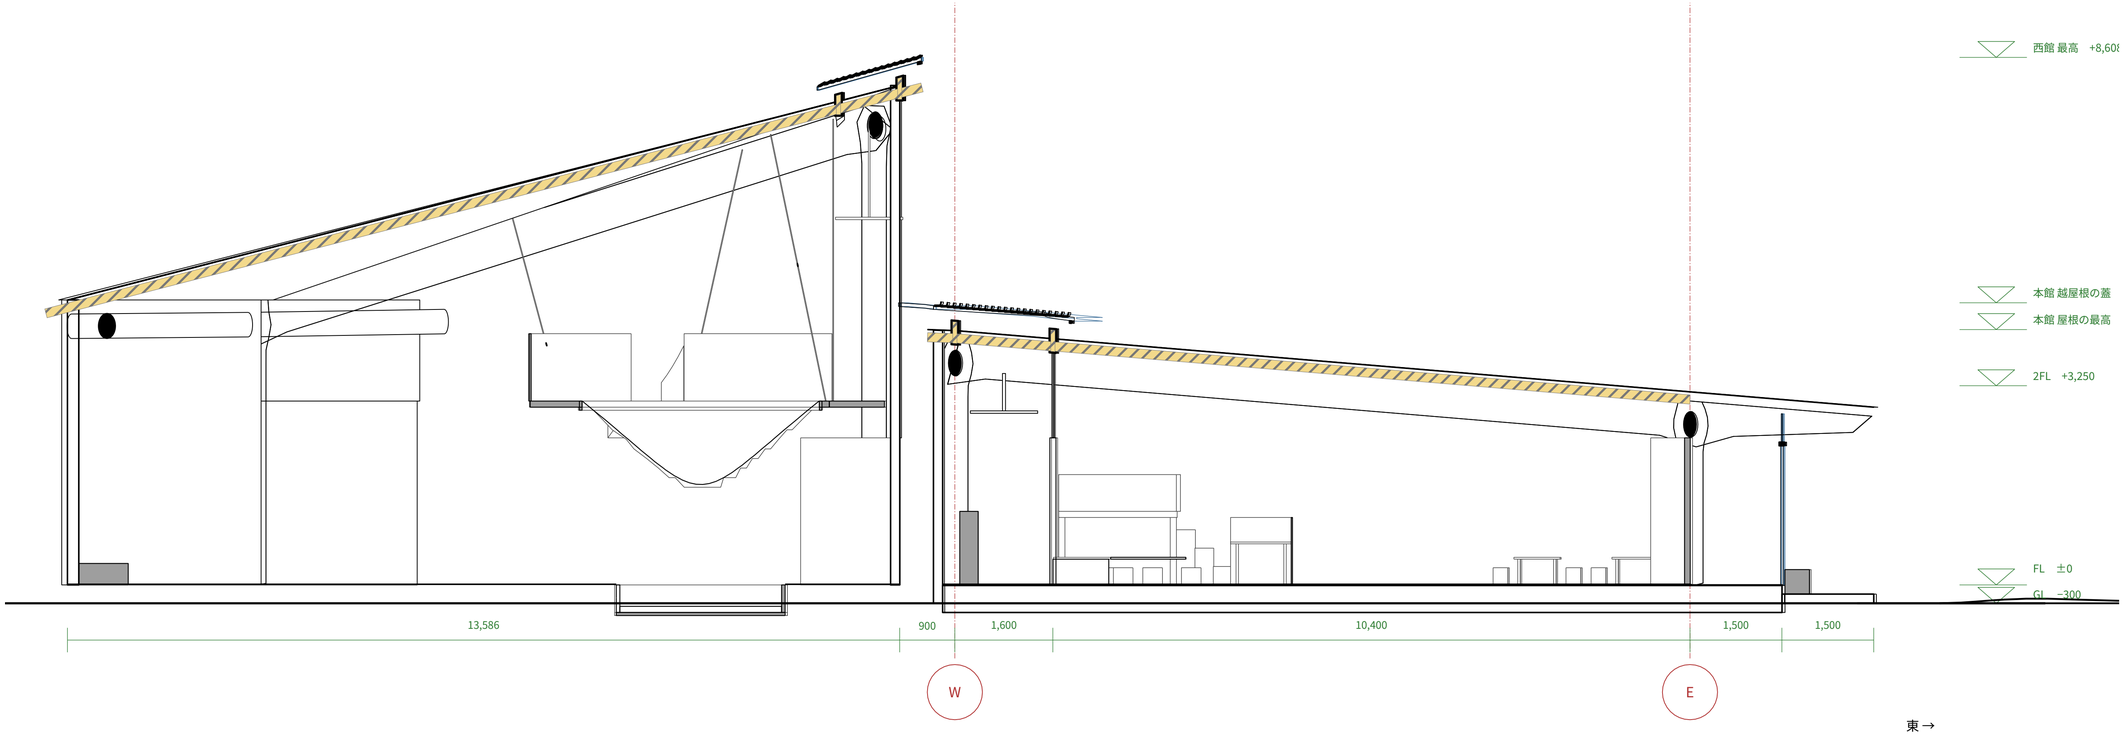

環境の枠
LEED v5
Gold 相当

脱炭素 ①〜⑤
生活の質 ⑥⑦
生態系 ⑧⑨


夏の昼
庇で遮る・越屋根から抜く

夏の夜
比叡の冷気で冷やす（自動の窓）


春・秋
手で開ける（表示灯）

冬
床暖房・熱交換の換気・断熱

断面図 B　海峡　1/100　南の入口・キッチン・2 階・すき間・本館・縁側

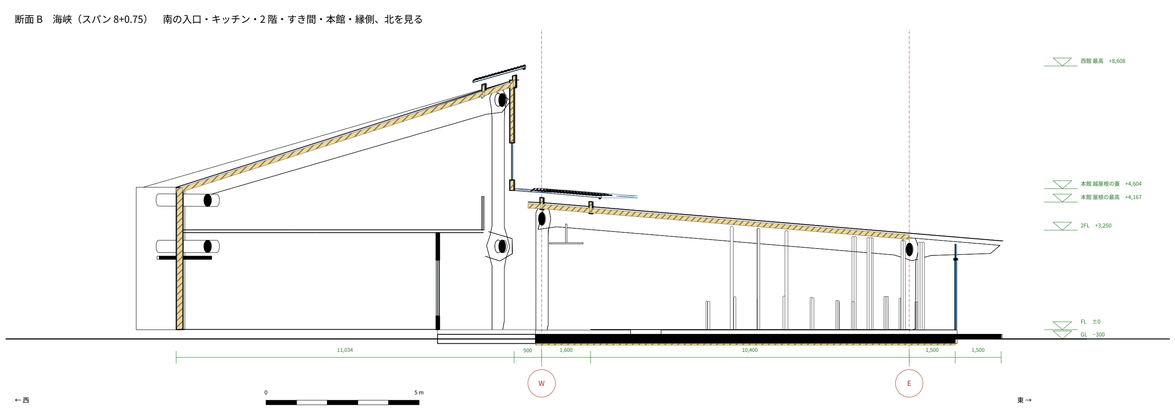

2 階平面図（西館）　1/100

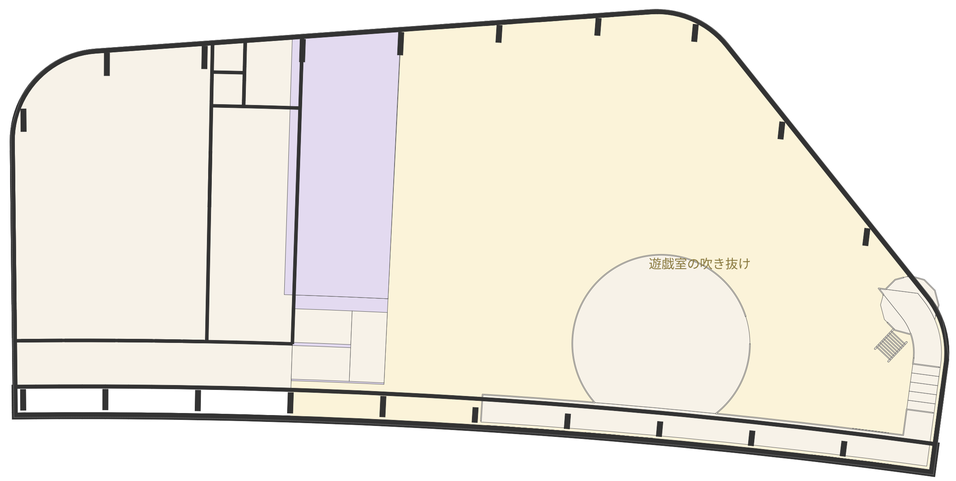

西館 33×17 m → 326×172 mm（1 階平面と同じ向き）


［割付の注記］フォーカス：空気・光・熱の流れが形の理由になっていること（断面 C を主役に）　／　目に入る順：断面 C 1/50 → ①〜⑨ と環境の枠 → 運転表 → 断面 B → 2 階

こどもたちの育ち舎　5/5　暮らしと構造


内観　ホール（A4）
海峡と飛び石・オープンキッチン
梁の見える天井・越屋根の光の線
（レンダリングが模型写真）

同じ部屋の一日　3〜5 歳の保育室　断面 1/100


10:00
遊ぶ

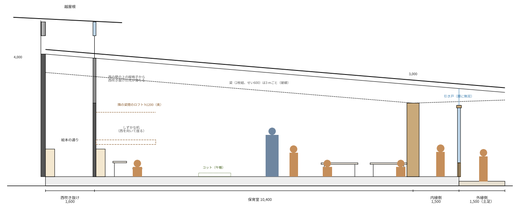

11:30
食べる

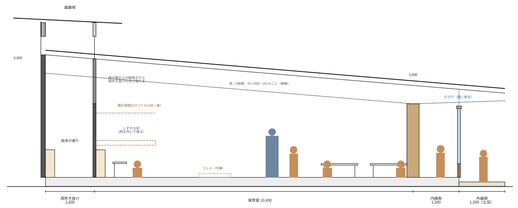

13:30
寝る

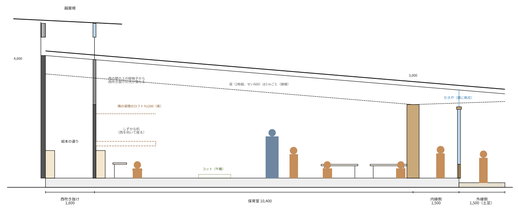

今は同じ図（既存の 1/50 を縮小）。時刻ごとに家具・人・光を描き分ける

遊戯室　平面・断面（縮小、遊戯室のチャット）

