こどもたちの育ち舎　1/5　敷地と自然環境

建築設計実習 II — I　2026.11.05　木田

地に足をつけて育つ

　比叡から降りる冷気と高野川の流れが出会う松ヶ崎の扇状地に、こどもたちが地に足をつけて育つ場所をつくる。ゆるやかな弧を東の比叡にひらく木造平屋の本館に0歳から5歳のすべての部屋を並べ、縁側と深い庇で園庭とつなぐ。比叡に見立てた築山と、用水を借りて高野川に見立てた小川を置く。

　オープンキッチンを玄関ホールに面する園の中心に据え、食べることを日々の求心力とする。野菜くずをこどもの手で土に還し、命の循環を知る。園庭には季節ごとに香る木と実のなる木を植え、こどもたちは手と鼻と舌で季節を知る。

　3 mスパンの木造架構によるスケルトン＆インフィルで用途の変化を受け止める。LEED v5 Gold相当を目指す。地域から様々なものを借り、無駄をせず巡らせて、こども園として地域に返す。

設計趣旨 約332字（課題は300字程度）。文字3.6 mmなら1 m離れて読める

自然環境と地域

借りぐらし　水と木を借りる

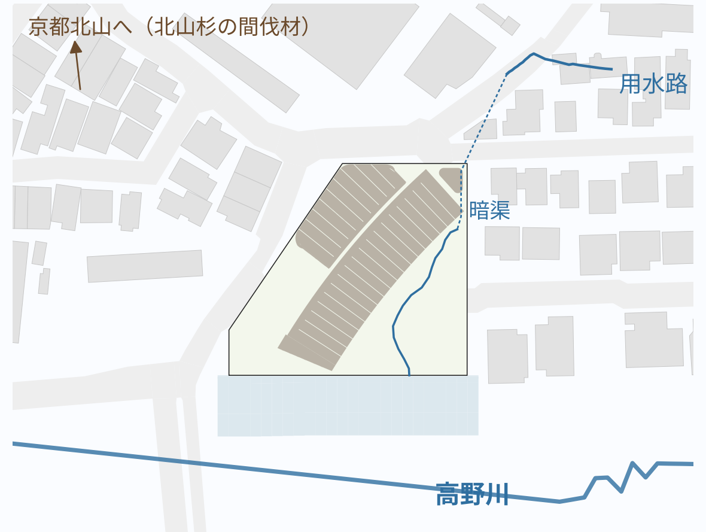

1/2000　松ヶ崎の用水から水を、北山から木を借りる
地下水の豊かな土地（物語）
（用水路と川は敷地図の線をなぞった、精度は数m）

山から川へ
小さな図＋
北のもりのみなもとから縁側の前・原っぱ
を流れ、護岸の溝を滑り落ちて高野川へ
築山＝比叡、小川＝高野川のうつし

河川敷とつなぐ
小さな図＋
のぞき（生垣の口から水面）
小川と雨の川が護岸の溝で河川敷へ
避難の帯・非常用の門から公園・河川敷へ

地域への配慮
小さな図＋
車は突き出た木より南（川側）で出入り
西館の西端は1階の高さ（向かいの住宅）
北東の隣家：1 m・木の帯・小屋が声の衝立
小竹薮公園を残す

配置図　1/200　高野川を下に（川向こうから見る向き、北は右上）

点線の枠＝園庭のチャットの配置1/200（garden01）を実寸で重ねた。本番は一枚に描き直す

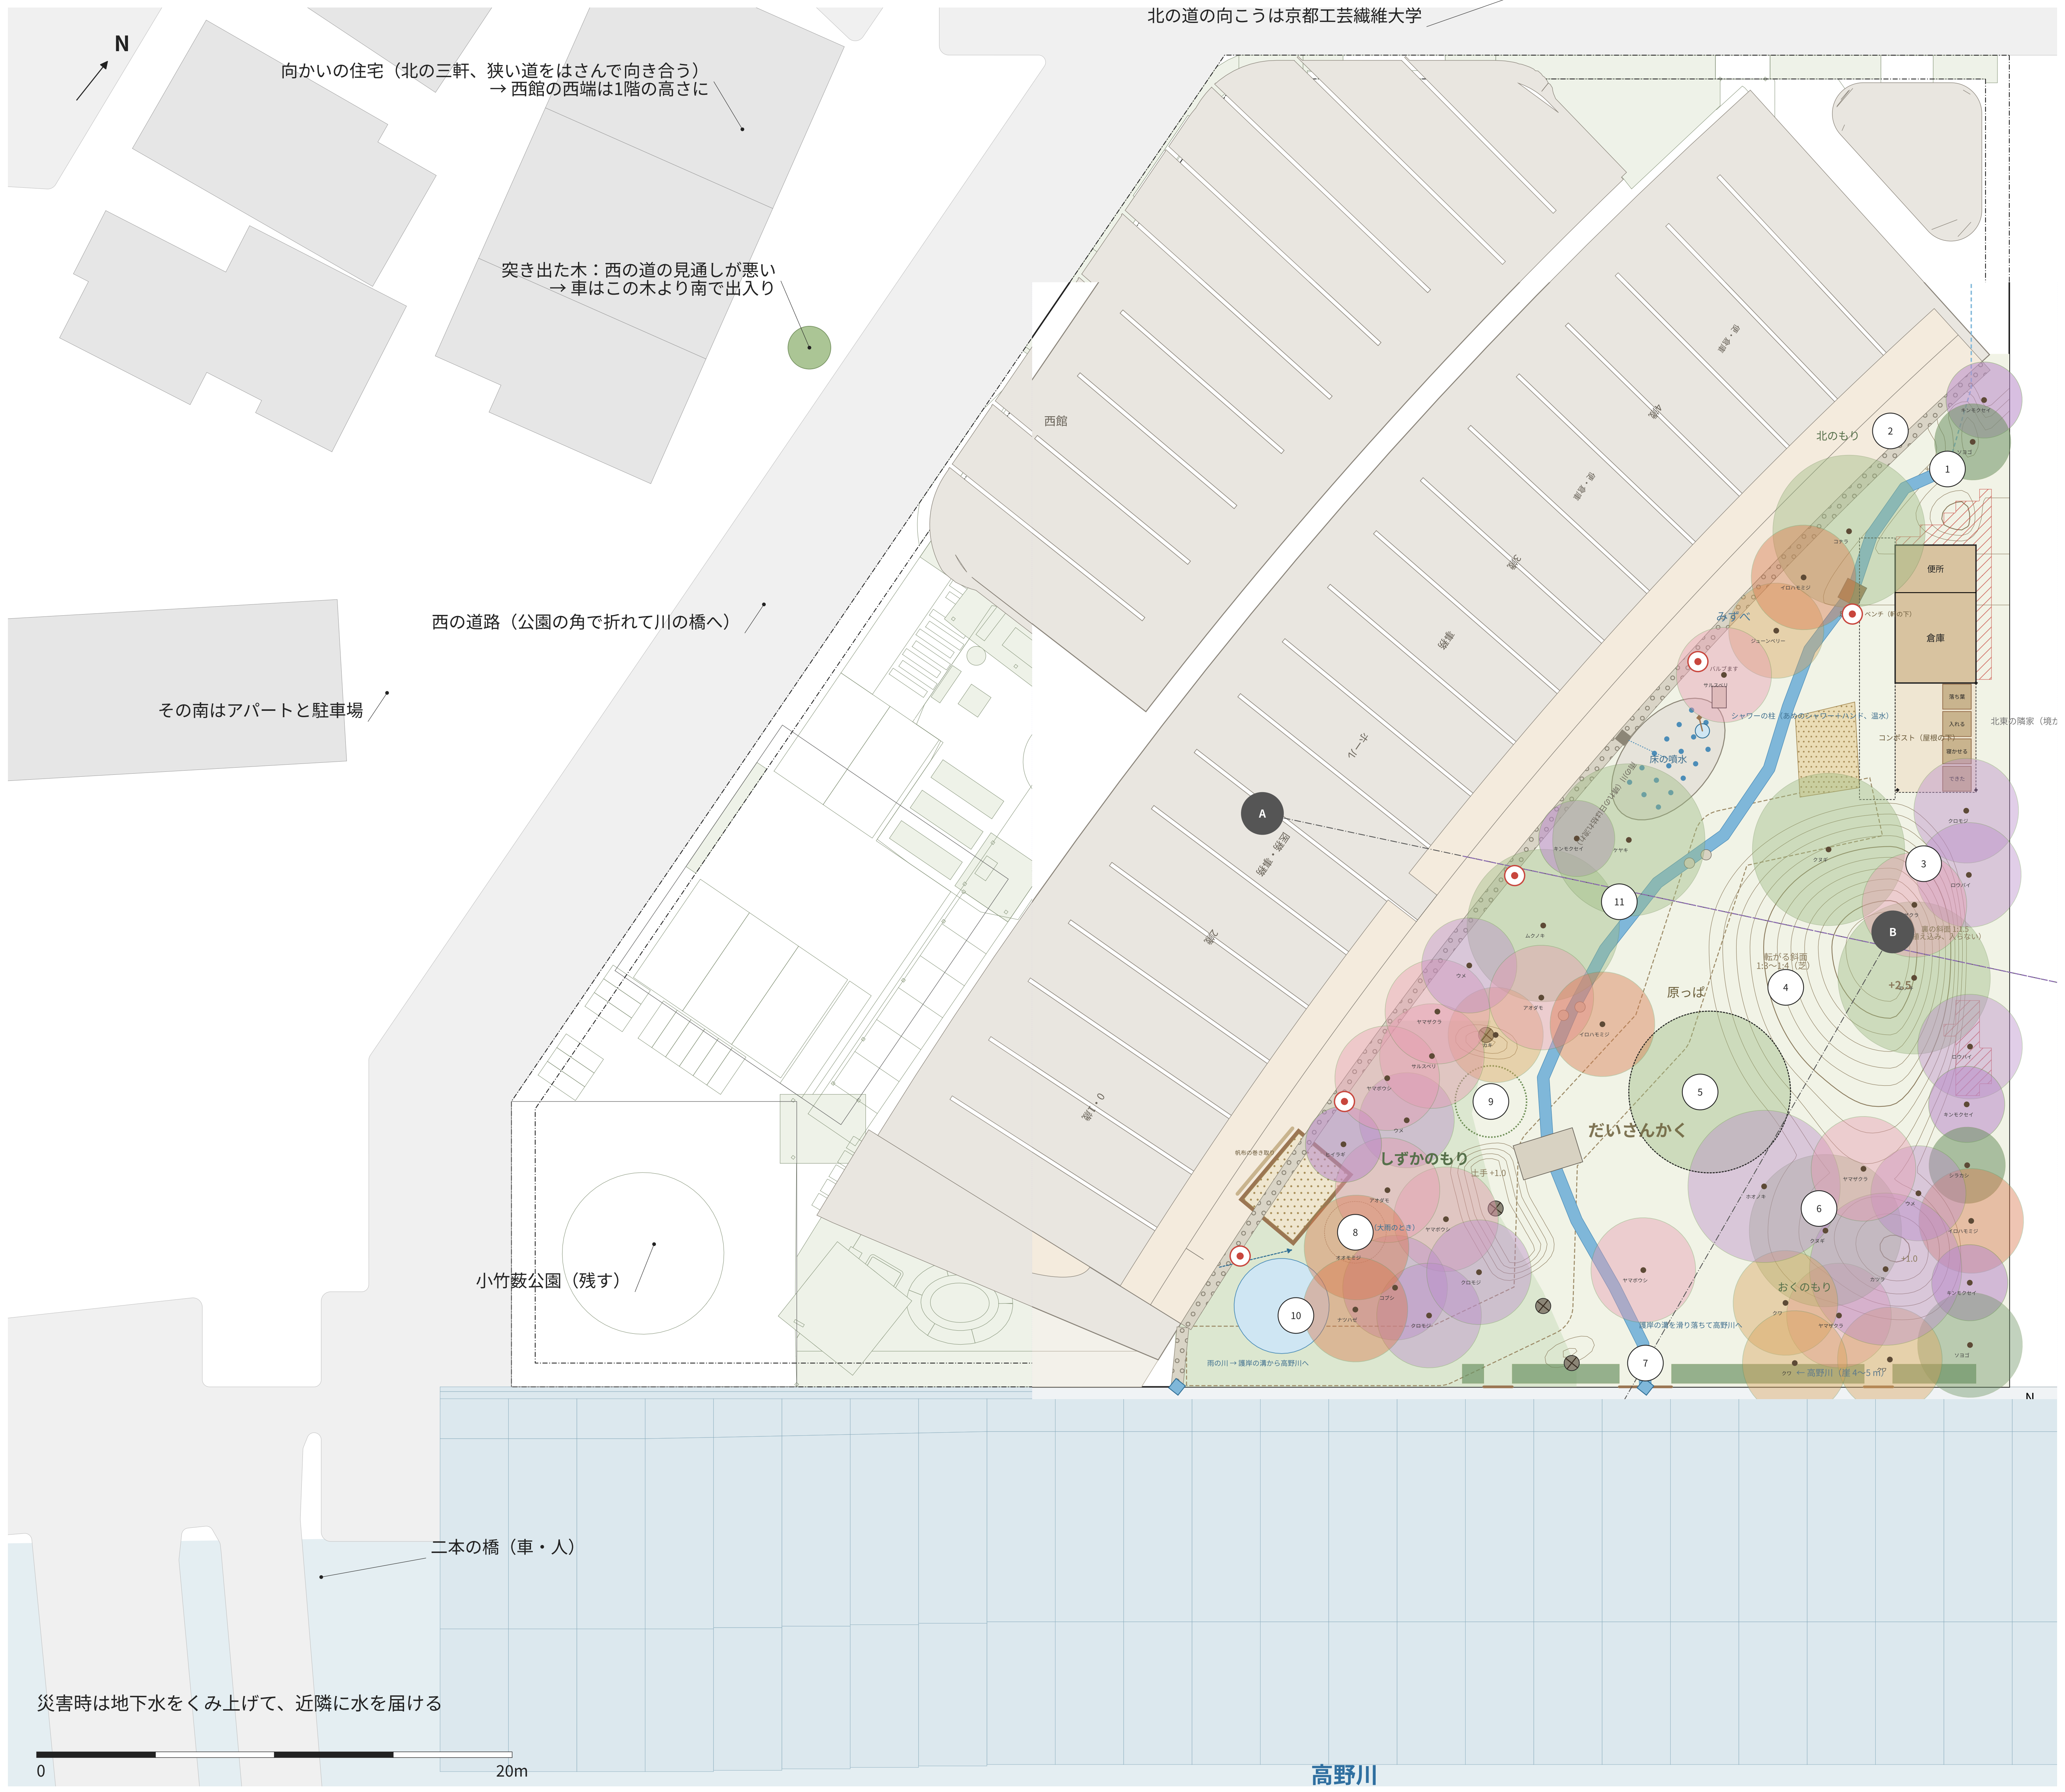

園庭　本物に触れて遊ぶ

見立て
小さな図＋
築山＝比叡、小川＝高野川
ホールから頂の向こうに比叡
足もとを掘った土で盛る

水の行方を隠さない
小さな図＋
用水→みなもと→小川
→護岸の溝→高野川
雨は樋なしで雨の川へ

土と世代のめぐり
小さな図＋
野菜くず→コンポスト
→菜園→給食、余りは農家へ
柳の家を上の子が編む

静かな場所と先生の目
小さな図＋
しずかのもり、ニッチ11か所
死角は植え込みだけ
取り除くのは命の危険だけ

模型写真　A4（入口の一枚）
園庭からこどもの目線（模型で約10 mm）
縁側・深い庇・築山の向こうに比叡の方向
選抜で最初に目に入る位置

園庭の断面　1/200　A 比叡へ／B 高野川・河川敷へ

死角：約 33 m²。築山の裏（隣家側）の植え込みと、北のもりの奥。植え込みは入らない所にする

断面 A–A　ホールから築山の頂を通って比叡山の向きへ　1/100

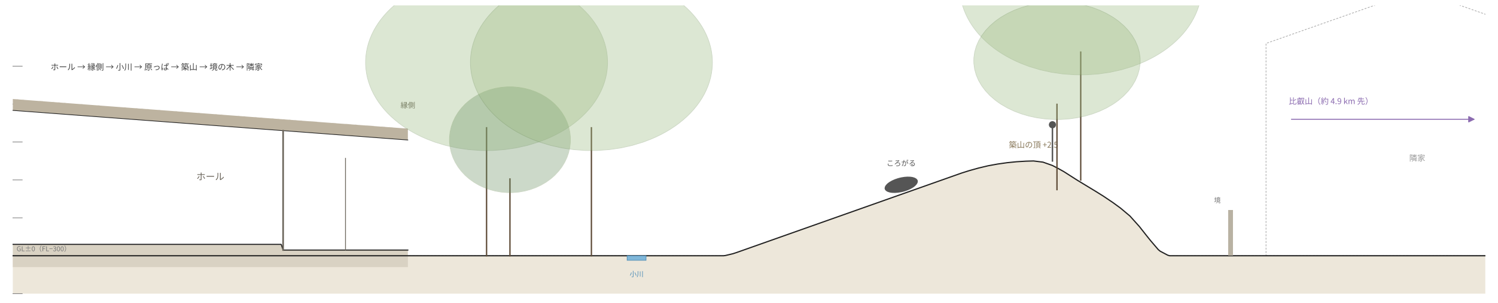

断面 B–B　築山から原っぱ・のぞき（生垣の口）を通って高野川へ　1/100（崖・河川敷の寸法は仮）

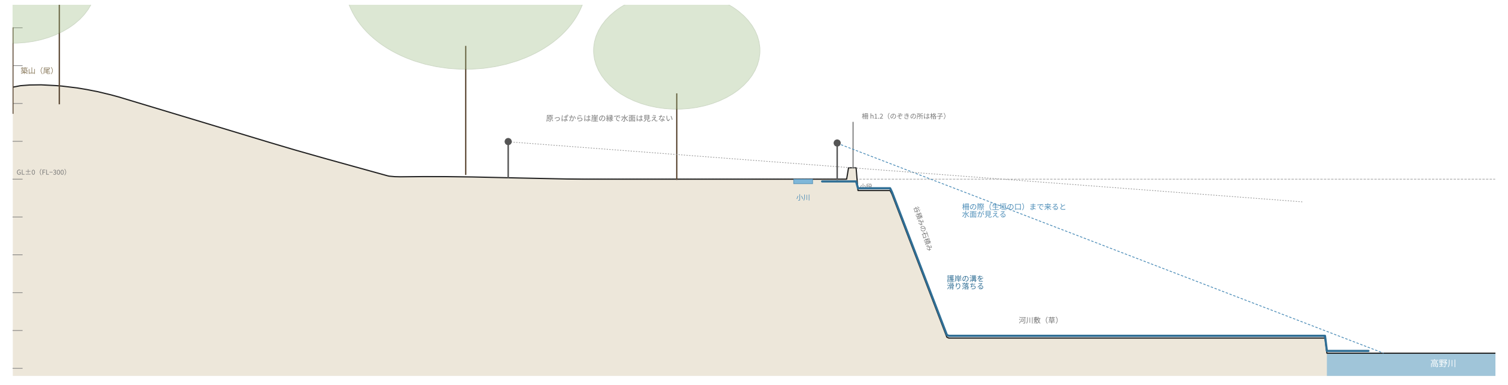
築山（尾）
GL±0（FL−300）
原っぱからは崖の縁で水面は見えない
柵 h1.2（のぞきの所は格子）
小川
柵の際（生垣の口）まで来ると
水面が見える
護岸の溝を
滑り落ちる
河川敷（草）
高野川

配置図の注

- 駐車5台・搬入は南（川側）。行事の日は駐車場を駐輪に
- セキュリティの線の出入口は公園の木戸だけ
- 園庭への搬入は公園の東の縁から川沿いの帯を通って
- 敷地の境から：北東の隣家1 m（厳守）、ほかは1 m

［割付の注記］フォーカス：周囲の自然環境との関係（用水・比叡と高野川のうつし・河川敷）と地域への配慮、屋外遊戯場としての園庭　／　目に入る順：模型写真（入口の一枚）→ タイトルと趣旨 → 配置図と園庭 → 園庭の筋 → 自然環境と地域

こどもたちの育ち舎　2/5　すべての人の一日　1階平面

建築設計実習 II ― I　2026.11.05　木田

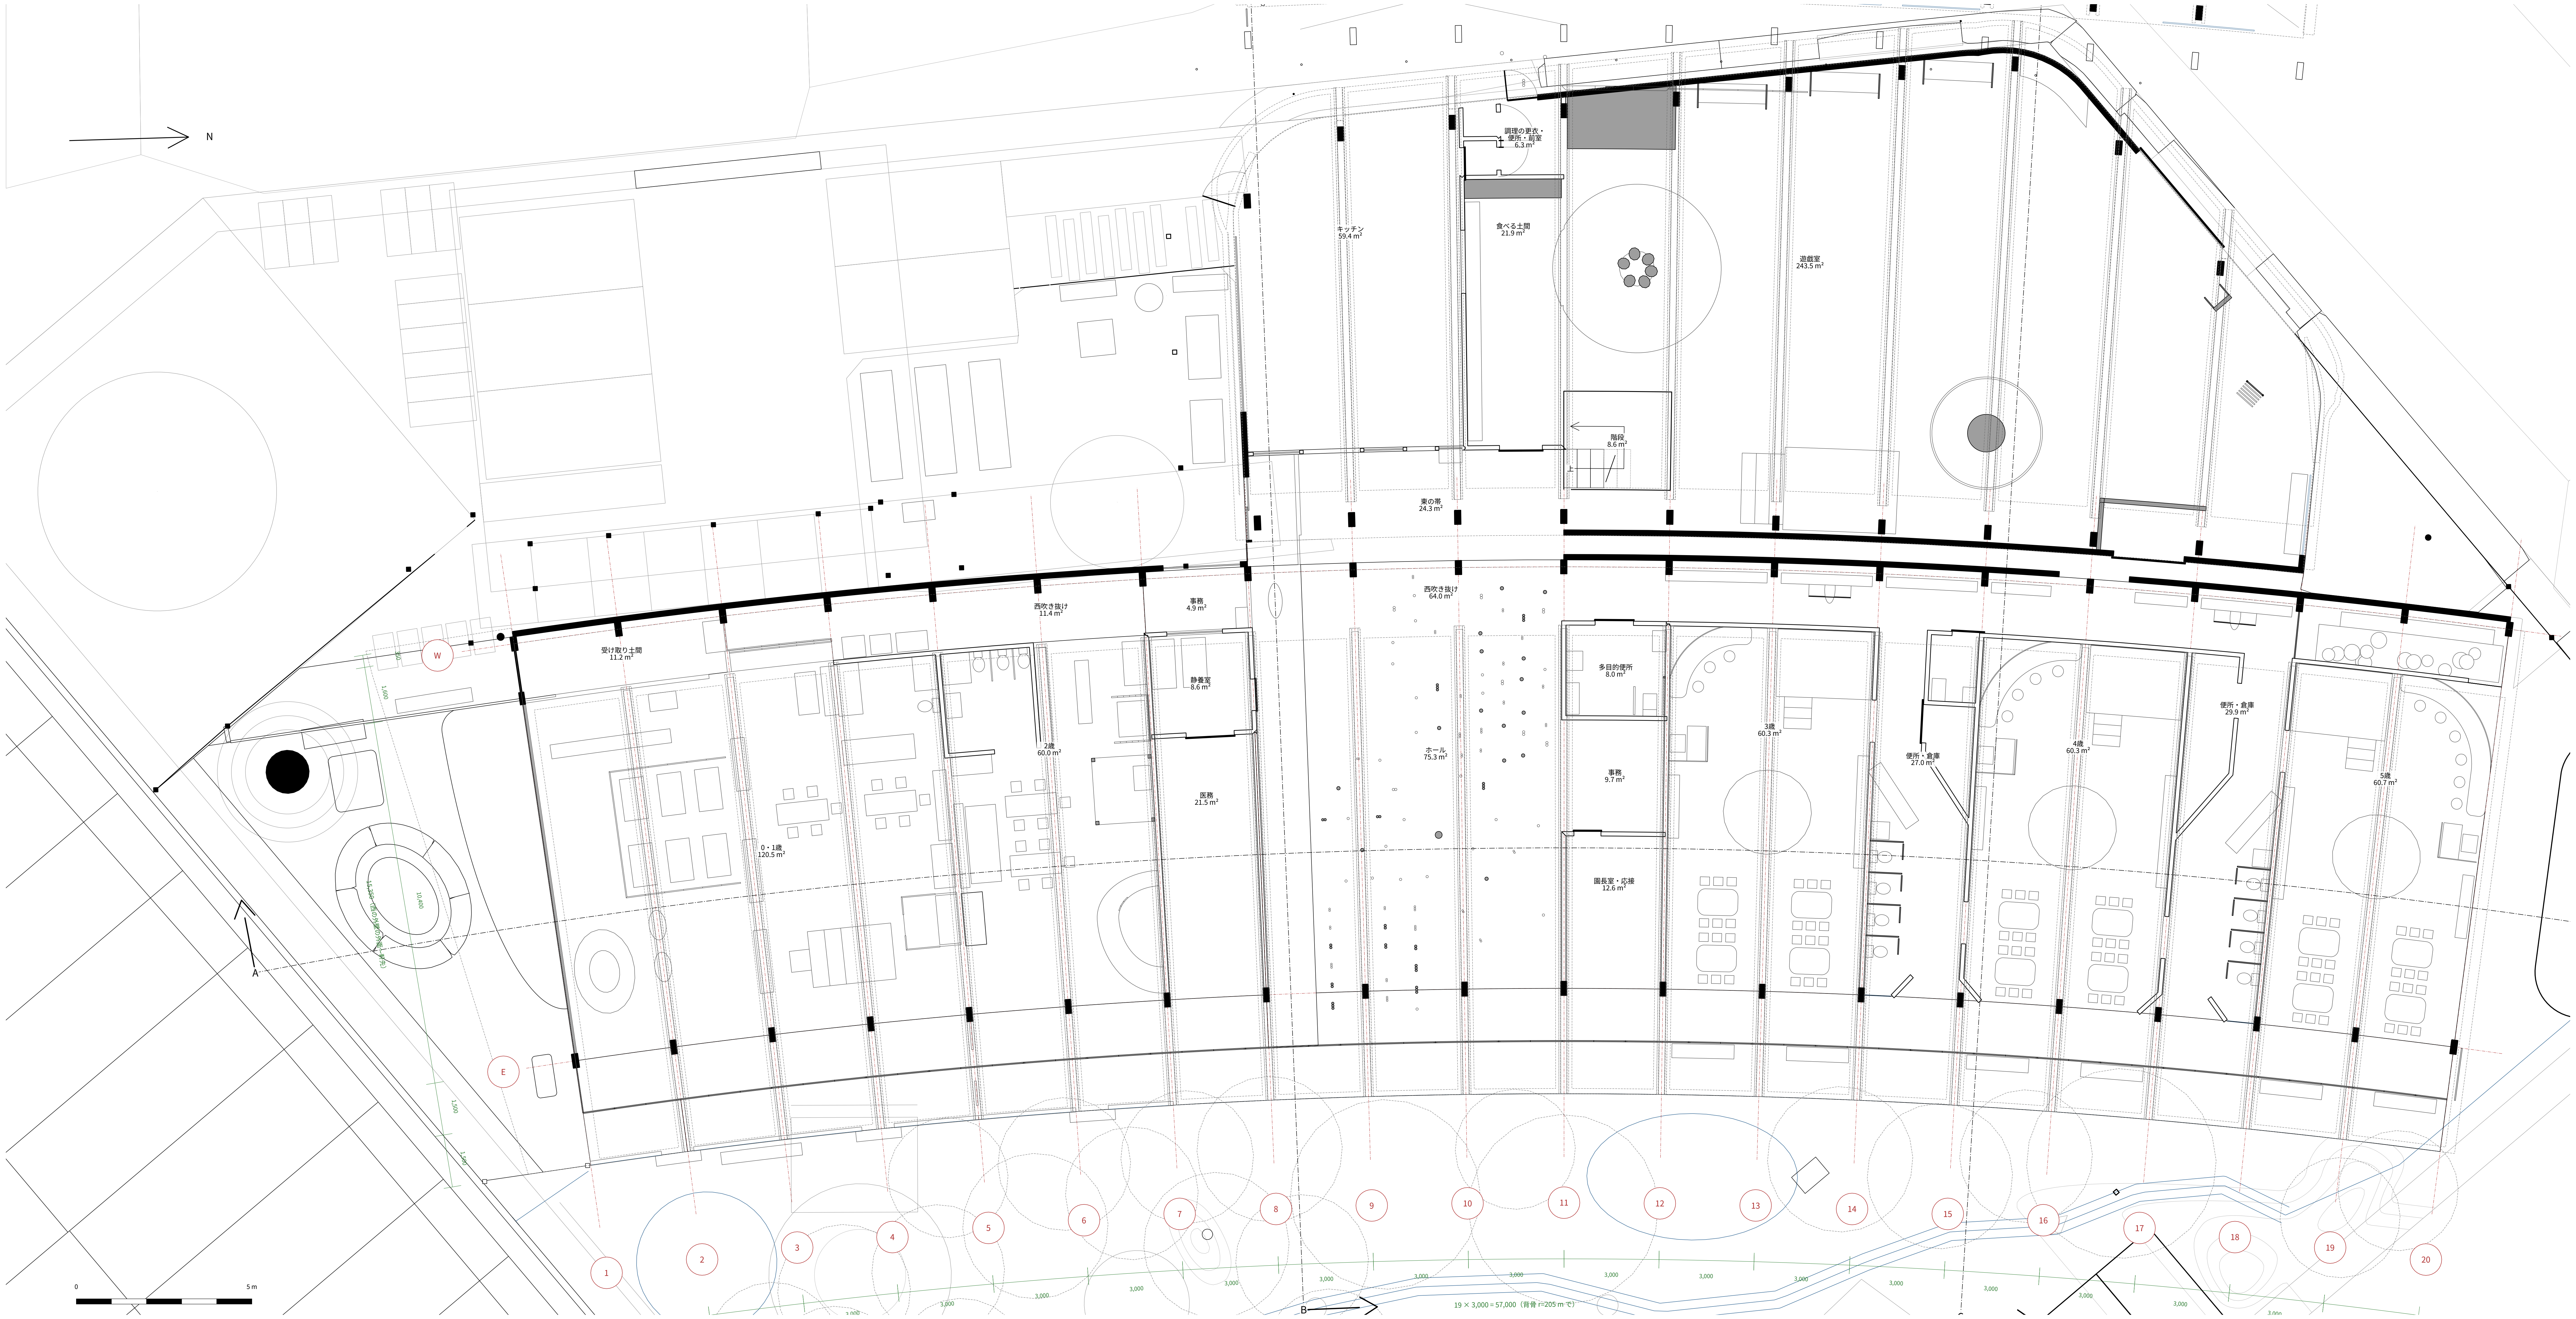

3dmから自動の平面図
（1/100、実寸）

描き足す注記：
・各保育室の先生の席
（机h700＋ついたて）
・0・1歳の腰掛ける机
・記録・連絡の机
・オープンキッチンの
東面のガラス
・生ごみの受け取り台
・はれのま
・2階の休憩室は4枚目

一日の帯：上は1/700の小さな配置（建物＋園庭）、下にこども・保育士・調理の三つの一日

登園 8:00

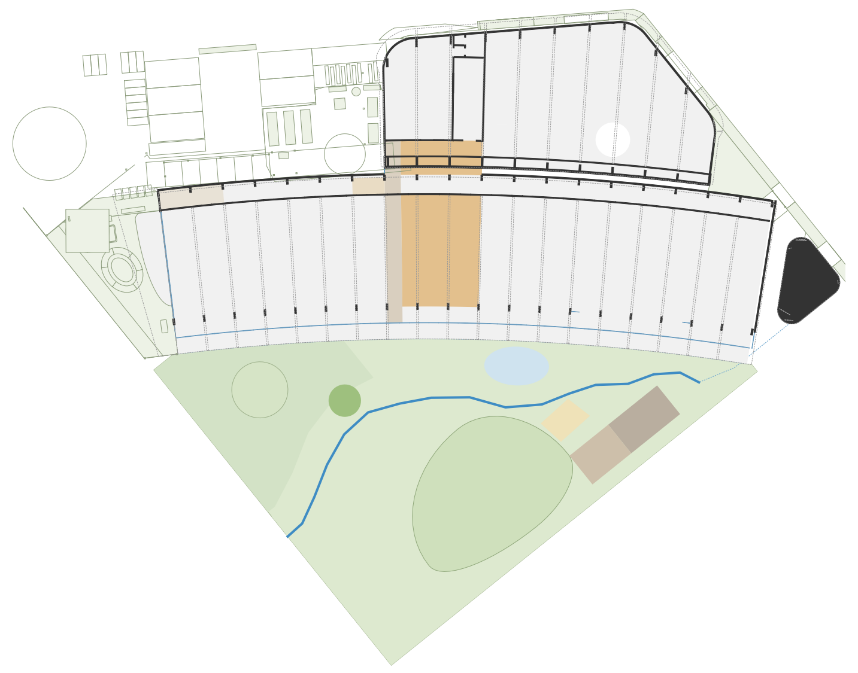

こども公園→木戸→小径→海峡。0・1歳は受け取り土間

保育士おはようの窓口で挨拶、受け取り土間で手渡し

調理　検収と下処理（南のガラス越しに見える）

外で遊ぶ 9:30

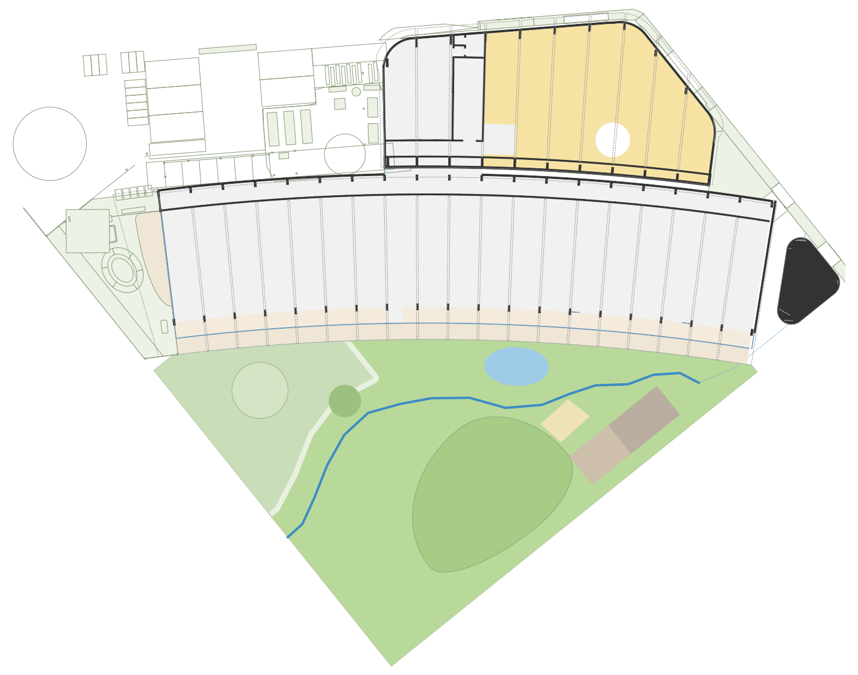

こども3〜5歳はだいさんかく、0〜2歳はしずかのもり

保育士縁側の縁に腰掛けて庭全体を見る

調理　仕込み。今日のごはんの窓にこどもが寄る

食べる 11:30

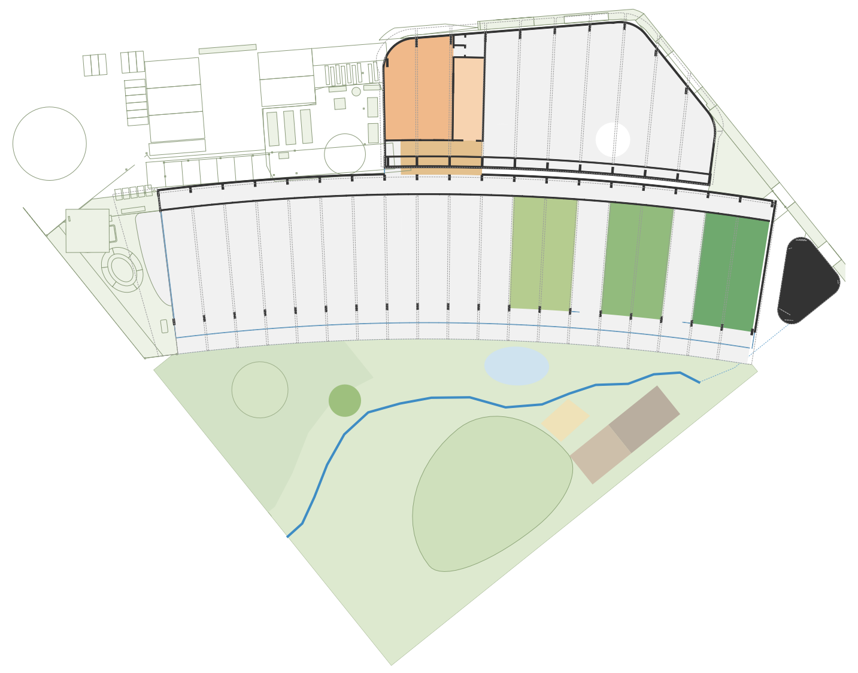

こども保育室の食卓、はれのまでクラスごと

保育士配膳口から飛び石を渡って配る。いっしょに座って食べる

調理　オープンキッチンでこどもと目が合う

寝る 12:45

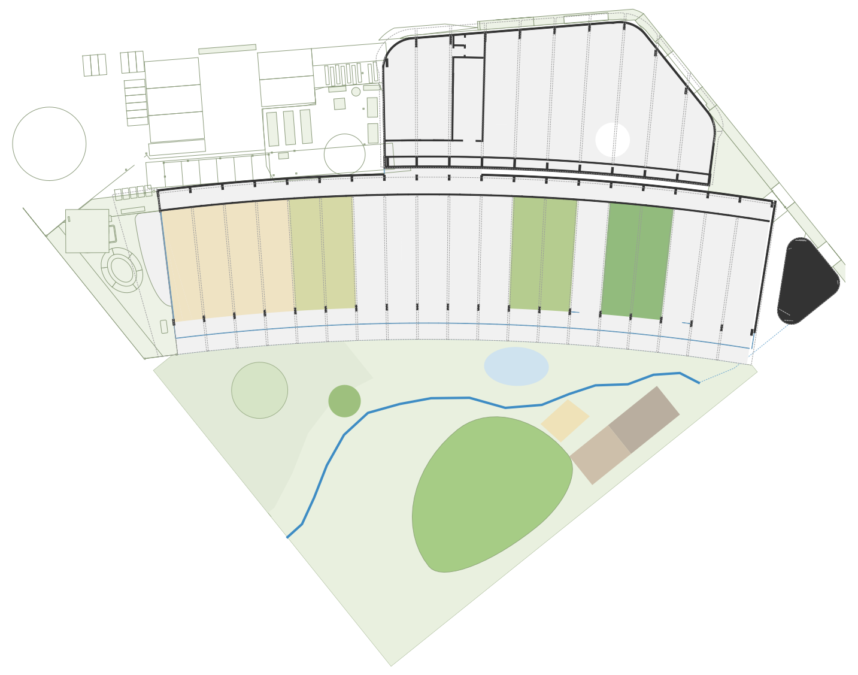

こどもねどこ・ロフトの下。起きている5歳は北の築山と遊戯室

保育士交代で2階の休憩室へ（こどもから離れる）、記録の机

調理　片付けと洗浄、おやつの仕込み

当番 15:00

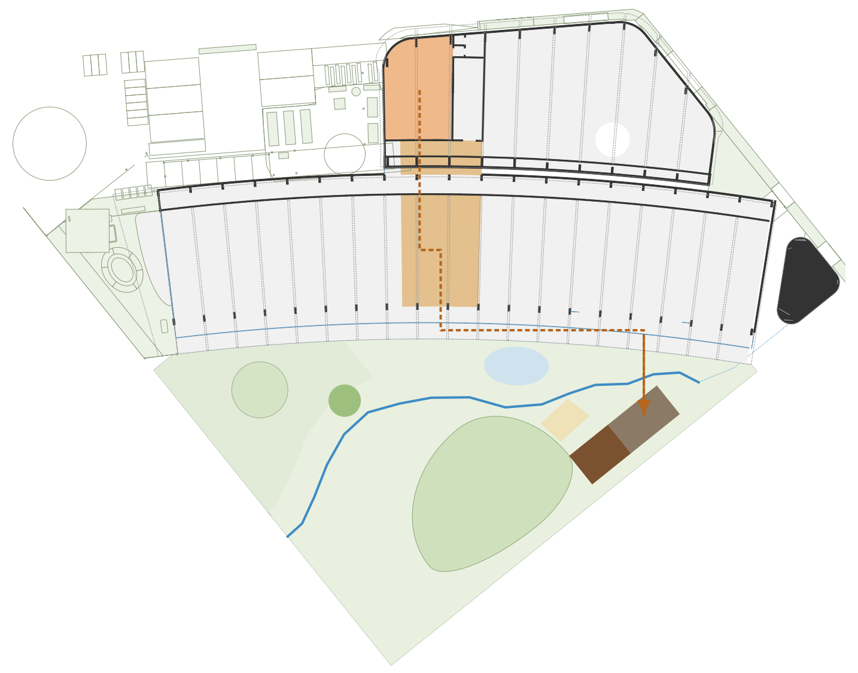

こども4・5歳のコンポスト当番：キッチン→小屋

保育士当番に付き添い、できた土を菜園へ

調理　受け取り台で野菜くずを渡す、はれのまでおやつ

降園 16:30

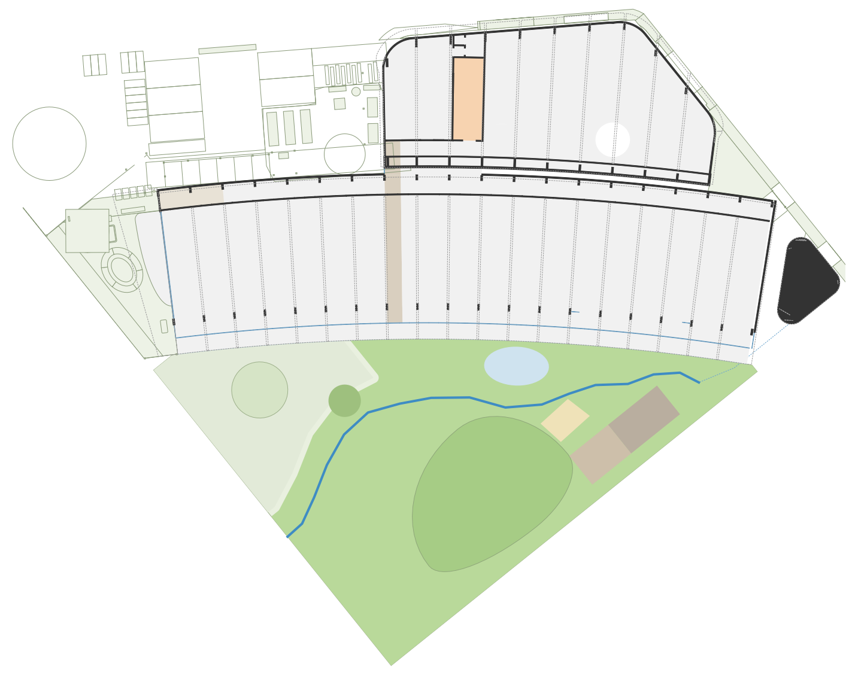

こどもはれのまで延長保育、迎えを待つ夕方の園庭

保育士縁台でお茶をしながら保護者と話す、2階で会議

調理　職員の通用口から帰る

［割付の注記］フォーカス：こども・保育士・調理の職員が一日を過ごす場所としての平面（食べる・寝る・遊ぶ）　／　目に入る順：1階平面（家具・先生の席）→ 一日の帯（こども／保育士／調理）

こどもたちの育ち舎　3/5　景観

建築設計実習 II — I　2026.11.05　木田

園庭の側の立面図 1/100　円弧の中心の方向から弧の真ん中に正対

伸びやかな梁と縁側（梁の端・庇が3 mごとに並ぶ）。屋根は屋根材型の太陽光

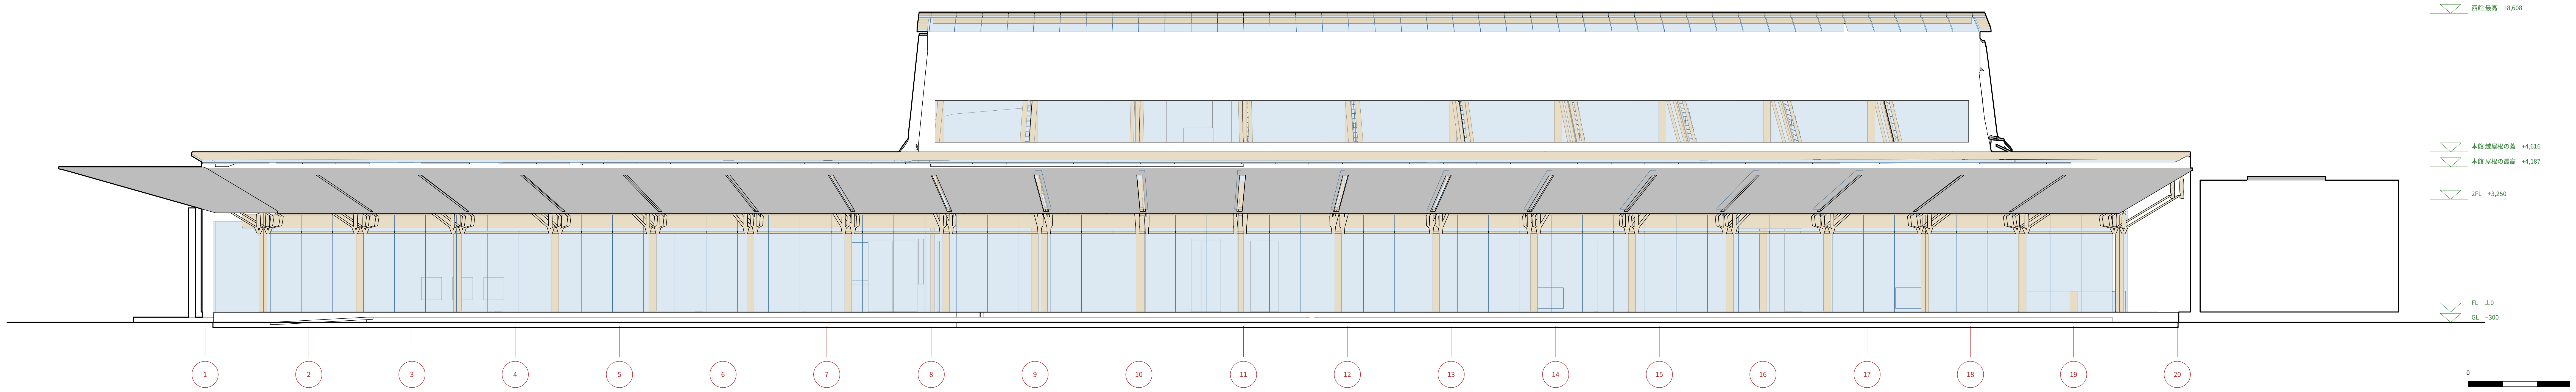

縦断面図A 1/100　保育室の中ほどの弧で切って展開、西を見る（左が南の高野川）

左（南）の高野川の崖から右（北）の大学へ、低い本館 → 高い西館 → おむすび。地域の建物の高低の流れに沿う

道路の側の立面図 1/100　西の道路から

西館の西端は1階の高さ（向かいの住宅を点線で描き足す）。西館の立ち上がりが北で主張する

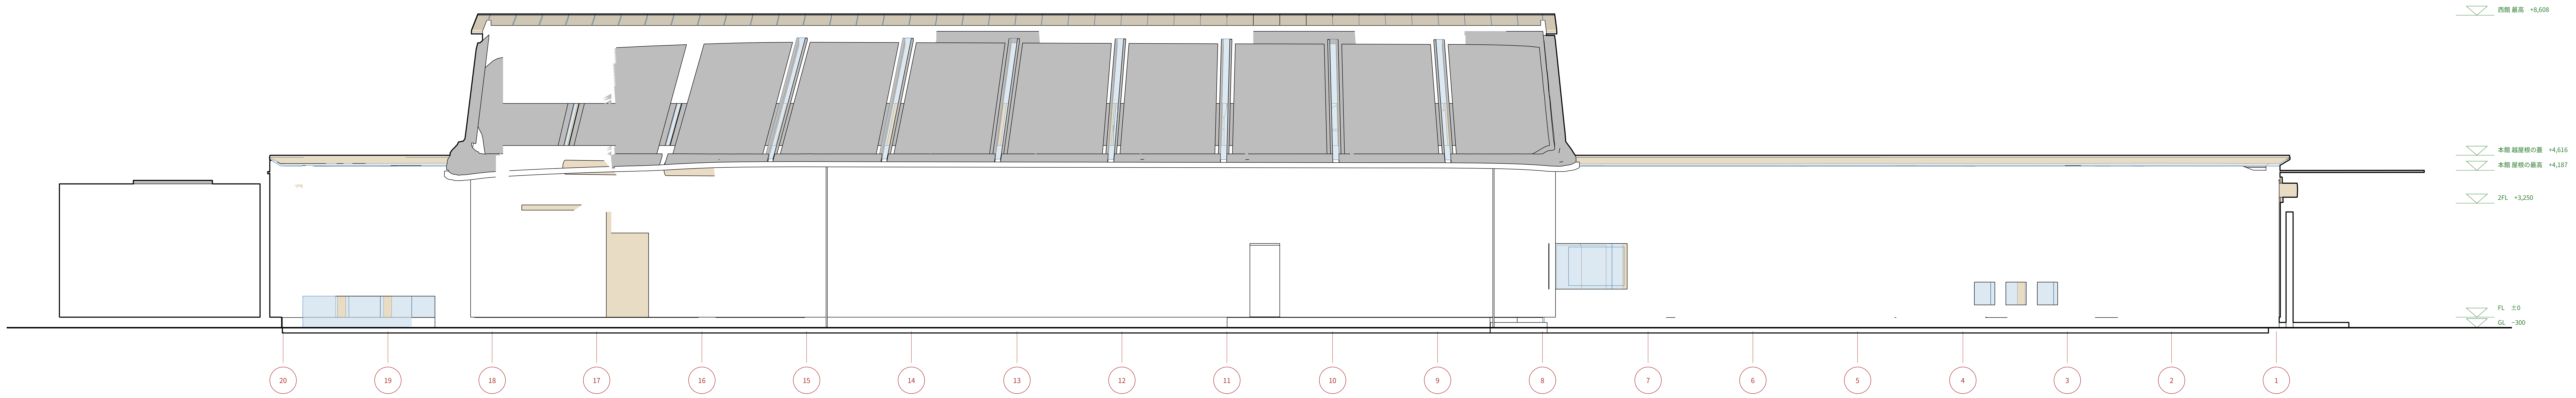

夜の立面（園庭の側）
黒地に越屋根の東の縁の光の線だけ
水平の光が一本、川向こうから見える
（模型の夜景写真でもよい）

模型写真　鳥瞰
敷地と高野川・崖・公園・西の道・園庭
配置図と同じ向き（高野川を手前）
川側が低く北へ高くなる流れが見える角度で

高野川の側の立面図 1/200　川の向こうから

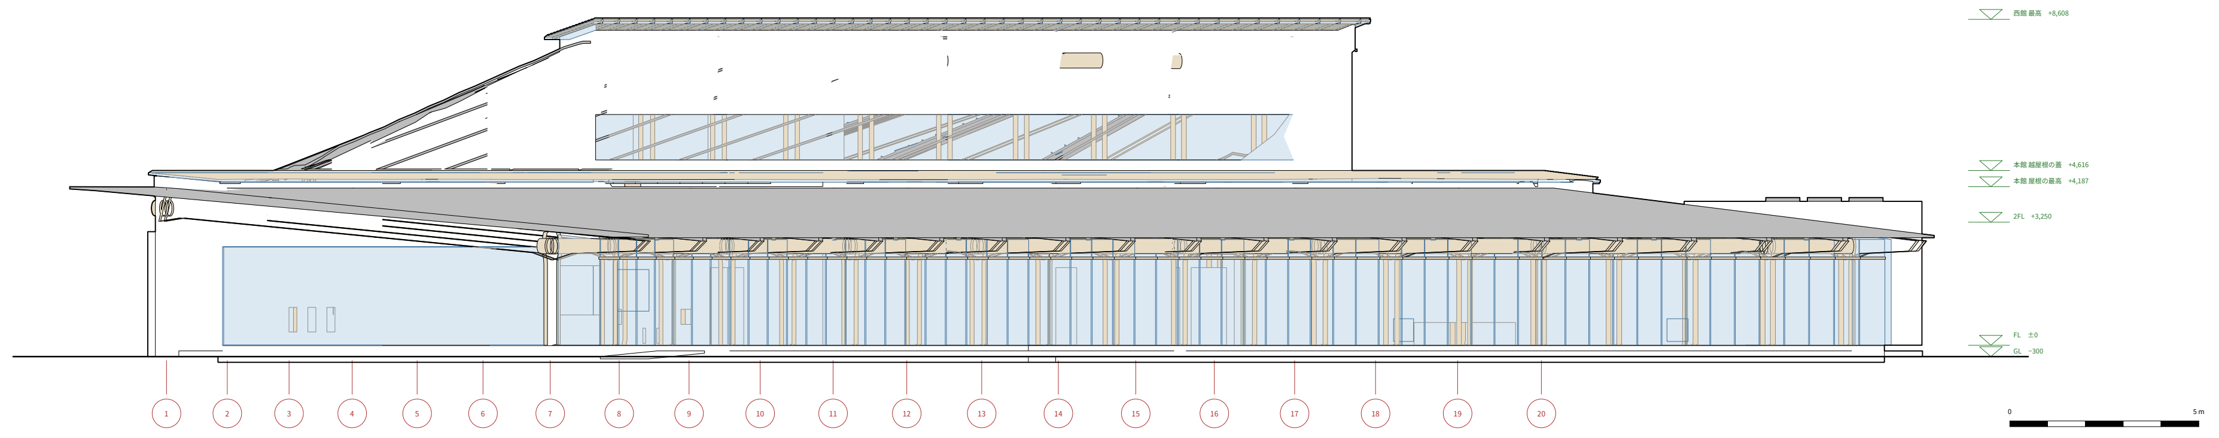

［割付の注記］フォーカス：高野川の側は低く、北の大学に向かって高く（地域の高低差の流れ）。同時に、伸びやかな梁・西館の立ち上がり・夜の水平の光で主張する　／　目に入る順：園庭の側の立面 → 縦断A（川から北へ）→ 道路の側の立面 → 高野川の側・夜

こどもたちの育ち舎　4/5　環境

建築設計実習 II — I　2026.11.05　木田

断面図C　4歳・遊戯室の摺鉢ネット

1/50（1/100の自動の図を2倍）　西の道路から園庭へ

矢印：昼の道（青）と夏の夜の道（紺）。床下の底板t200と断熱の帯。光の筋の光

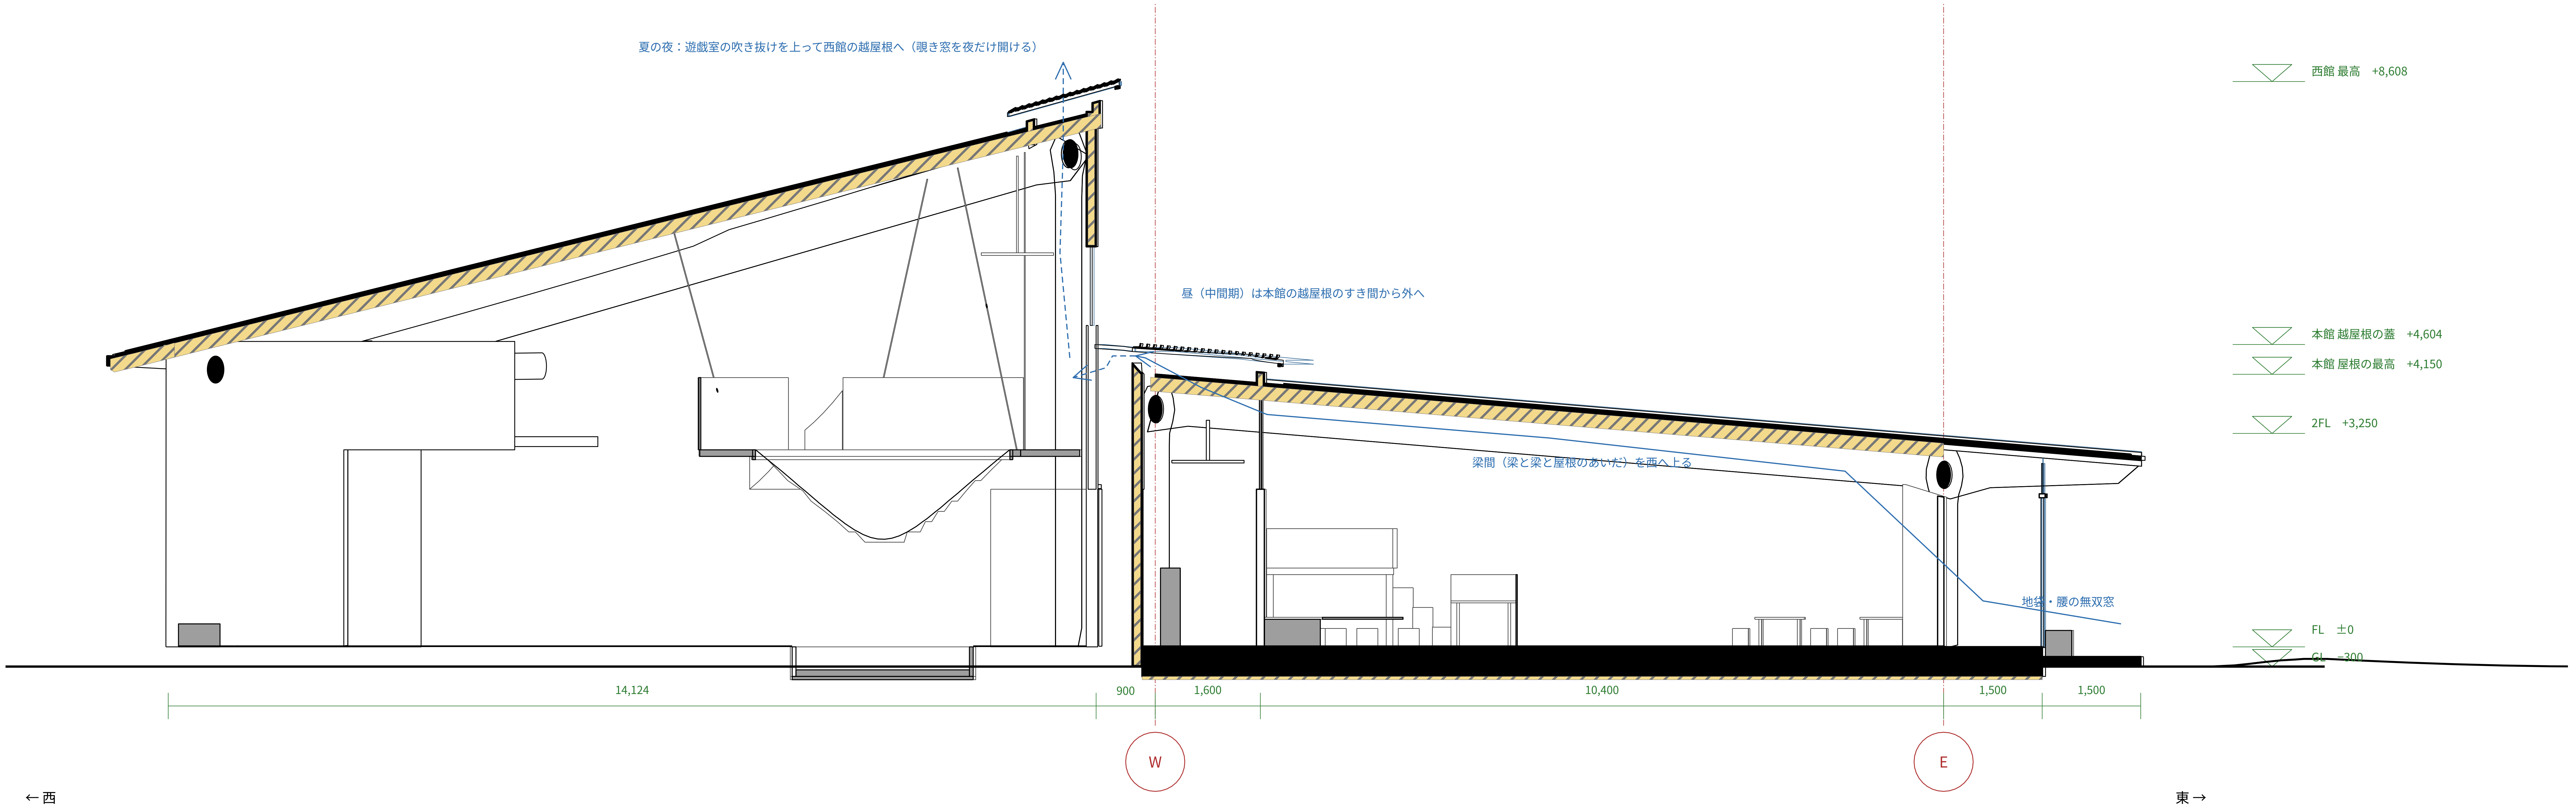

夏の夜：遊戯室の吹き抜けを上って西館の越屋根へ（覗き窓を夜だけ開ける）
昼（中間期）は本館の越屋根のすき間から外へ
梁間（梁と梁と屋根のあいだ）を西へ上る
地袋・腰の無双窓
西館 最高　+8,608
本館 越屋根の蓋　+4,604
本館 屋根の最高　+4,150
2FL　+3,250
FL　±0
GL　−300
14,124
900
1,600
10,400
1,500
1,500
W
E
←西
東→

運転表

夏の昼
庇で遮る・天井扇
床下空調（底板の冷え）

夏の夜
縁側の段のガラリ→床下→梁間
→越屋根・遊戯室の吹き抜け

春・秋
越屋根の換気口を開ける
縁側を開け放す

冬
換気口を閉じる・熱交換
基礎断熱・屋根の断熱

環境への配慮（LEED v5 Gold相当を目指す）

パッシブ
床下に冷えをためる
越屋根の通風、光の筋の昼光

エネルギー
屋根材型の太陽光
蓄電池（災害時の拠点）

資源
北山杉の間伐材（山の手入れを支える）
地域のスギ、土・雨・生ごみを敷地で回す

時間
スケルトン＆インフィル
水まわりはどのスパンにも

西館2階＝職員の側（休憩室・ぐったり休憩・会議室・更衣）。こどもから離れて休む

西館2階平面図

1/100　職員の側

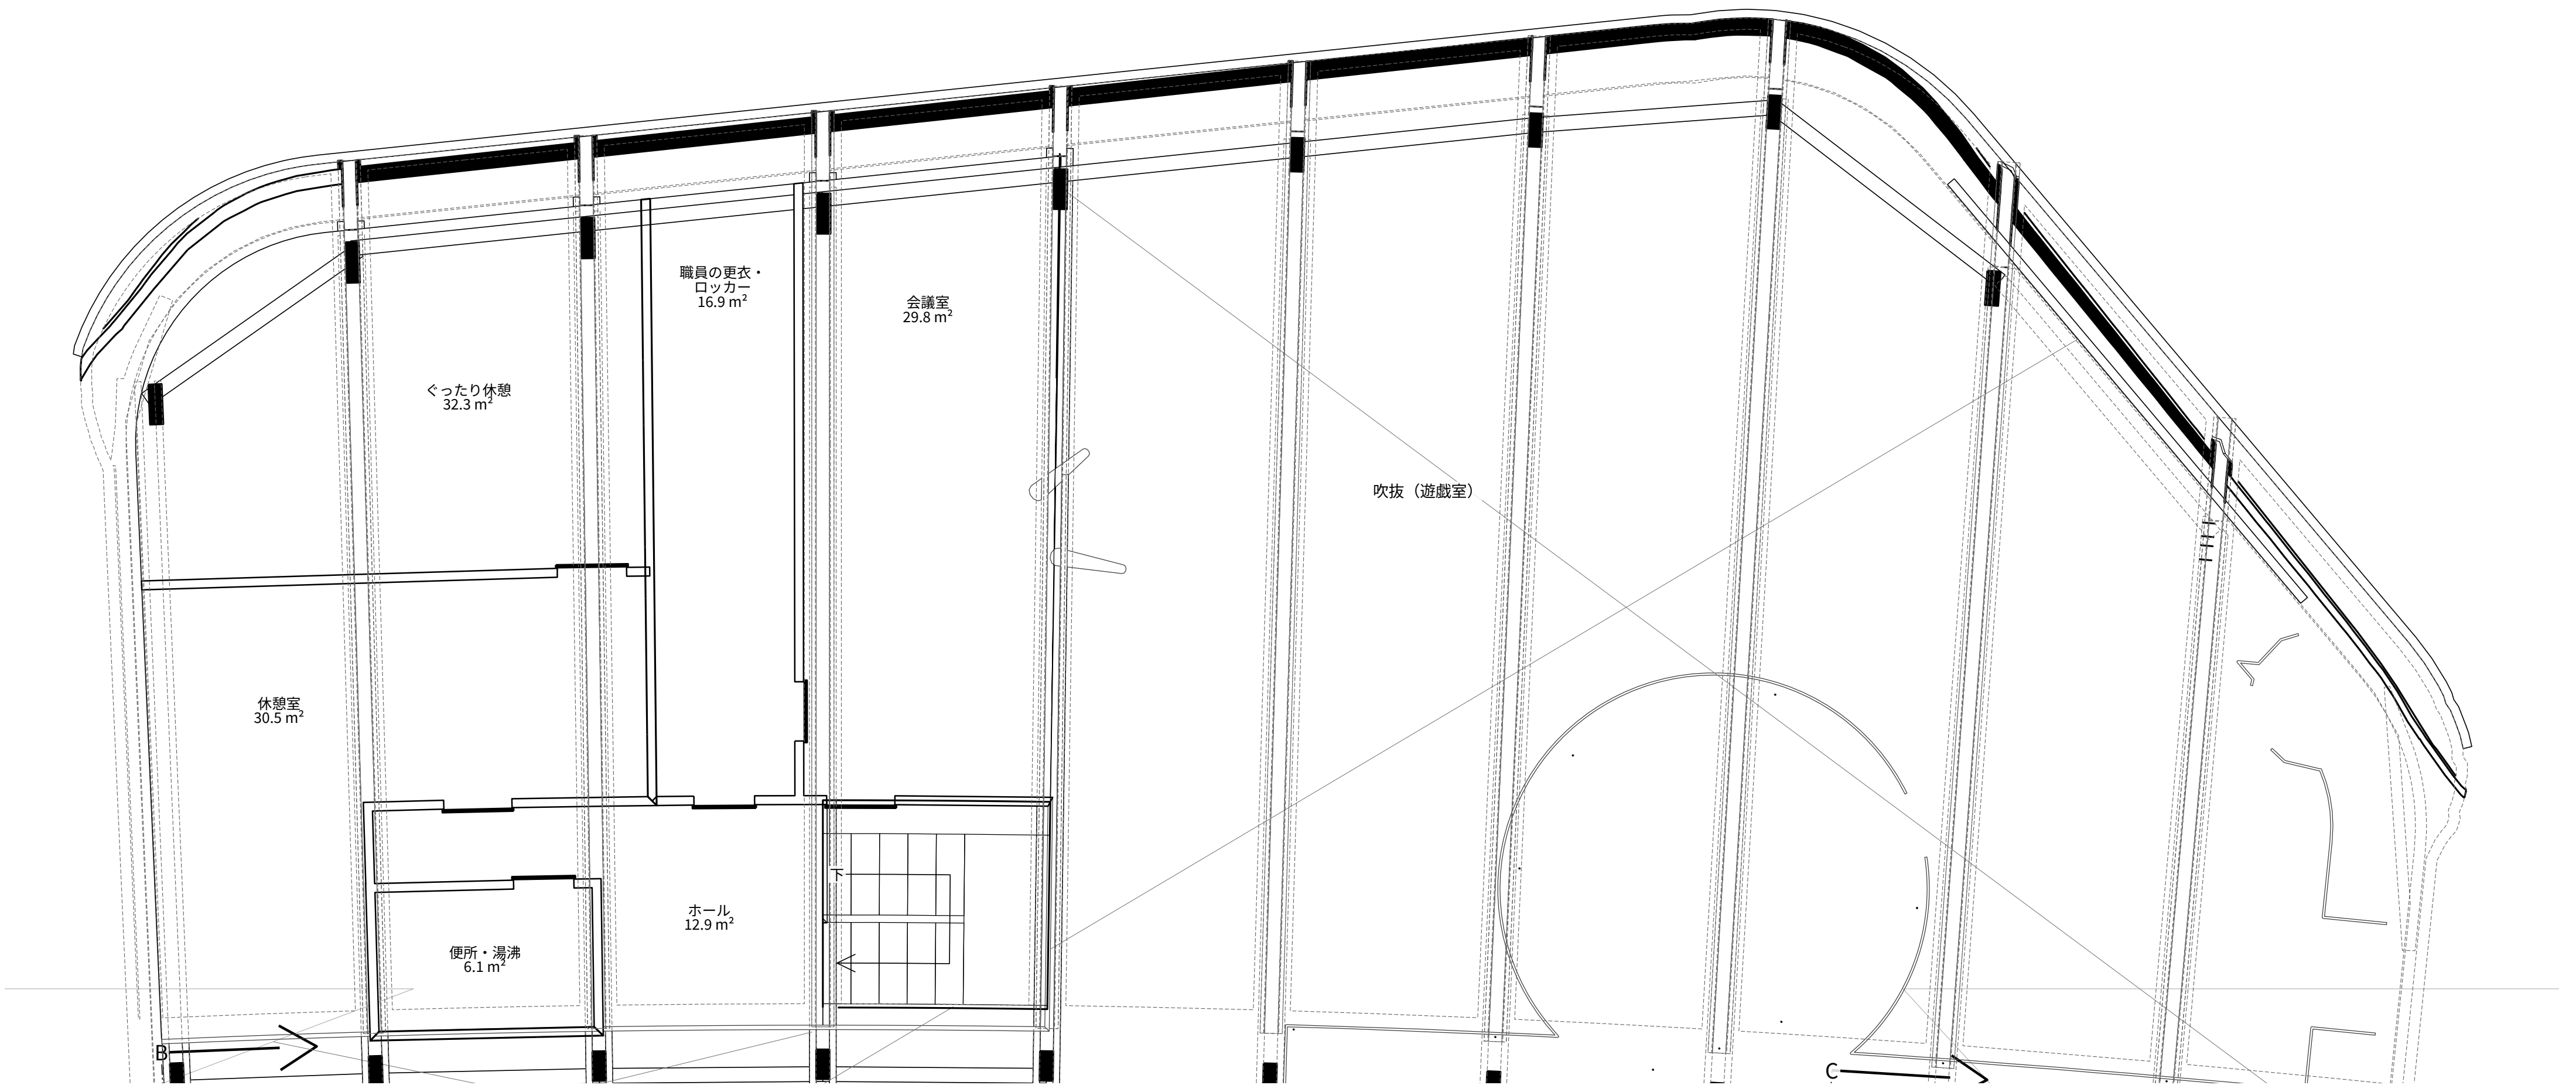

断面図B　海峡

1/100　南の入口・キッチン・2階・すき間・本館・縁側

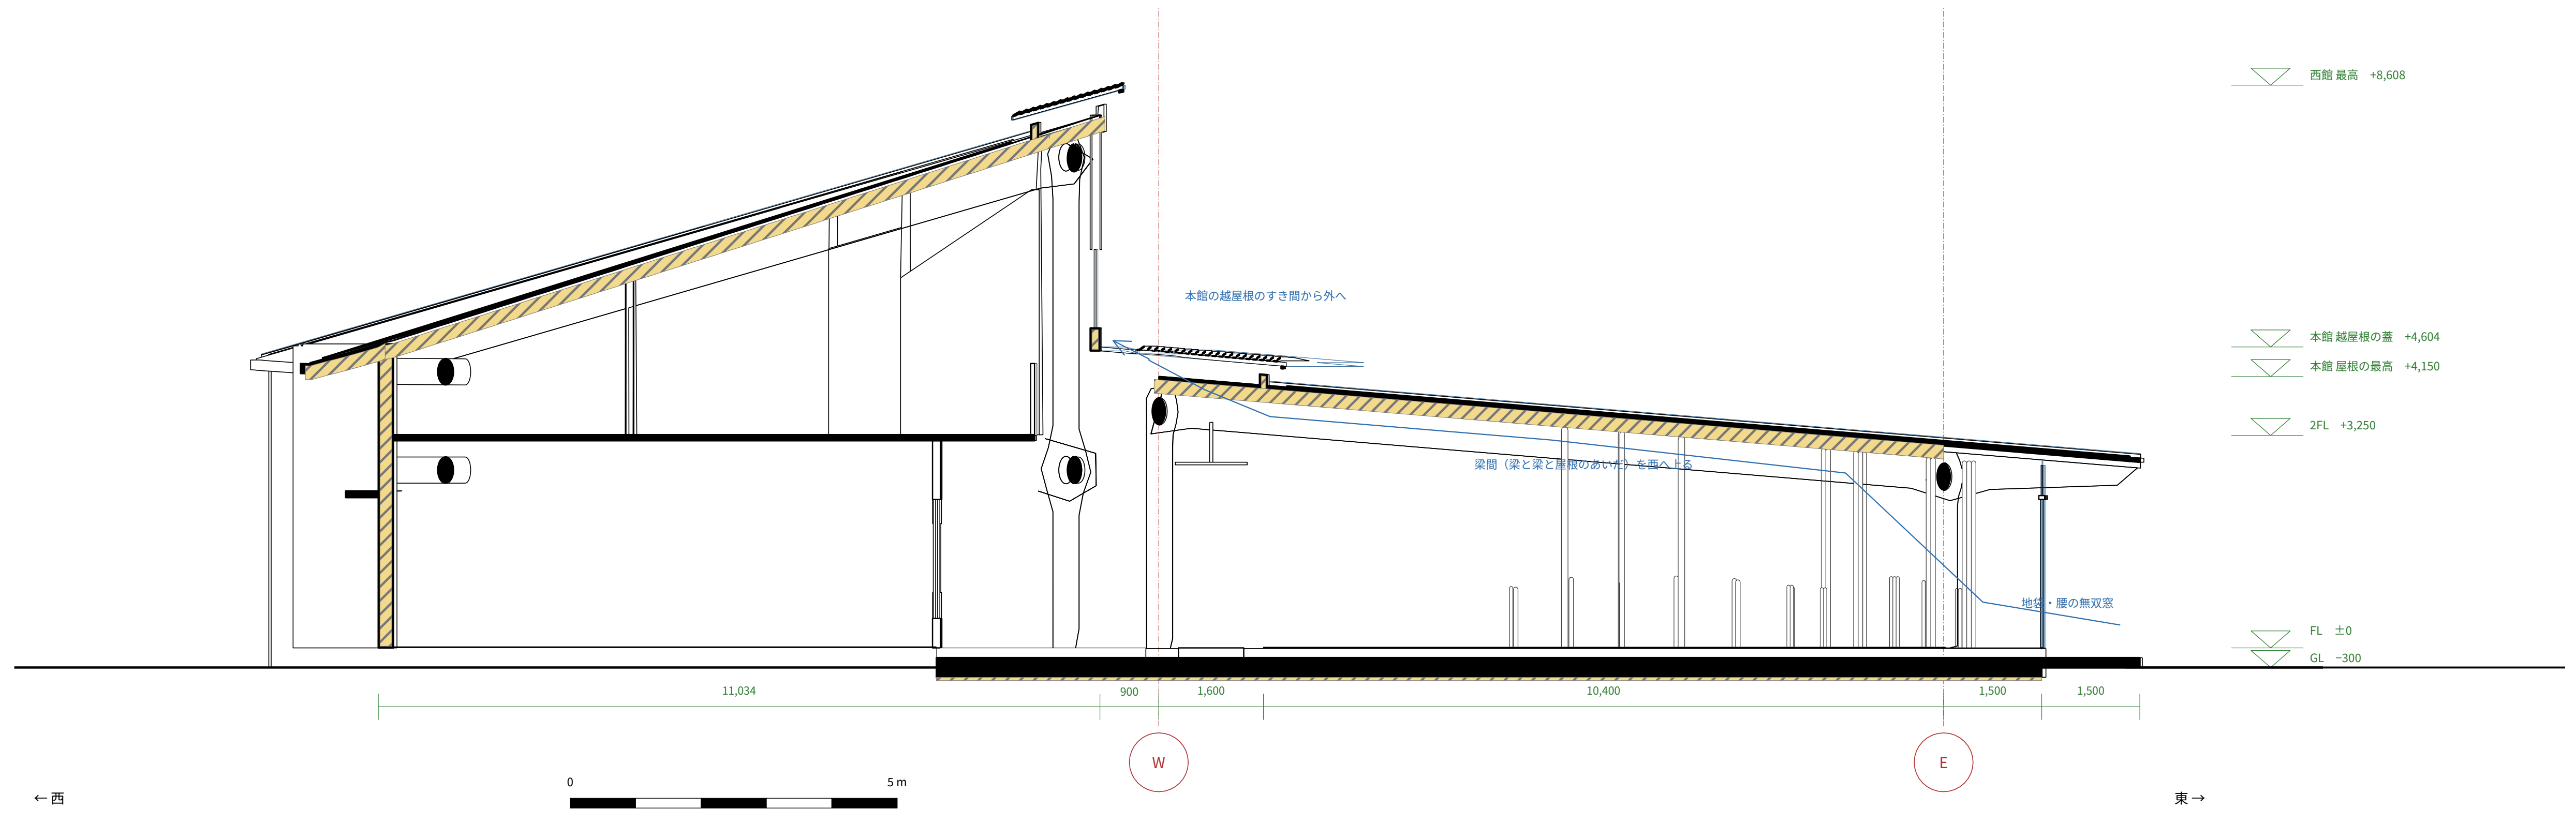

［割付の注記］フォーカス：木造・パッシブ（床下・越屋根・光の筋）で空調を補う。エネルギー・資源・時間（S&I）まで　／　目に入る順：断面C 1/50（昼と夏の夜の風、光の筋、床下）→ 運転表と4つの配慮 → 断面B → 2階（職員の側）

こどもたちの育ち舎　5/5　こどもたちへの環境

建築設計実習 II — I　2026.11.05　木田

内観　ホール（A4）
北山杉の林・海峡と飛び石・オープンキッチン
梁の見える天井・光の筋・越屋根の光の線
（レンダリングか模型写真）

同じ部屋の一日　3〜5歳の保育室　断面

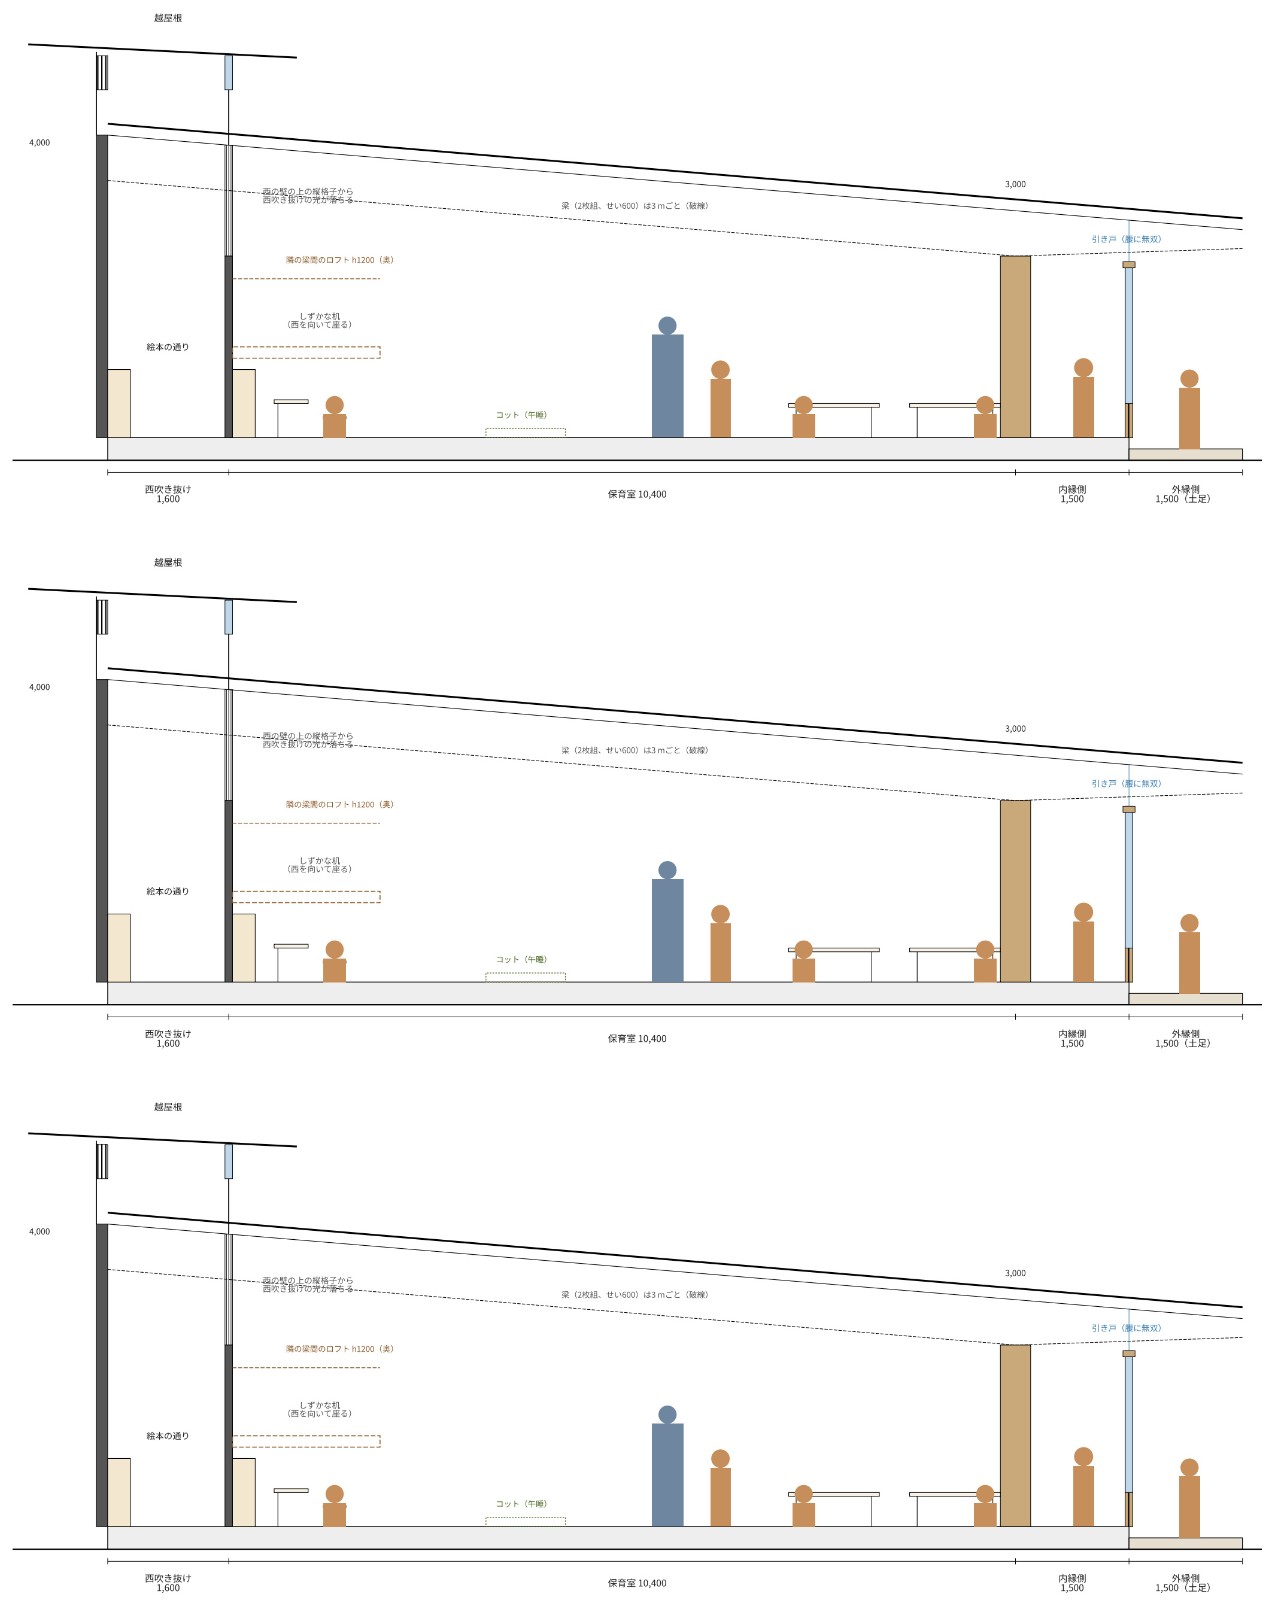
10:00
遊ぶ

11:30
食べる

13:30
寝る

今は同じ図。部屋の分け方と天井の高低が決まったら描き分ける

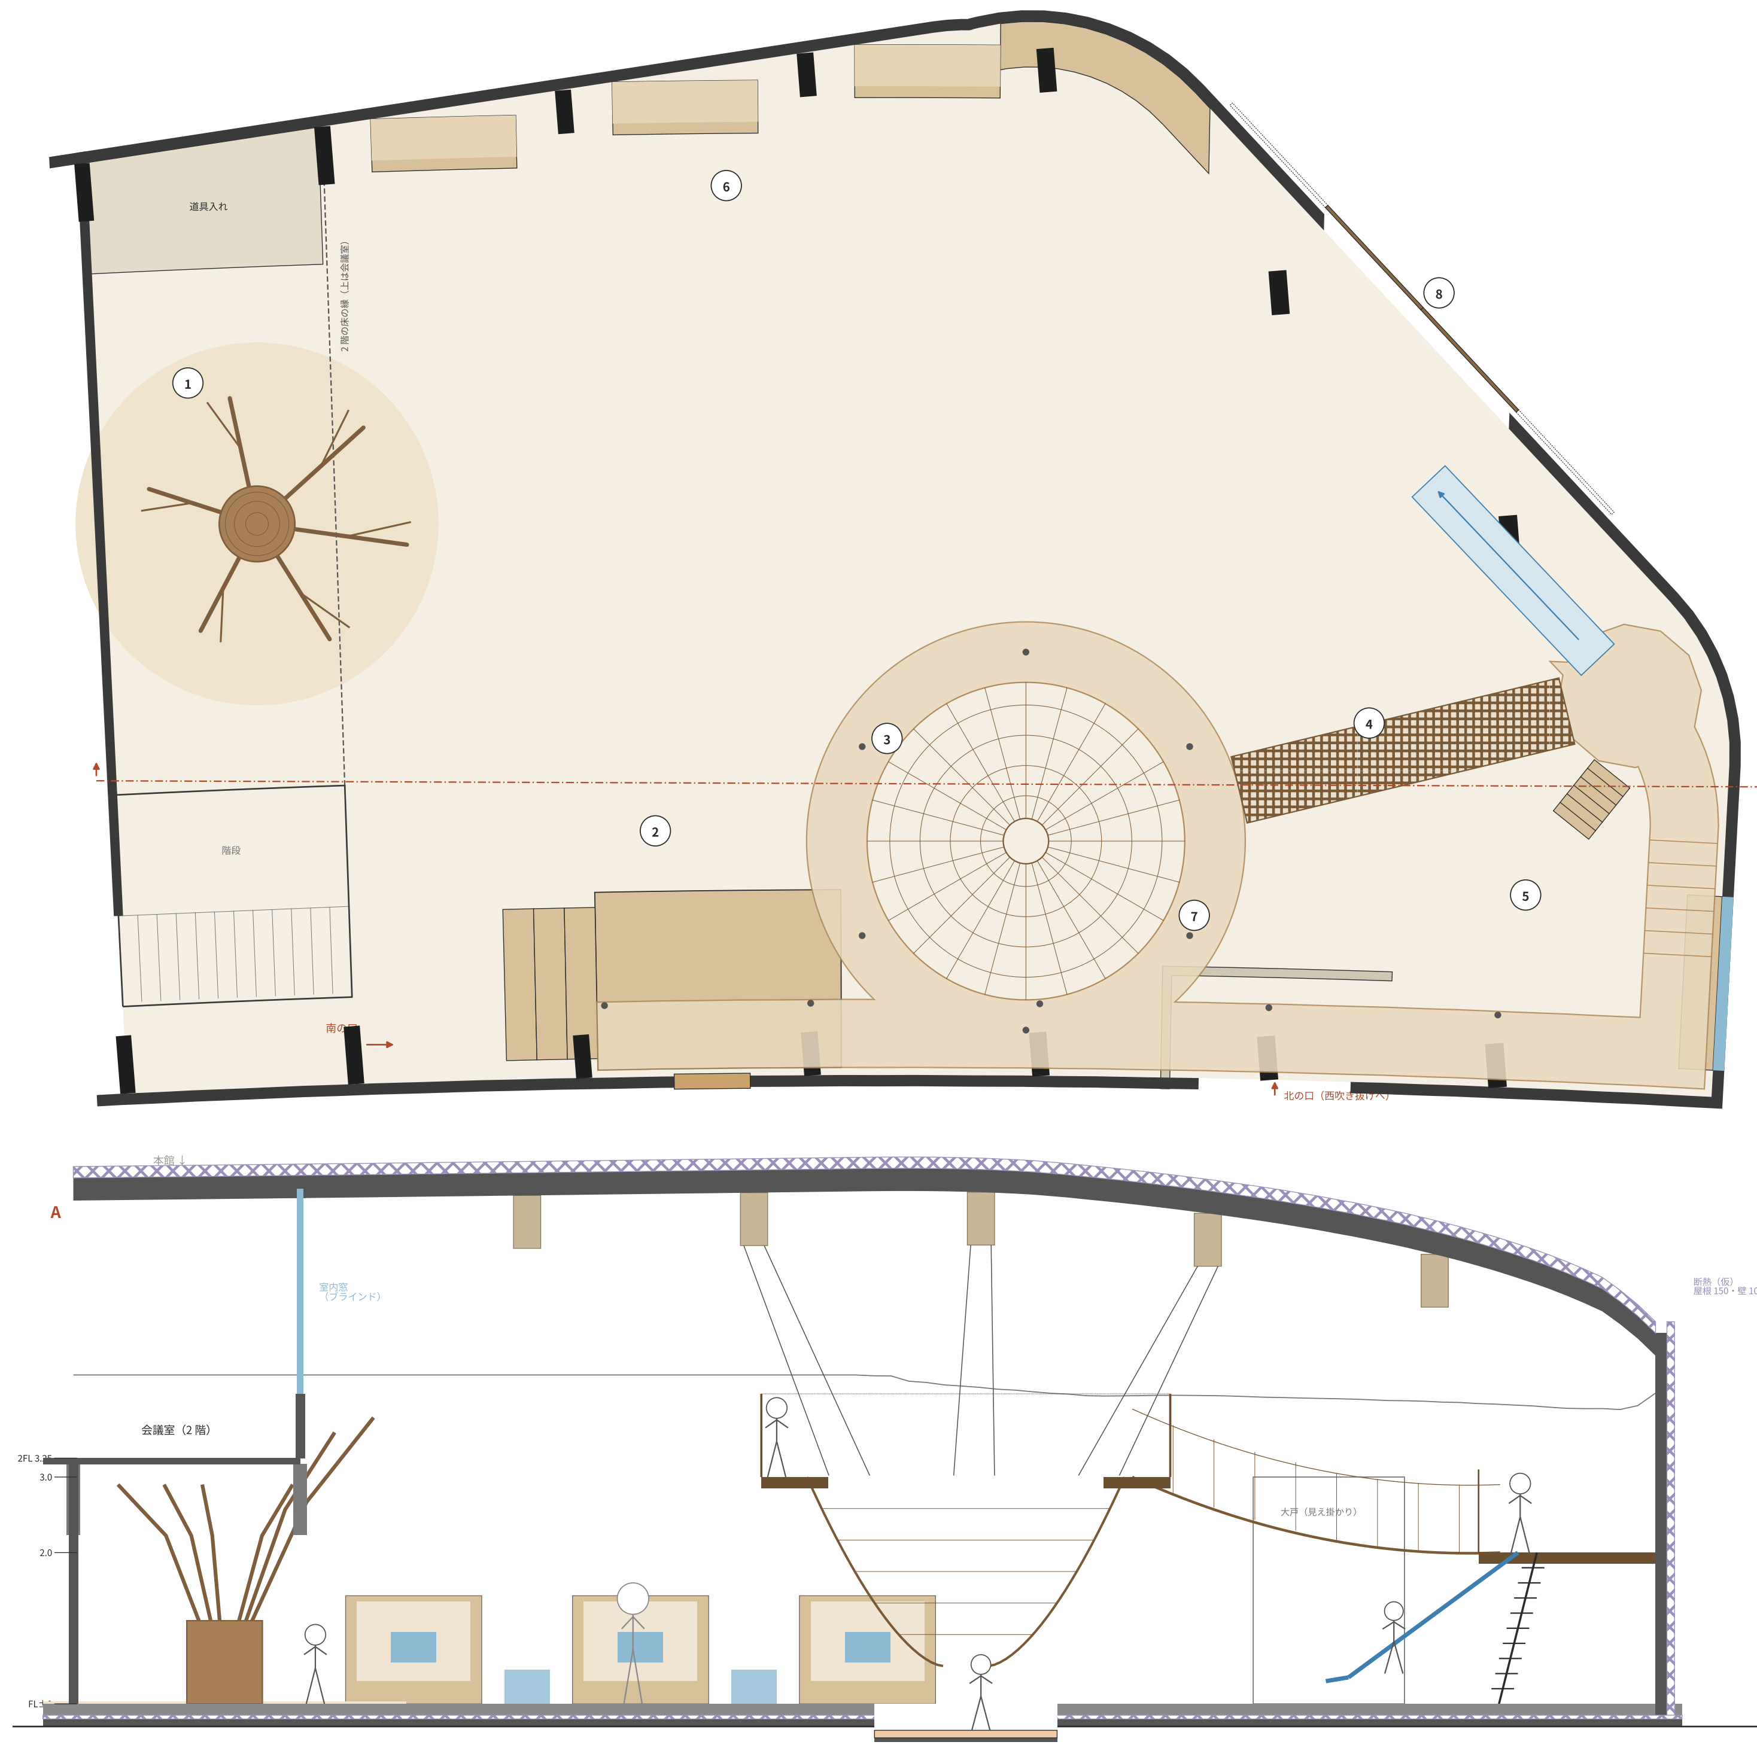

平面・断面 A 1/100

平面は FL+1.2 で切る。淡い茶は
キャットウォーク・輪・踊り場
（h3.0／2.0）、黒い点は吊り材。
断面 A は東から 4.3 で切って西を見る

遊び方

1. 洞とクスノキ
てっぺんが 2 階の床に届く
2. デッキと登り壁
→ キャットウォーク h3.0
3. 摺鉢ネットと穴の底
ネットからも輪へ登れる
4. 輪 → 網の吊り橋 → 踊り場 h2.0
空中で一周する
5. 北の段 3.0→2.0・はしご・
すべり台（落下 2.0 m 以下）
6. ひだ：くぼみ・丸いベンチ・
窓辺の腰掛け（モミジを見る）
7. 北の口のついたて（吸音）
8. 搬入の大戸（外付けの引き戸）

安全

手すりは縦格子 h1.1・すき間 90
（頭が通らない、横桟なし）
床の板のすき間 8 未満
網目 上 90・下 50、ロープ φ18

支え方

重さは梁から吊る（梁のあいだを
通す）。横の揺れは壁とハの字の
吊り材で止め、吊り橋だけ揺れる。
梁 90×700×2 は満員でも持つ
（略算：曲げ 8.0／11.0 N/mm²）

音

階段の箱がホールとの衝立。
北の口に吸音のついたて、
東の覗き窓は夜だけ開く

ホールの北山杉の林　こどもの目の高さ（0.9 m）から

ホールの北山杉の林　こどもの目の高さ（0.9 m）から見た景色　（たたき台・6 版：すべて自立）

円筒投影（横＝方位 110°、縦＝仰角）。幹は北山杉（φ50 は磨き丸太、群の φ70・100 は太鼓落とし＝両側を平らに挽いた丸太、平らな面を列の向きにそろえる）。奥の色：うす緑＝縁側のガラス越しの園庭、ベージュ＝壁、橙＝キッチンのガラス、灰＝海峡。低い木（0.85〜1.1）はこどもの目の高さを隠し、高い木は屋根の近くまで

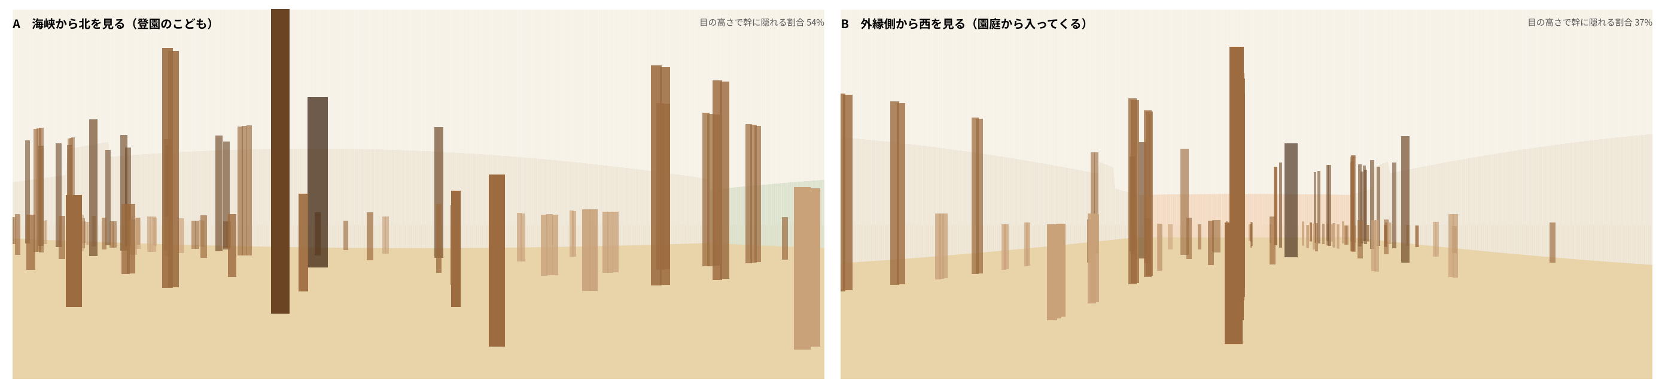
A　海峡から北を見る（登園のこども）　目の高さで幹に隠れる割合 54%

B　外縁側から西を見る（園庭から入ってくる）　目の高さで幹に隠れる割合 37%

A　本館と西館の取り合い（越屋根を含む）　断面詳細（架構 9 の面）　1/40

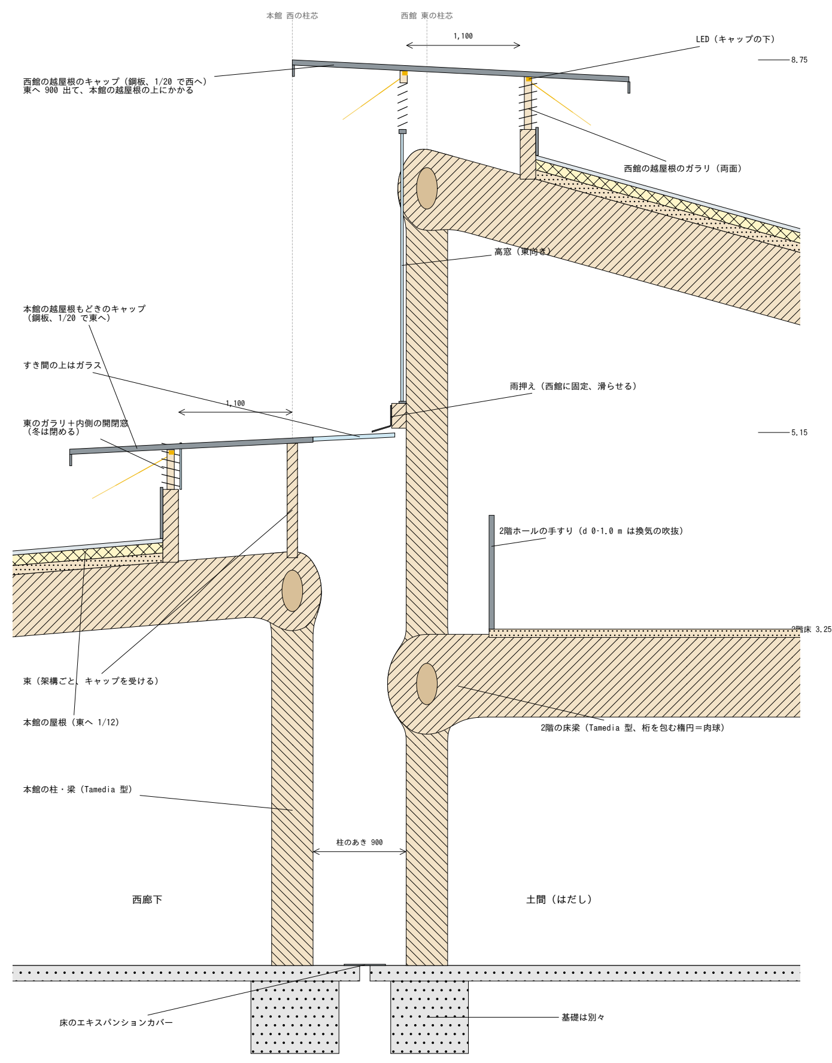

本館 西の柱芯
西館 東の柱芯
1,100
LED（キャップの下）
8.75
西館の越屋根のキャップ（鋼板、1/20 で西へ）東へ 900 出て、本館の越屋根の上にかかる
西館の越屋根のガラリ（両面）

A'　キャップがすき間をまたぐところ　1/10

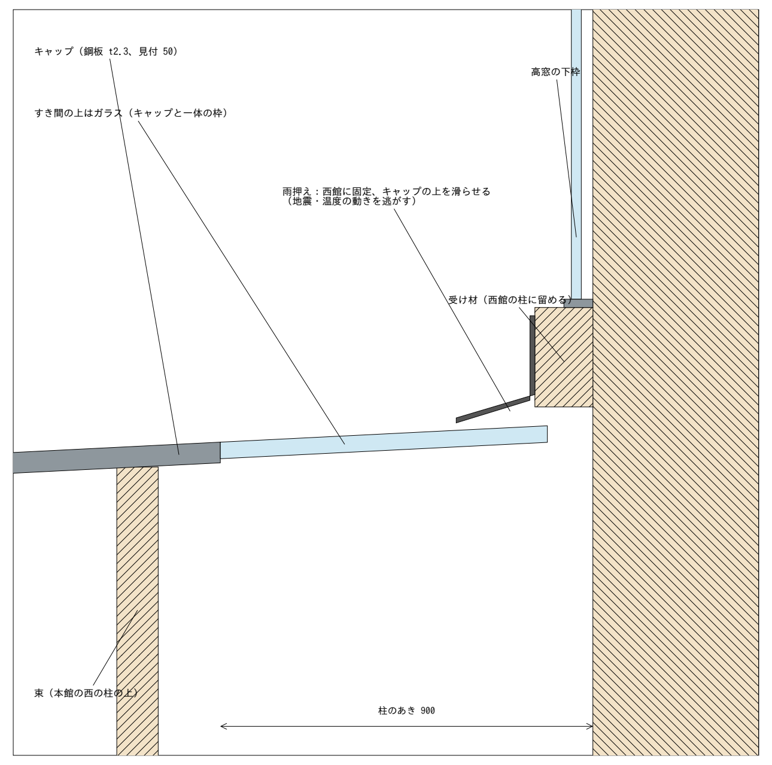

キャップ（鋼板 t2.3、見付 50）
すき間の上はガラス（キャップと一体の枠）
雨押え：西館に固定、キャップの上を滑らせる（地震・温度の動きを逃がす）
高窓の下枠

- 本館の越屋根は、西館と接する区間では西のガラリをやめ、キャップを西館の壁まで延ばして
  すき間の屋根を兼ねる（すき間の上はガラス）。外から見る越屋根の形は端から端まで続く。
- 西館の越屋根は屋根の頂点（東の縁）、換気の吹抜の真上。キャップは東へ 900 出て本館の越屋根に重なる。
- 水はどちらのキャップも外へ流れ（本館は東、西館は西）、すき間には落ちない。
- LED はキャップの下。夜は低く長い線（本館）と高く短い線（西館）の二段の光になる。
- 西館の 2 階床梁（せい 800）は、桁を包む木を厚く（280）して、楕円が梁の下に出るようにした。

洞のクスノキ　断面パース（遊戯室のチャット）

断面パース　スパン 11 の北の端（u 32.9）で切って南を見る

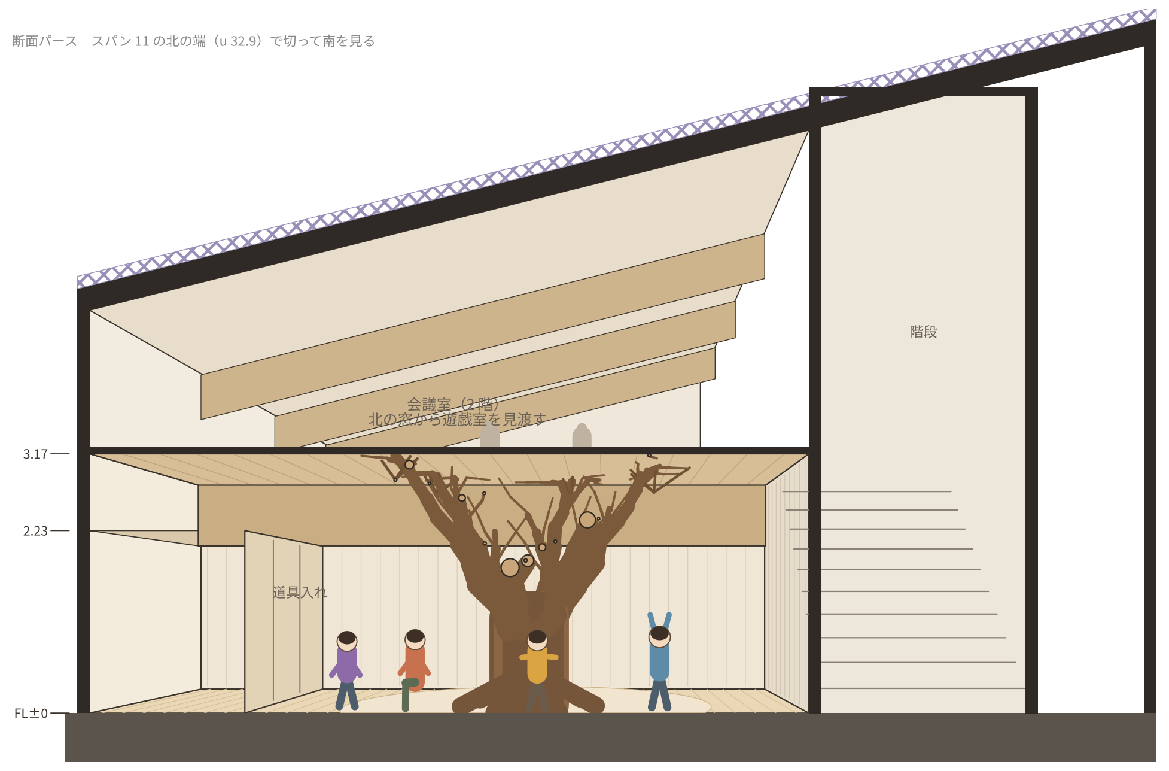

洞のクスノキ
2 階の床の下の低い洞（梁の下 2.23）。クスノキの枝の先が天井に触れ、木が 2 階を支えているように見える。
北の枝は床の縁の下をくぐって遊戯室の高い側へ（この図では切断面で切れている）。

光の筋と架構　1/20
2枚の梁のあいだ180の上に
乳白ガラスの光の筋
垂木・楕円の桁と一枚で（作成）

スケルトン＆インフィル
3 mスパンの架構（固定）と
間仕切りA・B・C、家具（可変）を色分け
どのスパンにも上水・下水の口

今／定員が変わる／学童・地域の場
の3コマ

面積表　m²（壁芯、3dmから自動）

室	要求	計画
乳児室（0〜1歳）	約60×2	120.5
保育室（2歳）	約60	60.0
保育室（3〜5歳）	約60×3	181.3
遊戯室	240以上	243.5
便所	適宜	57.3
食堂	必要に応じて	21.9
園庭	350以上	982.2
事務室	約60	73.8
休憩室	約60	62.8
医務室	約30	30.1
調理室	約60	65.7
便所（大人用）	適宜	17.1
機械室	約30	30.0
駐車場	5台以上	○
延床（2,000以内）		**1,286.5**

inspired by

Asilo Nido Iride
Mario Cucinella Architects・Guastalla・2015
→ 梁の列が並ぶ長細い本館と、外に付く付属の建物
Tamedia
坂茂・Zürich・2013
→ 梁の端の楕円の頭と、それを貫く楕円の桁
レイモンド斑鳩こども園
キノアーキテクツ・斑鳩・2026
→ 室内に木を立てる（ホールの北山杉）
KAIT工房
石上純也・厚木・2008
→ 柱の配列：見る向きで景色が変わる並び
認定こども園らみどり
はりゅうウッドスタジオ・須賀川・2026
→ 内と外の二重の縁側、遊具を置かない地形の園庭
仙田満の園舎
環境デザイン研究所
→ 摺鉢のネット、キャットウォーク、ニッチ
Waldorf School of the Peninsula
California
→ 遊戯室の切り株

［割付の注記］フォーカス：娘にこんな環境を与えたい、という空間：遊戯室・切り株・北山杉の林・組み方・変わり方　／　目に入る順：内観 → 遊戯室 → 同じ部屋の一日 → 林 → 洞 → 接合部 → S&I → 面積表 → inspired by