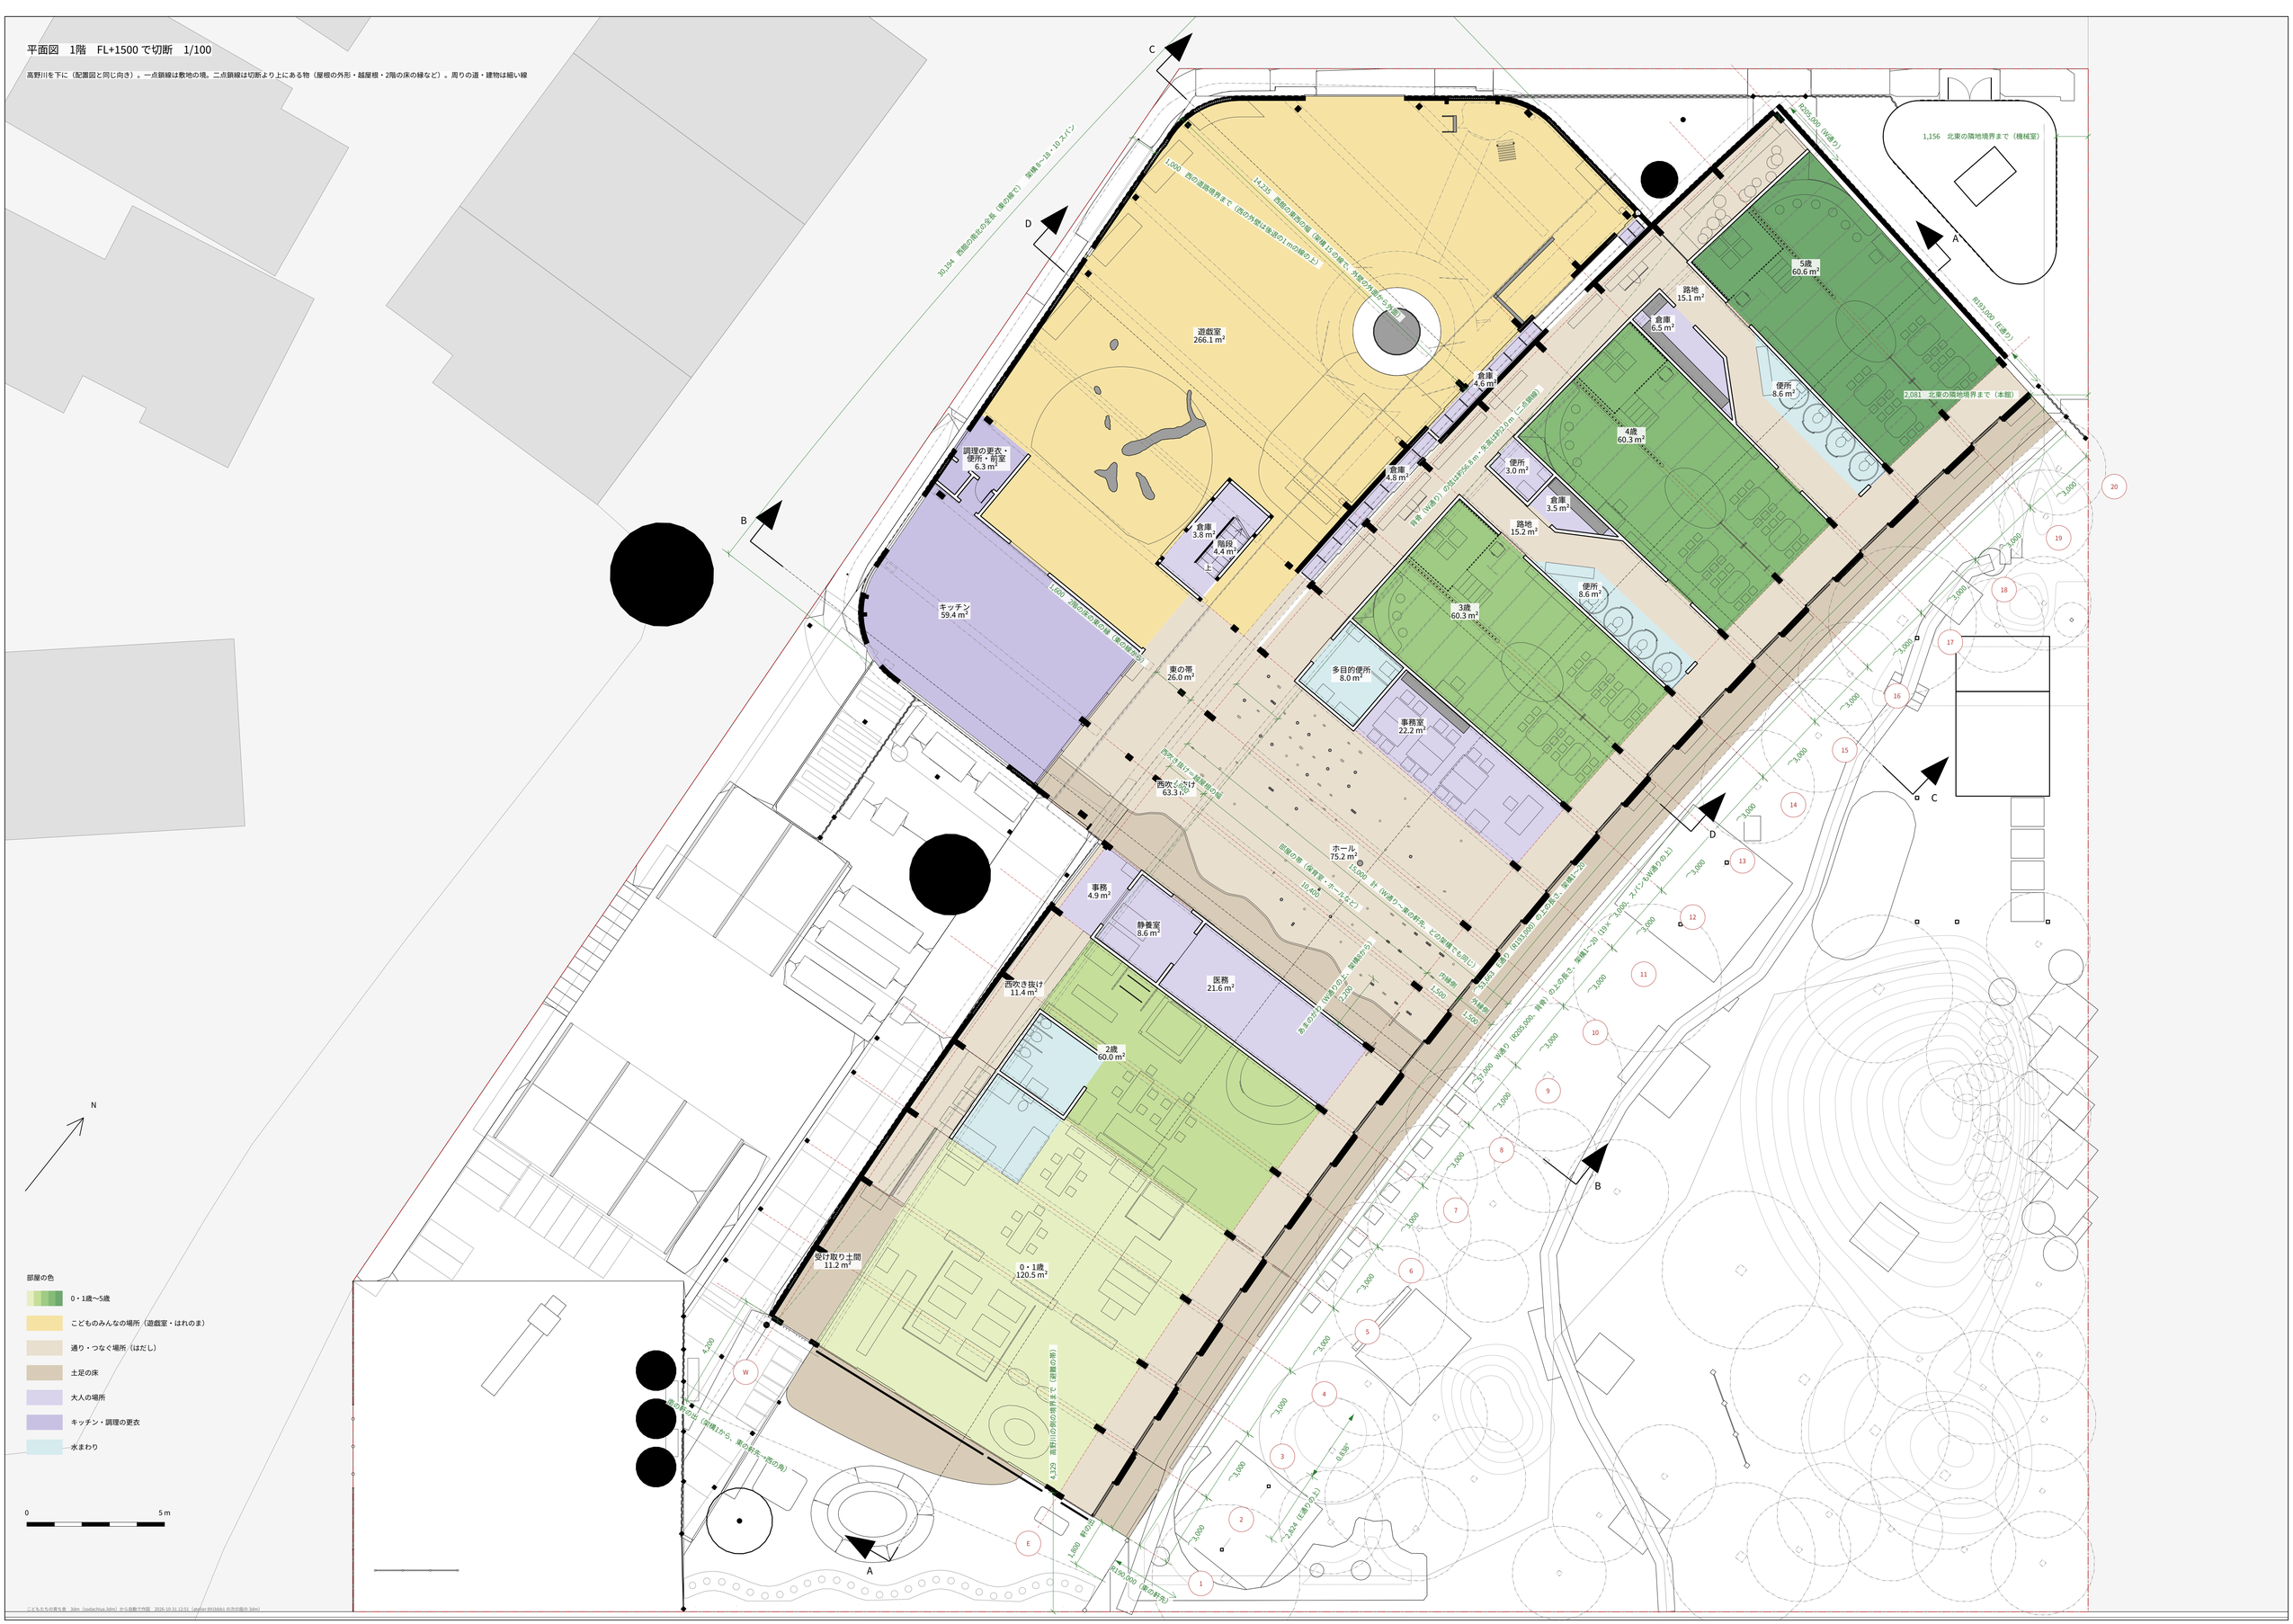
平面図　1階　FL+1500 で切断　1/100

高野川を下に（配置図と同じ向き）。一点鎖線は敷地の境。二点鎖線は切断より上にある物（屋根の外形・越屋根・2階の床の縁など）。周りの道・建物は細い線


遊戯室 266.1 m²
キッチン 59.4 m²
調理の更衣・便所・前室 6.3 m²
倉庫 3.8 m²
階段 4.4 m²
東の雑 26.0 m²
西吹き抜け 63.3 ㎡
事務室 22.2 m²
多目的便所 8.0 m²
倉庫 4.6 m²
倉庫 4.8 m²
便所 3.0 m²
倉庫 3.5 m²
路地 15.2 m²
便所 8.6 m²
3歳 60.3 m²
4歳 60.3 m²
5歳 60.6 m²
路地 15.1 m²
倉庫 6.5 m²
便所 8.6 m²
ホール 75.2 m²
事務 4.9 m²
静養室 8.6 m²
医務 21.6 m²
西吹き抜け 11.4 m²
2歳 60.0 m²
0・1歳 120.5 m²
受け取り土間 11.2 m²
A
B
C
D
E
W
N
1,156　北東の隣地境界まで（機械室）
2,081　北東の隣地境界まで（本館）
30,194　西側の児童の全長（東の端で）　架構ﾀｲﾌﾟ 1B・1D スパン
1,600　西の道路境界まで（西の外壁は敷地より 1 m の線の上）
14,235　西側の屋根の幅（架構 12 台置で、外観の外壁から外の面積）
R205,000（W通り）
R193,500（E通り）
W通り（R205,000、青骨）の上の架さ：架構ﾀｲﾌﾟ 1B〜2D（1B＝3,000、スパンにより通りの上）
E通り（R193,000、青骨）の上の架さ：架構ﾀｲﾌﾟ 1B〜2D（1B＝3,000、スパンにより通りの上）
R190,500（東の軒先）
4,200
1,650
4,329
2,424（E通りから）
0.838
1,500
1,500
1,500
10,400
1,200
1,500
1,500
1,500