

断面図 A　1/100　縦断（展開）　保育室の中ほど r=197 m の弧で切って平らに伸ばす、西を見る

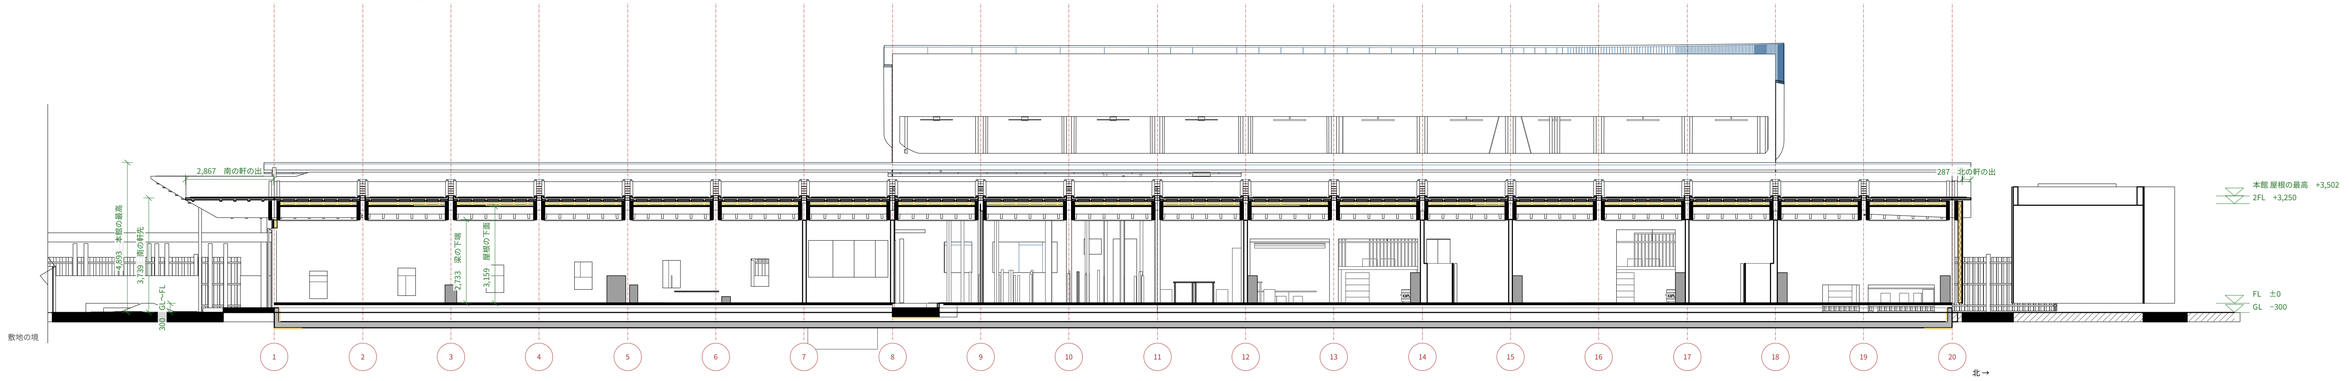


← 南（高野川の側）

断面図 B　1/100　あまのがわ（スパン 8+0.75）　南の入口・キッチン・2 階・すき間・本館・縁側、北を見る

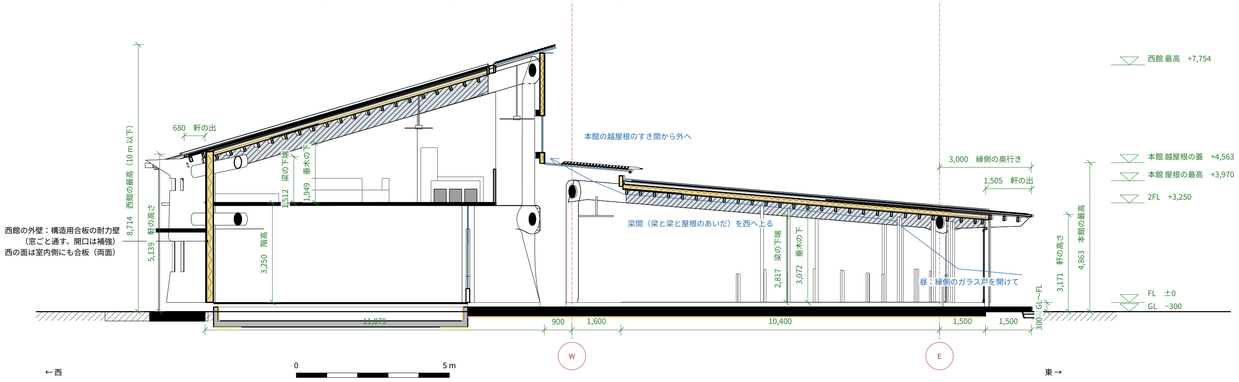

断面図 C　1/100　4 歳・遊戯室の摺鉢ネット（スパン 15+0.6）　北を見る

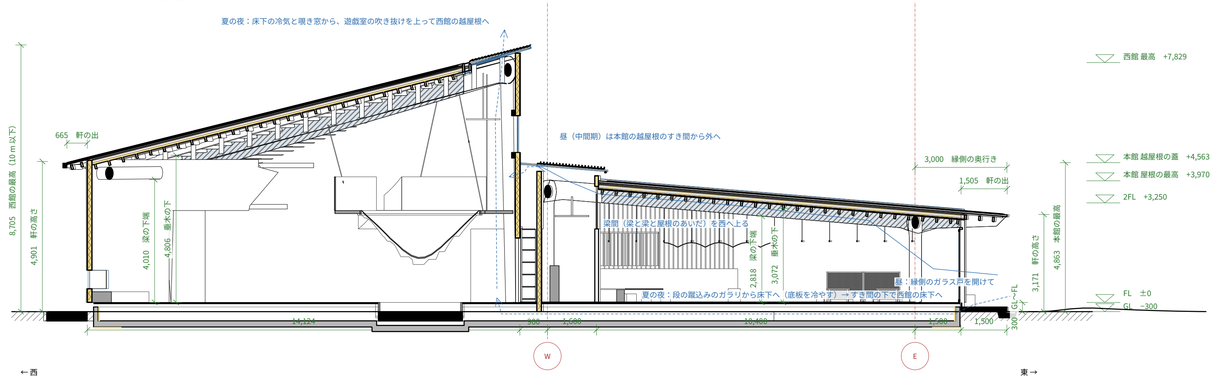

凡例（材料構造の表示、1/100 の簡略表示）

切断した構造・壁・床　／　基礎（コンクリート）　／　木（構造用合板・垂木）　／　断熱材（保温材）　／　地盤

断面図 A（縦断・展開）・B・C　1/100（A1）

こどもたちの育ち舎　3dm（sodachiya.3dm）から自動で作図　2026-10-31 12:51（atelier 891bbb1 の次の版の 3dm）