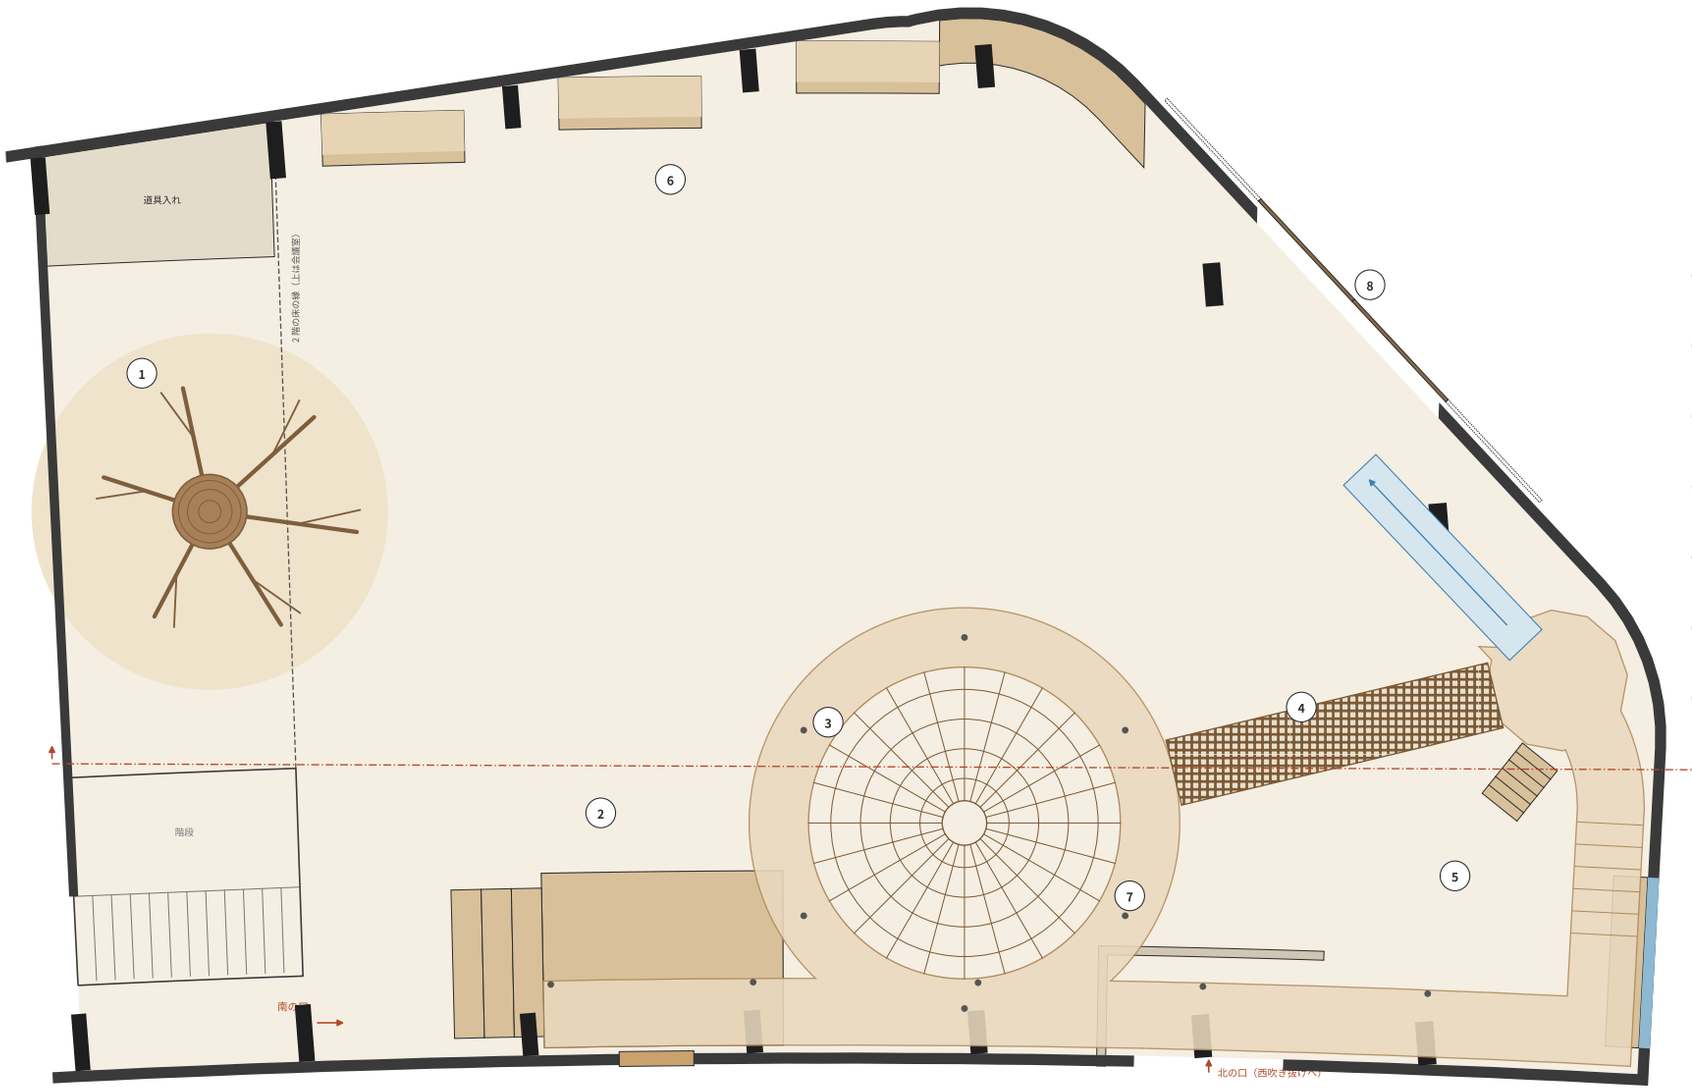


平面・断面 A 1/100

平面は FL+1.2 で切る。淡い茶はキャットウォーク・輪・踊り場（h3.0／2.0）、黒い点は吊り材。
断面 A は東から 4.3 で切って西を見る

遊び方


1. 洞とクスノキ
てっぺんが 2 階の床に届く
2. デッキと登り壁
→ キャットウォーク h3.0
3. 摺鉢ネットと穴の底
ネットからも輪へ登れる
4. 輪 → 網の吊り橋 → 踊り場 h2.0
空中で一周する
5. 北の段 3.0→2.0・はしご・すべり台（落下 2.0 m 以下）
6. ひだ：くぼみ・丸いベンチ・窓辺の腰掛け（モミジを見る）
7. 北の口のついたて（吸音）
8. 搬入の大戸（外付けの引き戸）

安全

手すりは縦格子 h1.1・すき間 90（頭が通らない、横桟なし）
床の板のすき間 8 未満
網目 上 90・下 50、ロープ φ18

支え方

重さは梁から吊る（梁のあいだを通す）。横の揺れは壁とハの字の吊り材で止め、吊り構だけ揺れる。
梁 90×700×2 は満員でも持つ（略算：曲げ 8.0／11.0 N/mm²）

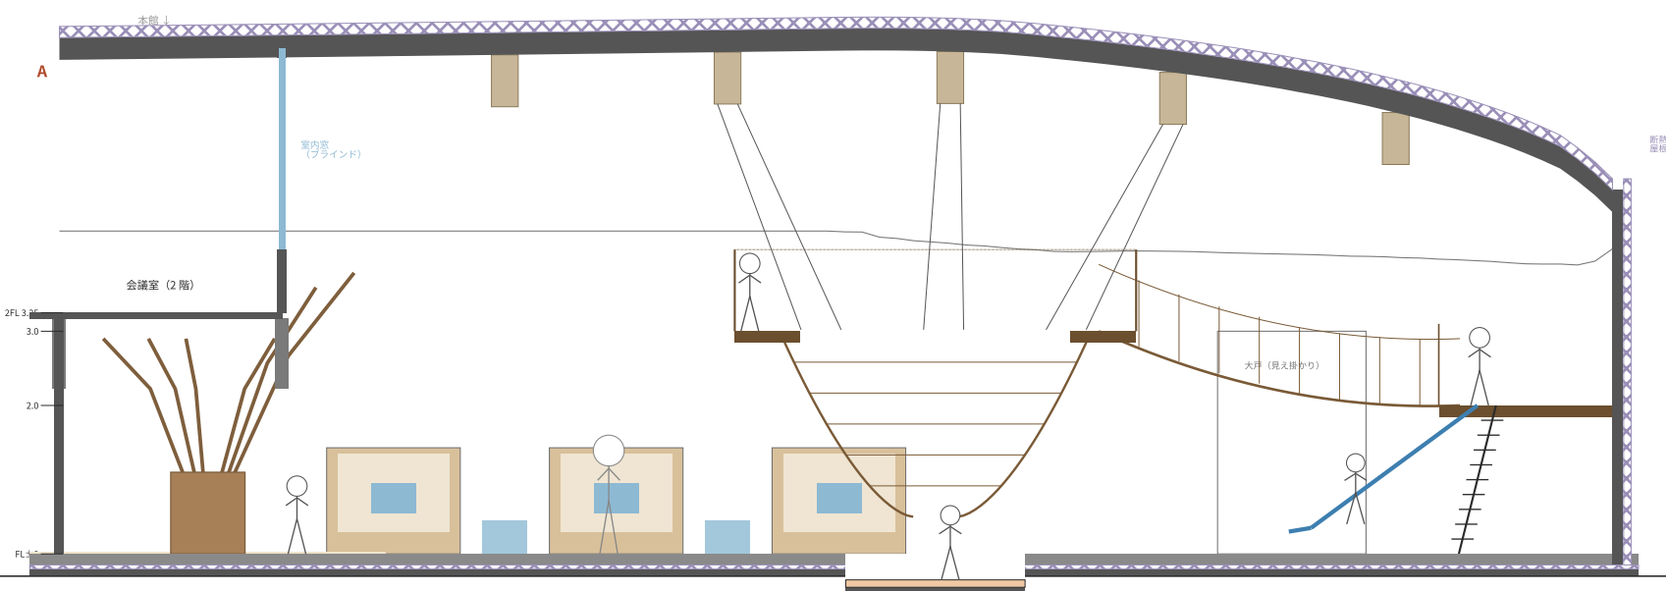

音

階段の箱がホールとの衝立。
北の口に吸音のついたて、
東の覗き窓は夜だけ開く

北

0 5 m