西館２階平面図　2FL+1200 で切断　1/100（梁は破線）

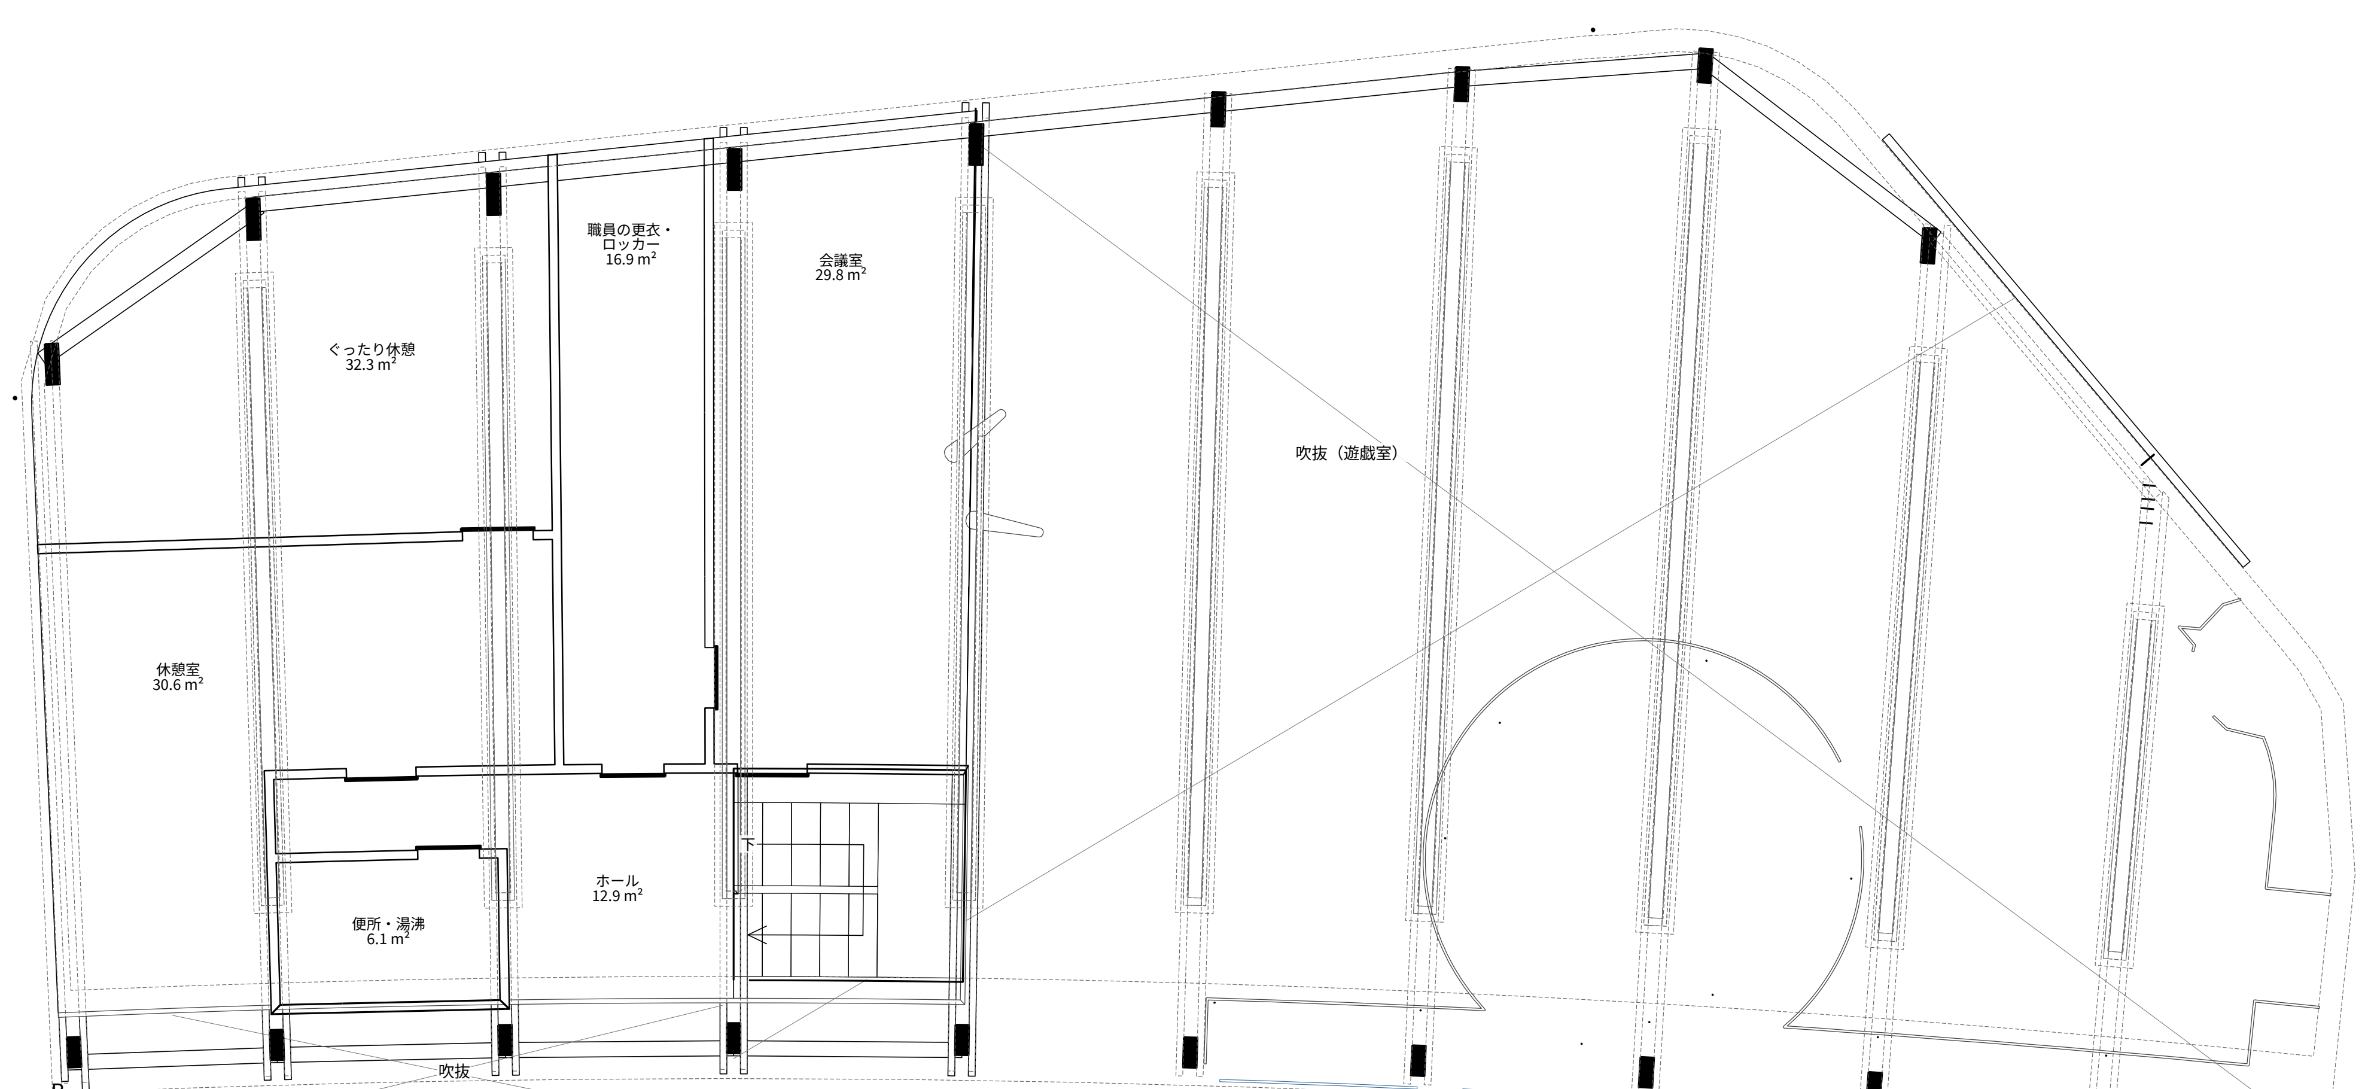

１階平面図　FL+1200 で切断　1/100　（右が北の端、下が園庭）

１階平面図・西館２階平面図　1/100（A1）　建物の軸に合わせて回してある（北は方位の矢印）

こどもたちの育ち舎　3dm（sodachiya_exact.3dm）から自動で作図　2026-10-24 10:44（atelier 00585c4 の次の版の 3dm）