育ち舎　園庭（だいさんかく・しずかのもり）　たたき台 8

配置 1/200　断面 1/100（A2）　2026-10-27　遊具は鉄棒ひと組だけ、木と地形で遊ぶ庭。山・川・原っぱ・森、そのあいだにたくさんのニッチ。

地形は GL（＝FL−300）からの高さ。等高線 0.2 m ごと（1 m を太く）。築山の位置と形はこの図で決め直した（Keynote の位置は前提にしていない）。



1/200　高野川を下に（北は右上）

凡例

- 香り：ウメ 3・クロモジ 3・キンモクセイ 4・カツラ 2・ホオノキ 1・コブシ 1
- 花：ヤマザクラ 4・サルスベリ 2・ヤマボウシ 2・アオダモ 2・ハナモモ 1
- 紅葉：イロハモミジ 4・ナツハゼ 1
- 実：カキ 1・ジューンベリー 1・クワ 3・クリ 1・ユズ 1
- 常緑：ソヨゴ 2・シラカシ 2・ホウライチク 1・ナンテン 1
- 木陰：エノキ 2・ケヤキ 1・ムクノキ 1・クヌギ 1・コナラ 1・カシワ 1
- 木登りの木（エノキ、下は木のチップ）
- 行事の草：セリ・ショウブ・摘み草・ススキ・キク
- てんぐのたに（入らない所）：両端の口をヒイラギの低い刈り込み（h1.1）でふさぐ。中は築山の裾にヤマブキ、足もとにシャガ
  飛び石：ホールの前から縁側沿いにしずかのもりへ。境は石や柵で示さず、「ここからは しずかに」と伝えるだけ（ユーザー：入ってだめなわけではない）。招かれた入口は柳の家をくぐる道
- 小川（幅 0.5、岸は急、底は平らで浅い。終わりは護岸の溝を滑り落ちる、破線は暗渠）
- 床の噴水（水遊び場、上水をためずに一度だけ使う、排水は雨の川へ。ポンプなし、弁はシャワーの柱の隣のバルブます）。上に輪のシャワー「あめのわ」。0〜2歳の前にも小さな床の噴水（φ4.0、低い泡と霧のわ、南のカツラの木陰）
- 雨の川（雨落ちの溝、玉石。本館の雨は樋なしで落ち、南へ流れて雨庭へ。大雨で溢れたらすりばちが雨の池）
- 雨庭（洲浜）：玉石の浜の浅いくぼみ −0.25、下に砕石。初めの約5 mmの雨を溜めてしみ込ませ、溢れた分だけ護岸の溝から高野川へ。景石3、ミソハギ（盆花）・ギボウシ・カンスゲ・ハンゲショウ
- 砂場・粒の遊び場（1〜2 mm、2.4×3.0 の木の縁、帆布を巻いた棒を転がして「おやすみね」とカバー）
- 等高線 0.2 m（太線 1.0 m）
- 剪定・搬入の車の道（芝の保護材 幅 2.5、ふだんは庭）
- 先生のいる所（縁側の外の縁・小屋の軒、目の高さ GL+1.35）
- 死角：どの先生からも子どもの頭（地面+0.9）が見えない所

ニッチ（静かに遊べる・ひとりになれる所）

1. みなもと：二つの丘のあいだから湧き出す石組み
2. 丸太の輪：切り株の腰掛け（おくのもり）
3. ほら：築山の北西の面の木の枠のくぼみ（3歳の縁側から見える向き）
4. 山の肩の平ら：腰掛ける段（丸太の土留め）
5. 木登りの木（エノキ）の根もと
6. かぜのもり：低い起伏と倒木
7. のぞき：小川が護岸の溝を滑り落ちる所（生垣の口、柵ごしに高野川を覗き込む）
8. すりばち：小さなくぼ地（お話の輪）
9. 柳の家：小川のほとりの生きたヤナギのドーム、しずかのもりの入口
10. 乳児の床の噴水（0〜2 歳、霧のわ）と粒の遊び場
11. 川辺の座り石

数字（この図から）

だいさんかく（しずかのもりを含む）約 886 m²。屋外遊戯場として数えるのは小屋（便所・倉庫・コンポストの間 約 35 m²）を除いた 約 851 m²（2 歳以上 70 人で 1 人 約 12.2 m²、基準は 3.3）。うち しずかのもり 約 162 m²

築山：頂 +2.5 m、裾の広さ 約 148 m²、土 約 143 m³。起伏・土手を足すと盛る土は 約 214 m³
→ おくのもりへの上り（最大 +0.7）・かぜのもりの林床・土手 +1.0 も含めて締め固め 約 207 m³。運び込まない。本館の床は床下空間（根切り GL−0.6、ユーザー）で、掘る土は 約 844 m³（本館 約 539、西館ほか 約 259、園庭 約 42）

小川：地上の長さ 約 46 m、みなもとの小さな滝（落差 約0.45）から、川床は滝壺 +0.05 → −0.40（地面から0.15以上下げる）。水深 3〜5 cm で 約 4〜10 L/s（流れ 0.3〜0.4 m/s）。用水路の口の堰板で加減、大雨は水門を閉じる

木 50 本（28 種）。噴水の夏の日陰（7 月下旬）：9 時 58%、10〜13 時 約 42%（南東のケヤキ）、15 時 38%、16 時 75%（本館の影）。休むのは縁側の庇の下

床の噴水：約 17 m²、噴き口 18 個（0.8 m ごと）＋輪のシャワー「あめのわ」。上水、排水は雨の川へ。雨の川：屋根 約 880 m²、100 mm/h で南の端 約 24 L/s、溝 0.5×0.2・1/200 で 約 50 L/s（目安）


小屋：便所 6.8＋倉庫 12.9＋コンポストの間 15.6 m²（一つの屋根）。倉庫は教材庫×2（13.0）＋遊戯室の道具入れ（5.7）に足して 30 m² を超える

コンポスト：小屋の倉庫の南東、屋根の下の壁のない間に木枠 4 つ（落ち葉・入れる・寝かせる・できた、全体 約 4.6×1.2）。4・5 歳の当番がキッチンから野菜くずをもらい、落ち葉と重ね、できた土を入口の前の菜園へ運ぶ（ユーザー）


土の使い道（ユーザー：無理なく使える分だけ）：表土 約 160 m³ は全部敷地に残す（築山の表面 0.2・木の下の林床 0.2 約 567 m²・菜園）。下の土は築山の芯・土手・林床の盛り・西館の床の下へ。外へ出すのは下の土 約 504 m³（近くの工事へ）

死角：約 33 m²。築山の裏（隣家側）の植え込み（てんぐのたに）と、おくのもりの奥。植え込みは入らない所にする

断面 A–A　ホールから築山の頂を通って比叡山の向きへ　1/100

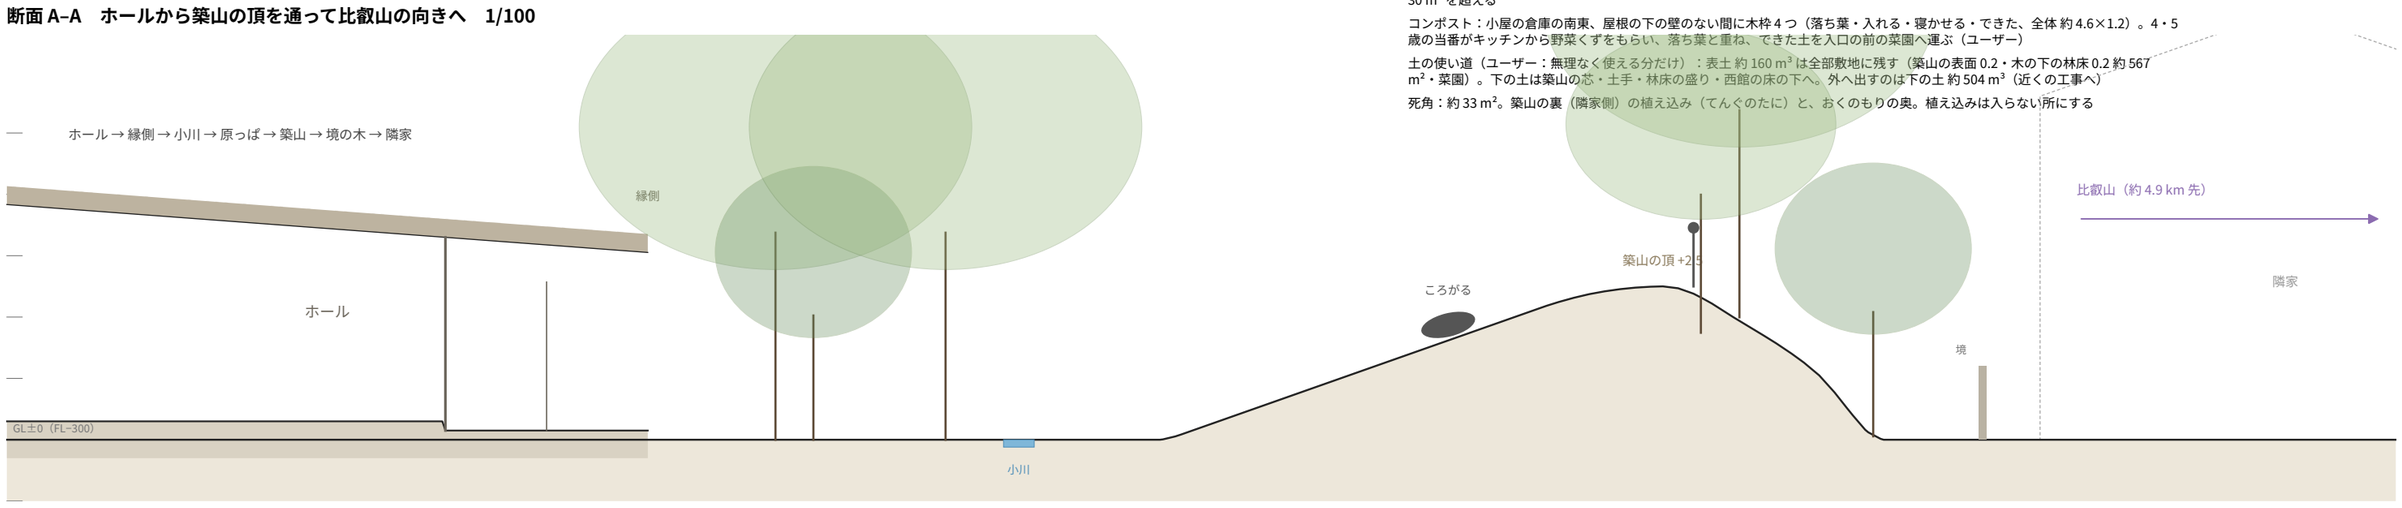

断面 B–B　築山から原っぱ・のぞき（生垣の口）を通って高野川へ　1/100（崖・河川敷の寸法は仮）

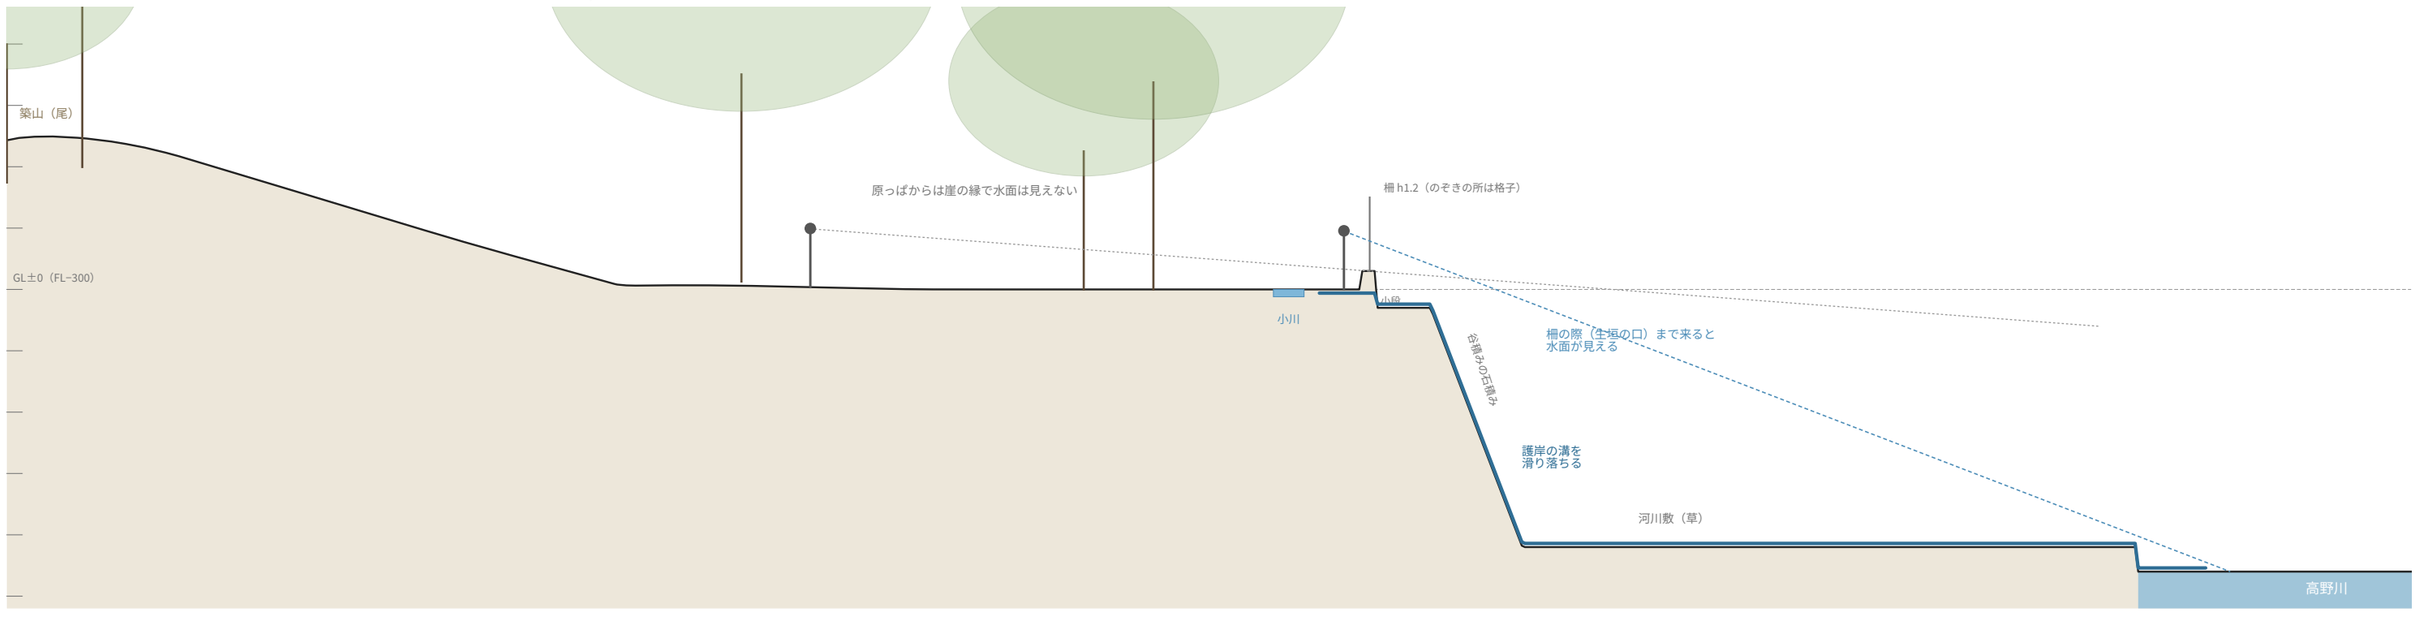

保母さんが困らないように（木と地形の約束）

- 高木は枝下 2 m 以上に仕立て、目の高さを見通す。低木は 60 cm 以下（大人は上から見える、子どもは隠れられる）。
- 縁側の外の縁と小屋の軒から全体が見える。見えない所（赤の斜線）は植え込みで入らない所にする。
- 毒・とげ・かぶれの木は使わない（キョウチクトウ・イチイ・アセビ・ピラカンサ・ハゼ・エゴノキ・ジンチョウゲ・ツツジ類 など）。ロウバイ（種に毒）は園庭に置かない（本館の読書の庭へ）。
- ツバキ・サザンカは植えない（チャドクガ）。落葉樹が中心、落ち葉は遊びに使い、掃くのは小径と縁側の前だけ。
- 木登りの木は決めておく（2 本まで）。下は剪定の枝でつくった木のチップ（剪定 → チップ → 根もと、を園の中で回す）。
- 水は浅く（小川 3〜5 cm）、床の噴水は水がたまらず外縁側のすぐ前（濡れたまま縁側へ、シャワーの柱）。子どもが手や口にふれる水は上水だけ（小川の水は飲まない、遊んだら足洗い場で洗う）。
- 縁側の前 1.5 m は木を植えない（出入りと見通し）。車の道は要素の間を縫う目安（車のために木や遊び場をずらさない）。