育ち舎　遊戯室（スパン 11–17）　たたき台

1/100（A3）　2026-10-21　上が北（本館の背骨に沿って回した）。西館の東西は「東から」（v = −0.9 の線から西へ）。寸法は data/play.json。破線の紫＝2 階の床（上）、青の破線＝越屋根の吹き抜け（上）、破線の円＝枝の広がり・扇、点の帯＝キャットウォーク（頭上h3.0）。

面積（概算）：遊戯室 264 m²（うち洞・階段・南の口のスパン 11 は 40 m²）　あけておく床 約 192 m²

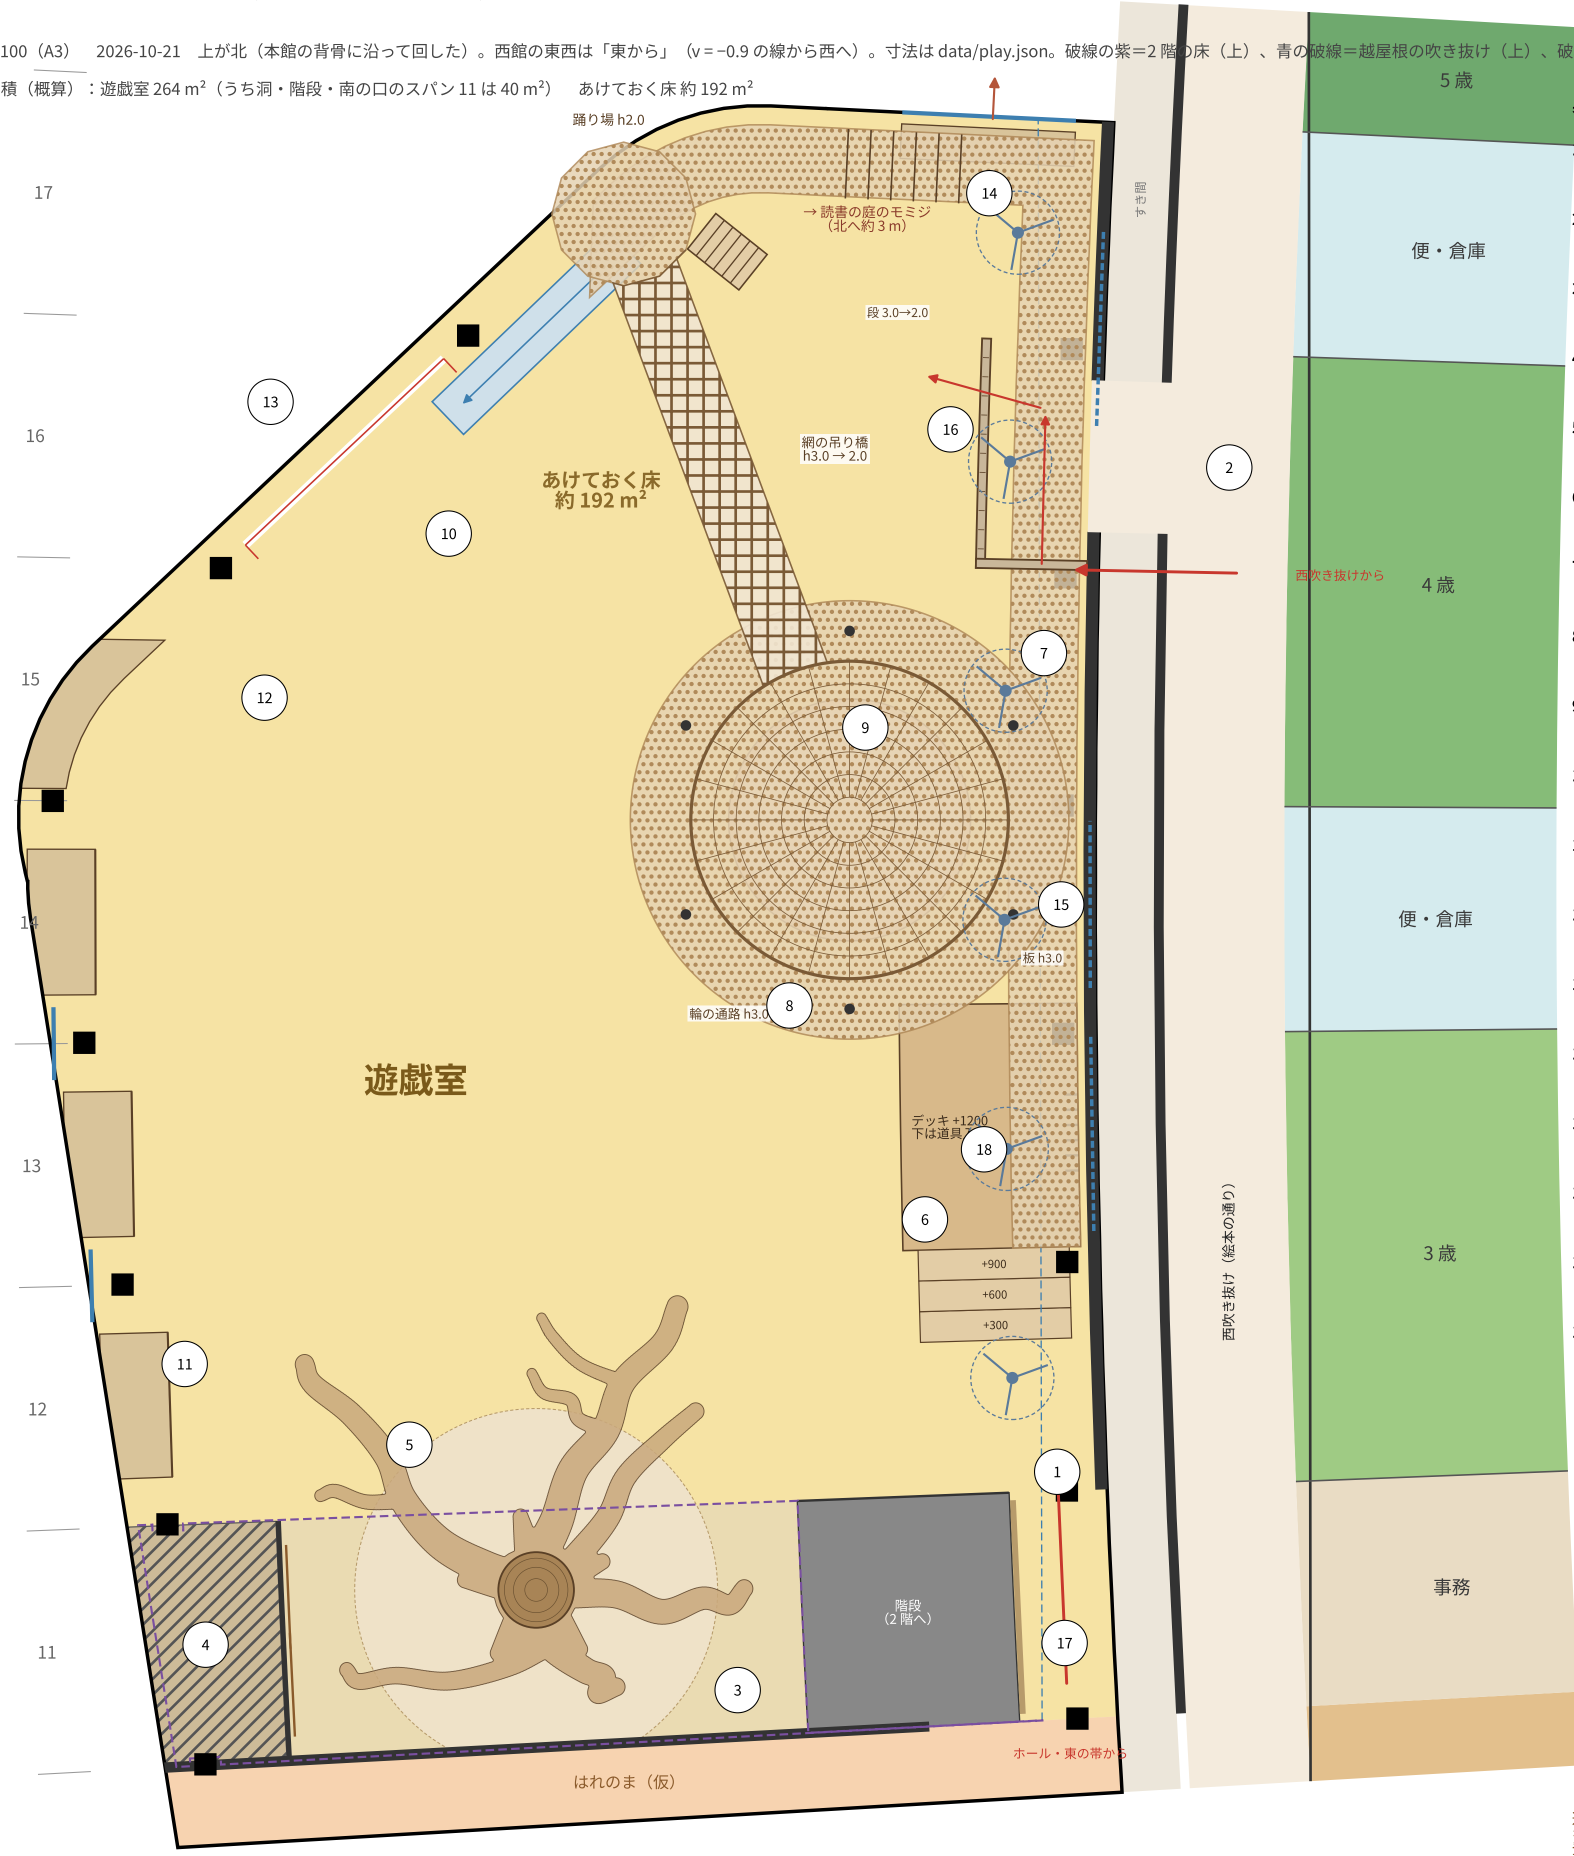
踊り場 h2.0
→ 読書の庭のモミジ（北へ約 3 m）
段 3.0→2.0
網の吊り橋 h3.0 → 2.0
あけておく床 約 192 m²
遊戯室
輪の通路 h3.0
板 h3.0
デッキ +1200 下は道具入れ
+900
+600
+300
階段（2 階へ）
はれのま（仮）
ホール・東の帯から
すき間
西吹き抜けから
西吹き抜け（絵本の通り）
5 歳
便・倉庫
4 歳
便・倉庫
3 歳
事務
17
16
15
14
13
12
11
1
2
3
4
5
6
7
8
9
10
11
12
13
14
15
16
17
18

番号

1 南の口（ホール・東の帯から、階段の東を抜ける）。口①はここにまとめた

2 北の口（口②、西吹き抜けから、すき間を渡る）

3 洞（2 階の下、梁の下 h2.23・床の裏 h3.17）。木のてっぺんが 2 階の床に届く。南は はれのま との壁（u30、2 階の床まで）

4 道具入れ 約 5.7 m²（西の低い隅、東向きの引き戸。発表会の椅子など。倉庫 30 m² の一つに数える）

5 枝付きのクスノキ（幹 φ1.0、約1mで太い枝5本に分かれ、肘で折れて横へうねる。本物のライブオークの枝ぶりに学んだ。樟脳の香り）。3本は2階の床の裏に届き、北の太い枝は天井の高い側へ横に張る（h1.5〜2.0）。西の枝は h約1.0の腰掛け、北東の低い枝は h約0.8。行事の日は木の前が舞台

6 デッキ h1.2（下はマット・ボールの道具入れ）。登り口は家具階段 +300／600／900、東の壁に登り壁 → キャットウォーク

7 キャットウォーク 幅 0.9：東の壁は板の床 h3.0、北の壁で段（200×5）を下りて北西の踊り場 h2.0 へ。手すりは縦格子 h1.1（すき間 90、横桟なし）。ネットの輪から踊り場へは網の吊り橋（3.0→2.0、真ん中が垂れる）。空中で一周。支え方：重さは吊り材で屋根へ、横は壁の受け材で止める。吊り橋だけ揺れてよい

8 摺鉢ネット（上の縁 φ4.2、下の口 φ0.6 が h0.5、網目 上 90・下 50、ロープ φ18）。吊り橋と踊り場から輪へ登れる（2 か所目の登り口）。まわりに輪の通路 h3.0（幅 0.8、外 φ5.8）、ネットの縁は内側の鋼の輪に一周留める。輪は 6 本の吊り材をハの字の 3 組に（三角形で横の揺れを止める）

9 穴の底（φ3.2、−450、マット 100）

10 すべり台：北西の踊り場 h2.0 から北西の面に沿って、大戸の前を滑り降りる（長さ約 3.2、約 32°、幼児用の落下高さ 2.0 m 以下）。踊り場の脇にはしご（3 か所目の登り口、段 200）。大戸は外開きで避難の邪魔にならない。搬入の工事のときは外す

11 西の柱と柱のあいだのくぼみ（造作の箱、奥行き 0.7、座 +300、天板 h1.4、奥に格子の覗き窓）。あいだの壁に地窓。詳しくは play02

12 北西の丸い角の丸いベンチ

13 搬入の大戸（幅 3.6×h3.0、外開き、ふだんは閉じる、避難口）

14 北の窓辺の腰掛け +300（窓 h350〜1200、座って読書の庭のモミジを見る）

15 東の壁の覗き窓（キャットウォークの高さ、すき間越しに本館）。昼は閉じ（音を本館へ回さない）、夏の夜だけ自動で開く

16 北の口のついたて（h2.4、長さ 3.0、吸音の面＋遊戯室側は掲示板）。南の端は閉じ、北へ抜ける（穴の底を避ける）。午睡の時間はすき間側に厚手の暖簾も

17 南の口の通路：階段の箱の東の面を吸音の板張りに

18 天井扇 φ1.1 ×6（本館と同じ、越屋根の吹き抜け w0–1.0 の真下、h6.0）

遊び方の輪：南の口 → 家具階段 → デッキ → 登り壁 → キャットウォーク → 北の段 → 踊り場 → 網の吊り橋 → ネットの輪 → 東。
登り口は登り壁・ネット・はしご、降りるのはネットかすべり台。
北の口から西吹き抜けへ。木は低い洞に：てっぺんが 2 階の床に届き、枝の先が高い側へ出る。

東西の断面（摺鉢ネットの中心 u 41.8 で切る、北を見る）　左＝西（道路）、右＝東（本館）

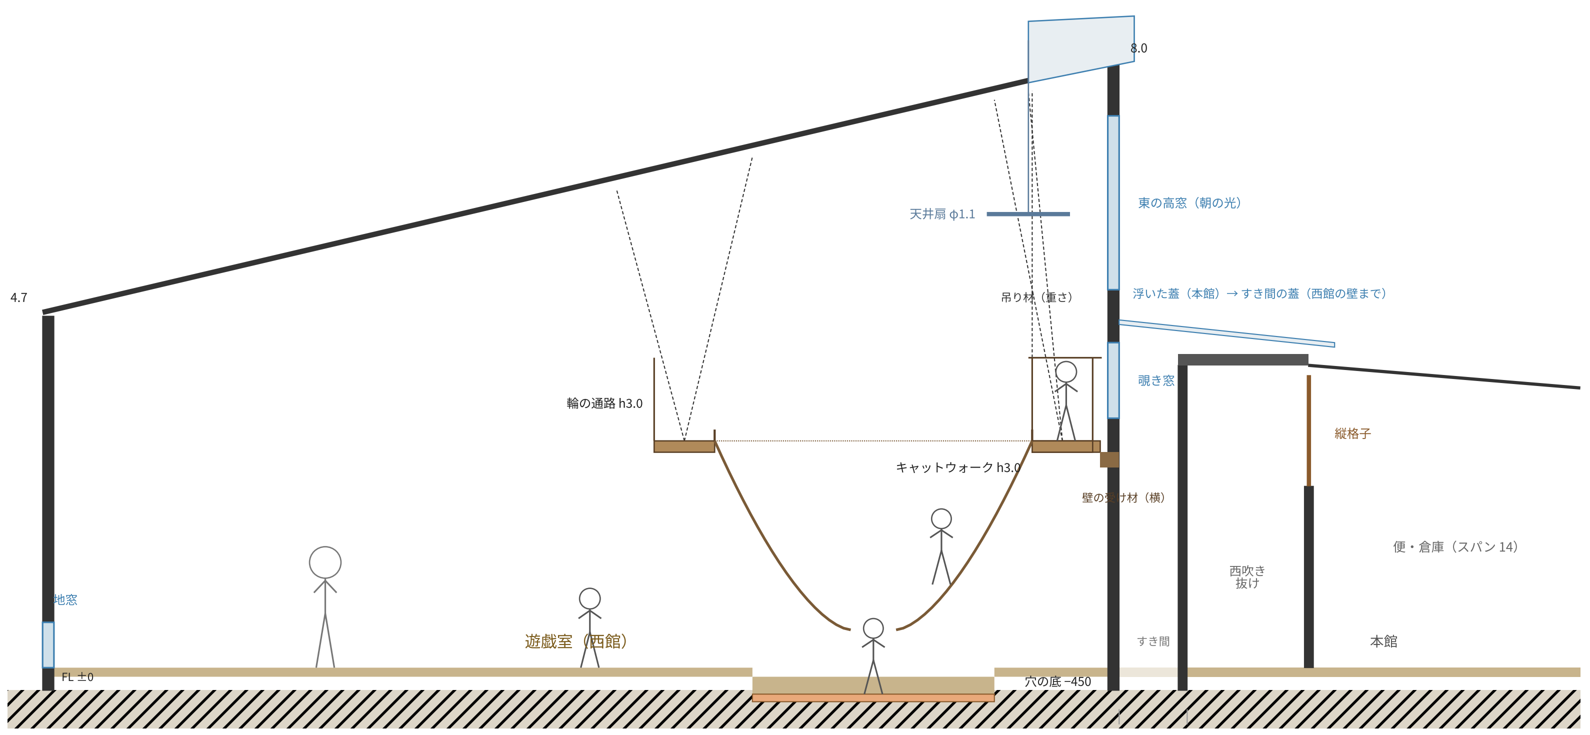
浮いた蓋（西館）
8.0
4.7
天井扇 φ1.1
東の高窓（朝の光）
吊り材（重さ）
浮いた蓋（本館）→ すき間の蓋（西館の壁まで）
覗き窓
縦格子
輪の通路 h3.0
キャットウォーク h3.0
壁の受け材（横）
便・倉庫（スパン 14）
西吹き抜け
地窓
遊戯室（西館）
すき間
本館
FL ±0
穴の底 −450

南北の断面（木の中心、東から 7.6 で切る、西を見る）
左＝南（はれのま）、右＝北

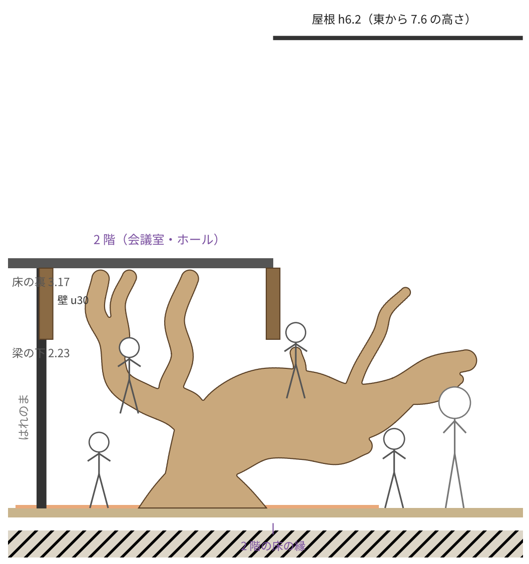
屋根 h6.2（東から 7.6 の高さ）
2 階（会議室・ホール）
床の裏 3.17
壁 u30
梁の下 2.23
はれのま
2 階の床の縁