平面図　2階（西館）　2FL+1000 で切断　1/100

高野川を下に（配置図と同じ向き）。1階の平面図と同じ位置・同じ縮尺（重ねると上下が合う）。西館の外（本館の屋根・園庭・周り）は上から見た見えがかり。二点鎖線は切断より上にある物（西館の屋根の外形など）

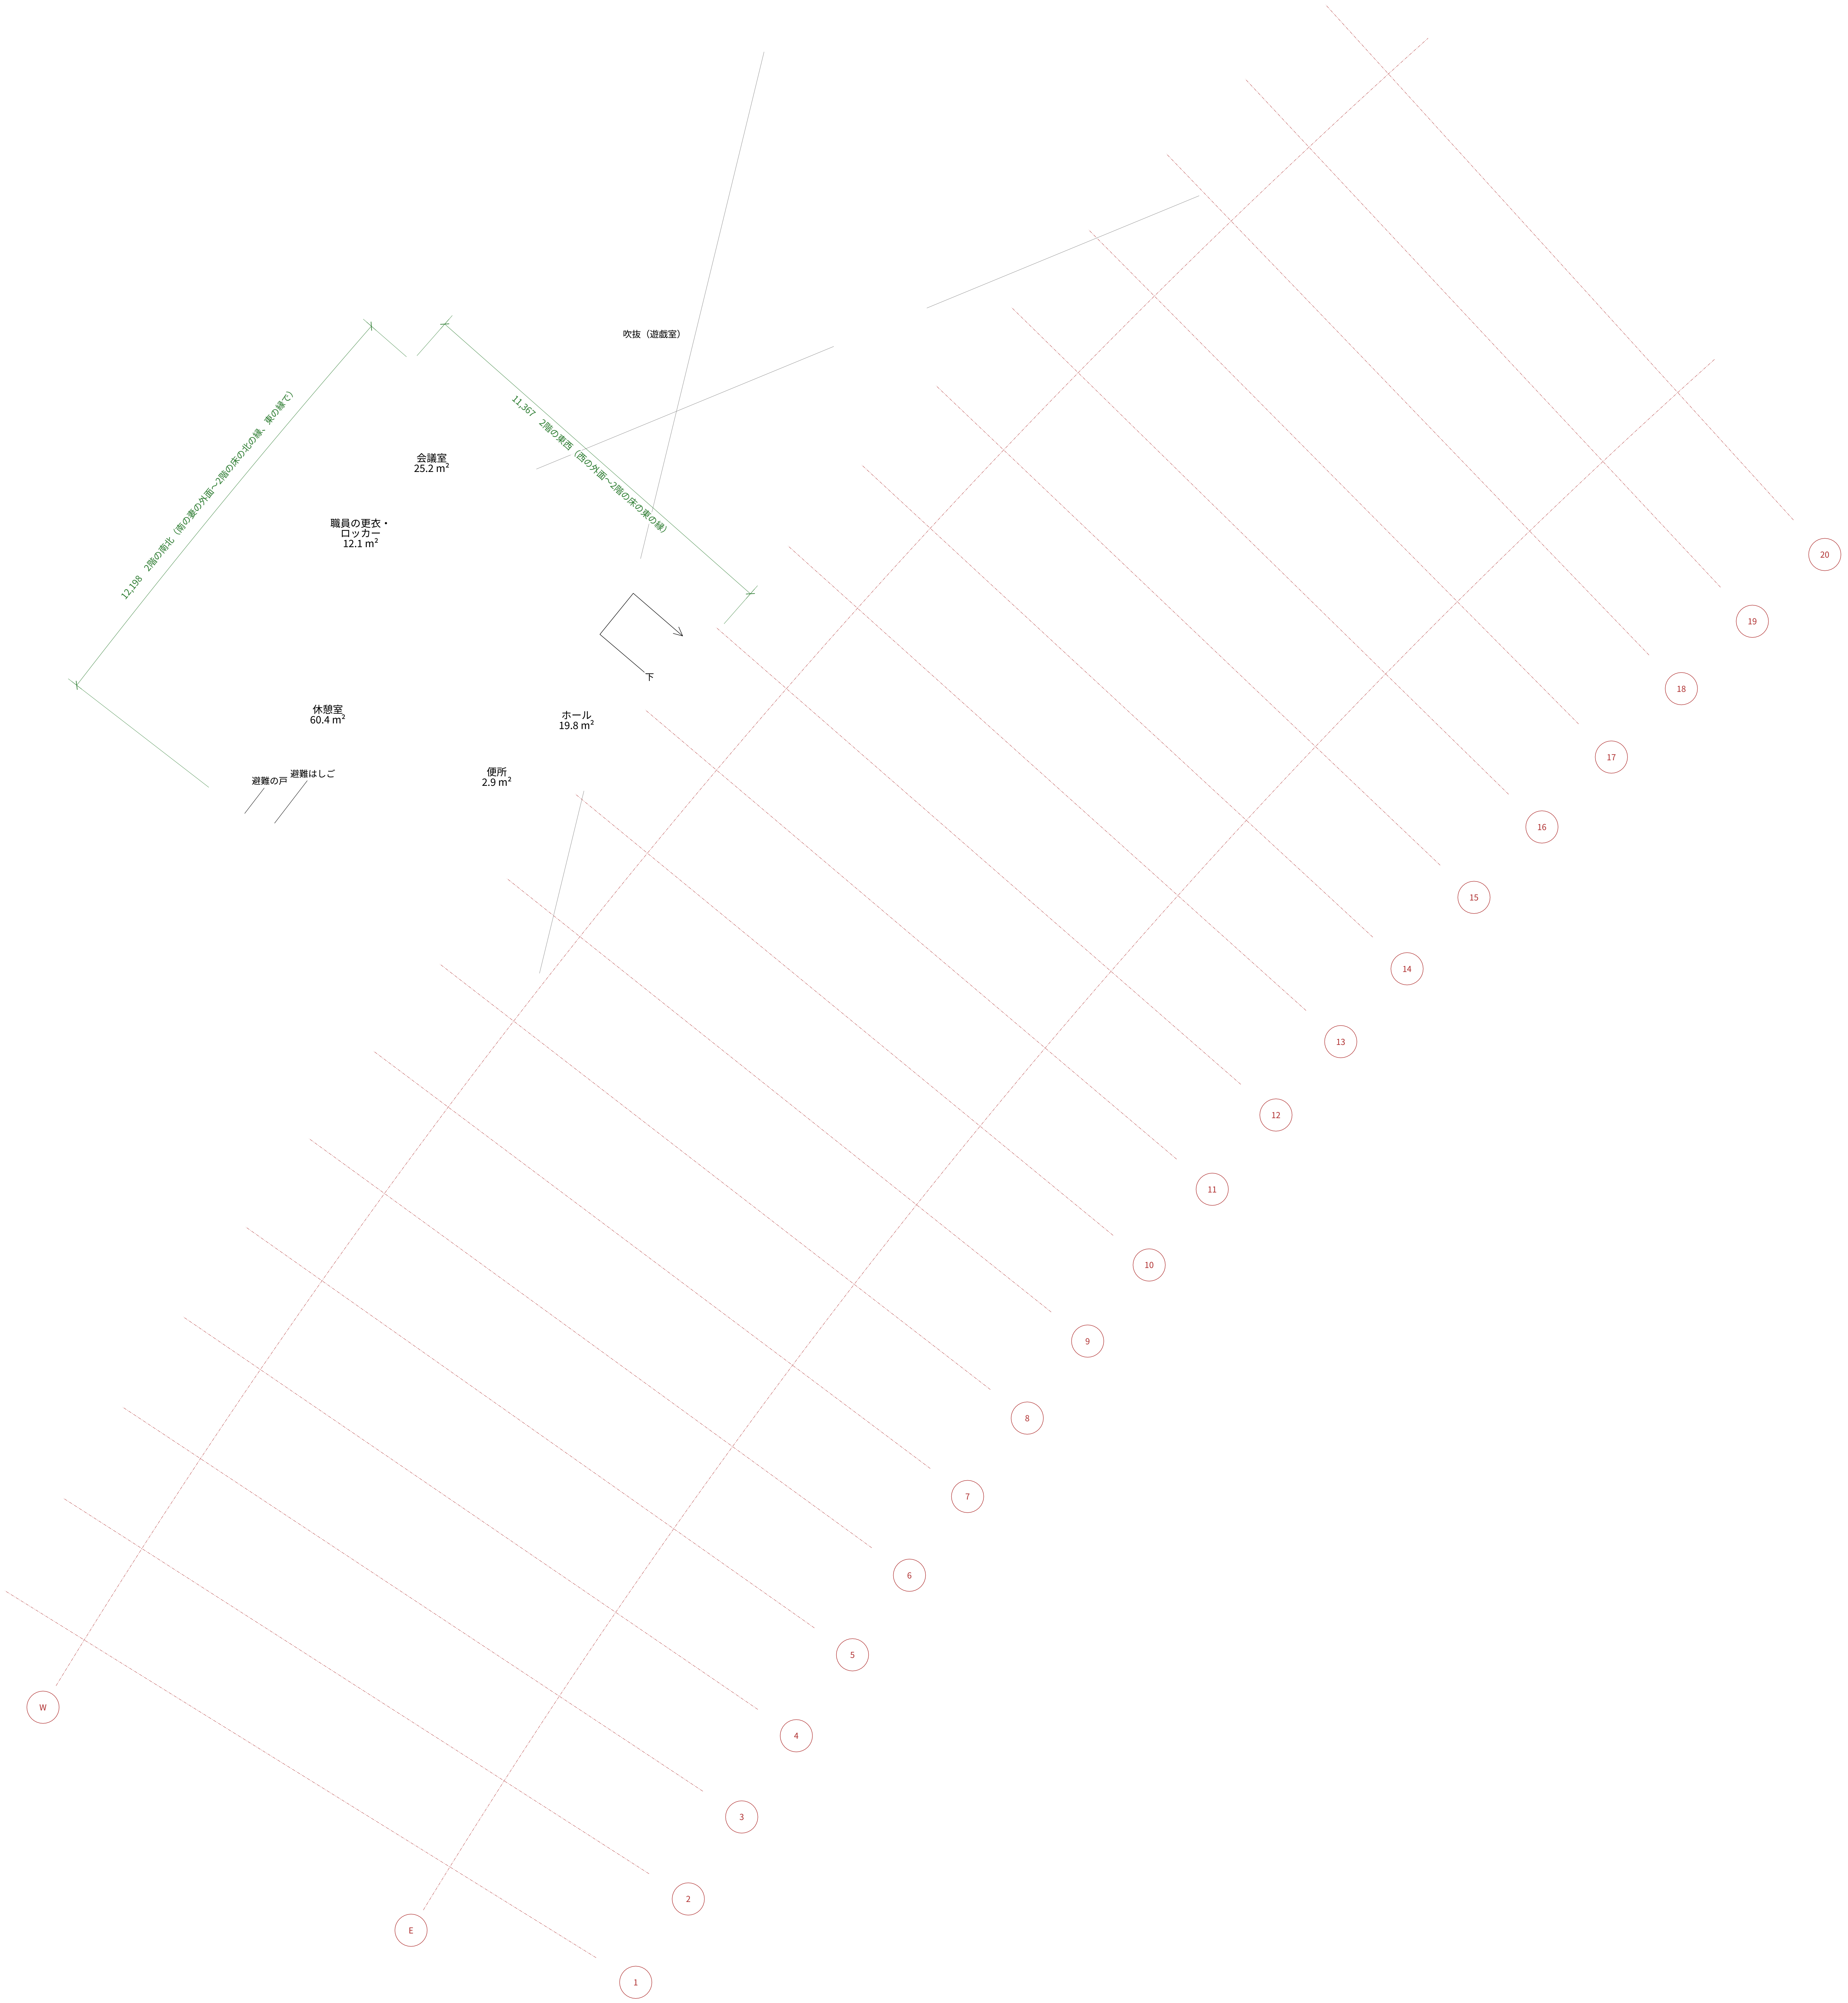

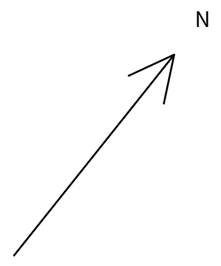

部屋の色

🟩	0・1歳～5歳
🟨	こどものみんなの場所（遊戯室・はれのま）
▨	通り・つなぐ場所（はだし）
🟫	土足の床
🟪	大人の場所
🟪	キッチン・調理の更衣
🟦	水まわり

こどもたちの育ち舎　3dm（sodachiya.3dm）から自動で作図　2026-11-01 15:36（atelier b35f15f の次の版の 3dm）