地に足をつけて育つ

　比叡から降りる冷気と高野川の流れが出会う松ヶ崎の扇状地に、こどもたちが地に足をつけて育つ場所をつくる。ゆるやかな弧を東の比叡にひらく木造平屋の本館に0歳から5歳のすべての部屋を並べ、縁側と深い庇で園庭とつなぐ。比叡に見立てた築山と、用水を借りて高野川に見立てた小川を置く。

　オープンキッチンを玄関ホールに面する園の中心に据え、食べることを日々の求心力とする。野菜くずをこどもの手で土に還し、命の循環を知る。園庭には季節ごとに香る木と実のなる木を植え、こどもたちは手と鼻と舌で季節を知る。

　3 mスパンの木造架構によるスケルトン＆インフィルで用途の変化を受け止める。LEED v5 Gold相当を目指す。地域から様々なものを借り、無駄をせず巡らせて、こども園として地域に返す。

設計趣旨 約332字（課題は300字程度）。文字3.6 mmなら1 m離れて読める

配置図の注

- 駐車5台・搬入は南（川側）。行事の日は駐車場を駐輪に
- セキュリティの線の出入口は公園の木戸だけ
- 園庭への搬入は公園の東の縁から川沿いの帯を通って
- 敷地の境から：北東の隣家1 m（厳守）、ほかは1 m

松ヶ崎の用水の網　高野川の堰から借りて、川へ返す

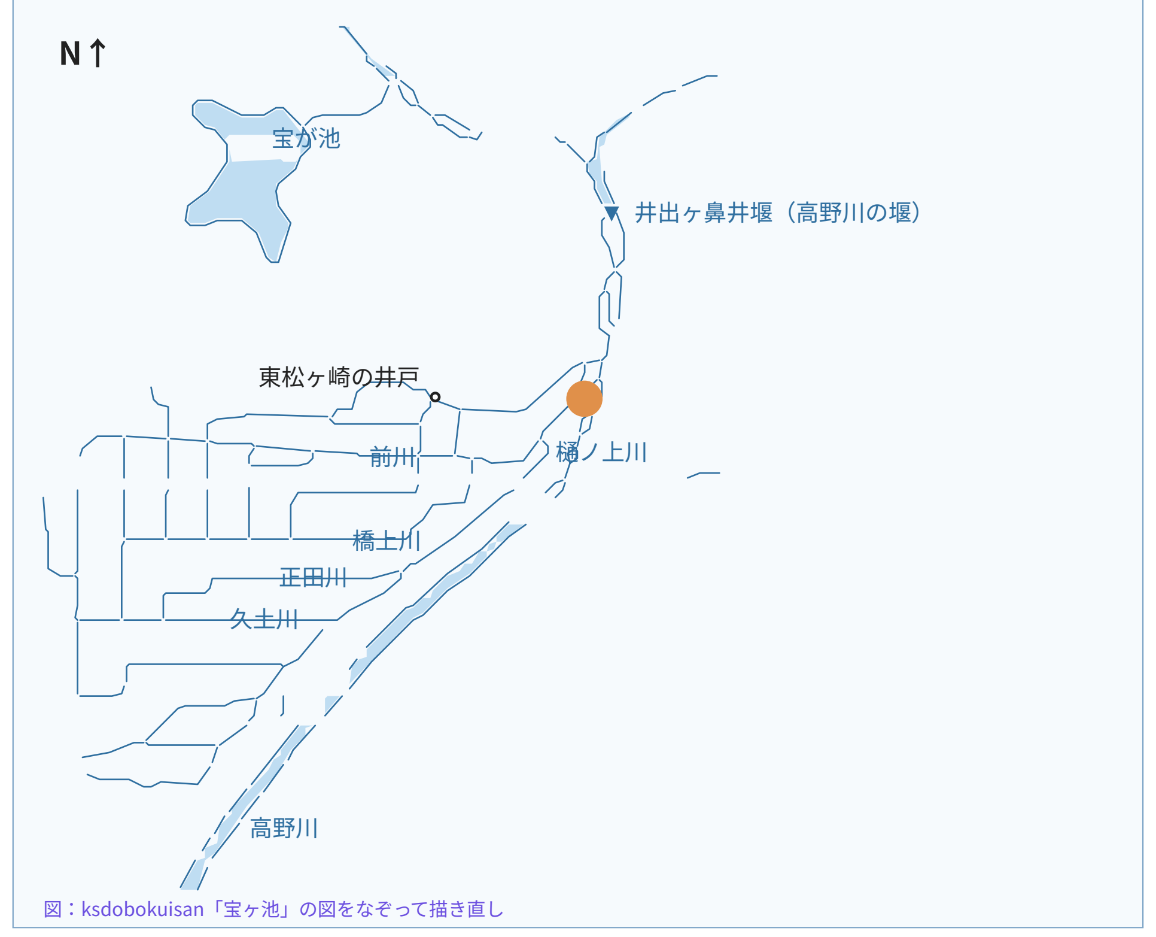

図：ksdobokuisan「宝ヶ池」の図をなぞって描き直し

配置図　1/200　高野川を下に（川向こうから見る向き、北は右上）

点線の枠＝園庭のチャットの配置1/200（garden01）を実寸で重ねた。本番は一枚に描き直す

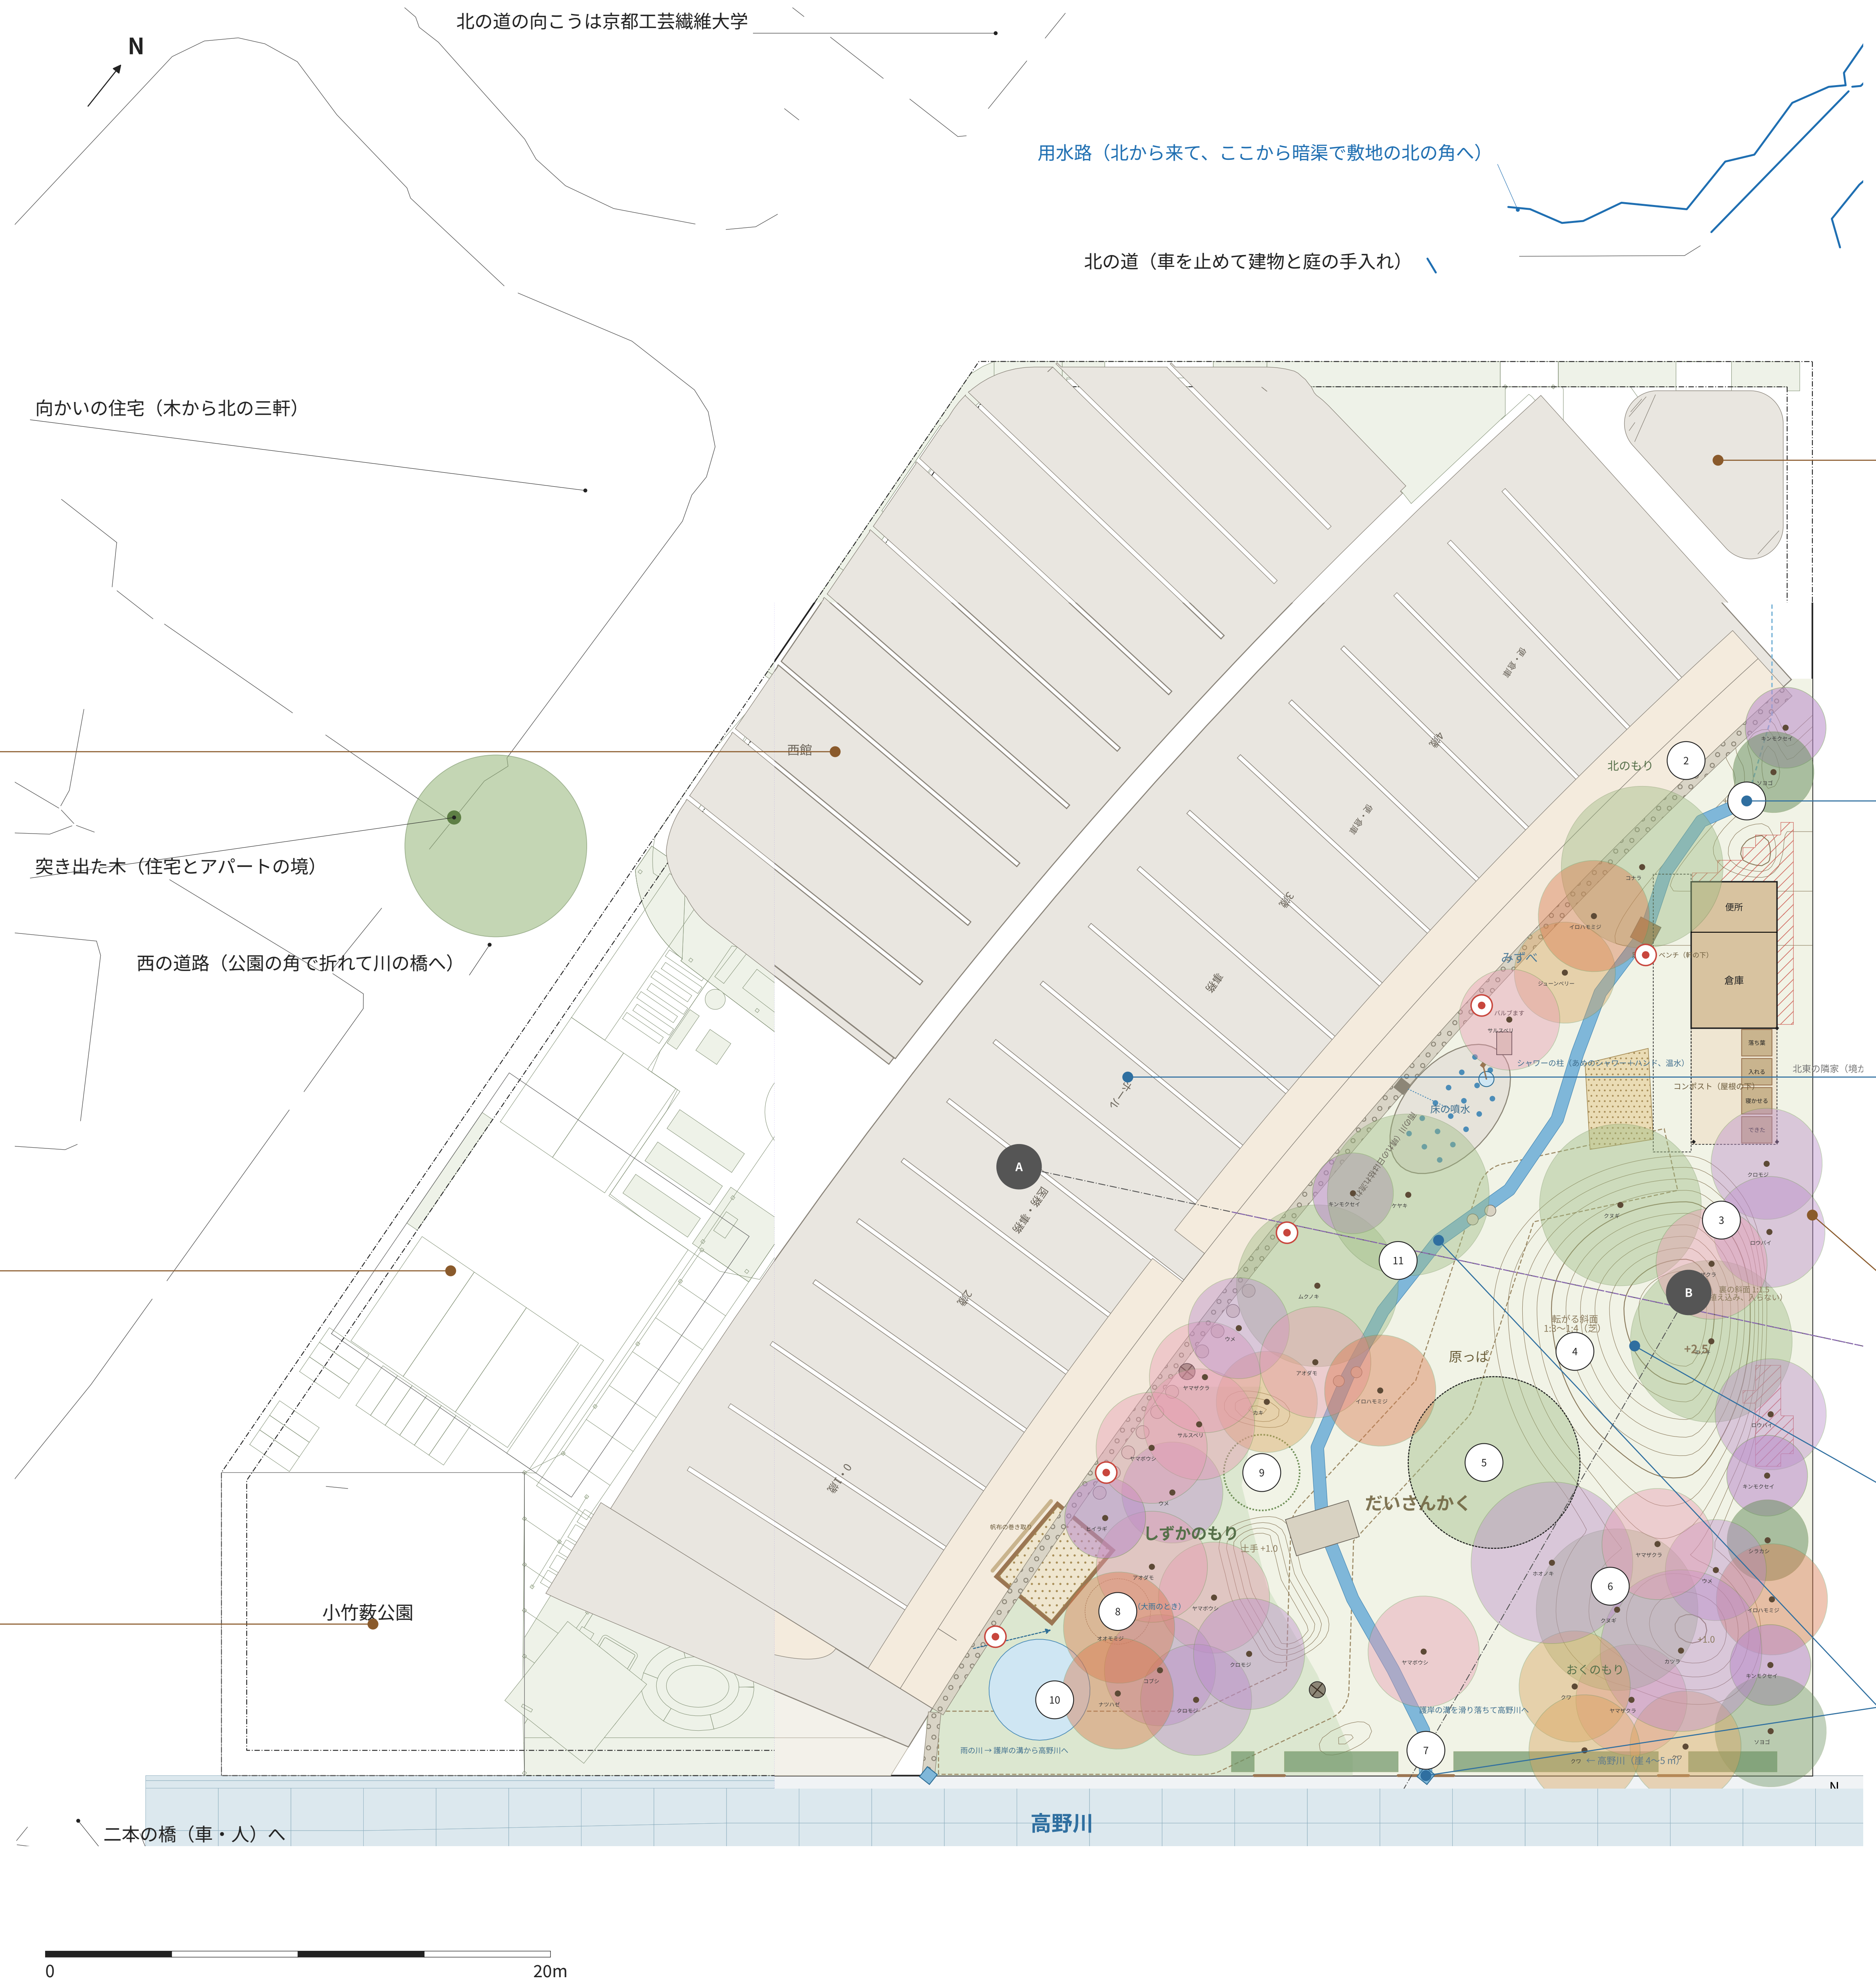

地域2　向かいの住宅へ
狭い道をはさんで向き合う住宅に対し、西館の西の端は1階の高さに抑えた。

地域1　車は西の道の真ん中より南で
西の道は突き出た木で見通しが悪い。外からの車の出入り（駐車・搬入）は、西の道の真ん中より南（川の側）にまとめた。

地域4　小竹薮公園を残す
地域の記憶の公園をそのまま残し、園の入口の前庭にする。

地域5　災害時に水を届ける
地下水をくみ上げて、災害時に近隣に水を届ける。屋根材型の太陽光と蓄電池で停電の時も動く。

自然1　用水を借りる
高野川の上の堰で取った水が、松ヶ崎の田を潤してきた用水の網を巡る。その水を借りる。
北の道の下の暗渠から敷地の北の角へ、北のもりのみなもとに湧き出し、小川になって高野川へ返る。

自然4　地下の水と北山の木を借りる
松ヶ崎は地面を走る用水と地下の水の両方が豊か。涌泉寺の井戸に見るように井戸水が豊富で、その地下水も借りる。
京都北山の北山杉の間伐材141本を、ホールの林に立てる。

地域3　東の隣家へ
視線と音に配慮：境から1 m、木の帯、園庭の小屋が声の衝立になる。

自然3　比叡と高野川のうつし
築山は比叡のうつし。ホールから頂の向こうに比叡が見える。
小川は高野川のうつし。足もとを掘った土で築山を盛る。

自然2　山から川へ
みなもとから縁側の前・原っぱを流れ、護岸の溝を滑り落ちて高野川に合流するまでを、こどもが追える。
雨は樋に隠さず、雨の川から同じ溝で川へ。

［割付の注記］フォーカス：周囲の自然環境との関係（用水を借りる・山から川へ・比叡と高野川のうつし・北山杉と地下水）と地域環境への配慮　／　目に入る順：タイトルと趣旨 → 真ん中の配置図 → 左右の箱（青＝自然環境、茶＝地域）→ 用水のネットワーク

こどもたちの育ち舎　2/5　景観

建築設計実習 II — I　2026.11.05　木田

沿川の景観立面　昼　1/300　高野川の向こうから（川の辺に直角）、周りの建物とともに

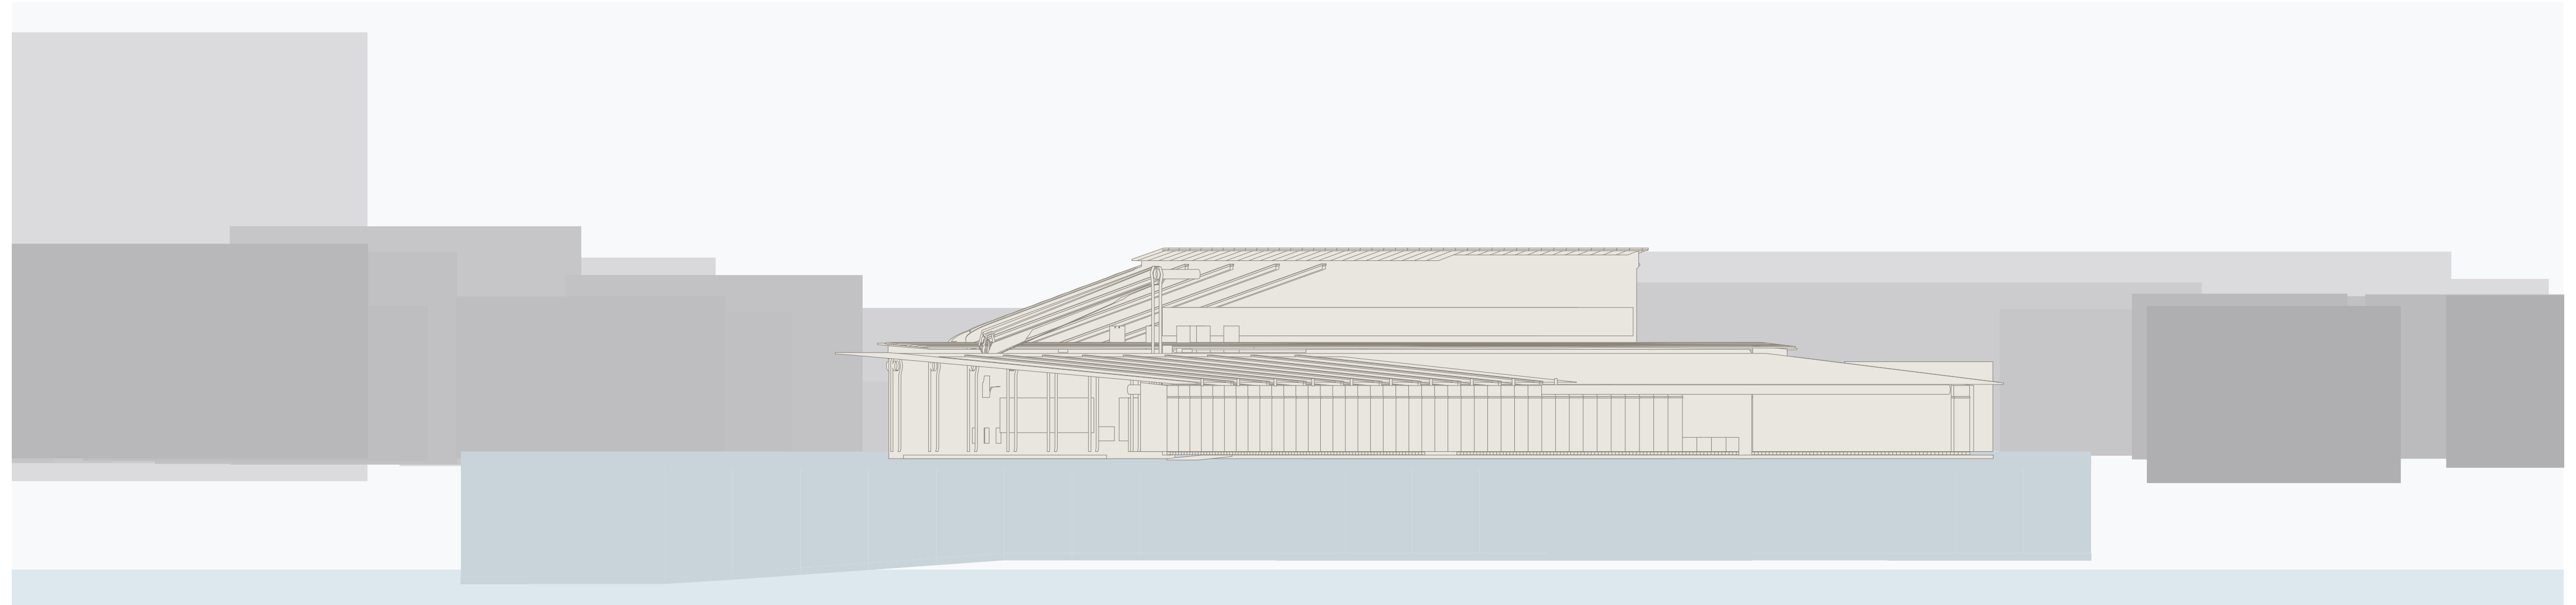

夜　越屋根の東の縁の光が水平に一本

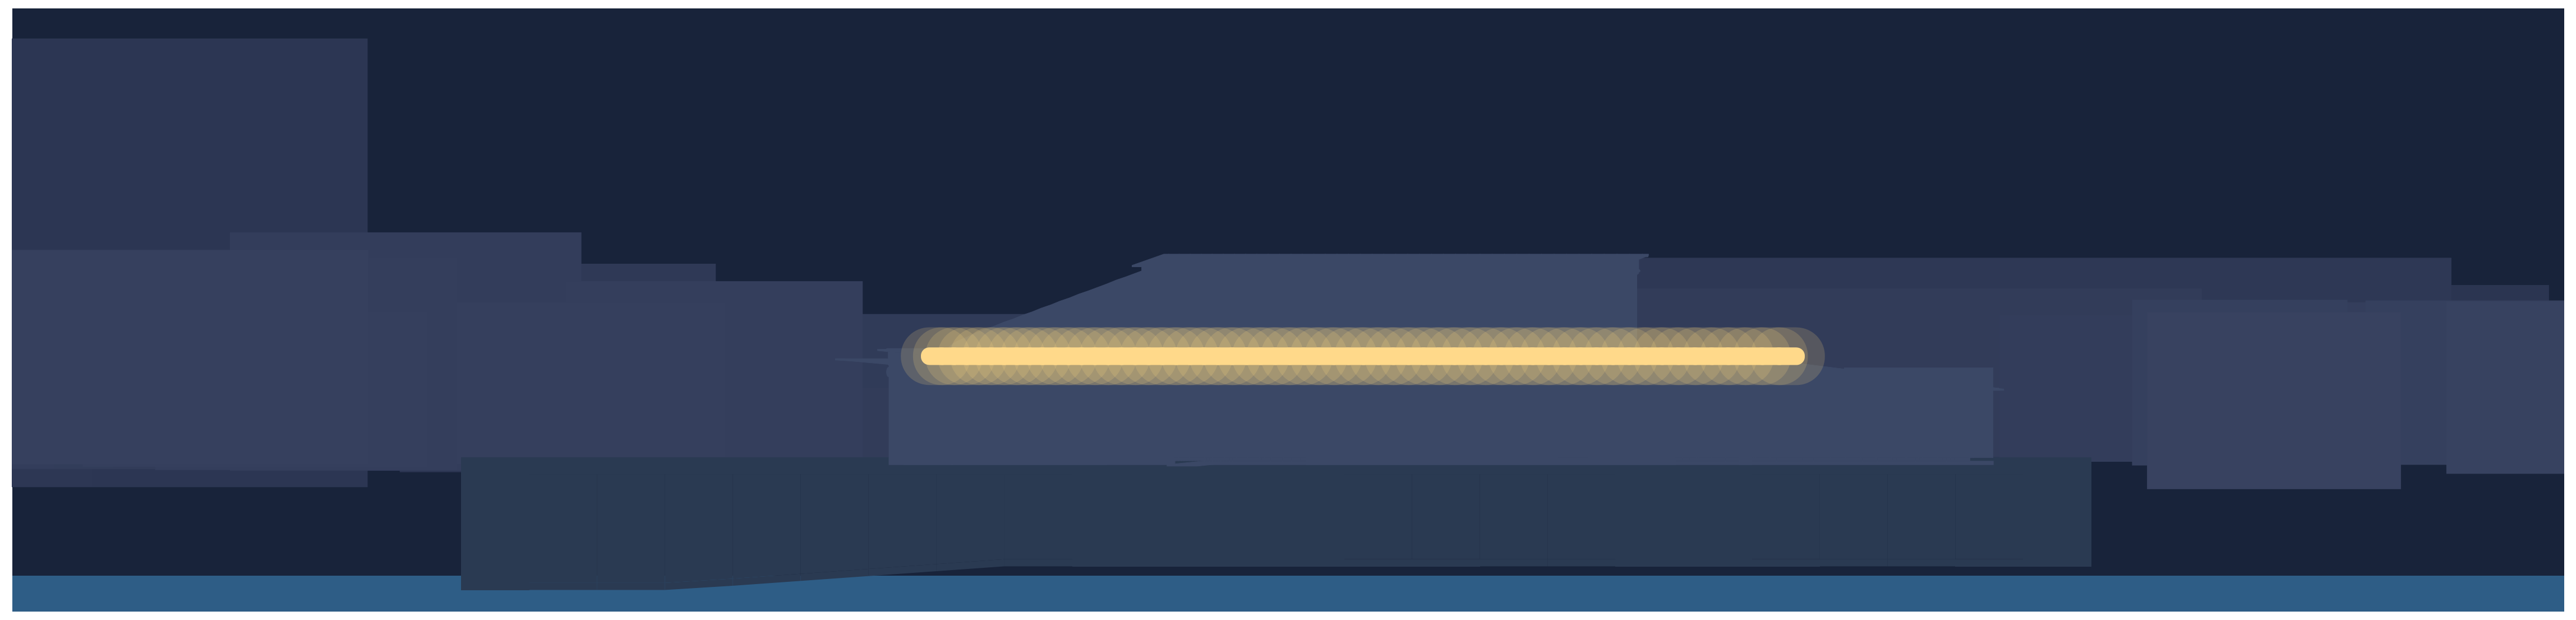

川側は低く
北の大学へ高く
（周りの建物は
PLATEAUの箱）

園庭の側の立面図　1/100　円弧の中心の方向から弧の真ん中に正対

伸びやかな梁と縁側（梁の端・庇が3 mごとに並ぶ）。屋根は屋根材型の太陽光

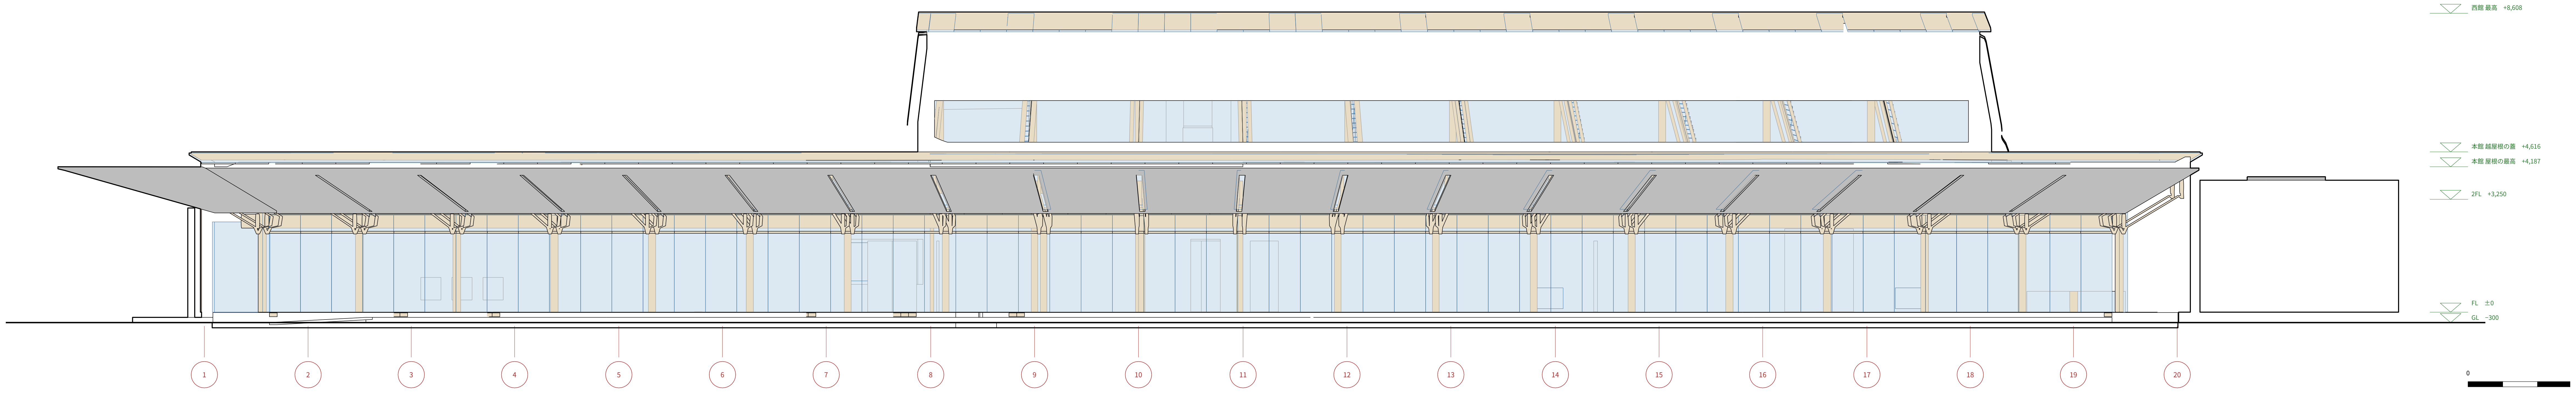

道路の側の立面図　1/100　西の道路から

西館の西端は1階の高さ（向かいの住宅）。西館の立ち上がりが北で主張する

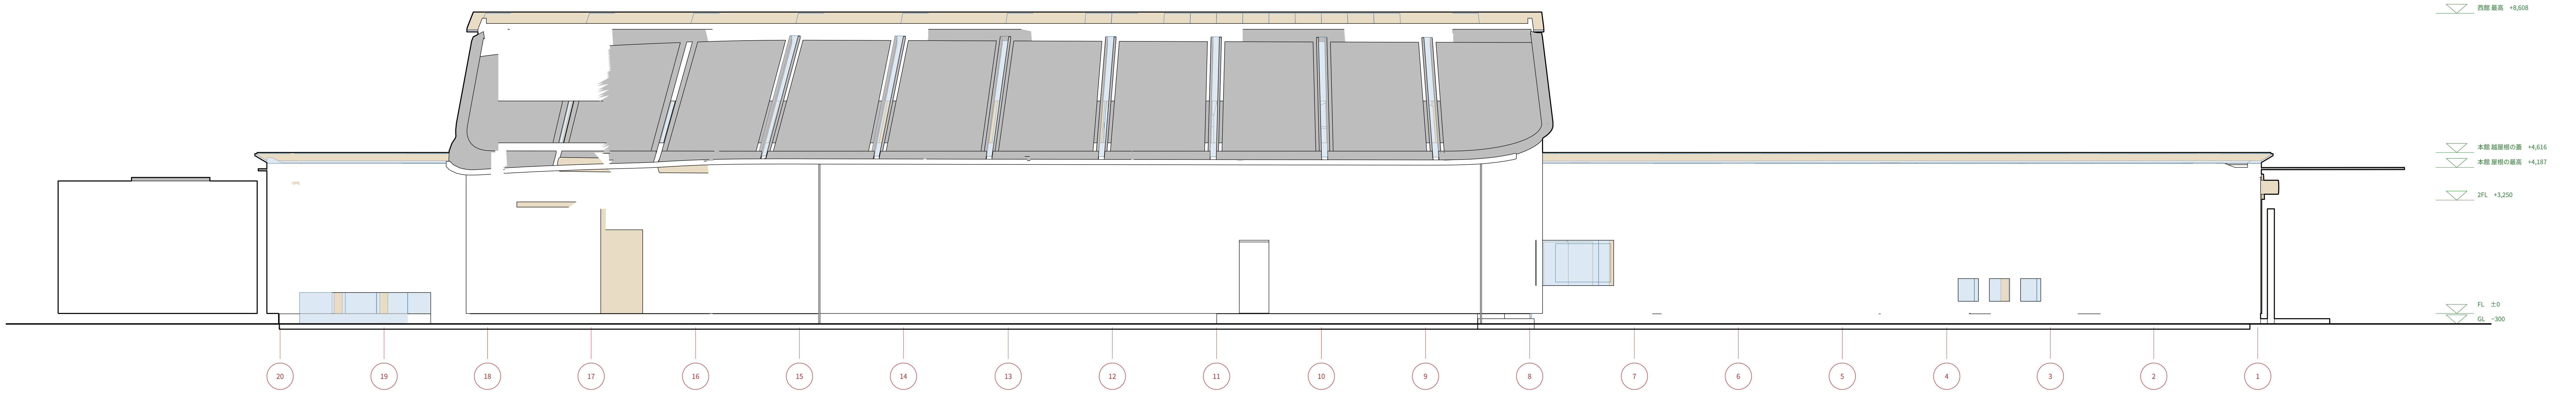

模型写真　鳥瞰
配置図と同じ向き（高野川を手前）
川側が低く北へ高くなる流れが見える角度で

景観の約束

第一種低層住居専用地域。西館の棟は約8.5 m（GLから）。

高野川特別修景地域（右岸）：河岸の樹木と清流が一体の水と緑の空間。川に面する側に植栽帯（園庭の林と生垣）、川に面する側に勾配のある下屋（南の深い軒）と和風の外観（深い庇、木の柱・梁とスギ板、ゆるい勾配の屋根）。

遠景デザイン保全区域（高野川・修学院離宮・船岡山公園からの眺め）：外壁と屋根に禁止色を使わず、山並みと調和する色（黒い金属の屋根、木の色のまま）。

小竹薮公園と既存の木を残す。

素材と色

- ■ 北山杉の柱・梁（木の色のまま）
- ■ スギ板の外壁
- ■ 屋根：黒い金属（屋根材型の太陽光）
- ■ 越屋根のガラスの蓋・縁側の白
- ■ 生垣と園庭の緑

［割付の注記］フォーカス：高野川の側は低く、北の大学に向かって高く（地域の高低差の流れ）。同時に、伸びやかな梁・西館の立ち上がり・夜の水平の光で主張する　／　目に入る順：沿川の景観立面（昼・夜）→ 園庭の側・道路の側の立面図 → 鳥瞰・景観の約束・素材と色

こどもたちの育ち舎　3/5　平面図　1階・2階

建築設計実習 II ― I　2026.11.05　木田

1階平面図　FL+1200 で切断　1/100　（右が北の端、下が園庭）

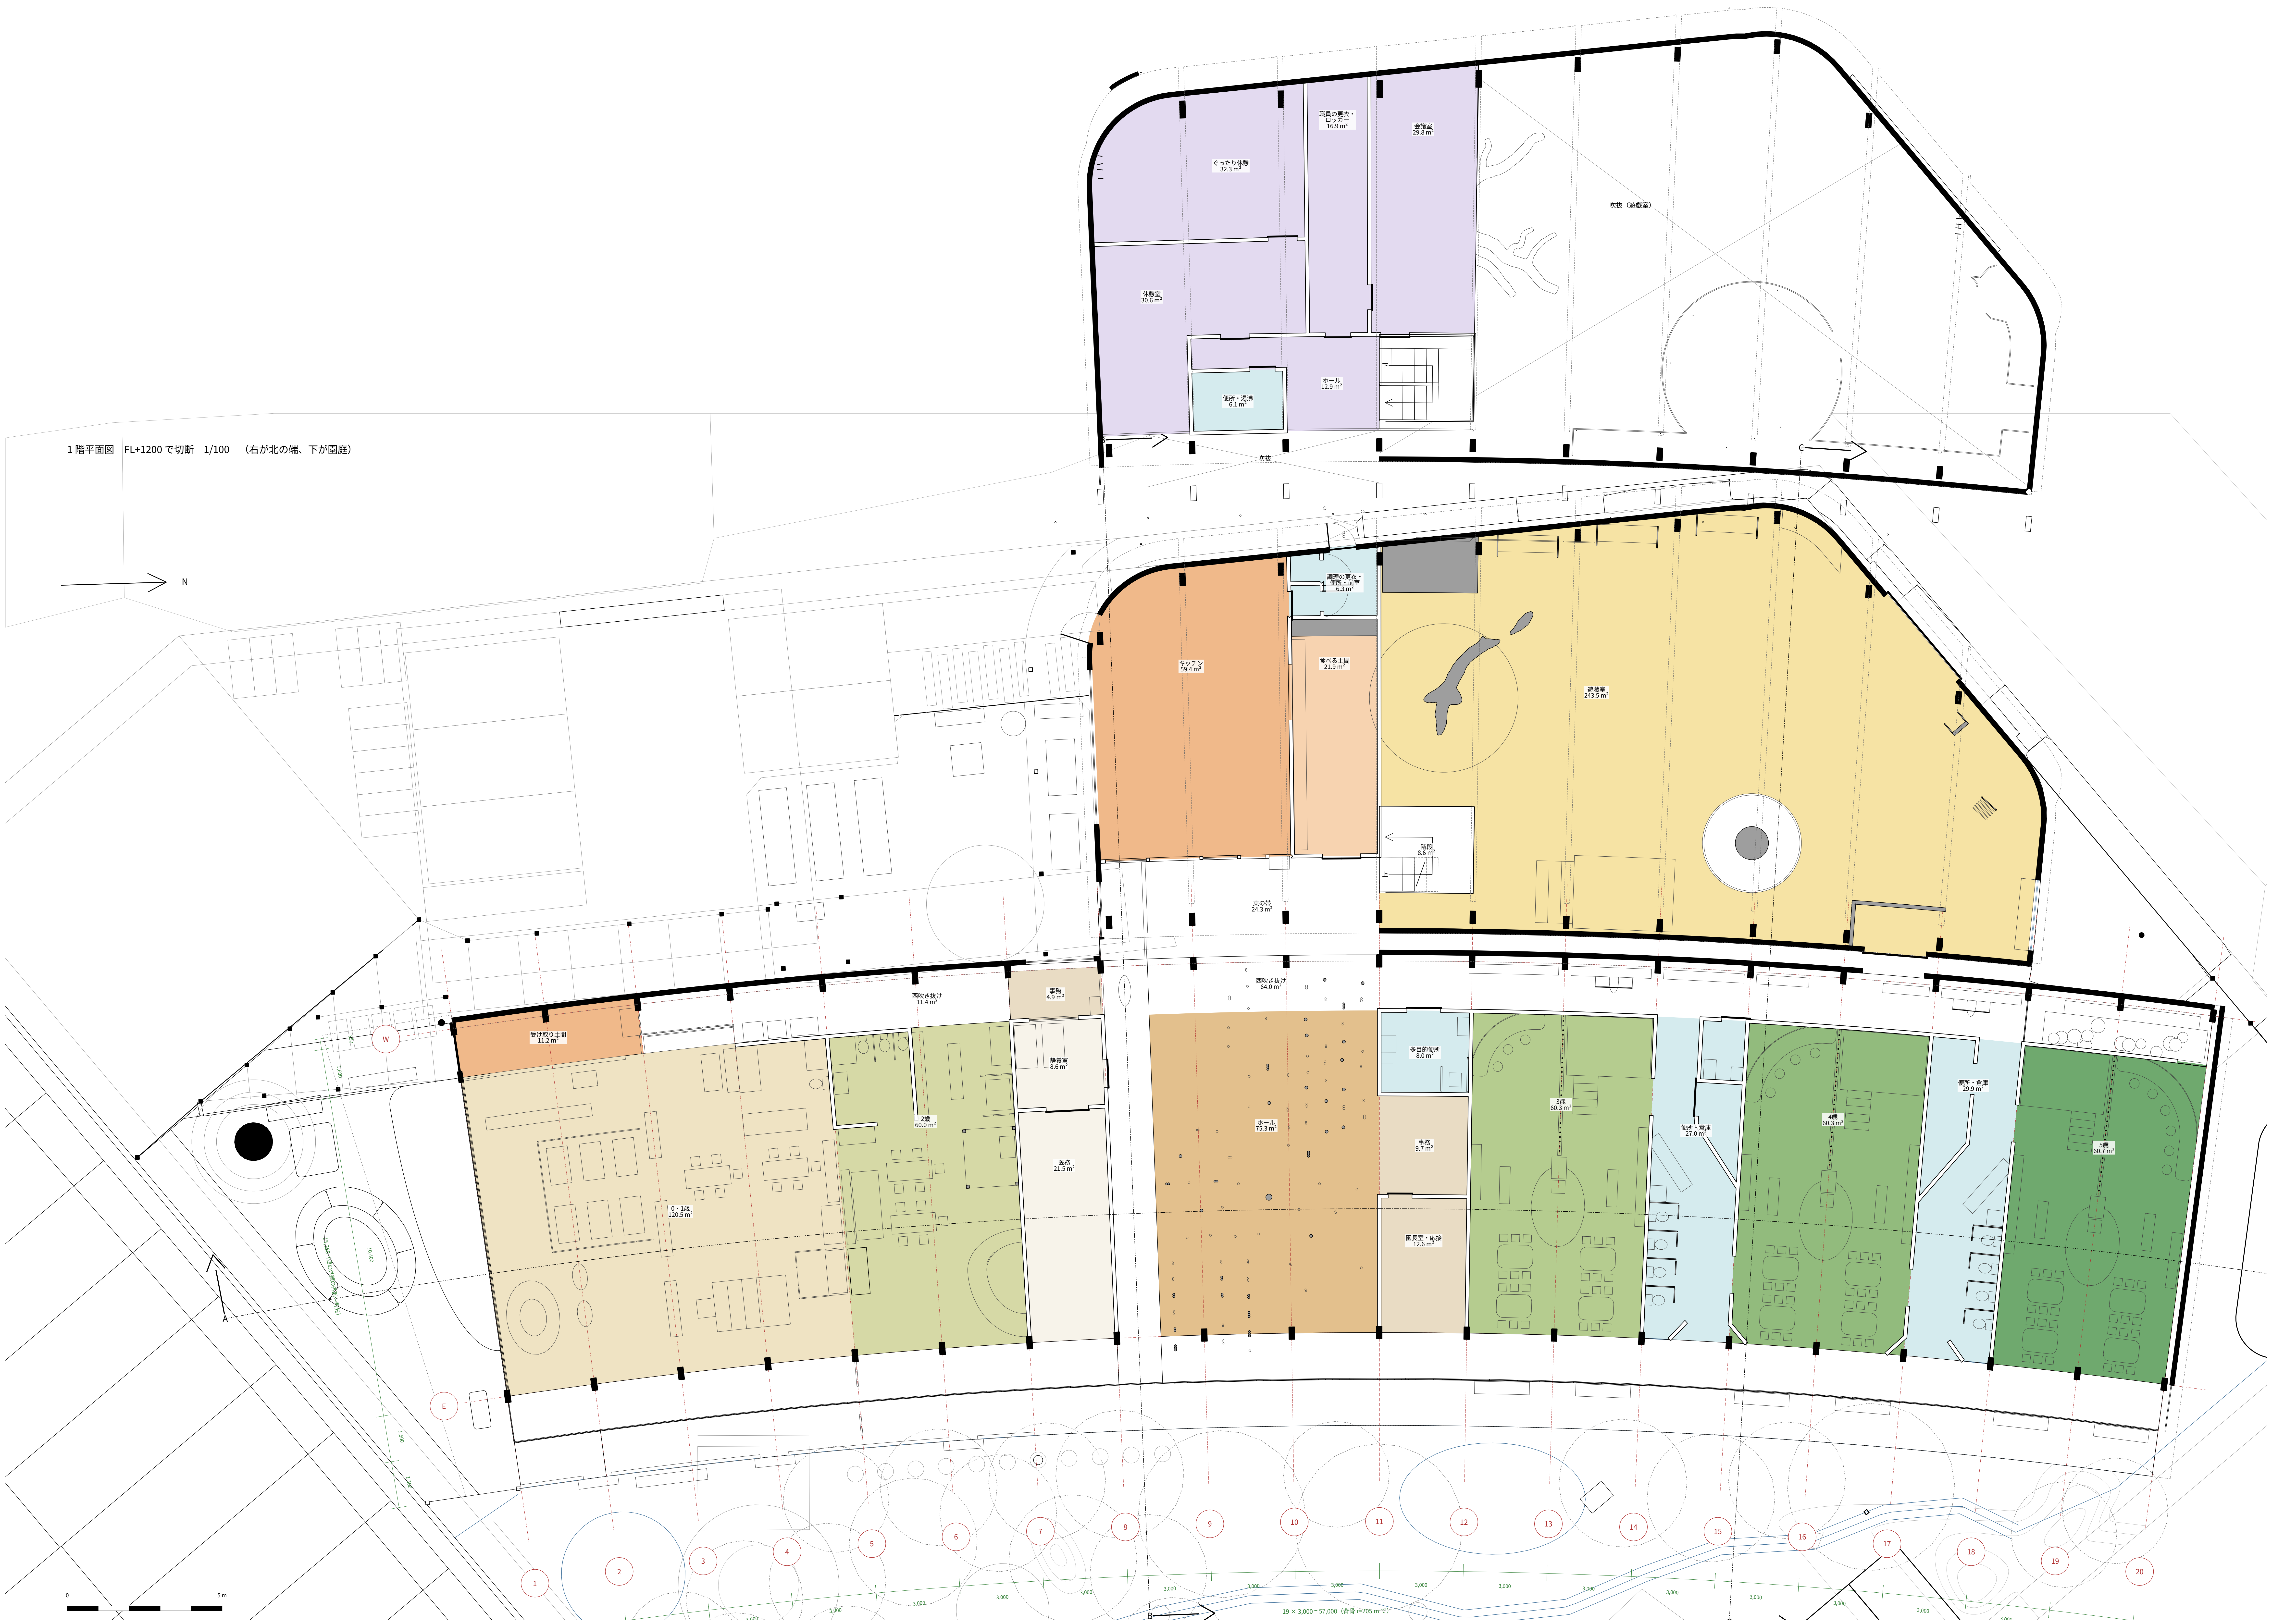

面積表　m²（壁芯、3dmから自動）

室	要求	計画
乳児室（0〜1歳）	約60×2	120.5
保育室（2歳）	約60	60.0
保育室（3〜5歳）	約60×3	181.3
遊戯室	240以上	243.5
便所	適宜	57.3
食堂	必要に応じて	21.9
園庭	350以上	982.2
事務室	約60	73.8
休憩室	約60	62.9
医務室	約30	30.1
調理室	約60	65.7
便所（大人用）	適宜	17.1
機械室	約30	30.0
駐車場	5台以上	○
延床（2,000以内）		**1,286.7**

色

- 🟩 0・1歳
- 🟩 2歳
- 🟩 3歳
- 🟩 4歳
- 🟩 5歳
- 🟨 遊戯室・はれのま
- 🟫 通り・ホール
- 🟫 土足の通り
- 🟪 大人の場所
- 🟪 キッチン
- 🟦 水まわり

平面は3dmから自動（1/100）。
道路・隣地の線と色は更新係へ依頼中

［割付の注記］フォーカス：すべての人の場所：こどもの部屋（緑）・みんなの場所（黄）・通り（木の色）・大人の場所（青紫）を色で。道路と隣地の線も　／　目に入る順：1階・2階の平面（1/100、家具）→ 面積表と色の凡例

こどもたちの育ち舎　4/5　こどもたちと働く人たちの環境

建築設計実習 II — I　2026.11.05　木田

一日の帯：上は1/700の小さな配置（建物＋園庭）と三者の動線（こども緑・保育士茶・調理青）、下にそれぞれの一日

登園 8:00

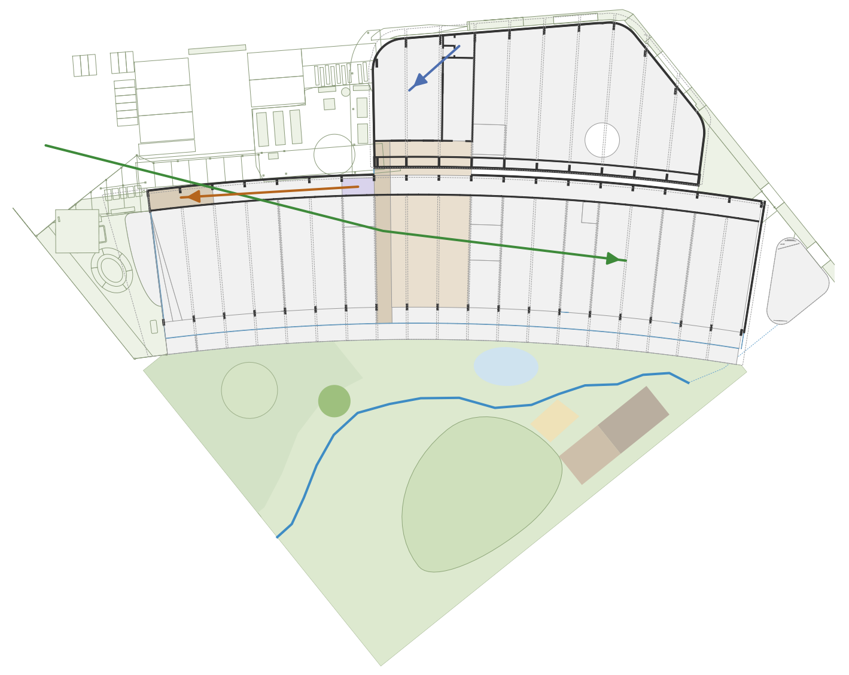

こども公園→木戸→小径→海峡。0・1歳は受け取り土間

保育士おはようの窓口で挨拶、受け取り土間で手渡し

調理　検収と下処理（南のガラス越しに見える）

外で遊ぶ 9:30

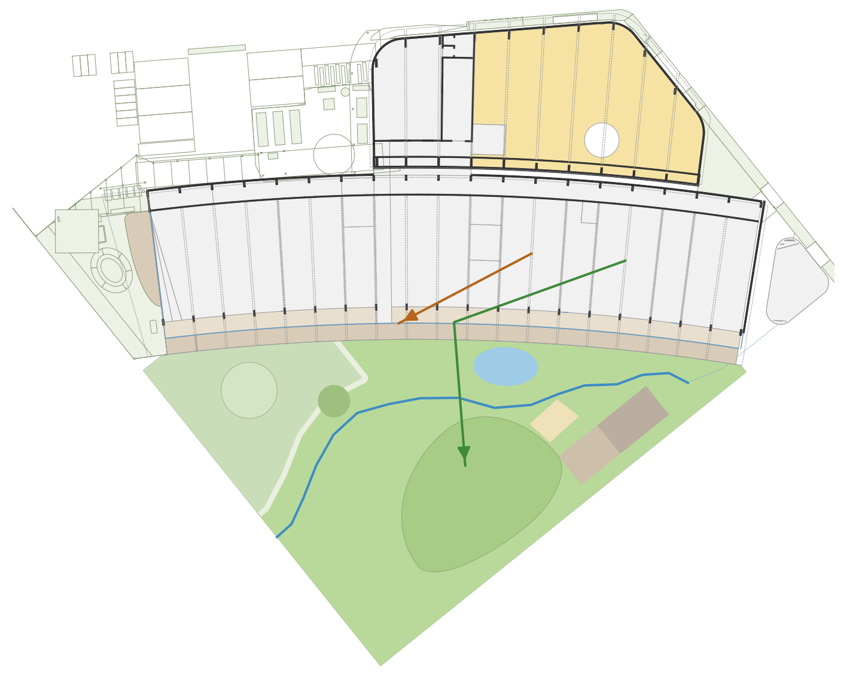

こども3〜5歳はだいさんかく、0〜2歳はしずかのもり

保育士縁側の縁に腰掛けて庭全体を見る

調理　仕込み。今日のごはんの窓にこどもが寄る

食べる 11:30

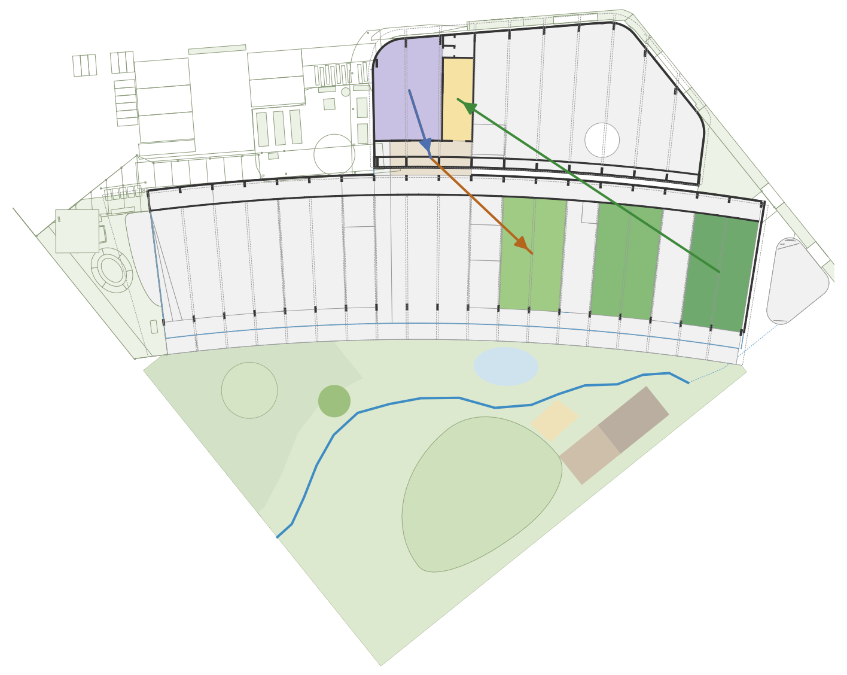

こども保育室の食卓、はれのまでクラスごと

保育士配膳口から飛び石を渡って配る。いっしょに座って食べる

調理　オープンキッチンでこどもと目が合う

寝る 12:45

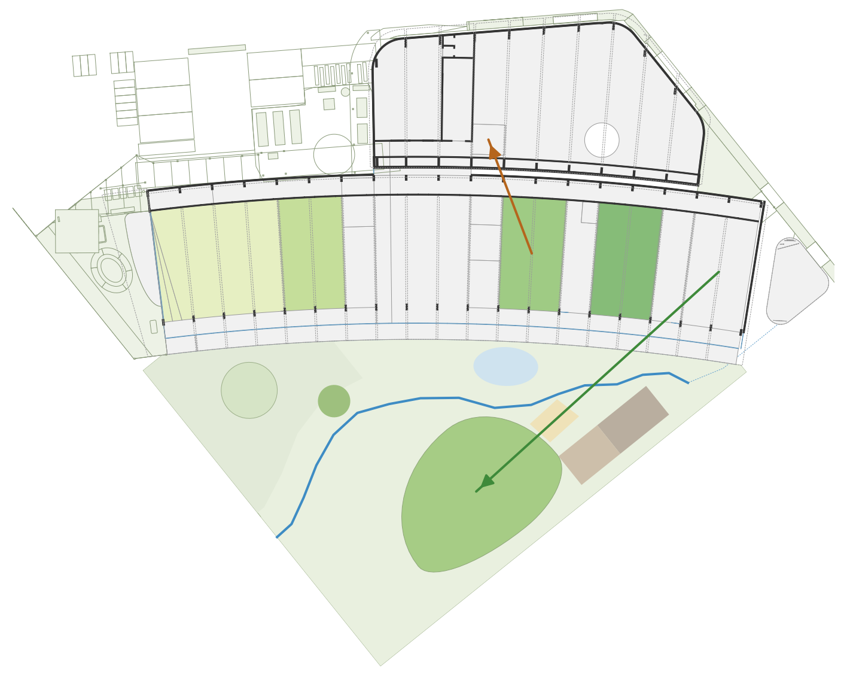

こどもねどこ・ロフトの下。起きている5歳は北の築山と遊戯室

保育士交代で2階の休憩室へ（こどもから離れる）、記録の机

調理　片付けと洗浄、おやつの仕込み

当番 15:00

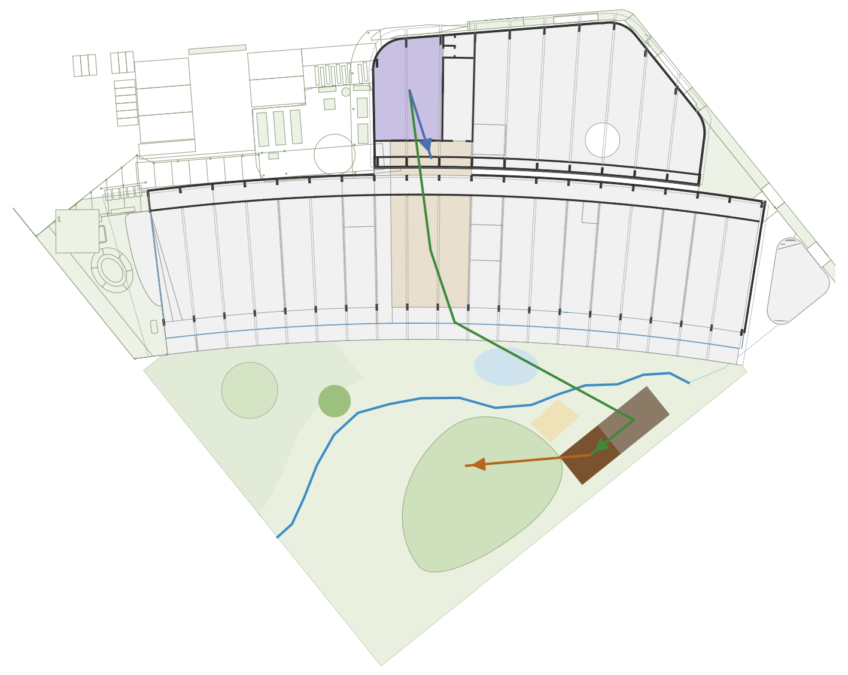

こども4・5歳のコンポスト当番：キッチン→小屋

保育士当番に付き添い、できた土を菜園へ

調理　受け取り台で野菜くずを渡す、はれのまでおやつ

降園 16:30

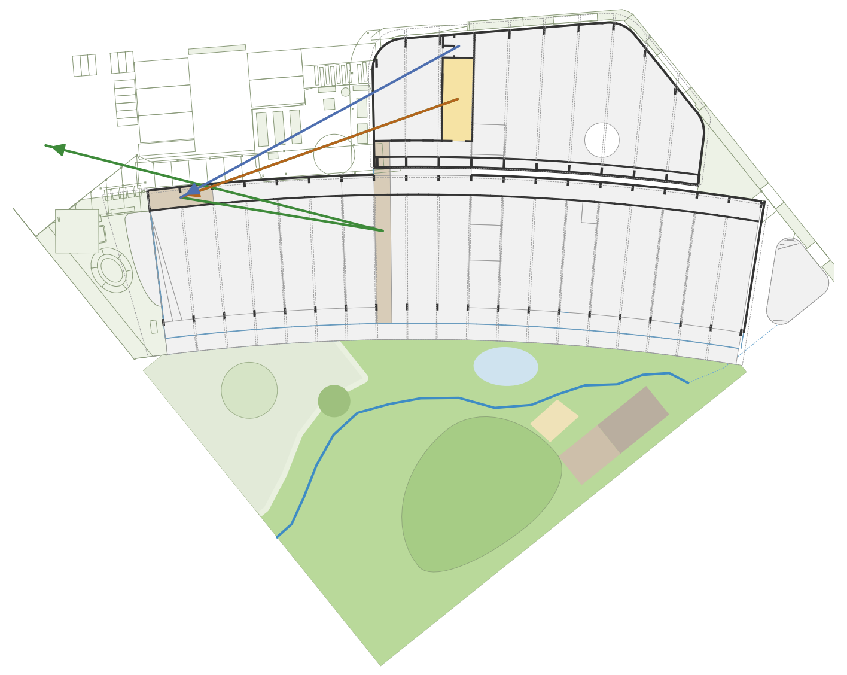

こどもはれのまで延長保育、迎えを待つ夕方の園庭

保育士縁台でお茶をしながら保護者と話す、2階で会議

調理　職員の通用口から帰る

透視図（A4）　模型写真か彩色の透視図
こどもの目の高さで、園庭から縁側とホールの北山杉の林を見る
梁の見える天井・光の筋・オープンキッチン

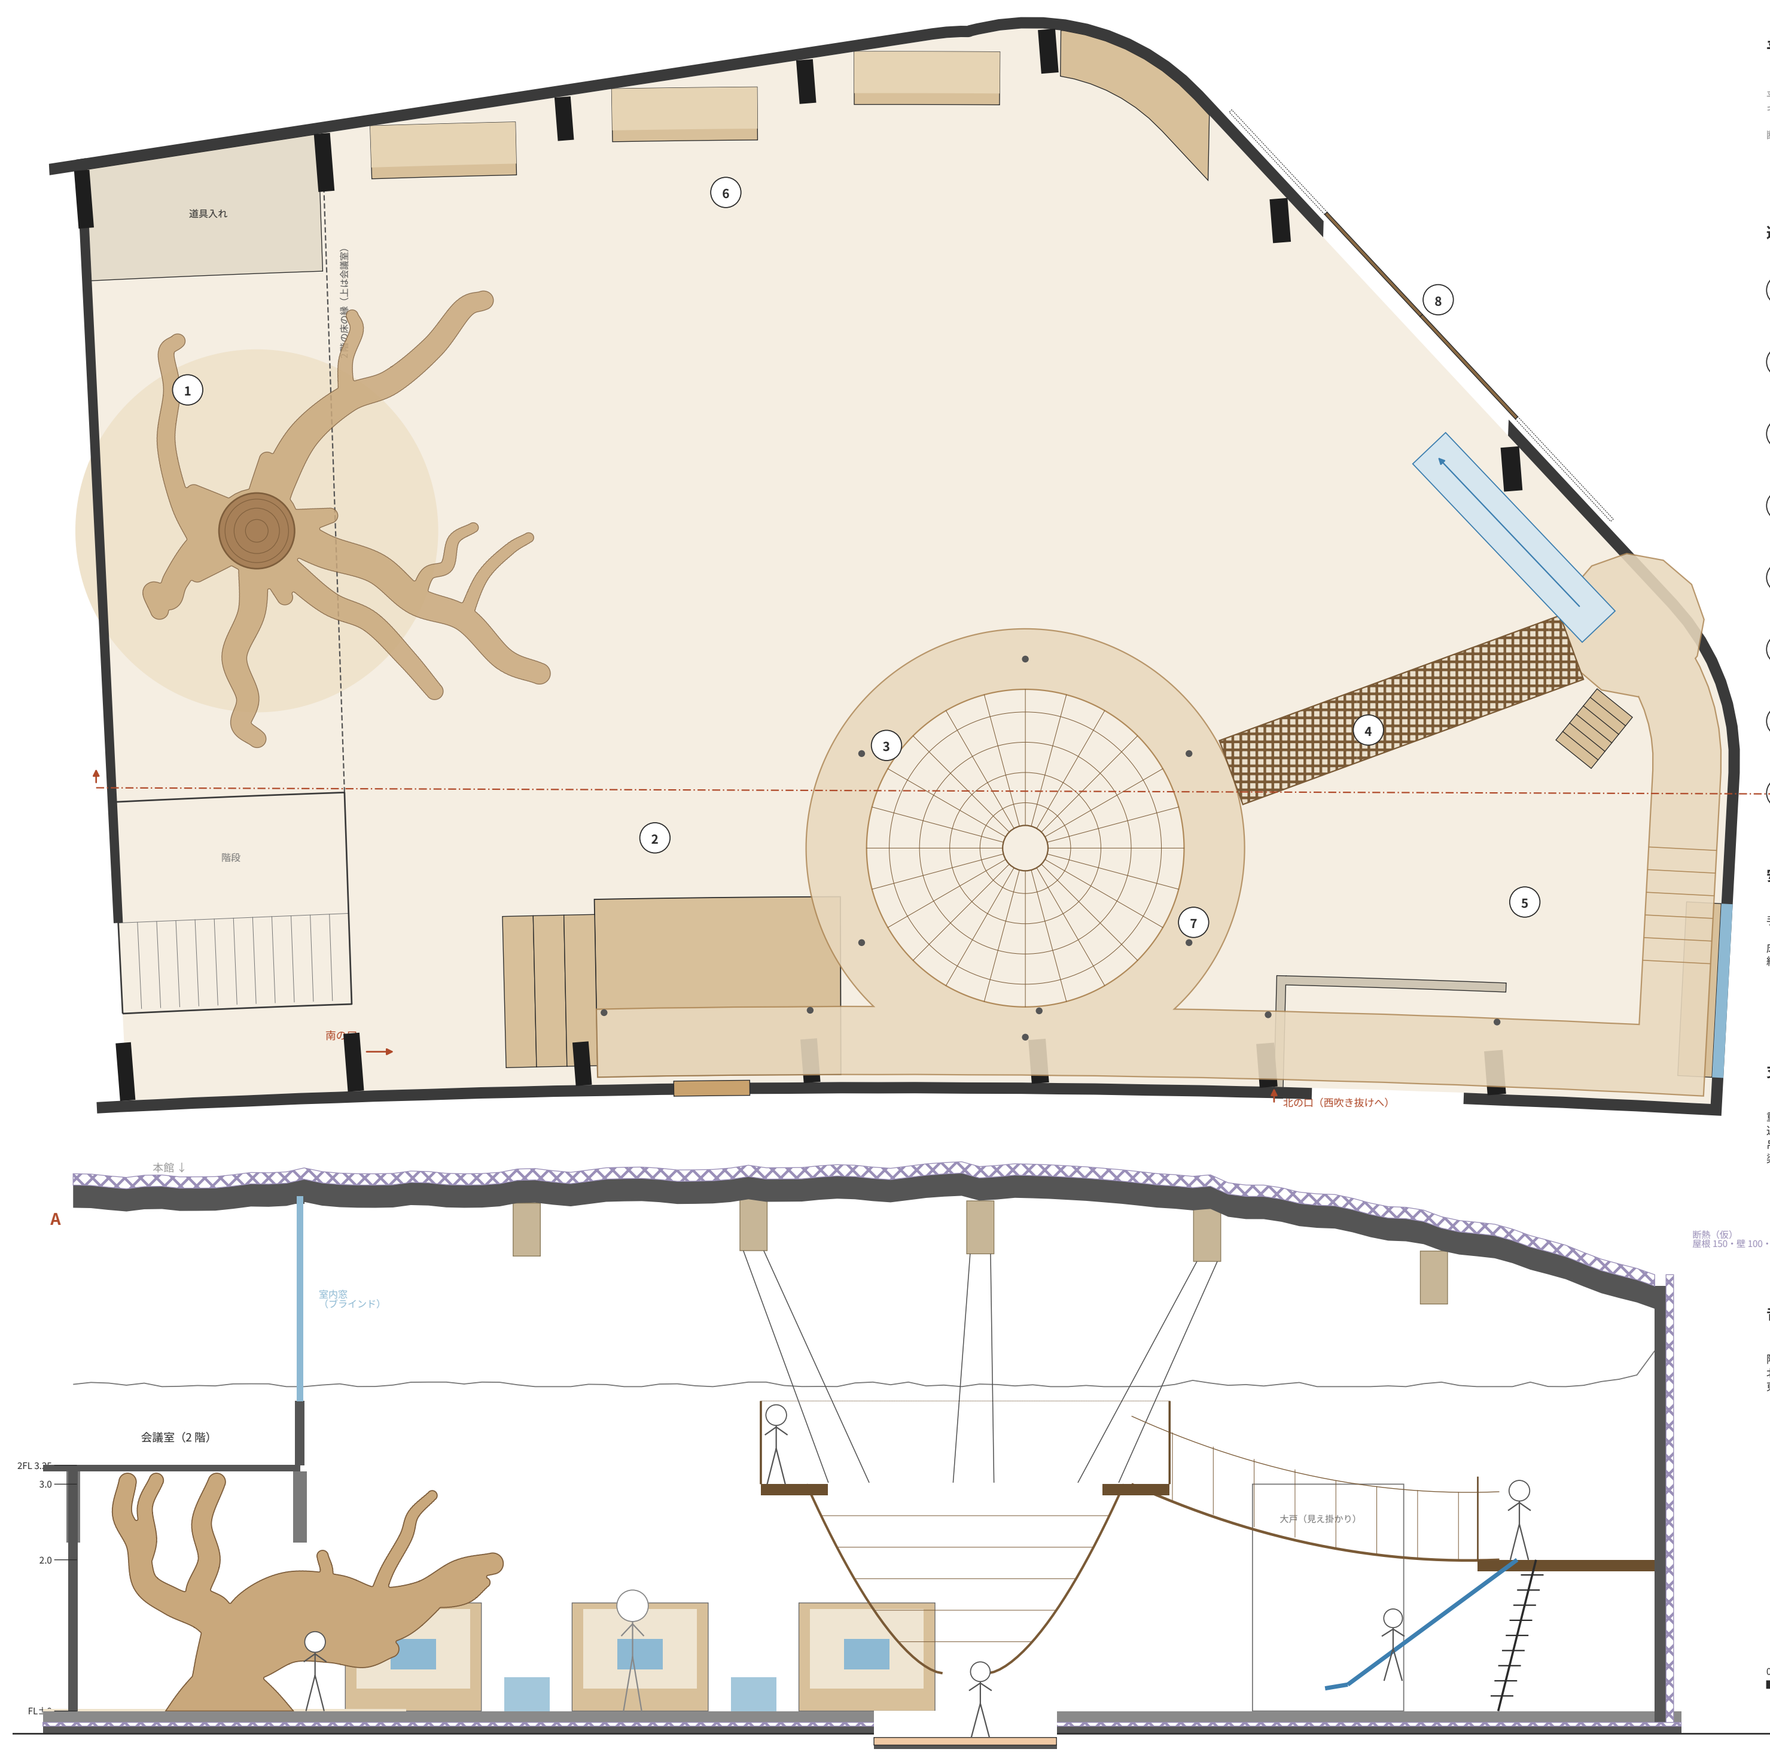

平面・断面 A 1/100

平面は FL+1.2 で切る。淡い茶は
キャットウォーク・輪・踊り場
（h3.0／2.0）、黒い点は吊り材。
断面 A は東から 4.3 で切って西を見る

遊び方

① 洞とクスノキ
てっぺんが 2 階の床に届く

② デッキと登り壁
→ キャットウォーク h3.0

③ 擂鉢ネットと穴の底
ネットからも輪へ登れる

④ 輪 → 網の吊り橋 → 踊り場 h2.0
空中で一周する

⑤ 北の段 3.0→2.0・はしご・
すべり台（落下 2.0 m 以下）

⑥ ひだ：くぼみ・丸いベンチ・
窓辺の腰掛け（モミジを見る）

⑦ 北の口のついたて（吸音）

⑧ 搬入の大戸（外付けの引き戸）

安全

手すりは縦格子 h1.1・すき間 90
（頭が通らない、横桟なし）
床の板のすき間 8 未満
網目 上 90・下 50、ロープ φ18

支え方

重さは梁から吊る（梁のあいだを
通す）。横の揺れは壁とハの字の
吊り材で止め、吊り橋だけ揺れる。
梁 90×700×2 は満員でも持つ
（略算：曲げ 8.0／11.0 N/mm²）

断熱（仮）
屋根 150・壁 100・床 50

音

階段の箱がホールとの衝立。
北の口に吸音のついたて、
東の覗き窓は夜だけ開く

見立て

築山は比叡、小川は高野川。足もとを掘った土で盛る。

水の行方を隠さない

用水→みなもと→小川→護岸の溝→高野川。雨は樋なしで。

土と命のめぐり

野菜くずはこどもの手でコンポストへ、土に還す。ミミズに驚く。

季節を手と鼻と舌で

季節ごとに香る木と実のなる木。とげの木は一本だけ、わざと。

静かな場所と先生の目

関守石で「ここからはしずかに」。取り除くのは命に関わる危険だけ。

園庭　約1/440（配置1/200を縮小）

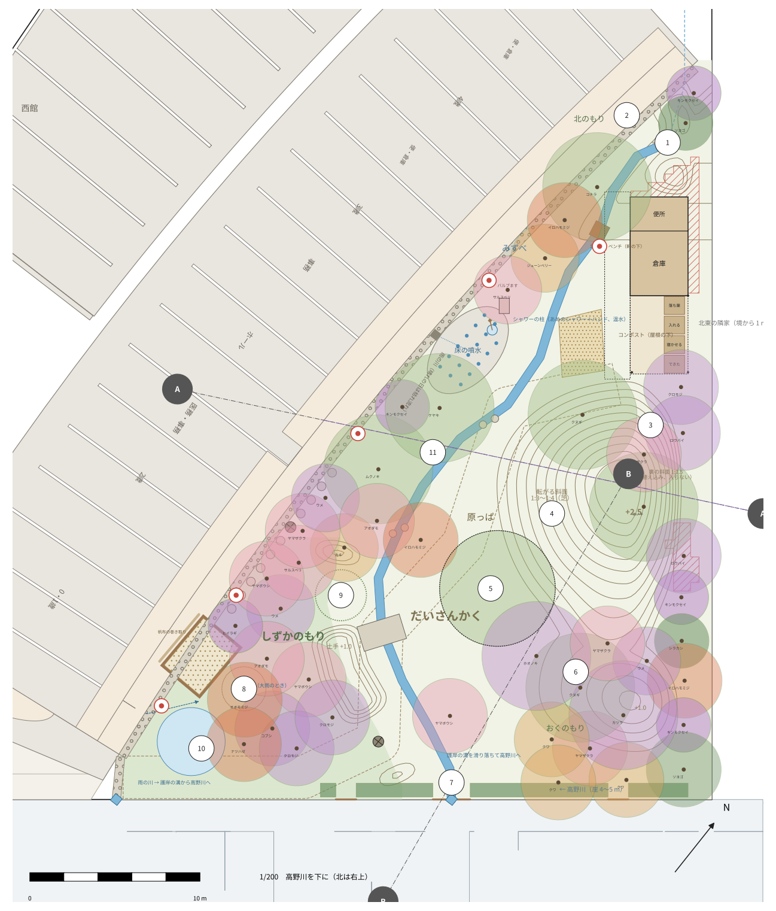

ホールの北山杉の林　こどもの目の高さから

ホールの北山杉の林　こどもの目の高さ（0.9 m）から見た景色　（たたき台・6 版：すべて自立）

円筒投影（横＝方位 110°、縦＝仰角）。幹は北山杉（φ50 は磨き丸太、群の φ70・100 は太鼓落とし＝両側を平らに挽いた丸太、平らな面を列の向きにそろえる）。奥の色：うす緑＝縁側のガラス越しの園庭、ベージュ＝壁、橙＝キッチンのガラス、灰＝海峡。低い木（0.85〜1.1）はこどもの目の高さを隠し、高い木は屋根の近くまで

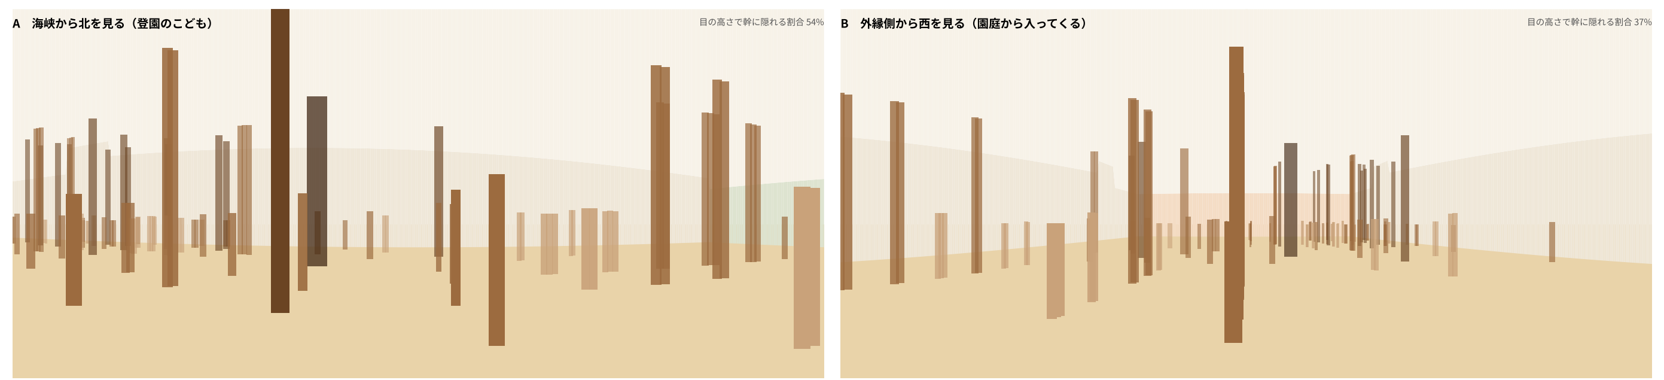

A　海峡から北を見る（登園のこども）　目の高さで幹に隠れる割合 54%

B　外縁側から西を見る（園庭から入ってくる）　目の高さで幹に隠れる割合 37%

洞のクスノキ　遊戯室の切り株

断面パース　スパン 11 の北の端（u 32.9）で切って南を見る

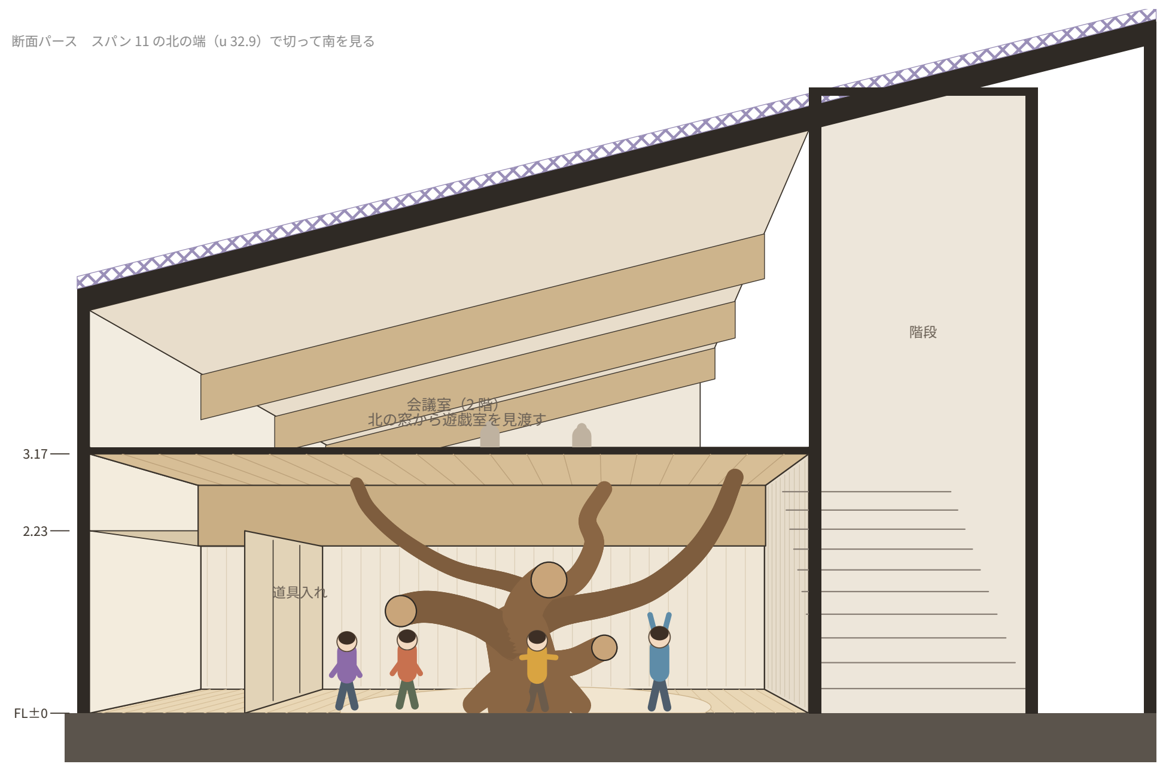

洞のクスノキ
2 階の床の下の低い洞（梁の下 2.23）。クスノキの枝の先が天井に触れ、木が 2 階を支えているように見える。
北の枝は床の縁の下をくぐって遊戯室の高い側へ（この図では切断面で切れている）。

園庭の断面　A 比叡へ／B 高野川へ（縮小）

死角：約 33 m²。築山の裏（隣家側）の植え込みと、北のもりの奥。植え込みは入らない所にする

断面 A–A　ホールから築山の頂を通って比叡山の向きへ　1/100

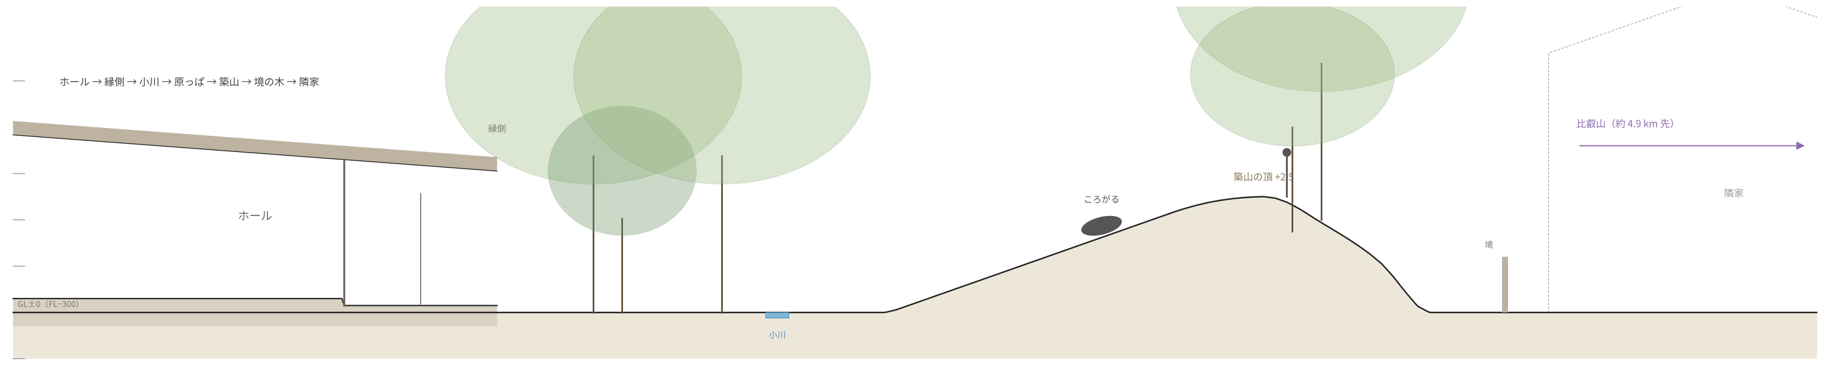

断面 B–B　築山から原っぱ・のぞき（生垣の口）を通って高野川へ　1/100（崖・河川敷の寸法は仮）

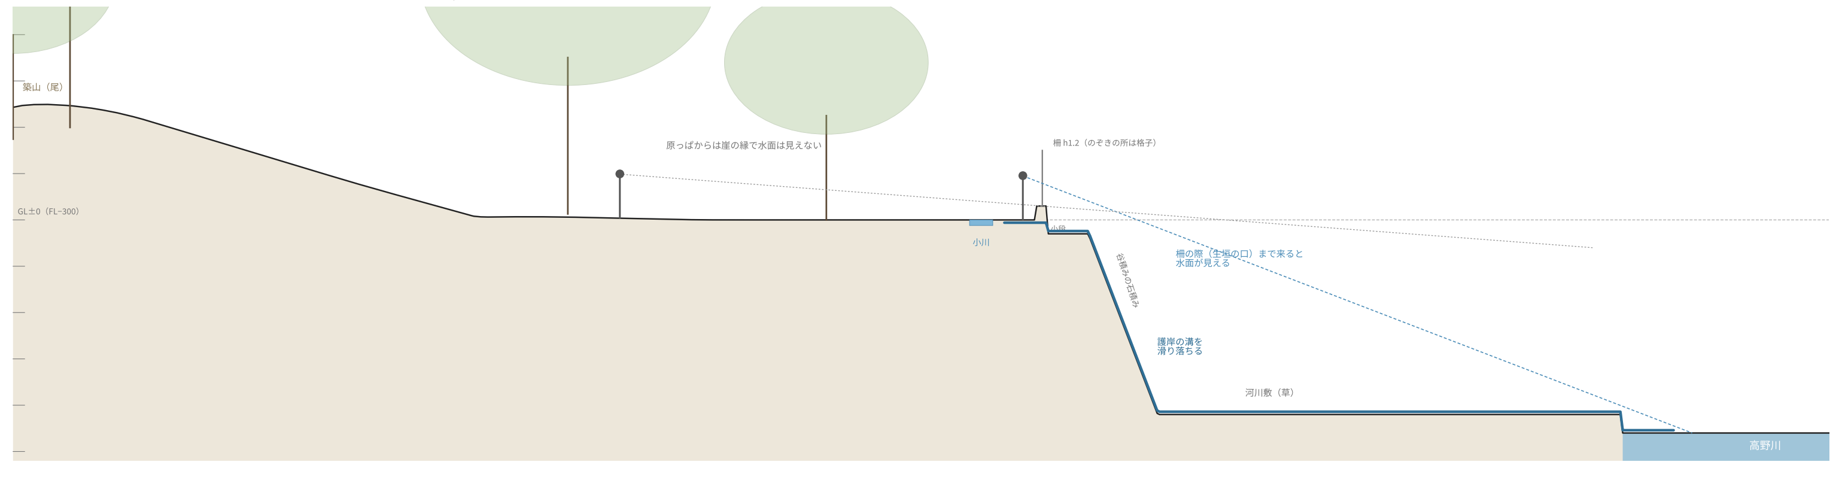

［割付の注記］フォーカス：すべての人の一日（こども・保育士・調理）と、こどもたちが地に足をつけて育つ場所：透視図・遊戯室・園庭・北山杉の林　／　目に入る順：一日の帯と動線 → 透視図（A4）→ 遊戯室 → 園庭の5つ → 園庭・林・洞・断面

こどもたちの育ち舎　5/5　環境

建築設計実習 II — I　2026.11.05　木田

断面図C　東西に切る（4歳・遊戯室の擂鉢ネット）

1/75（1/100の自動の図を1.5倍）　西の道路から園庭へ

矢印：昼の道（青）と夏の夜の道（紺）。床下の底板t200と断熱の帯。光の筋の光

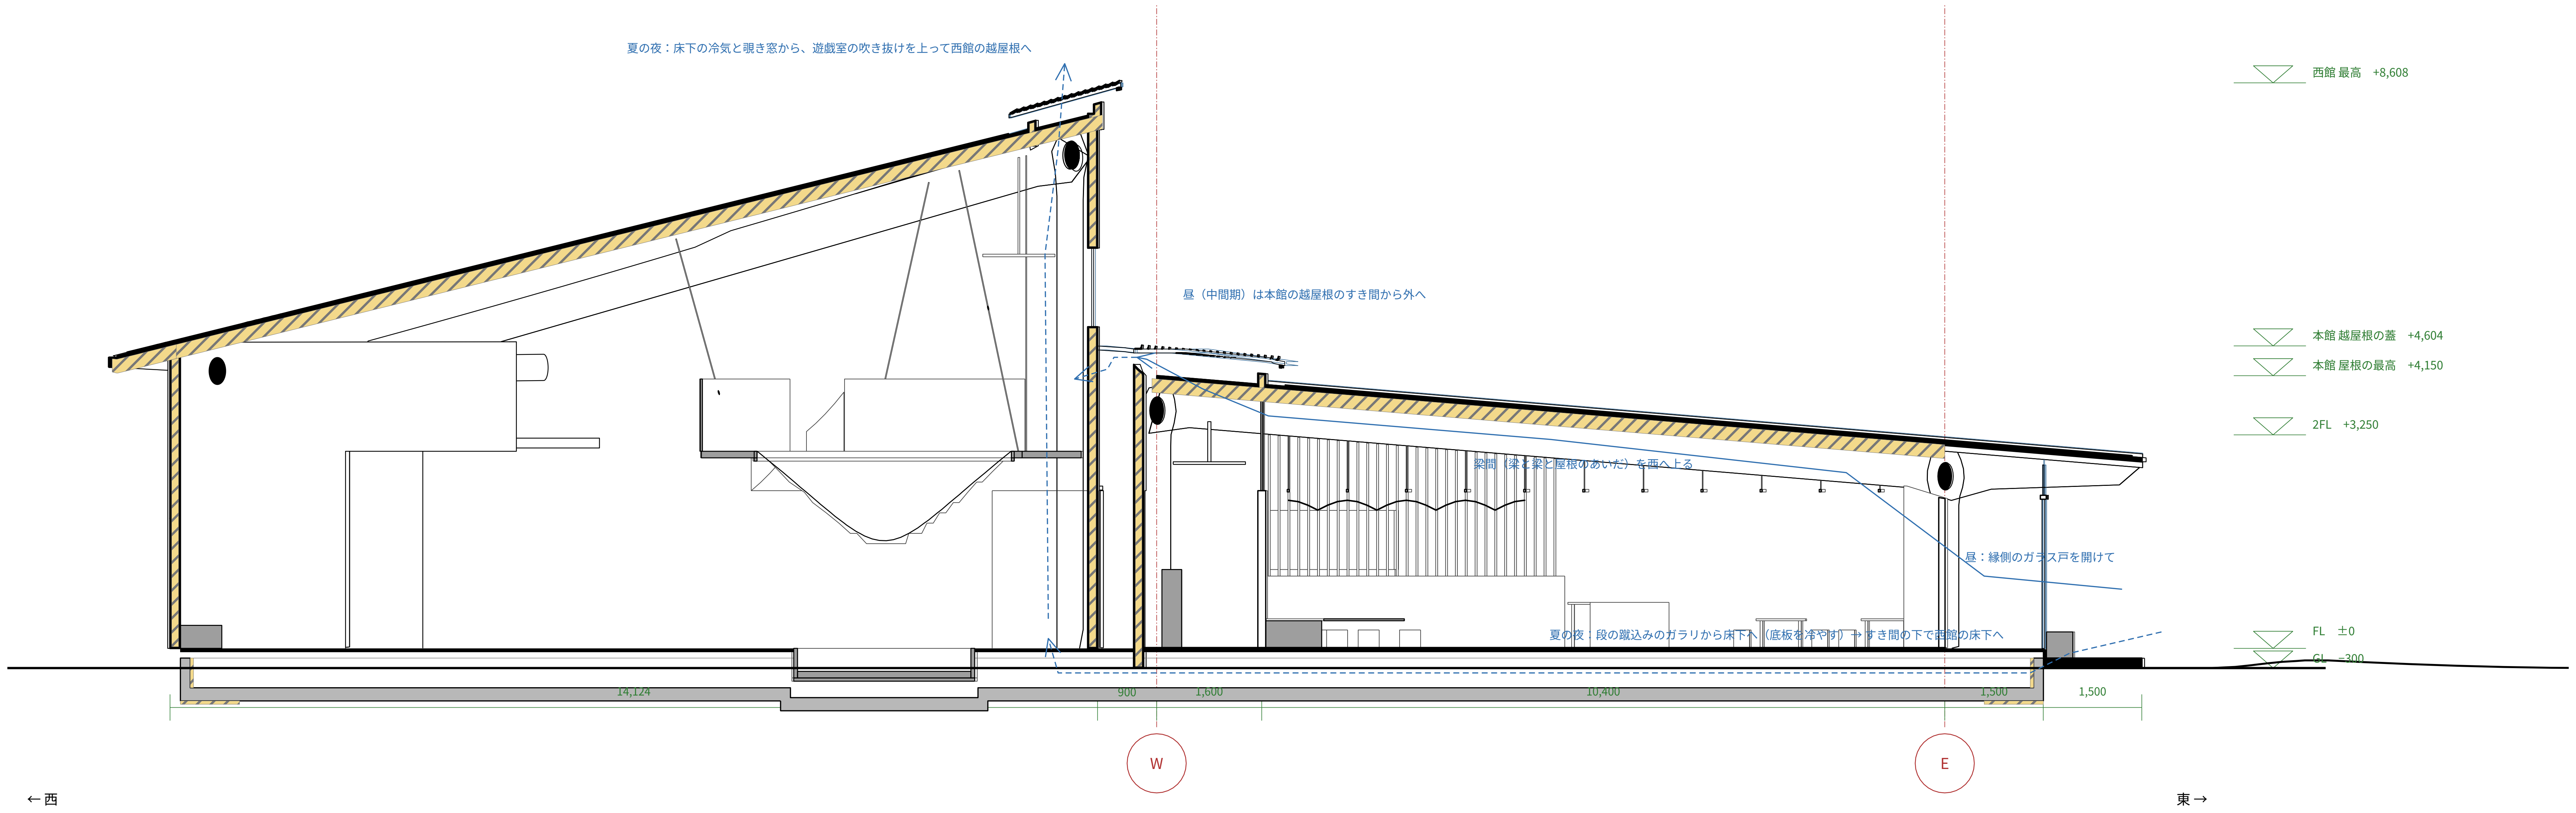
夏の夜：床下の冷気と覗き窓から、遊戯室の吹き抜けを上って西館の越屋根へ
昼（中間期）は本館の越屋根のすき間から外へ
梁間（梁と梁と屋根のあいだ）を西へ上る
昼：縁側のガラス戸を開けて
夏の夜：段の蹴込みのガラリから床下へ（底板を冷やす）→ すき間の下で西館の床下へ
西館 最高　+8,608
本館 越屋根の蓋　+4,604
本館 屋根の最高　+4,150
2FL　+3,250
FL　±0
GL　−300
14,124
900
1,600
10,400
1,500
1,500
W
E
←西
東→

運転表

環境への配慮（LEED v5 Gold相当）

運転表	環境への配慮（LEED v5 Gold相当）
夏の昼 庇・天井扇 床下空調	**パッシブ** 床下に冷えをためる 通風・光の筋
夏の夜 床下→梁間 →越屋根・遊戯室	**エネルギー** 屋根材型の太陽光 蓄電池
春・秋 越屋根を開ける 縁側を開け放す	**資源** 北山杉の間伐材 土・雨・生ごみを回す
冬 換気口を閉じる 熱交換・断熱	**時間** S&I 水まわりはどこでも

縦断面図A

1/100　保育室の中ほどの弧で切って展開、西を見る（左が南の高野川）

断面図B　海峡

1/100　南の入口・キッチン・2階・すき間・本館・縁側

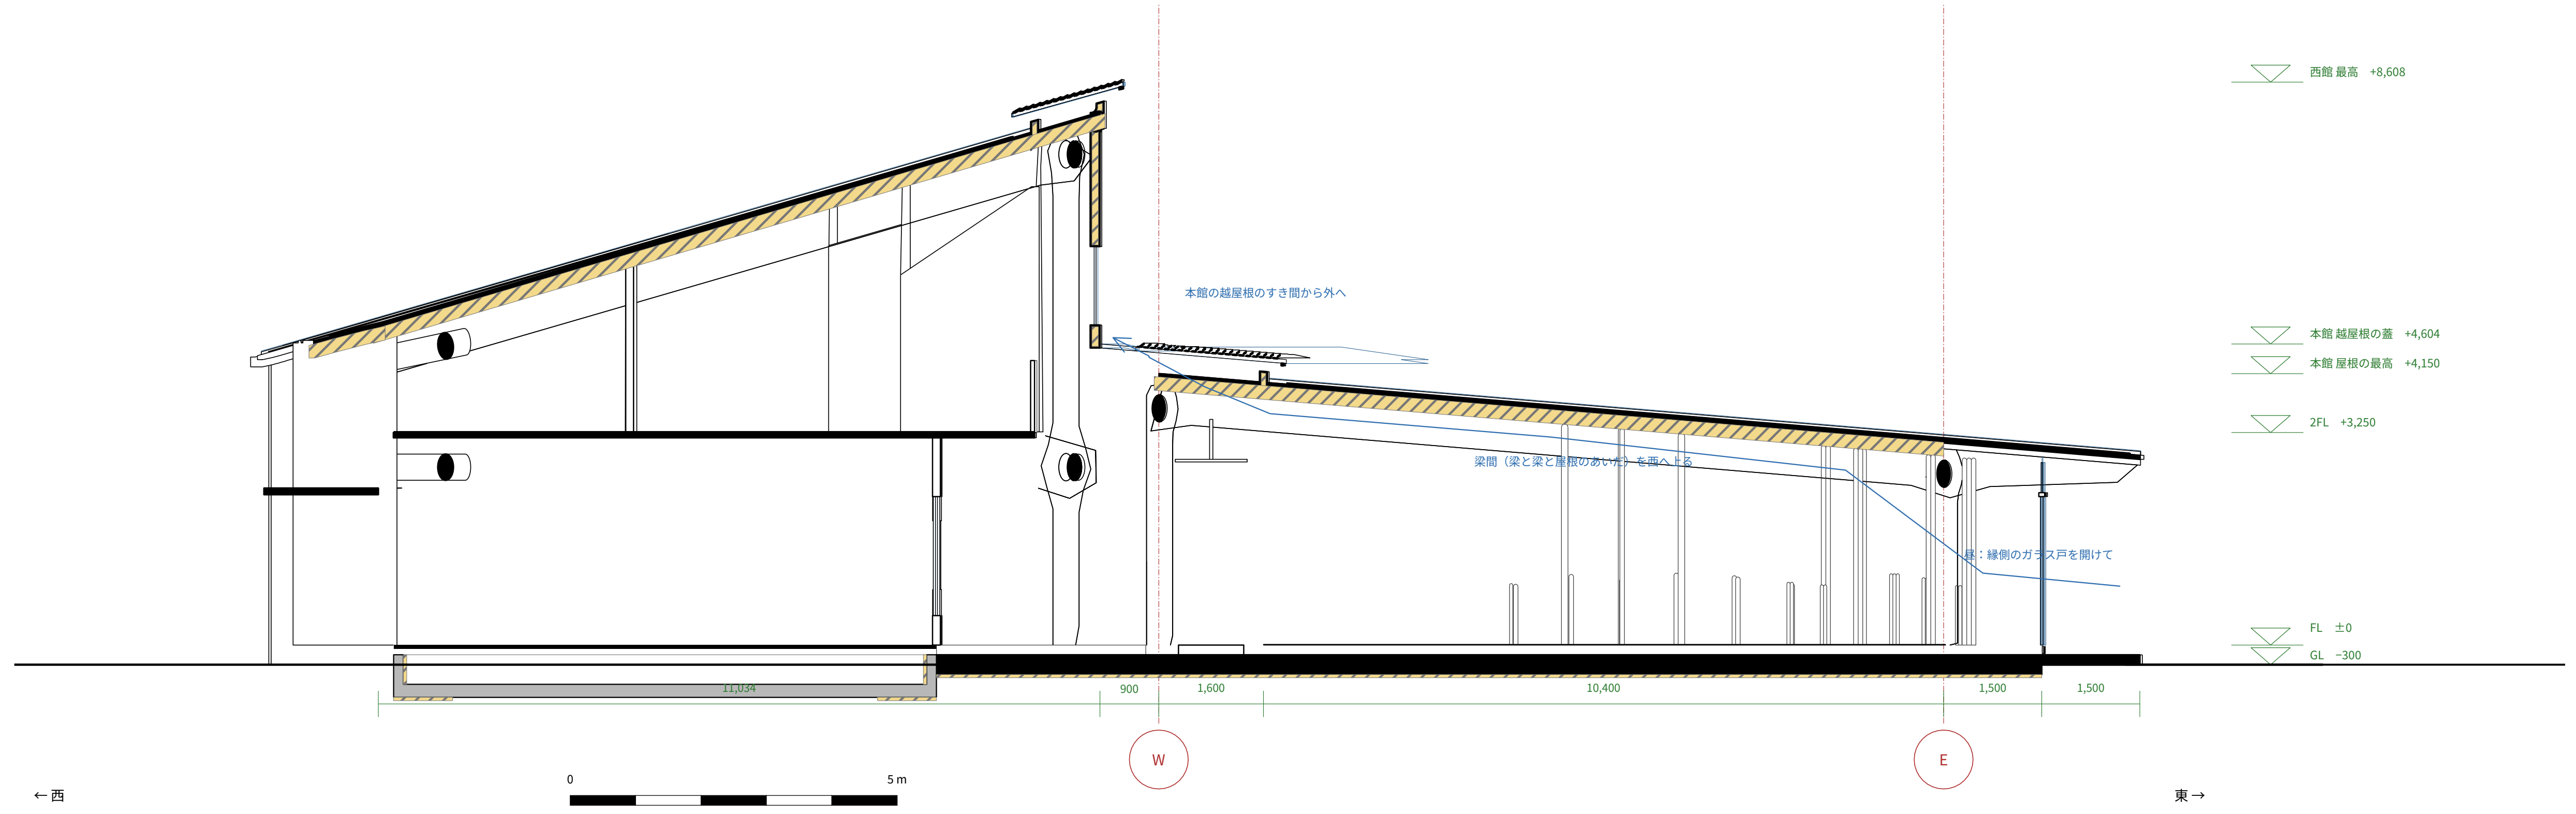

スケルトン＆インフィル
3ｍスパンの架構（固定）と
間仕切り・家具（可変）
今／定員が変わる／地域の場

光の筋と架構　1/20
2枚の梁のあいだ180の上に
乳白ガラス

inspired by

Asilo Nido Iride
Mario Cucinella Architects・Guastalla・2015
→ 梁の列が並ぶ長細い本館と、外に付く付属の建物

Tamedia
坂茂・Zürich・2013
→ 梁の端の楕円の頭と、それを貫く楕円の桁

レイモンド斑鳩こども園
キノアーキテクツ・斑鳩・2026
→ 室内に木を立てる（ホールの北山杉）

KAIT工房
石上純也・厚木・2008
→ 柱の配列：見る向きで景色が変わる並び

認定こども園らみどり
はりゅうウッドスタジオ・須賀川・2026
→ 内と外の二重の縁側、遊具を置かない地形の園庭

仙田満の園舎
環境デザイン研究所
→ 擂鉢のネット、キャットウォーク、ニッチ

Waldorf School of the Peninsula
California
→ 遊戯室の切り株

接合部（2枚の梁で柱を挟む）

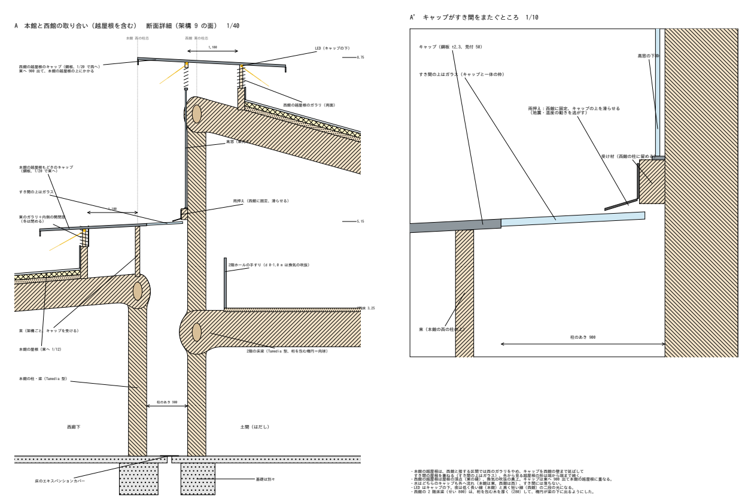
A　本館と西館の取り合い（越屋根を含む）　断面詳細（架構 9 の面）　1/40
A'　キャップがすき間をまたぐところ　1/10
西廊下
土間（はだし）
柱のあき 900

［割付の注記］フォーカス：木造・パッシブ（床下・越屋根・光の筋）で空調を補う。東西に切った断面Cで空気の流れ。屋根材型の太陽光と蓄電池、資源のめぐり、時間（S&I）　／　目に入る順：断面C（昼と夏の夜の風）→ 運転表と配慮 → 縦断A → 断面B → 木の組み方・S&I