園庭の側の立面図　1/100　（円弧の中心の方向から、弧の真ん中に正対。西を見る、右が北）

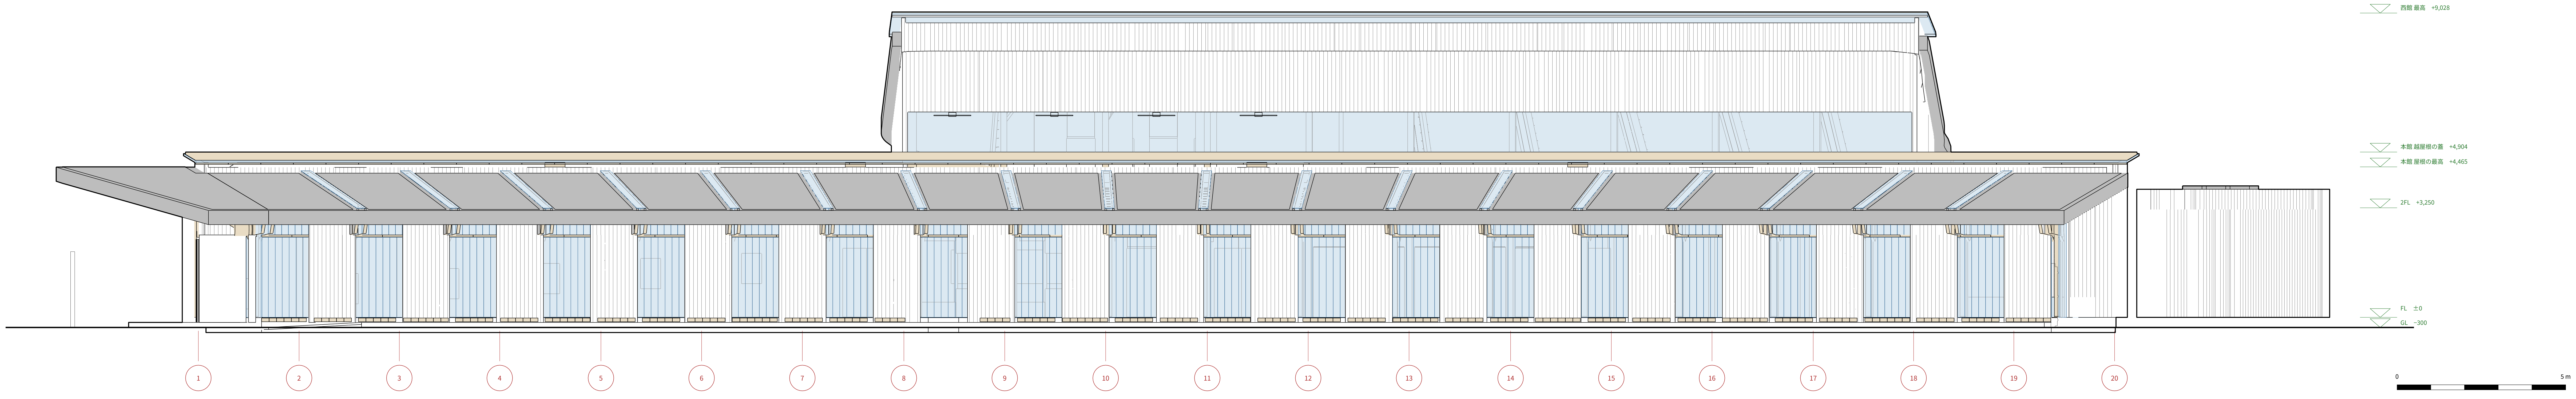
西館 最高　+9,028
本館 越屋根の蓋　+4,904
本館 屋根の最高　+4,465
2FL　+3,250
FL　±0
GL　−300
1
2
3
4
5
6
7
8
9
10
11
12
13
14
15
16
17
18
19
20
0
5 m

道路の側の立面図　1/100　（西の道路から、園庭の側の反対。東を見る、右が南）

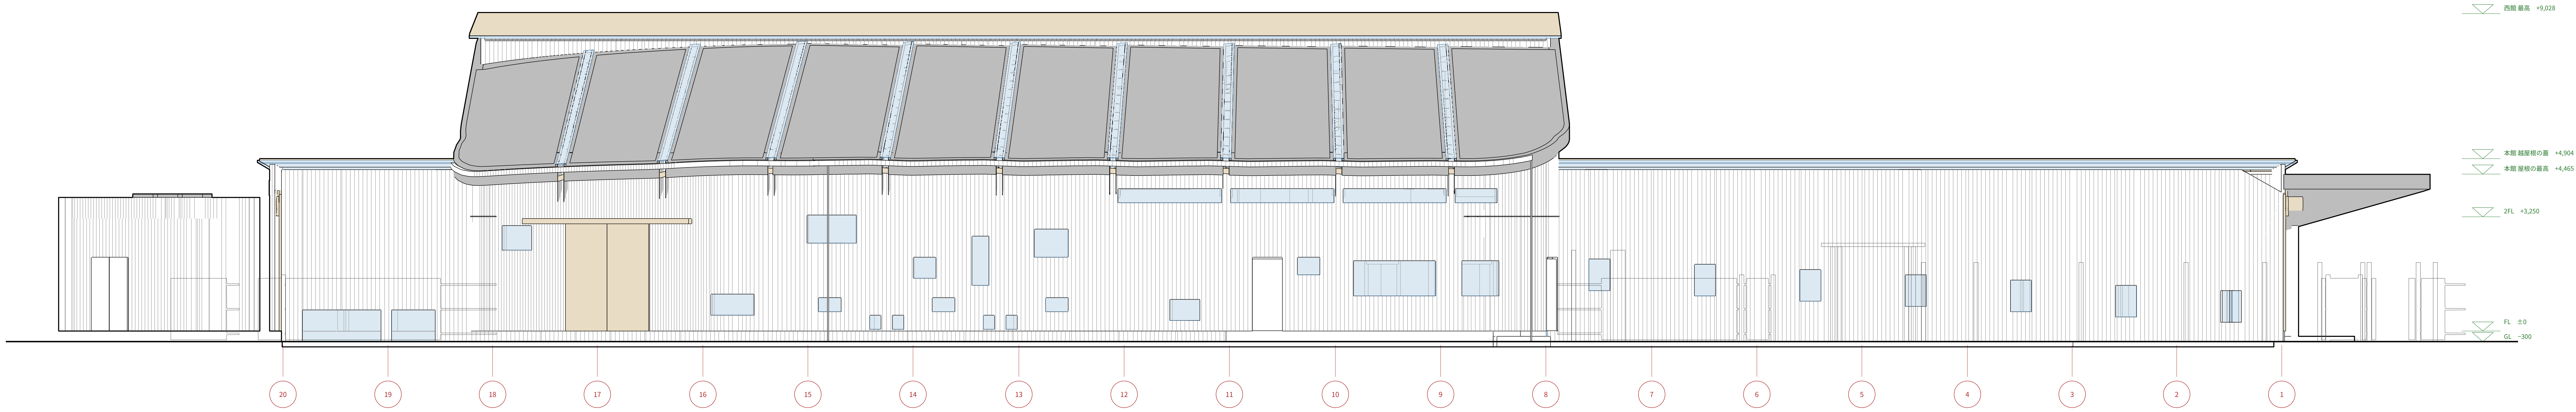
西館 最高　+9,028
本館 越屋根の蓋　+4,904
本館 屋根の最高　+4,465
2FL　+3,250
FL　±0
GL　−300
20
19
18
17
16
15
14
13
12
11
10
9
8
7
6
5
4
3
2
1

南の妻の立面図　1/100　（架構 1 に正対。北を見る、右が東）

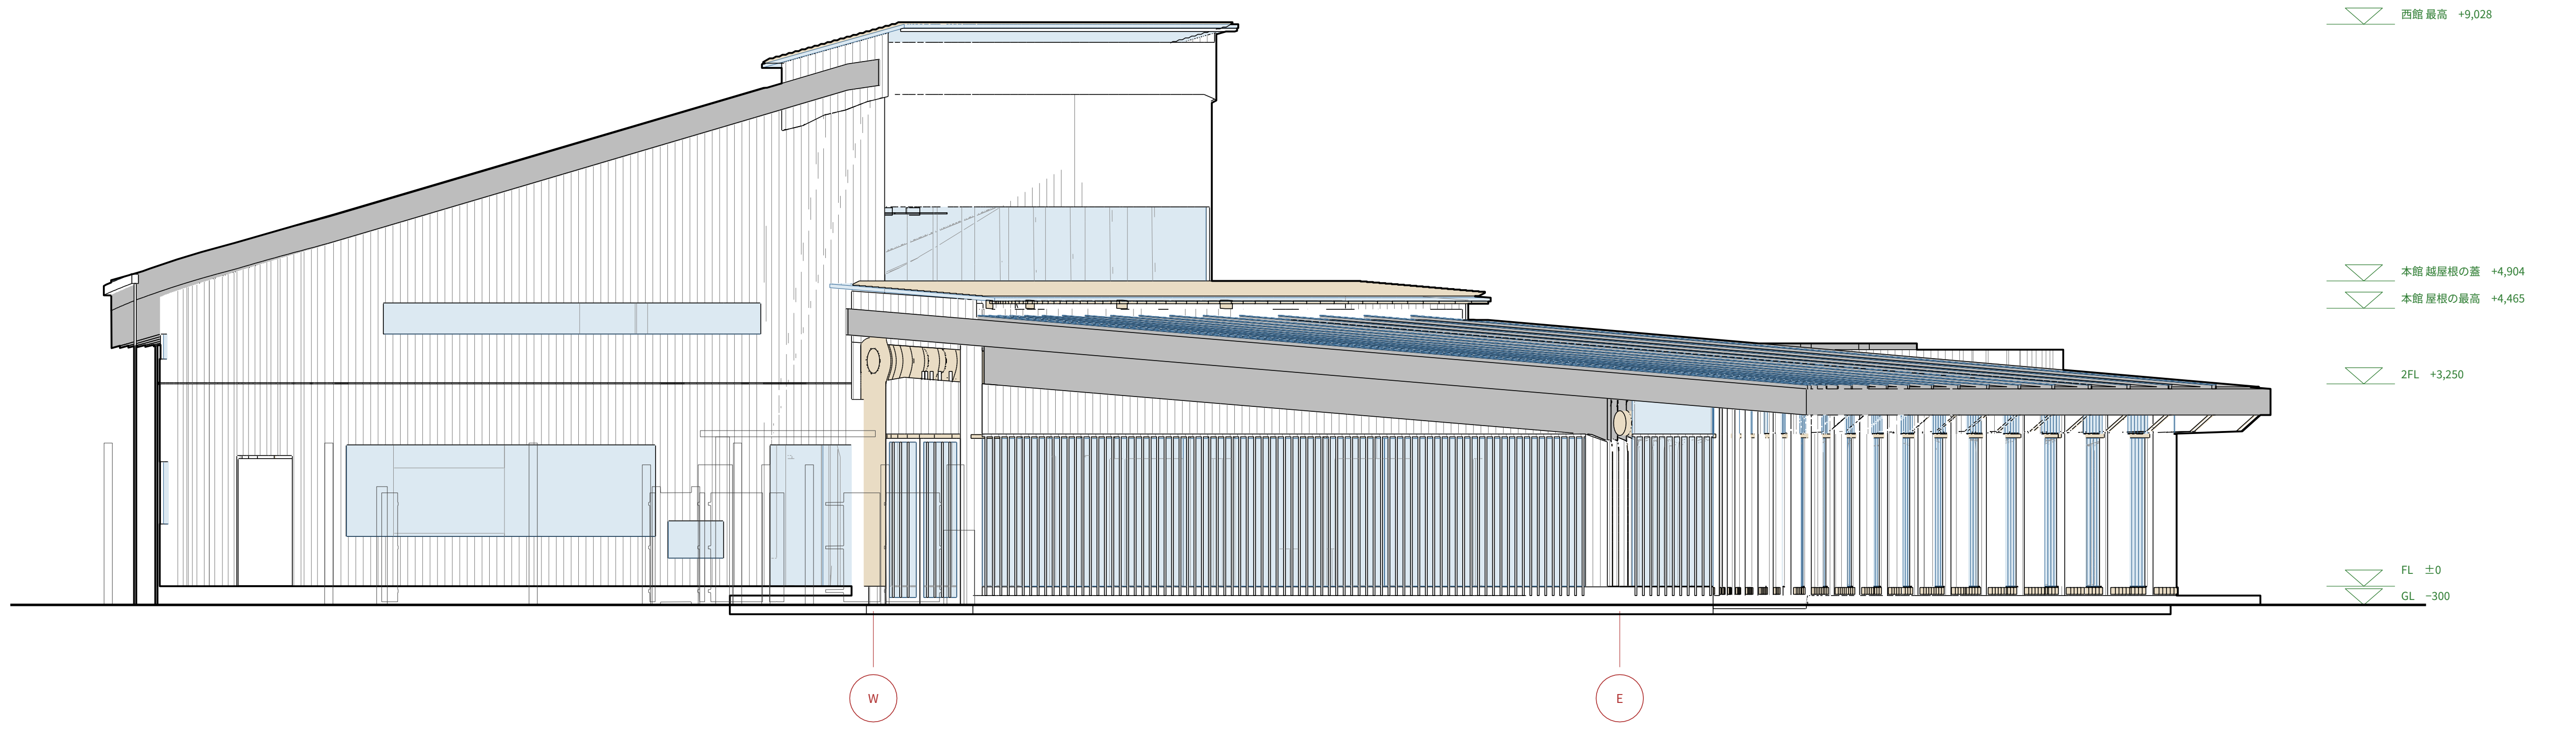
西館 最高　+9,028
本館 越屋根の蓋　+4,904
本館 屋根の最高　+4,465
2FL　+3,250
FL　±0
GL　−300
W
E

建物と、その手前の外構（塀・柵・木戸・棚・柱、細い線）・樹木（淡い緑の輪郭、手前 15 m まで）。駐車・駐輪・室内の家具は省いた。灰色は屋根の面、薄い青はガラス（奥は細い灰色の線で透けて見える）。建物の外形は太い線。
園庭の側と道路の側は本館の弧の真ん中に正対（平面と同じ向き、架構の番号は下の丸）。南の妻は架構 1 に正対。

立面図 1　園庭の側・道路の側・南の妻　1/100（A1）

こどもたちの育ち舎　3dm（sodachiya.3dm）から自動で作図　2026-10-27 18:04（atelier b1c5891 の次の版の 3dm）