平面図　1階　FL+1500 で切断／2階（西館）2FL+1000 で切断　1/100

高野川を下に（配置図と同じ向き）。2階は西の道路の外に同じ向きで置いた（遊戯室は吹き抜けから見下ろす）。一点鎖線は敷地の境。二点鎖線は切断より上にある物（屋根の外形・越屋根・2階の床の縁など）

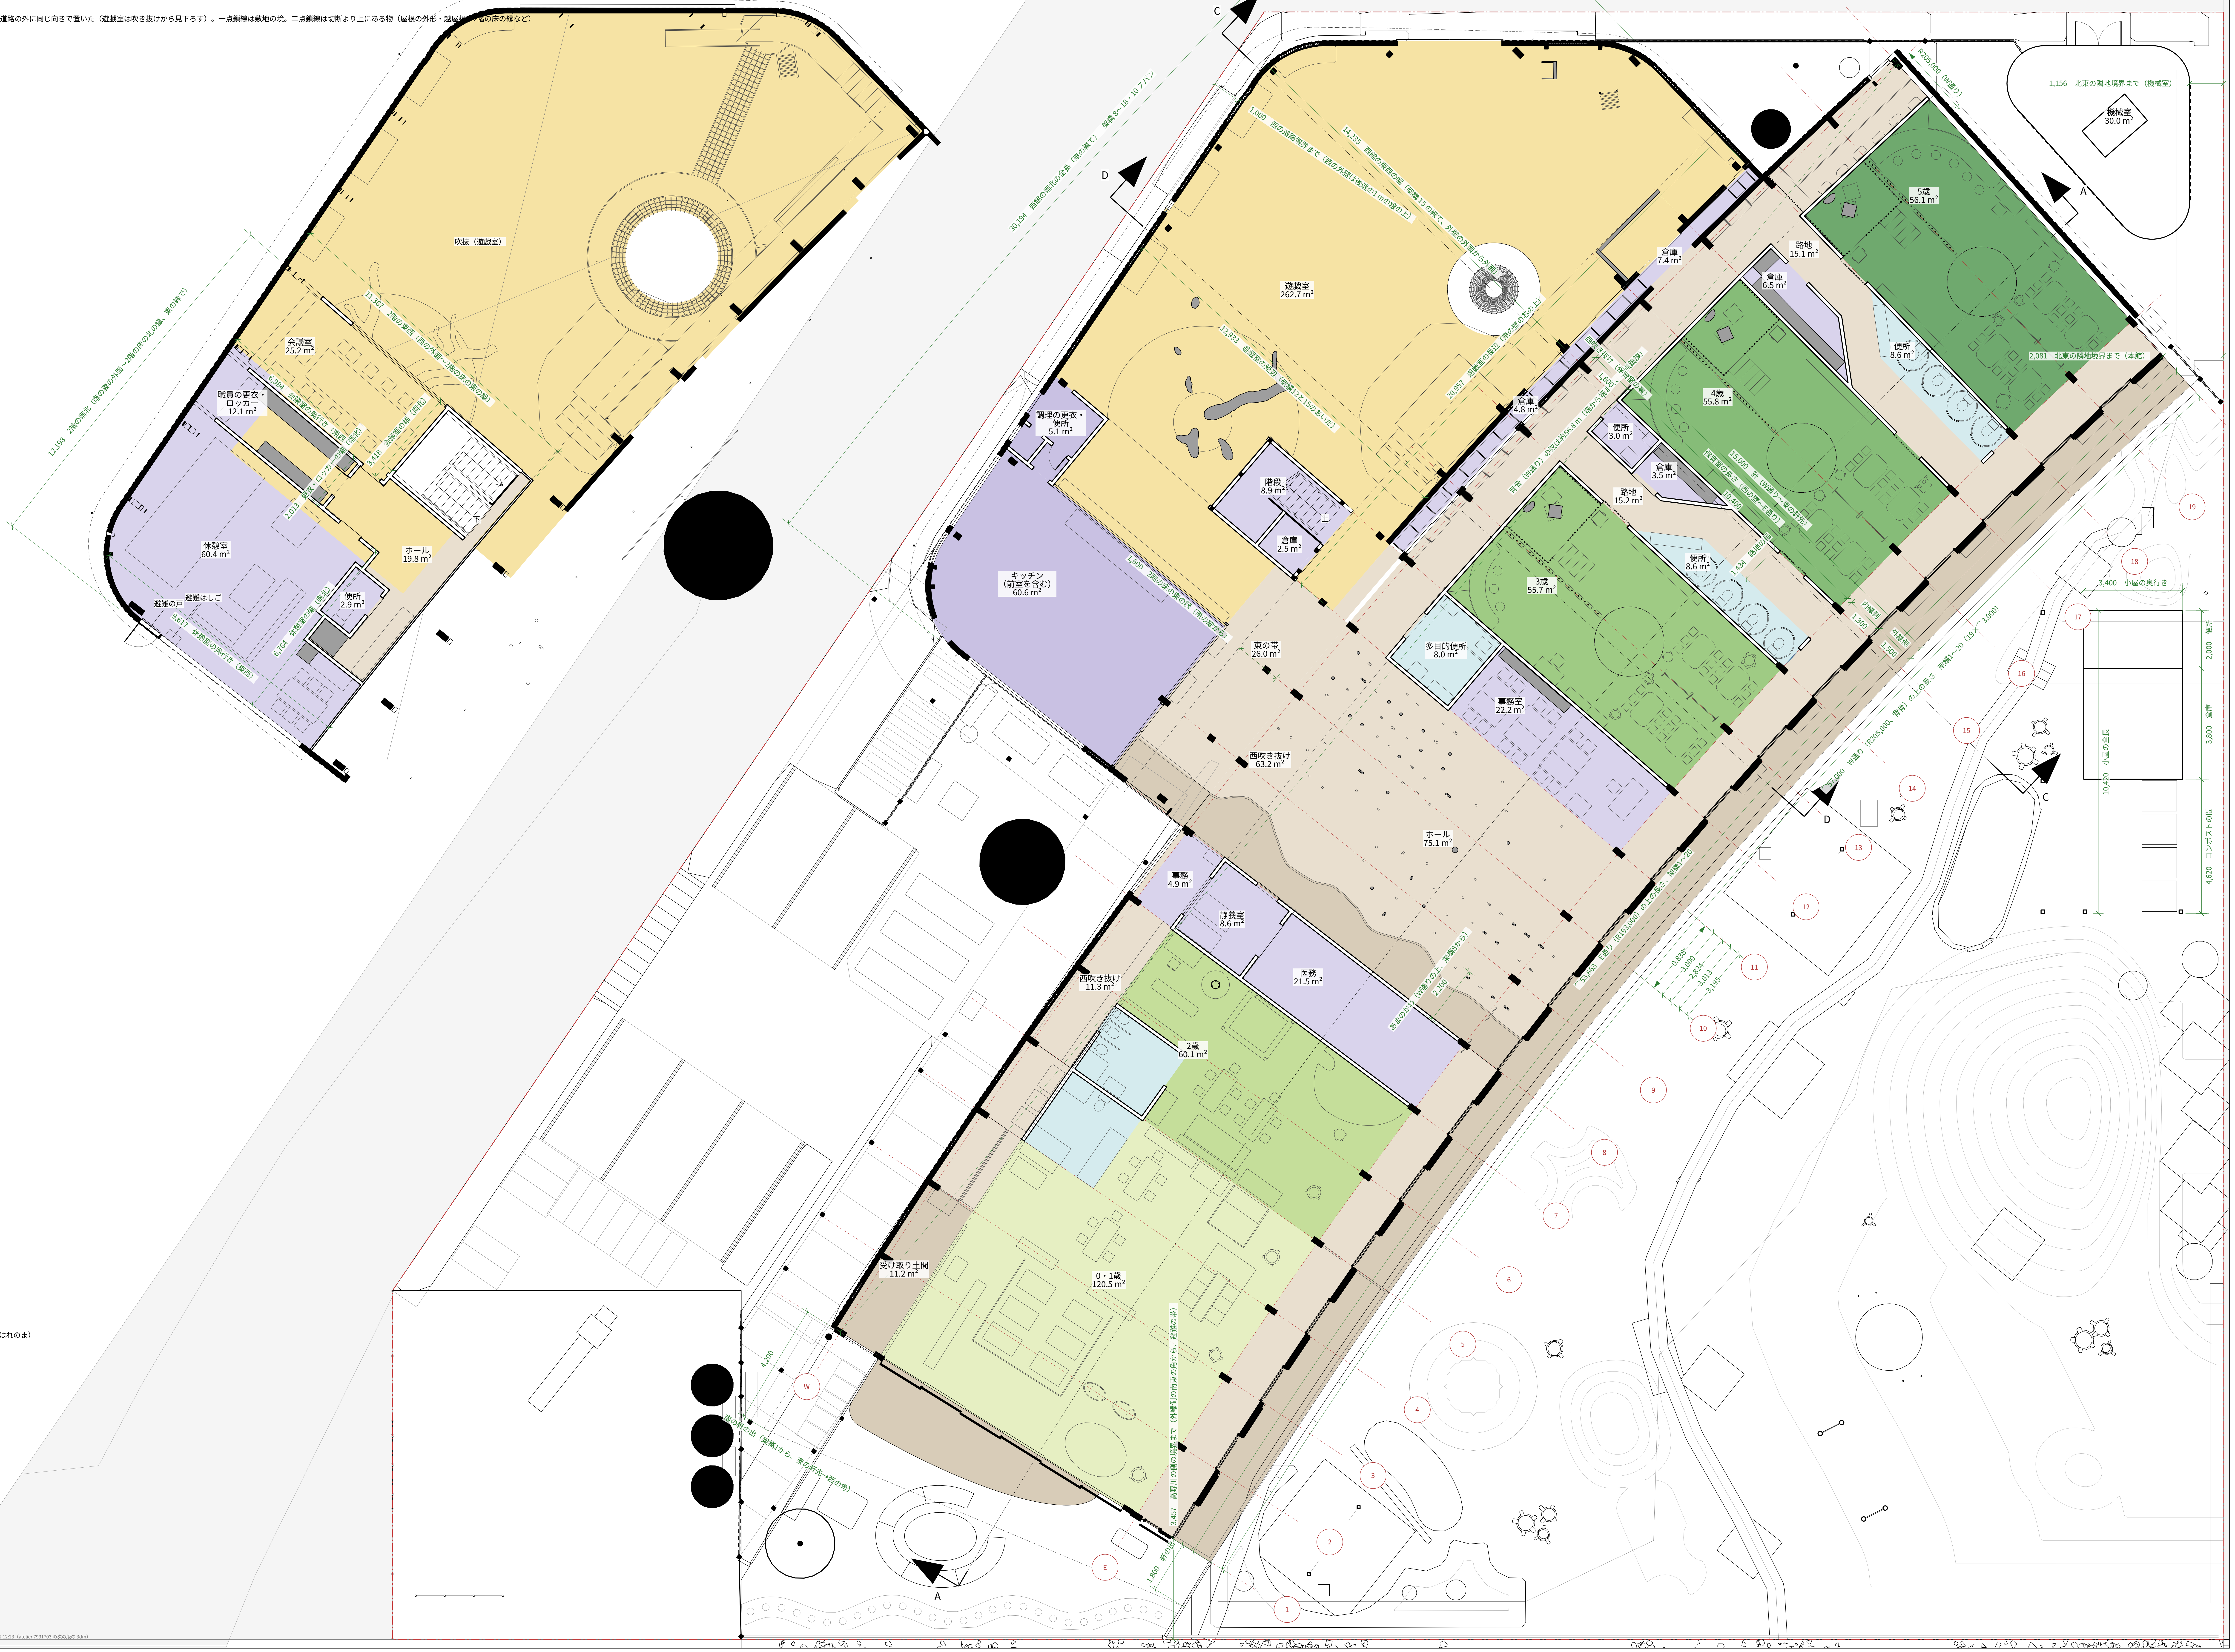

吹抜（遊戯室）
会議室 25.2 m²
職員の更衣・ロッカー 12.1 m²
休憩室 60.4 m²
ホール 19.8 m²
便所 2.9 m²
避難の戸
避難はしご
下
12,198　2階の南北（南の妻の外面〜2階の床の北の縁、東の縁で）
11,367　2階の東西（西の外面〜2階の床の東の縁）
6,984　会議室の奥行き（東西）
3,418　会議室の幅（南北）
2,013　更衣・ロッカーの幅（南北）
9,617　休憩室の奥行き（東西）
6,764　休憩室の幅（南北）
30,194　西館の南北の全長（東の線で）　架構 8〜18・10 スパン
C
D
A
1,000　西の道路境界まで（西の外壁は後退の1mの線の上）
14,235　西館の東西の幅（架構 15 の線で、外壁の外面から外面）
20,957　遊戯室の長辺（東の壁の芯の上）
12,933　遊戯室の短辺（架構12と15のあいだ）
1,600　2階の床の東の縁（東の線から）
遊戯室 262.7 m²
調理の更衣・便所 5.1 m²
キッチン（前室を含む）60.6 m²
階段 8.9 m²
上
倉庫 2.5 m²
倉庫 7.4 m²
倉庫 4.8 m²
西吹き抜け（保育室の裏）
1,600
背骨（W通り）の弦は約56.8 m（端から端まで）
路地 15.1 m²
倉庫 6.5 m²
5歳 56.1 m²
便所 8.6 m²
4歳 55.8 m²
便所 3.0 m²
倉庫 3.5 m²
路地 15.2 m²
3歳 55.7 m²
便所 8.6 m²
保育室の長さ（西の壁〜E通り）
10,400
15,000　計（W通り〜東の軒先）
1,434　路地の幅
内縁側
1,300
外縁側
1,500
R205,000（W通り）
1,156　北東の隣地境界まで（機械室）
機械室 30.0 m²
2,081　北東の隣地境界まで（本館）
東の帯 26.0 m²
多目的便所 8.0 m²
事務室 22.2 m²
西吹き抜け 63.2 m²
ホール 75.1 m²
事務 4.9 m²
静養室 8.6 m²
医務 21.5 m²
西吹き抜け 11.3 m²
2歳 60.1 m²
受け取り土間 11.2 m²
0・1歳 120.5 m²
あまのがわ（W通りの上、架構8から）
2,200
〜57,000　W通り（R205,000、背骨）の上の長さ、架構1〜20（19×〜3,000）
〜53,663　E通り（R193,000）の上の長さ、架構1〜20
0.838°
3,000
2,824
3,013
3,195
3,400　小屋の奥行き
2,000　便所
3,800　倉庫
4,620　コンポストの間
10,420　小屋の全長
3,457　高野川の側の境界まで（外縁側の南東の角から、避難の帯）
1,800　軒の出
4,200
南の軒の出（架構1から、東の軒先→西の角）
W
E
1
2
3
4
5
6
7
8
9
10
11
12
13
14
15
16
17
18
19
N

部屋の色

🟩	0・1歳〜5歳
🟨	こどものみんなの場所（遊戯室・はれのま）
▨	通り・つなぐ場所（はだし）
🟫	土足の床
🟪	大人の場所
🟪	キッチン・調理の更衣
🟦	水まわり

0　5 m

こどもたちの育ち舎　3dm（sodachiya.3dm）から自動で作図　2026-11-02 12:23（atelier 7931703 の次の版の 3dm）