平面図　1階　FL+1500 で切断　1/100

高野川を下に（配置図と同じ向き）。一点鎖線は敷地の境。二点鎖線は屋根の外形（軒の線）。周りの道・建物は細い線。スパンの寸法はスパン10の庭の側に重ねた5本（建物に近い順に、放射の線のあいだの角度／W通りの上の弧長／E通りの上の弧長／西館の東端の弧長／西館の西端の弧長）

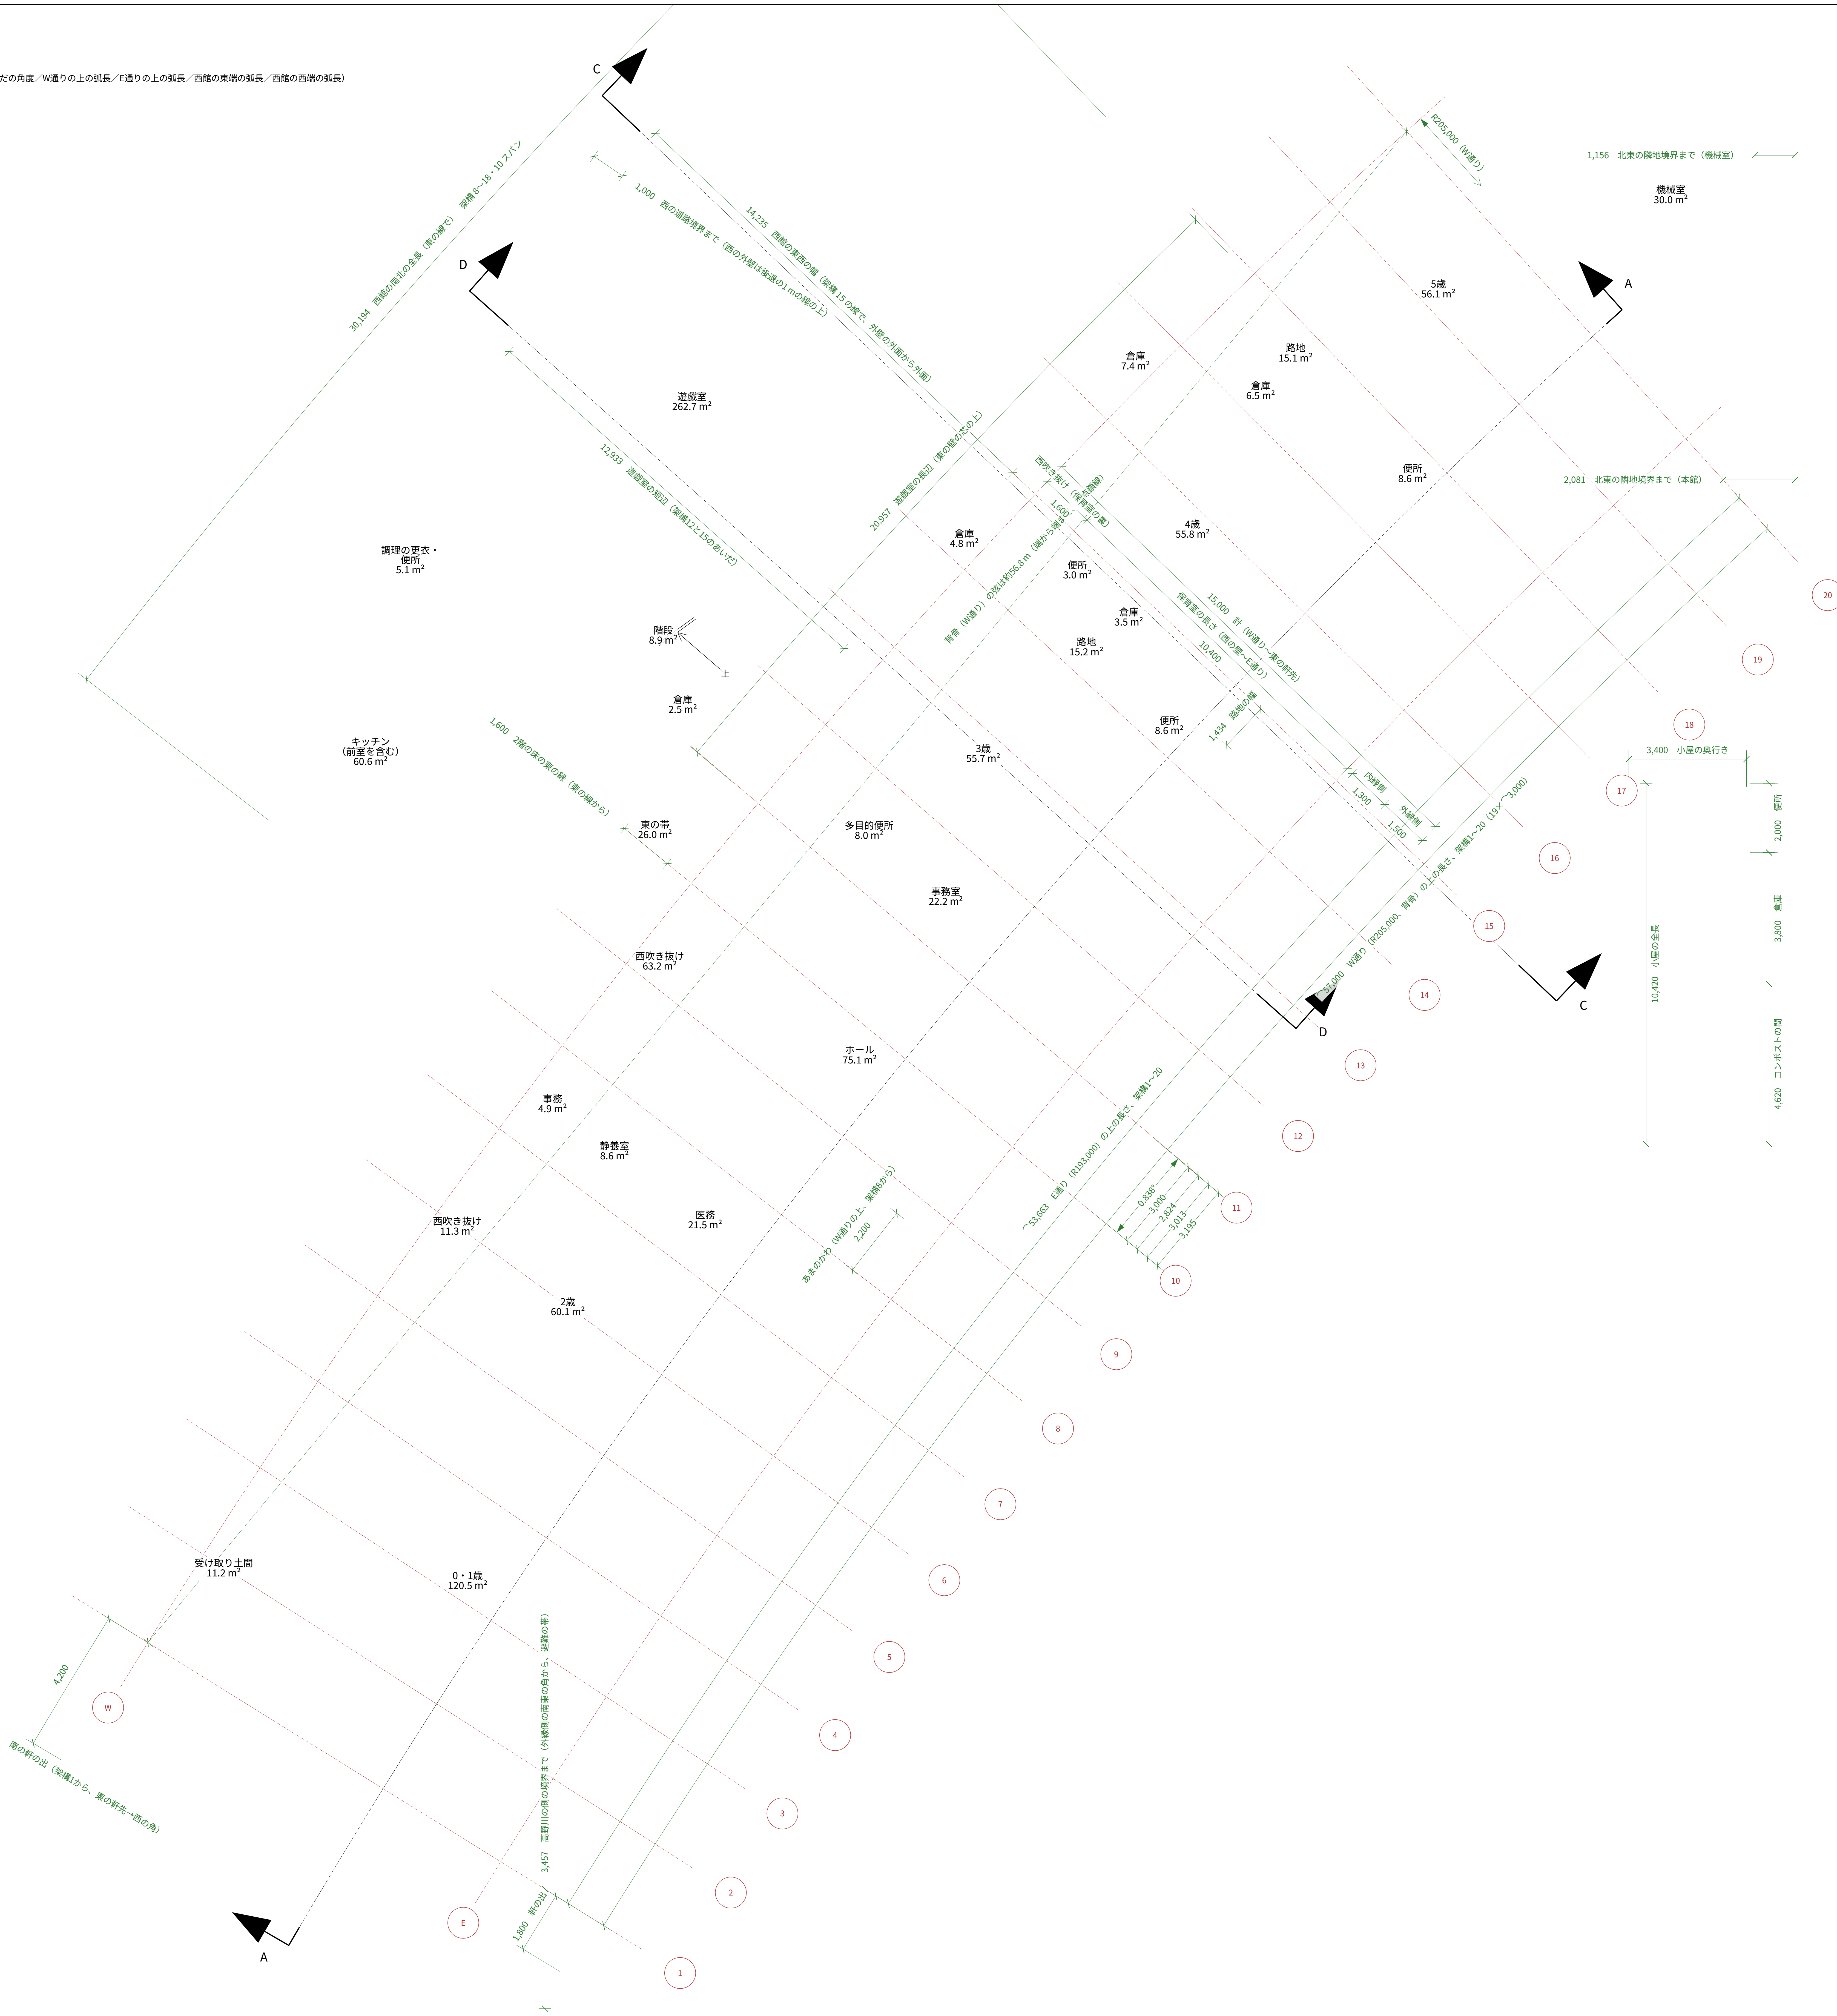
C
D
A
30,194　西館の南北の全長（東の線で）　架構 8〜18・10 スパン
1,000　西の道路境界まで（西の外壁は後退の1 mの線の上）
14,235　西館の東西の幅（架構 15 の線で、外壁の外面から外面）
R205,000（W通り）
1,156　北東の隣地境界まで（機械室）
機械室
30.0 m²
5歳
56.1 m²
倉庫
7.4 m²
路地
15.1 m²
倉庫
6.5 m²
遊戯室
262.7 m²
20,957　遊戯室の長辺（東の壁の芯の上）
12,933　遊戯室の短辺（架構12と15のあいだ）
便所
8.6 m²
2,081　北東の隣地境界まで（本館）
西吹き抜け（保育室の裏）
1,600
背骨（W通り）の弦は約56.8 m（端から端まで）
倉庫
4.8 m²
4歳
55.8 m²
調理の更衣・
便所
5.1 m²
便所
3.0 m²
倉庫
3.5 m²
15,000　計（W通り〜東の軒先）
保育室の長さ（西の壁〜E通り）
10,400
路地
15.2 m²
階段
8.9 m²
上
倉庫
2.5 m²
便所
8.6 m²
1,434　路地の幅
3歳
55.7 m²
キッチン
（前室を含む）
60.6 m²
1,600　2階の床の東の縁（東の線から）
内縁側
1,300
外縁側
1,500
3,400　小屋の奥行き
東の帯
26.0 m²
多目的便所
8.0 m²
〜57,000　W通り（R205,000、背骨）の上の長さ、架構1〜20（19×〜3,000）
10,420　小屋の全長
2,000　便所
3,800　倉庫
4,620　コンポストの間
事務室
22.2 m²
西吹き抜け
63.2 m²
ホール
75.1 m²
事務
4.9 m²
静養室
8.6 m²
〜53,663　E通り（R193,000）の上の長さ、架構1〜20
0.838°
3,000
2,824
3,013
3,195
西吹き抜け
11.3 m²
医務
21.5 m²
あまのがわ（W通りの上、架構8から）
2,200
2歳
60.1 m²
受け取り土間
11.2 m²
0・1歳
120.5 m²
4,200
南の軒の出（架構1から、東の軒先→西の角）
3,457　高野川の側の境界まで（外縁側の南東の角から、避難の帯）
1,800　軒の出
W
E
1
2
3
4
5
6
7
8
9
10
11
12
13
14
15
16
17
18
19
20

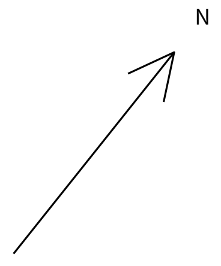

部屋の色

🟩	0・1歳〜5歳
🟨	こどものみんなの場所（遊戯室・はれのま）
▨	通り・つなぐ場所（はだし）
🟫	土足の床
🟪	大人の場所
🟪	キッチン・調理の更衣
🟦	水まわり

こどもたちの育ち舎　3dm（sodachiya.3dm）から自動で作図　2026-11-03 12:12（atelier 3e8ea96 の次の版の 3dm）