
育ち舎　3〜5歳の範囲　回遊のはしごと便・倉庫（たたき台）

1/100（A3）　2026-10-19　スパン11〜19。断熱ガラス戸は縁側の中ほど（柱の列から1.5 m外）。破線の矢印は回遊、青の破線はトップライト、一点鎖線は天袋（頭上）。保育室の家具は次回。

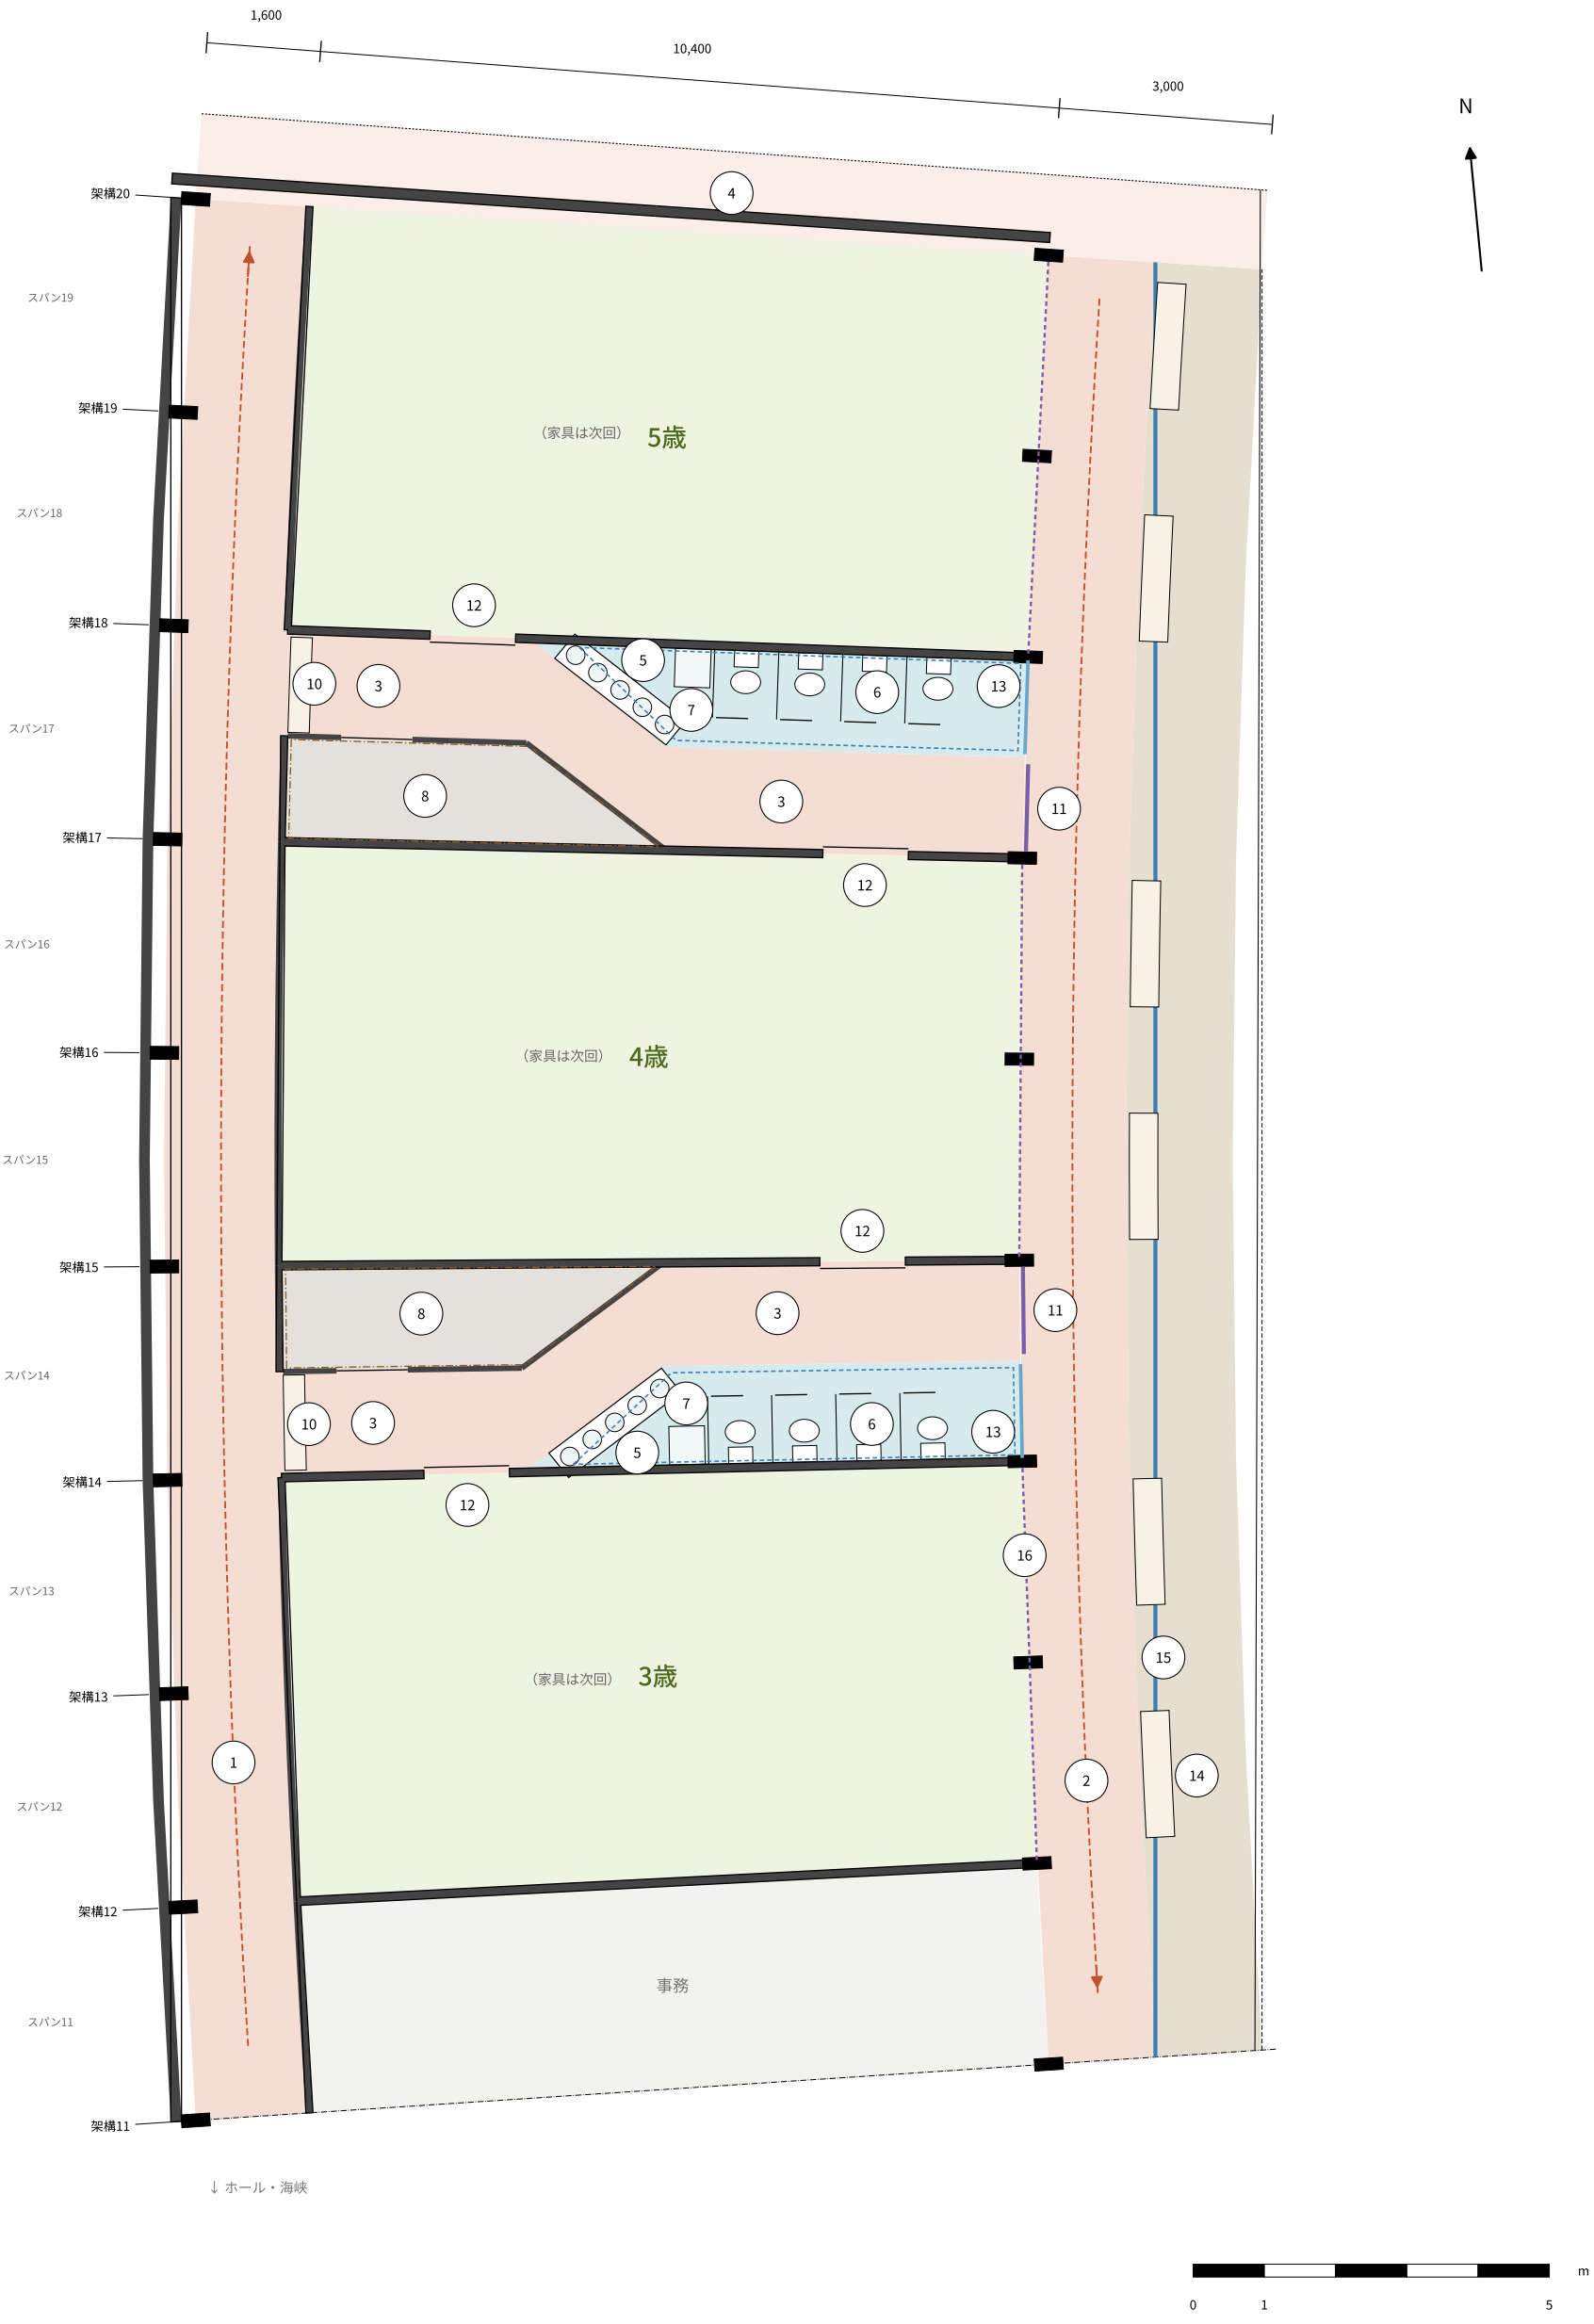

1　西吹き抜け（はしごの縦木。遊戯室に開く子どもの道）
2　内縁側 幅1.5（はしごの縦木。はだし）
3　路地 幅1.5（横木。途中で斜めに折れ、南北の側が入れ替わる）
4　北の小径（機械室とのすき間。外、検討中）
5　手洗い×5 h500（折れ目の溜まり。斜めのカウンター）
6　便所：座る便器×4（仕切りと扉 h1300）
7　汚物流し（先生用）
8　教材庫 約6.6 m²（路地から。上は天袋）
10　式台 150（路地の西の入口）
11　暖簾（路地の東の入口）
12　保育室から路地への戸（南の部屋は西寄り、北の部屋は東寄り）
13　トップライト（便所の上）。東の端に縁側への低い窓
14　外縁側 幅1.5（土足、FL−150。海峡から各クラスへ）
15　断熱ガラス戸と下足箱・腰掛け（外縁側の側）
16　保育室と内縁側の境（ふだんは開け放す吊り戸）
スパン17はスパン14を南北に裏返した形（二つの路地は折れ方が逆）

面積（芯々、概算）　保育室 各 60.3 m²（要求 約60）　便スパン1つあたり：路地 15.1、便所と手洗い 8.7、教材庫 6.5 m²

便器：3〜5歳 60人に8（7.5人に1）＋園庭の便所2〜3。手洗い10。スパン14は3歳と4歳、スパン17は4歳と5歳が使う。外遊びの道具と行事の倉庫は園庭の小屋へ。