
育ち舎　3〜5歳の保育室　断面のたたき台

1/50（A3）　2026-10-20　梁と梁のあいだで切る。人の高さ：先生 1,600、5歳 約1,100、3歳 約950。

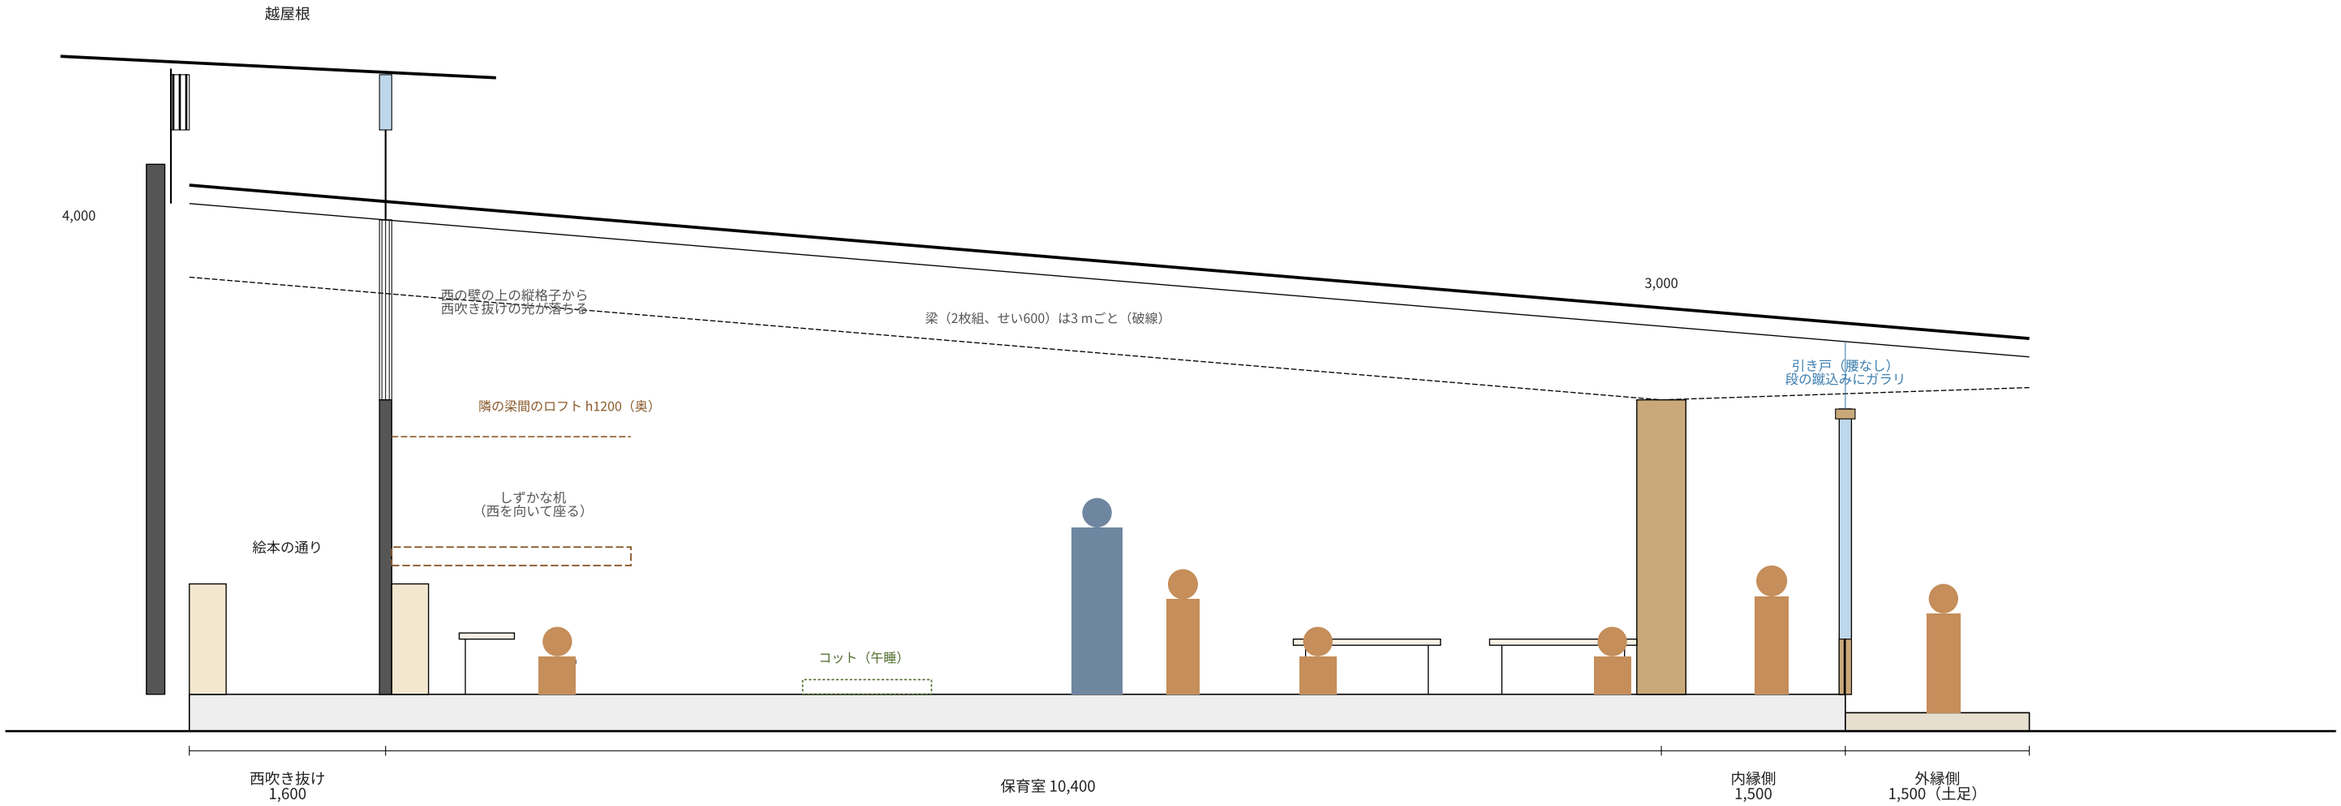

・西から、絵本の通り（西吹き抜け）→ しずかな机 → あつまり・午睡 → 食卓 → 内縁側 → 外縁側。静から動へ、暗から明へ。
・しずかな机は西へふくらむ弧。子どもは弧の内側から西を向いて座り、隣の子と少しそっぽを向く（ソシオフーガル）。正面は西の壁と縦格子の光。
・西の二つの梁間のうち、片方が「しずかな角」（角のない曲線の机、奥は収納）、もう片方がロフト h1200（下はデンとコット収納）。