松ヶ崎こども園　1敷地と自然環境

地に足をつけて育つ

比叡から降りる冷気と高野川の流れが出会う松ヶ崎の扇状地に、こどもたちが地に足をつけて育つ場所をつくる。

ゆるやかな弧を東の比叡にひらく木造平屋の本館に0歳から5歳のすべての部屋を並べ、縁側と深い庇で園庭とつなぐ。比叡に見立てた築山と、用水を借りて高野川に見立てた小川を置く。

オープンキッチンを玄関ホールに面する園の中心に据え、食べることを日々の求心力とする。野菜くずをこどもたちの手で土に還し、命の循環を知る。園庭にはチクチクする植物、季節ごとに香る木と実のなる木を植え、こどもたちは手と鼻と舌で季節を知る。

3 mスパンの木造架構によるスケルトン＆インフィルで用途の変化を受け止める。地域から様々なものを借り、無駄をせず巡らせて、こども園として地域に返す。

設計趣旨 約326字（課題は300字程度）。文字20 pt（5.1 mm）

4 災害時の持ちつ持たれつ

大洪水が予想される場合の緊急避難先として京都工芸繊維大学と協定（京都市ハザードマップによる浸水深1.5 m）。太陽光発電、蓄電池、地下水の利用によって、災害時に水を地域に提供。

3 お向かいさん

西の道の北半分は狭い道を挟んで向かいに住宅がある。圧迫感を与えないよう、この面の建物高さを1階程度に抑える。

6 間伐材を使った林

京都北山の北山杉の間伐材141本を、ホールの林として立てる。

2 車と自転車の出入りを南にまとめる

西の道の中ほどでは、道に突き出た木が見通しをさえぎる。車と送り迎えの自転車の出入りはこの木より南にまとめ、出入口にはスピードバンプを置いて速度を落とす。

1 小竹薮公園を残す

地域の記憶である小竹薮公園をそのまま残し、園への入口の前庭にする。そこから北へ、西の道沿いに幅1 mの歩道を開き、歩く人を車から守る。

地域のなかの敷地　1/10000

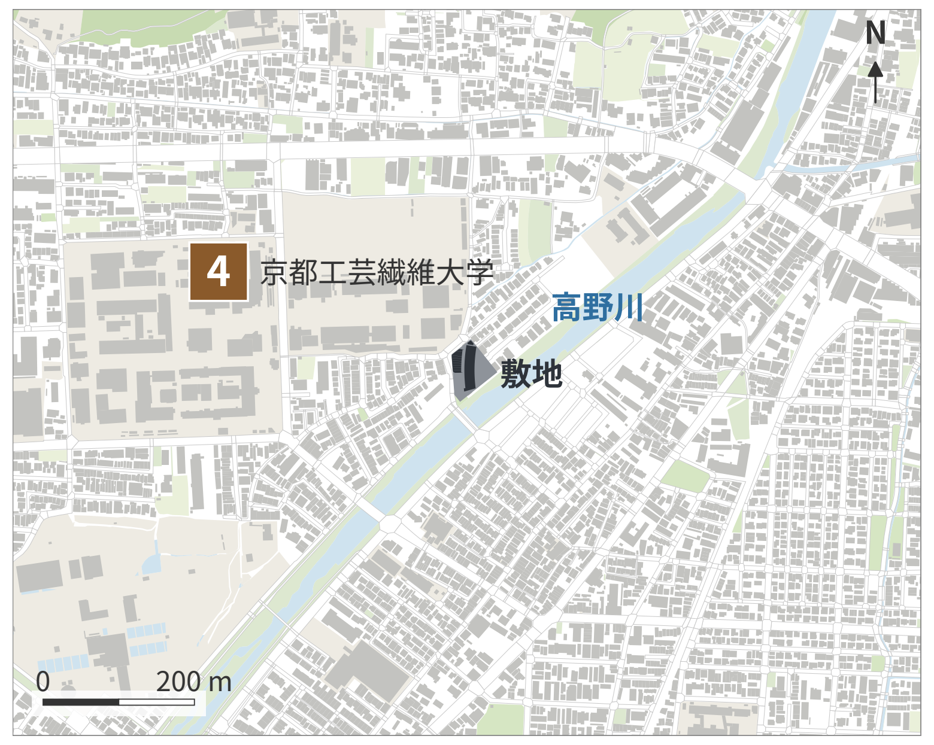
N
4 京都工芸繊維大学
高野川
敷地
0　200 m

出典：国土交通省 Project PLATEAU（京都市 2025）の建物・道路・土地利用から作図

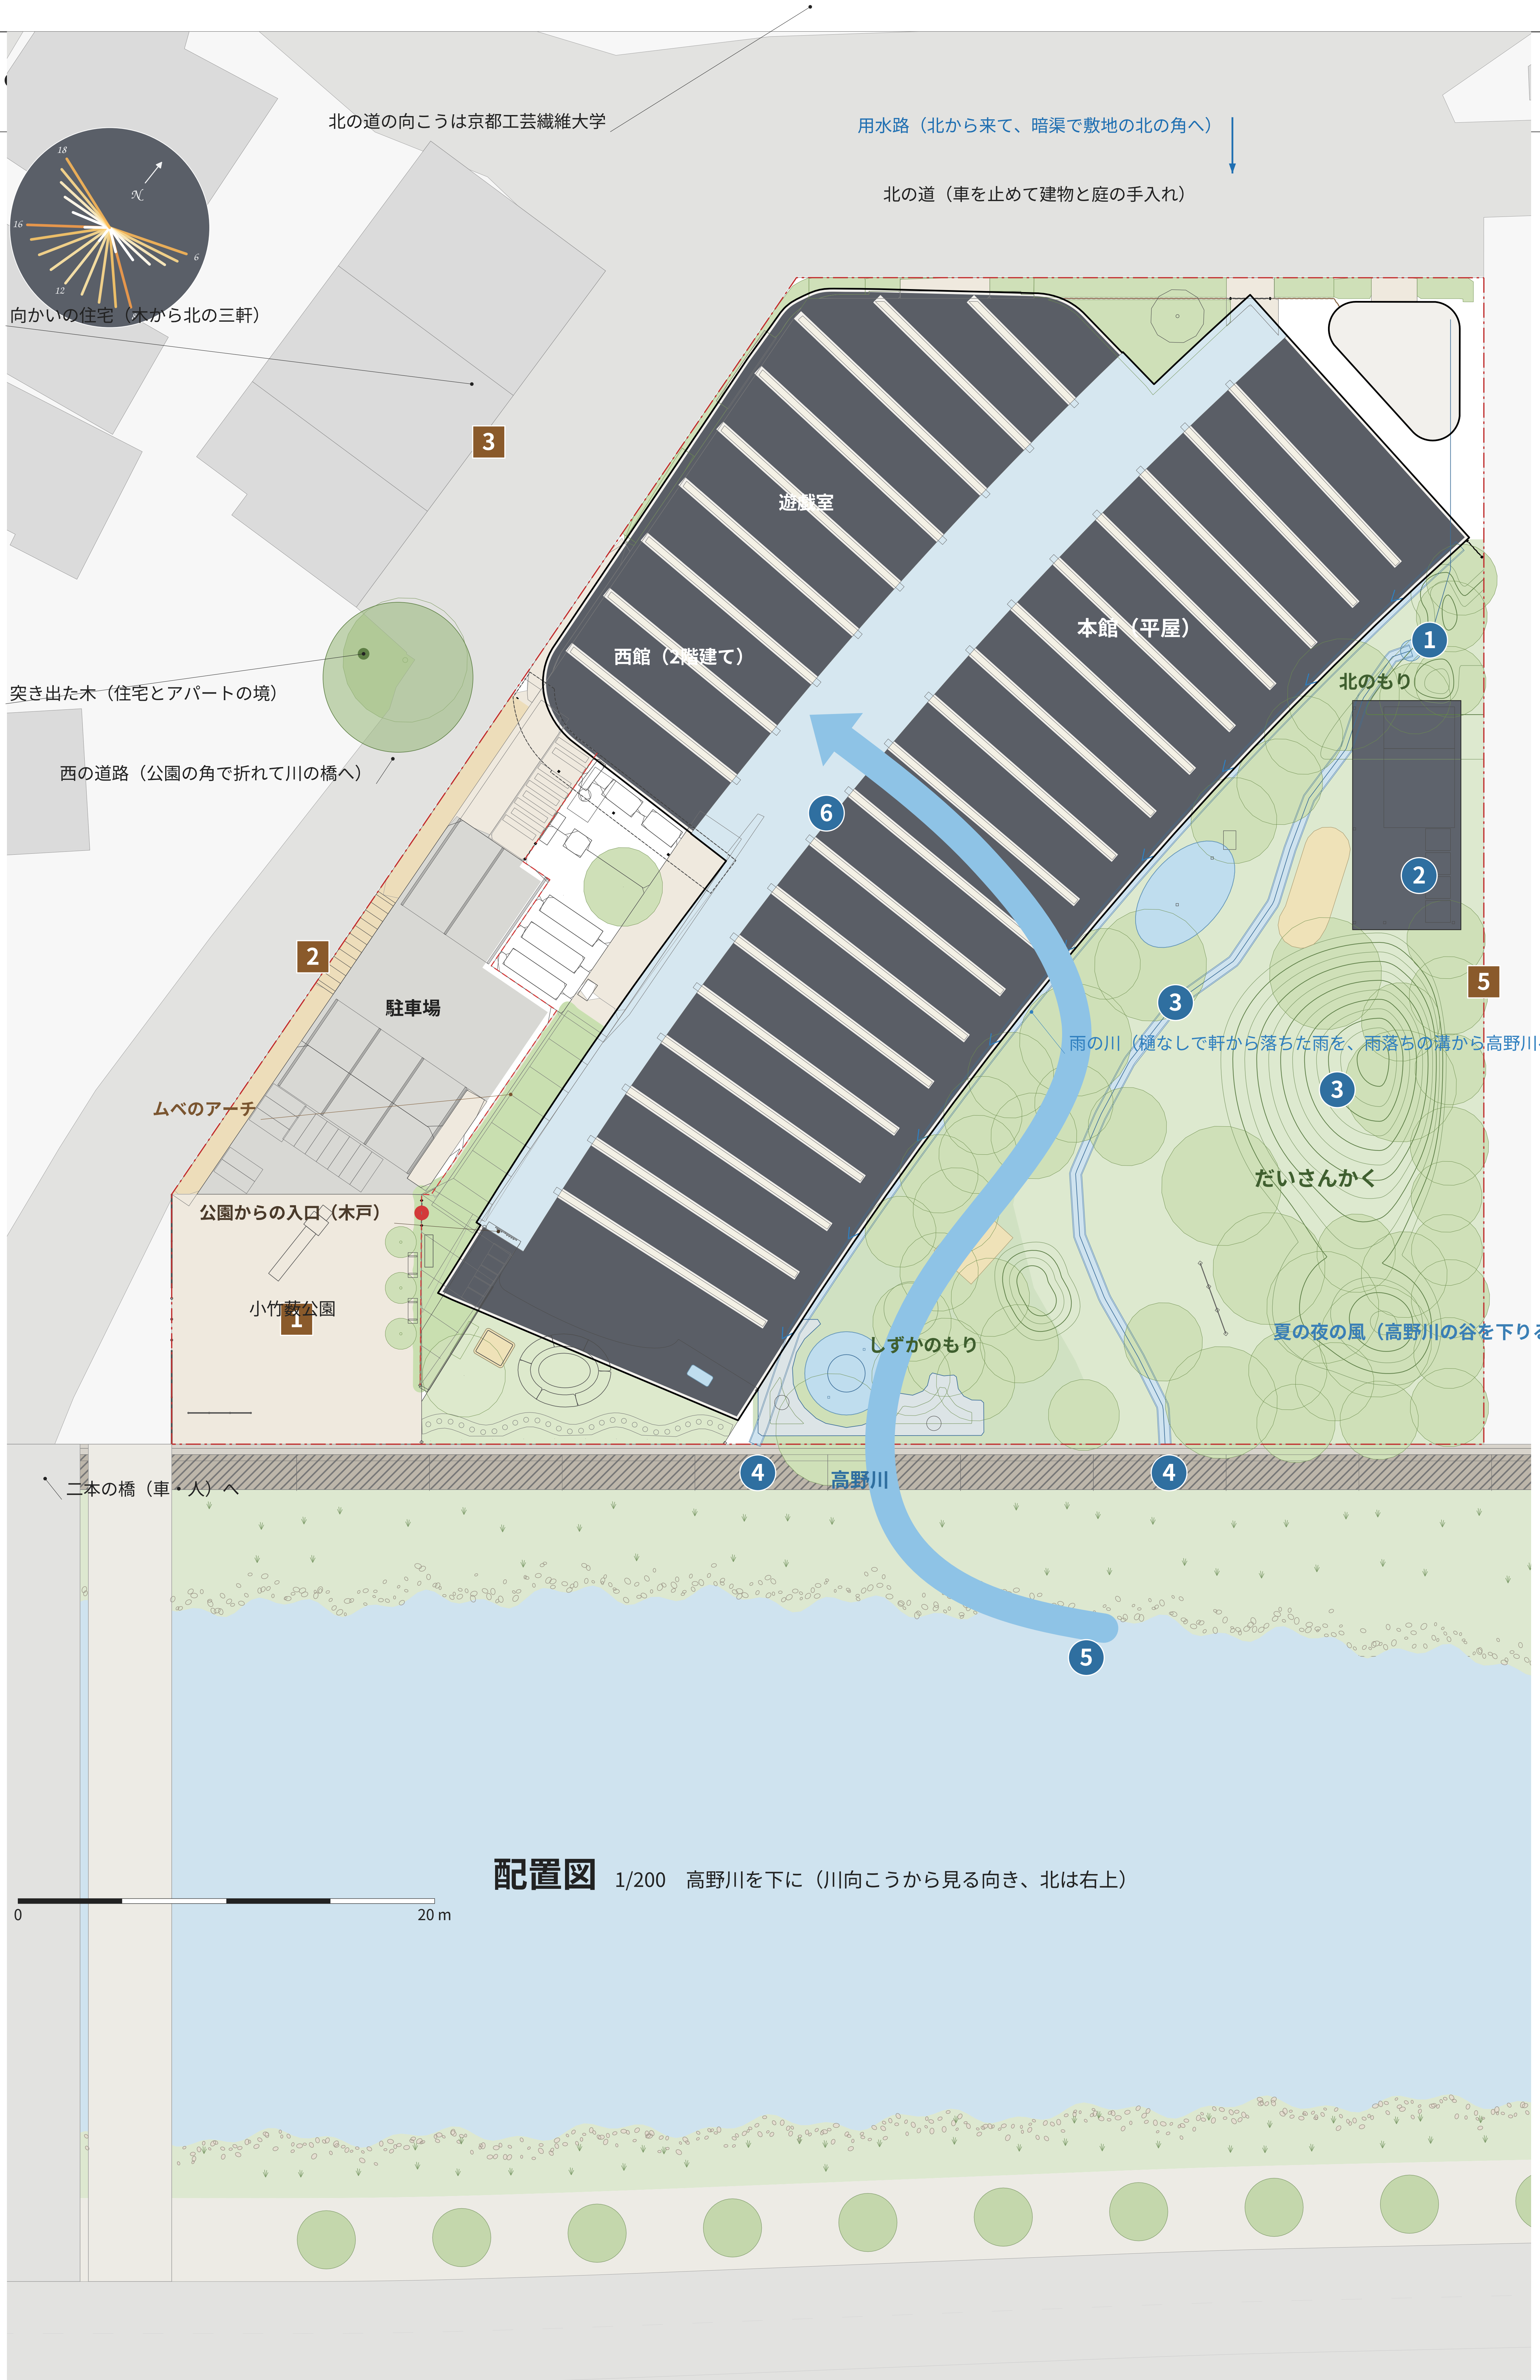
18
16
12
6
N
北の道の向こうは京都工芸繊維大学
用水路（北から来て、暗渠で敷地の北の角へ）
北の道（車を止めて建物と庭の手入れ）
向かいの住宅（木から北の三軒）
3
遊戯室
西館（2階建て）
本館（平屋）
1
北のもり
突き出た木（住宅とアパートの境）
西の道路（公園の角で折れて川の橋へ）
6
2
2
駐車場
5
3
雨の川（樋なしで軒から落ちた雨を、雨落ちの溝から高野川へ）
3
ムベのアーチ
だいさんかく
公園からの入口（木戸）
小竹薮公園
1
夏の夜の風（高野川の谷を下りる風）
しずかのもり
4
高野川
4
二本の橋（車・人）へ
5
0
20 m

配置図　1/200　高野川を下に（川向こうから見る向き、北は右上）

松ヶ崎の用水ネットワーク

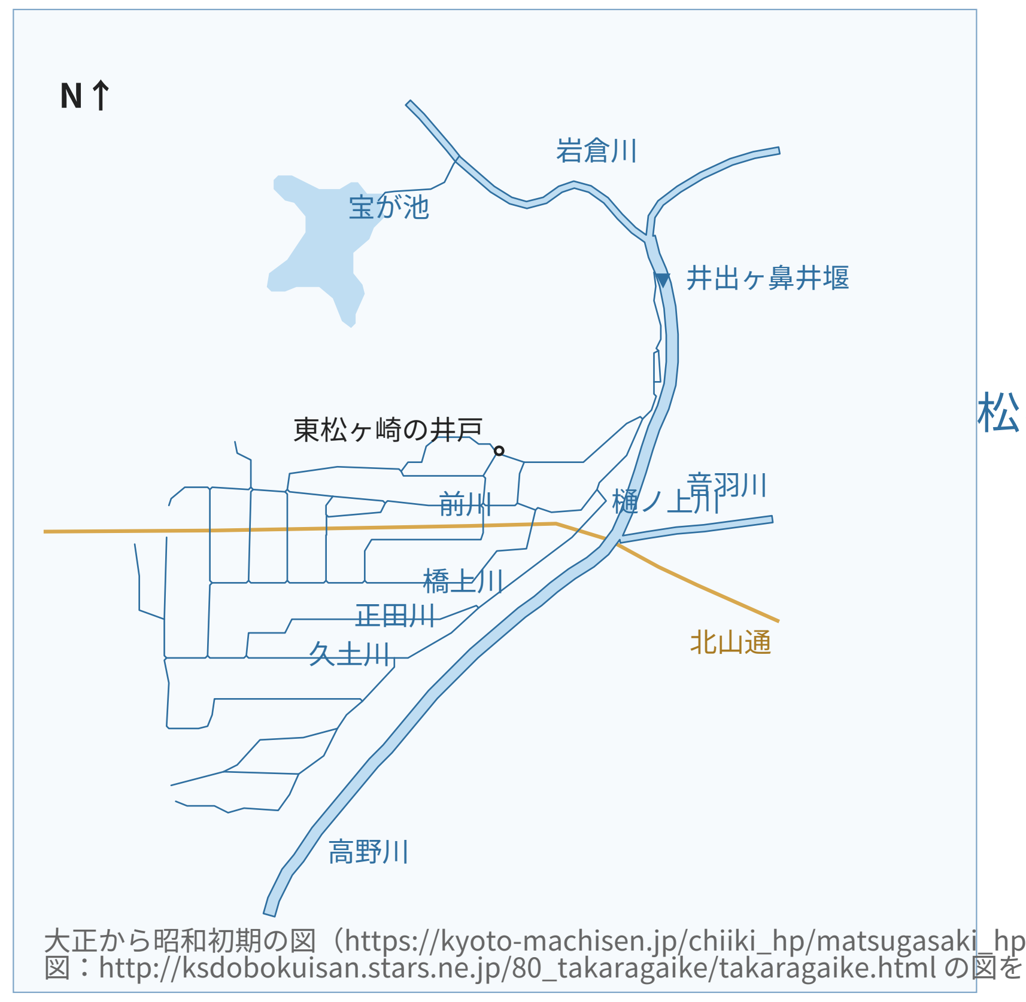
N ↑
岩倉川
宝が池
井出ヶ鼻井堰
東松ヶ崎の井戸
前川
樋ノ上川
音羽川
橋上川
正田川
久土川
北山通
高野川

大正から昭和初期の図（https://kyoto-machisen.jp/chiiki_hp/matsugasaki_hp/history/history.htm）
図：http://ksdobokuisan.stars.ne.jp/80_takaragaike/takaragaike.html の図をなぞって描き直し

松ヶ崎の用水ネットワーク

° 敷地

1 用水を借りる

井出ヶ鼻井堰に端を発する松ヶ崎の用水ネットワークから、水を借り、園庭の小川にする。

大正から昭和初期の図（https://kyoto-machisen.jp/chiiki_hp/matsugasaki_hp/history/history.h

2 野菜くずコンポスト

野菜くずや落ち葉をこどもたちの手で土に還す。発酵する暖かい土とミミズに驚く。野菜を育てる。命の循環を知る。

5 東の隣家への配慮

東の隣家との境は1 m下げ（セットバック）、園庭の小屋と植樹で視線と音をやわらげる。

5 風の道

夏の夜、高野川の谷を下りてくる涼しい風を、縁側の床下から越屋根へ抜く。床下に冷えをためて、昼の冷房を抑える。

3 高野川と比叡にみたてる

日本文化が育ててきた「みたて」。園内の小川と築山を高野川と比叡にみたてる。それを超えて視線を遠くにすると、高野川を超えて比叡の山。

4 水の行方を見る

小川は暗渠に隠さず高野川に注ぐ。屋根に降った雨は、雨落ちに落ち、雨水浸透側溝と雨庭を経て、溢れは高野川に。

［割付の注記］フォーカス：周囲の自然環境との関係と地域環境への配慮。配置図の上に夏の夜の風・比叡への視線　／　目に入る順：タイトルと趣旨 → 真ん中の配置図 → 左右の箱（青＝自然環境、茶＝地域）→ 用水のネットワーク・地域のなかの敷地

松ヶ崎こども園　2景観

園庭の側の立面図 1/100　円弧の中心の方向から弧の真ん中に正対

園庭にひらく　縁側と深い軒が57 m続き、3 mごとの柱とガラス戸の半分が開く。屋根の光の筋が架構を照らし、こどもは縁側から庭へ下りる。

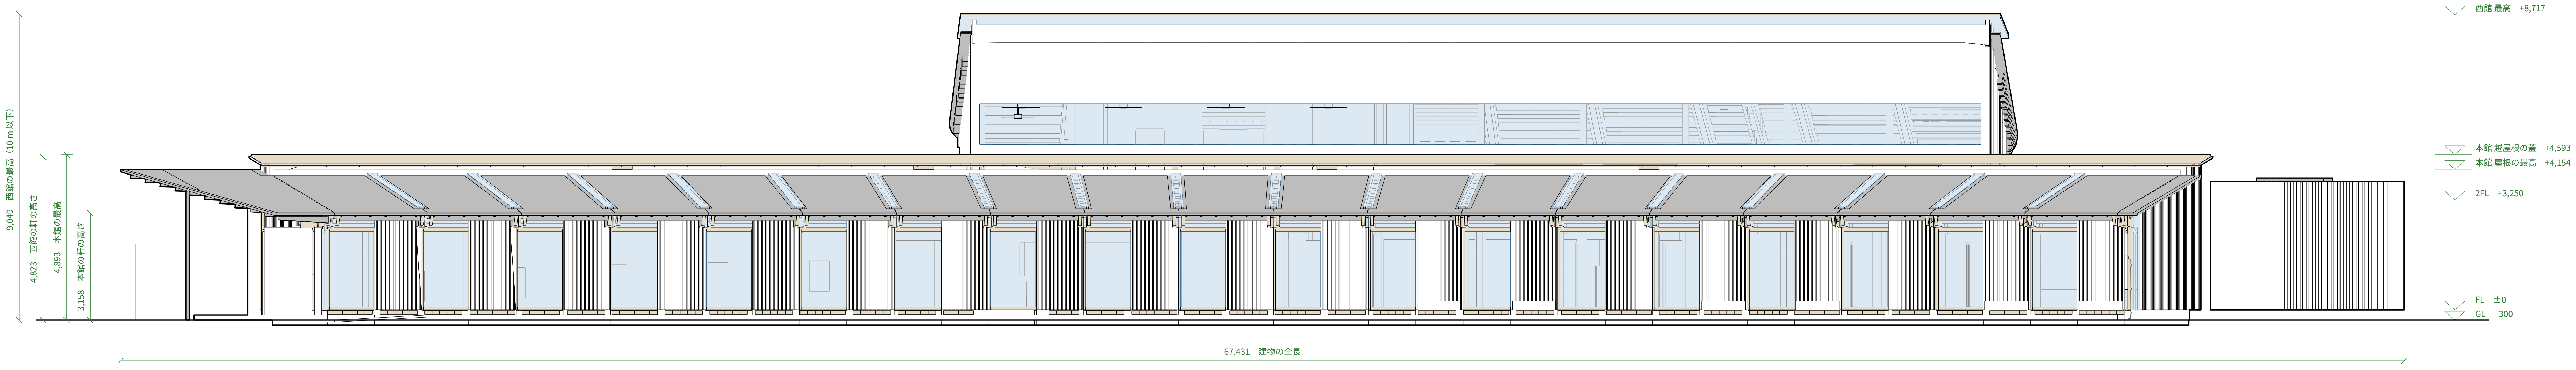
9,049　西館の最高（10 m 以下）
4,823　西館の軒の高さ
4,893　本館の最高
3,158　本館の軒の高さ
西館 最高　+8,717
本館 越屋根の蓋　+4,593
本館 屋根の最高　+4,154
2FL　+3,250
FL　±0
GL　−300
67,431　建物の全長

道路の側の立面図 1/100　西の道路から

まちに溶け込み、やさしく守る　杉の大和張りの静かな板の壁。西館は向かいの住宅に向けて1階の高さまで下げ、窓は小さく面ごとのリズムで。道からは中が見えすぎず、園を包む。

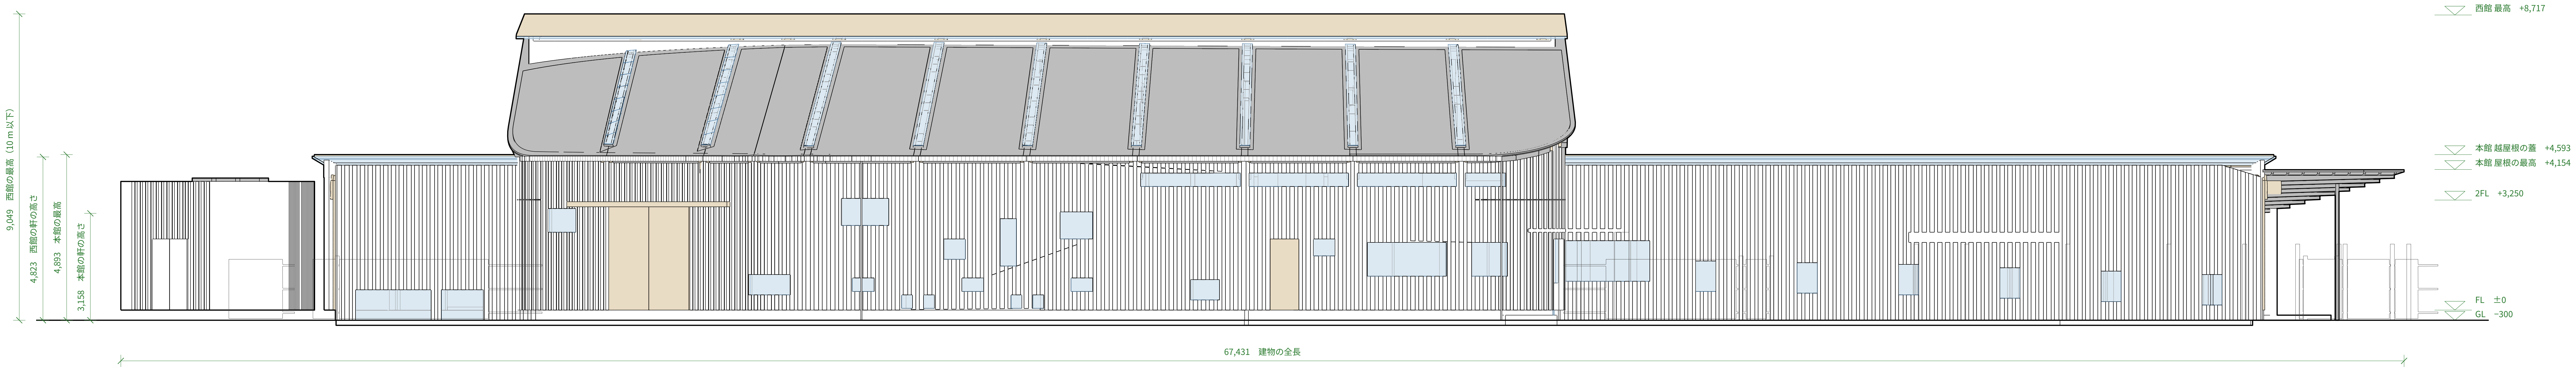
9,049　西館の最高（10 m 以下）
4,823　西館の軒の高さ
4,893　本館の最高
3,158　本館の軒の高さ
西館 最高　+8,717
本館 越屋根の蓋　+4,593
本館 屋根の最高　+4,154
2FL　+3,250
FL　±0
GL　−300
67,431　建物の全長

透視図（A4）　公園の角から西の道を見る 目の高さ1.5 m、左に向かいの住宅、右に西館の低い軒

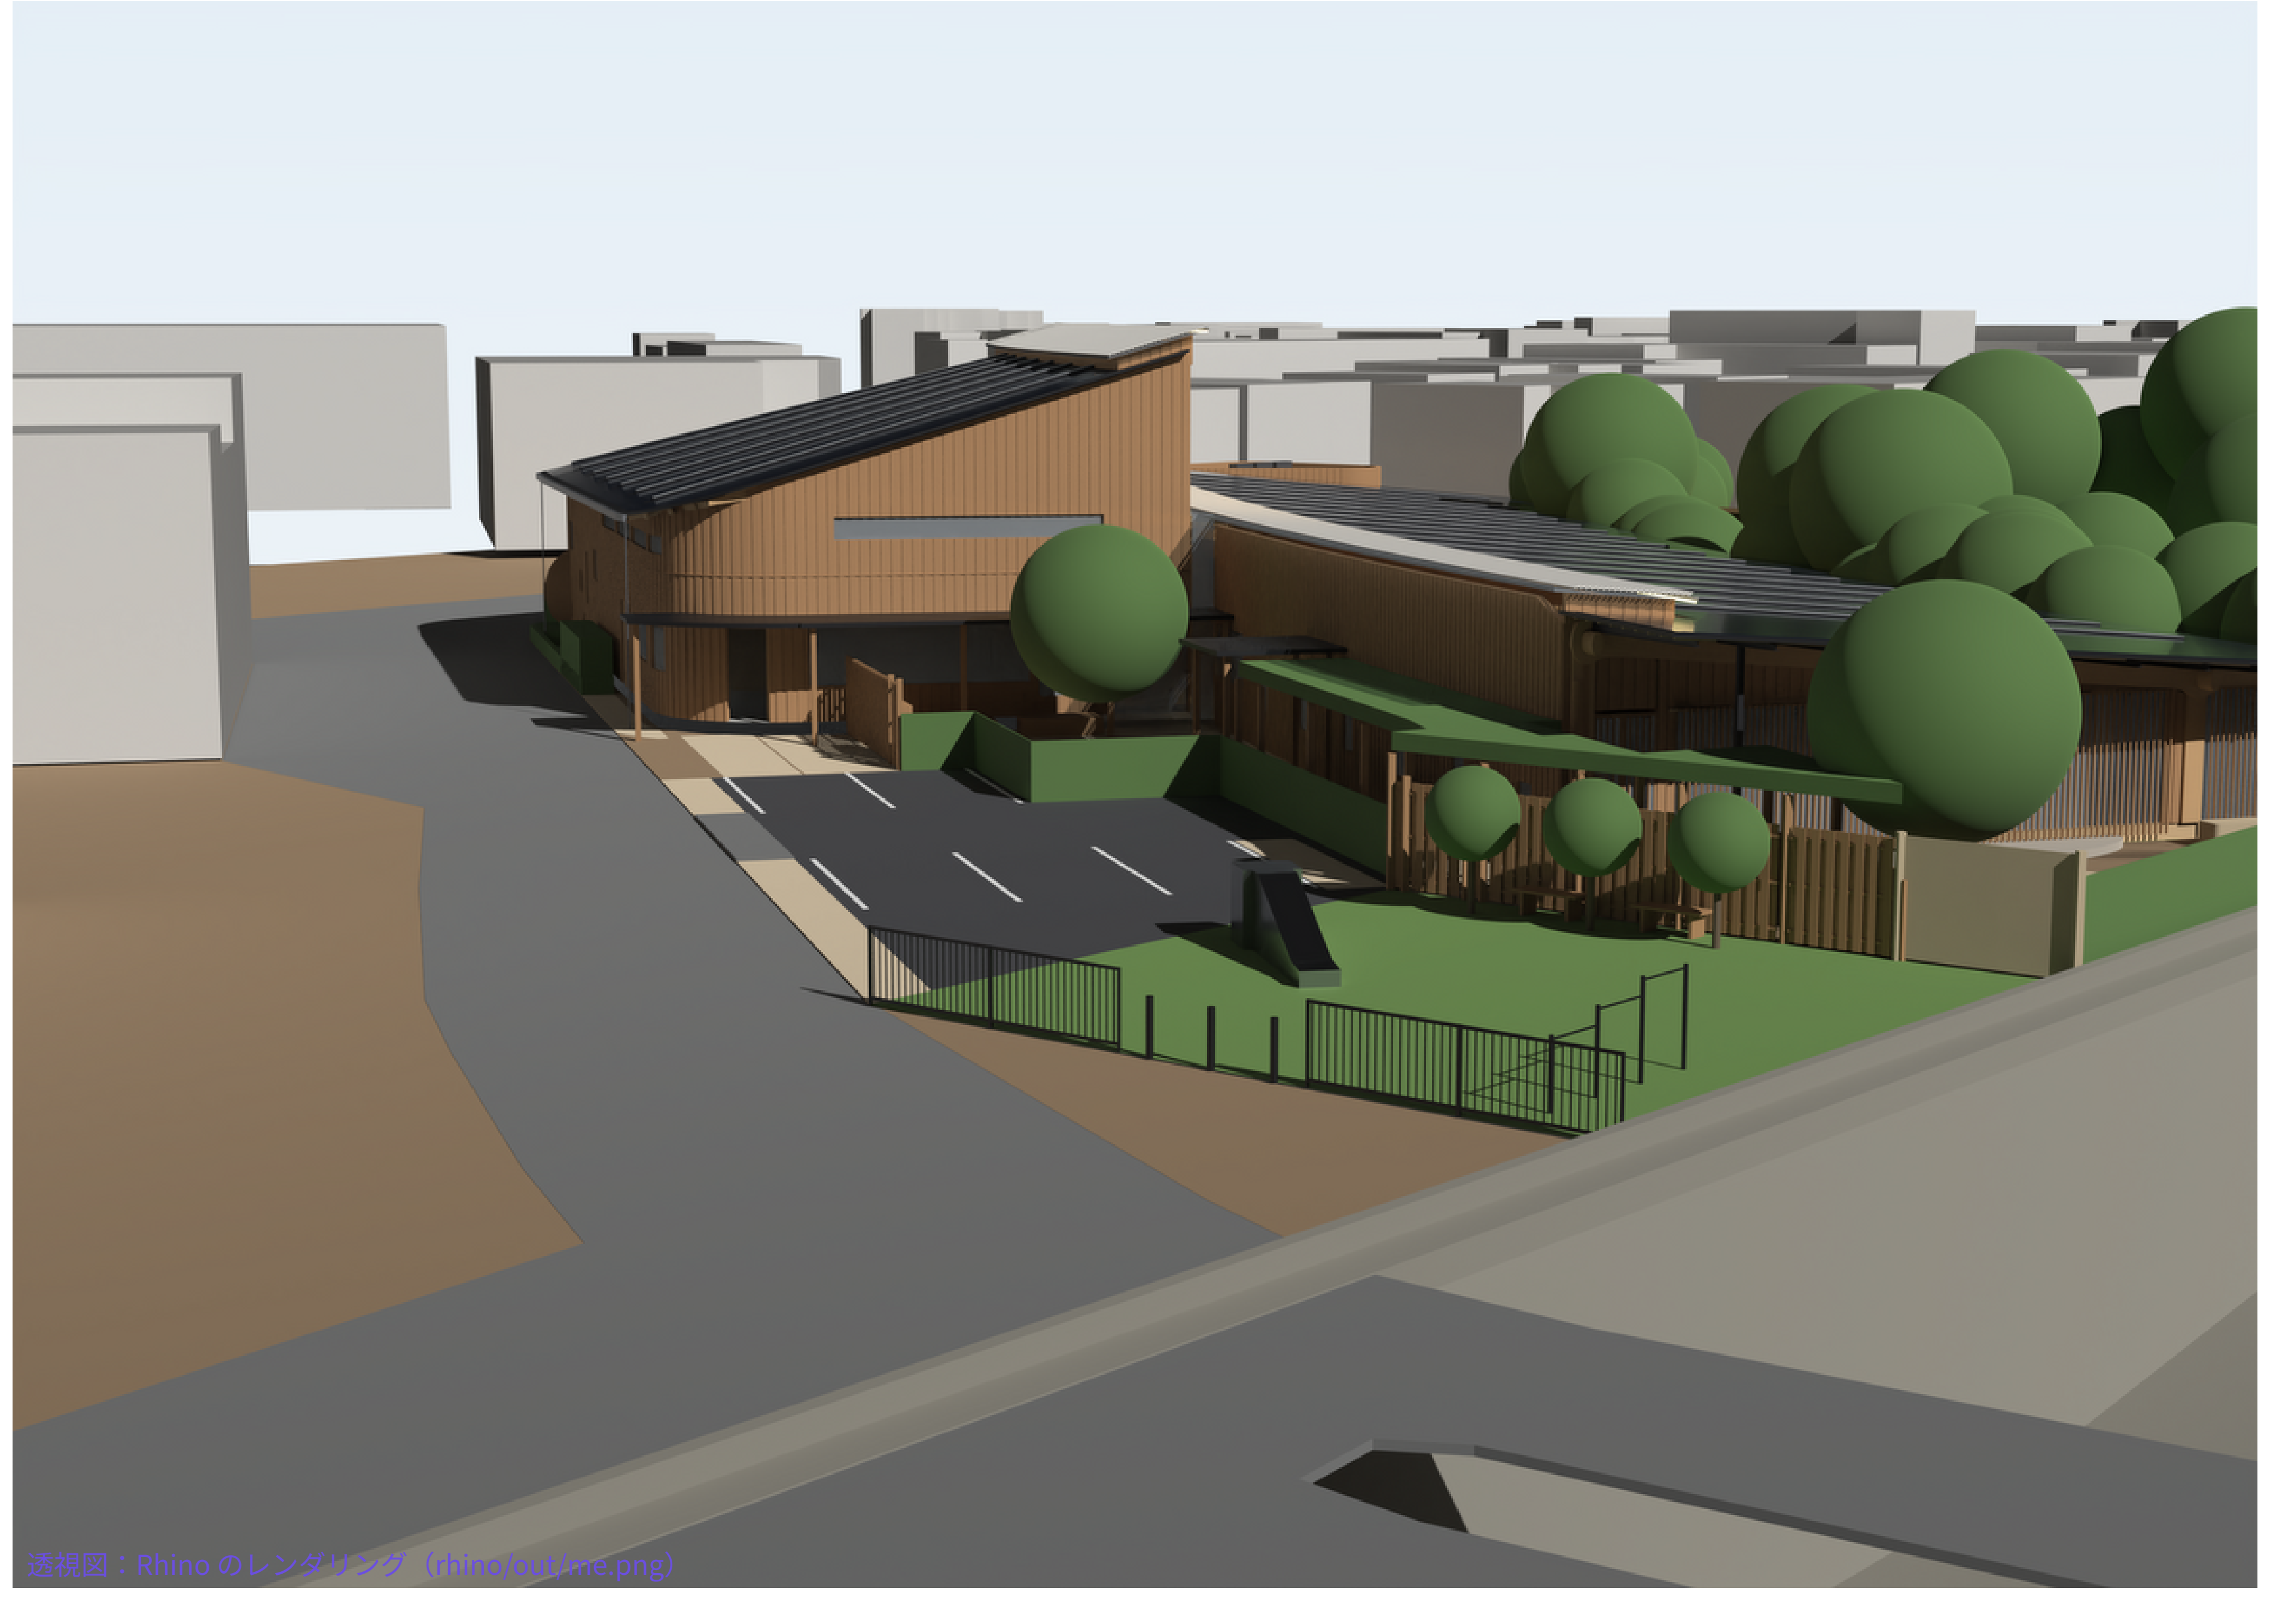
透視図：Rhino のレンダリング（rhino/out/me.png）

沿川の景観　昼 高野川の向こう岸の歩道から、目の高さ1.5 m

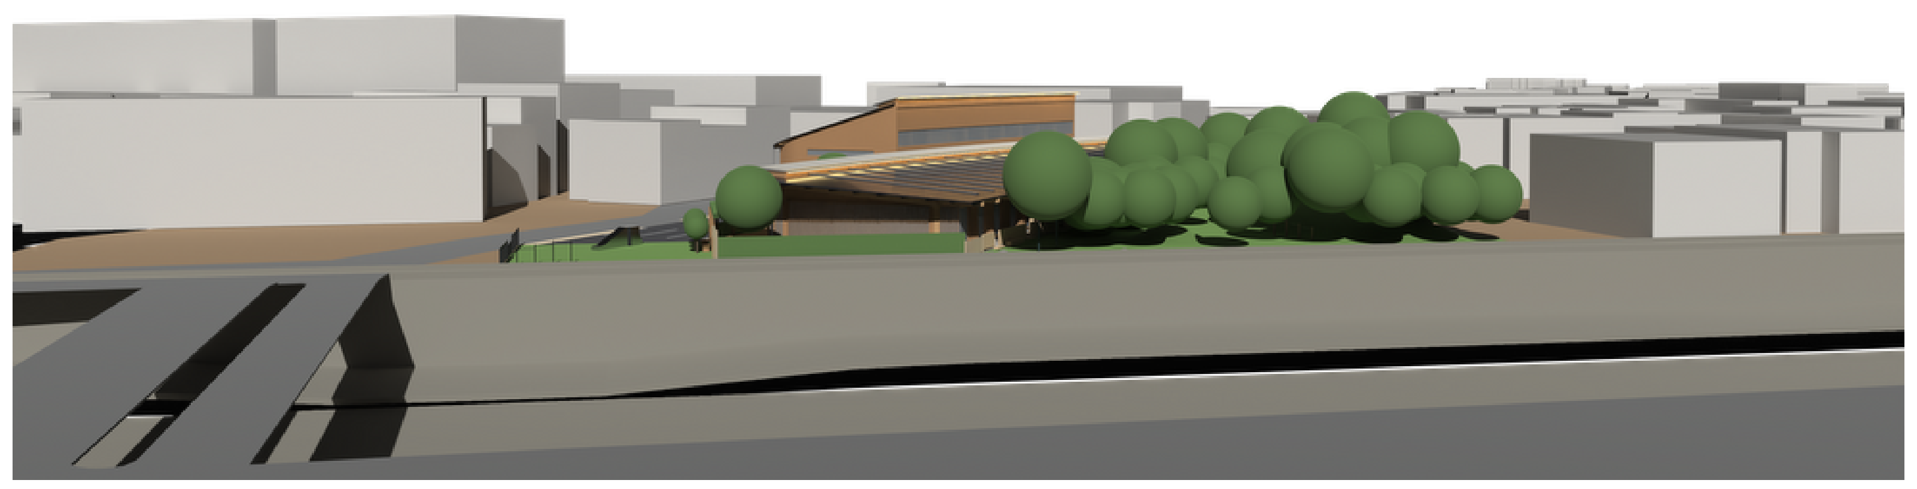

沿川の景観　夜 高野川の向こう岸の歩道から、目の高さ1.5 m　本館と西館の越屋根の光

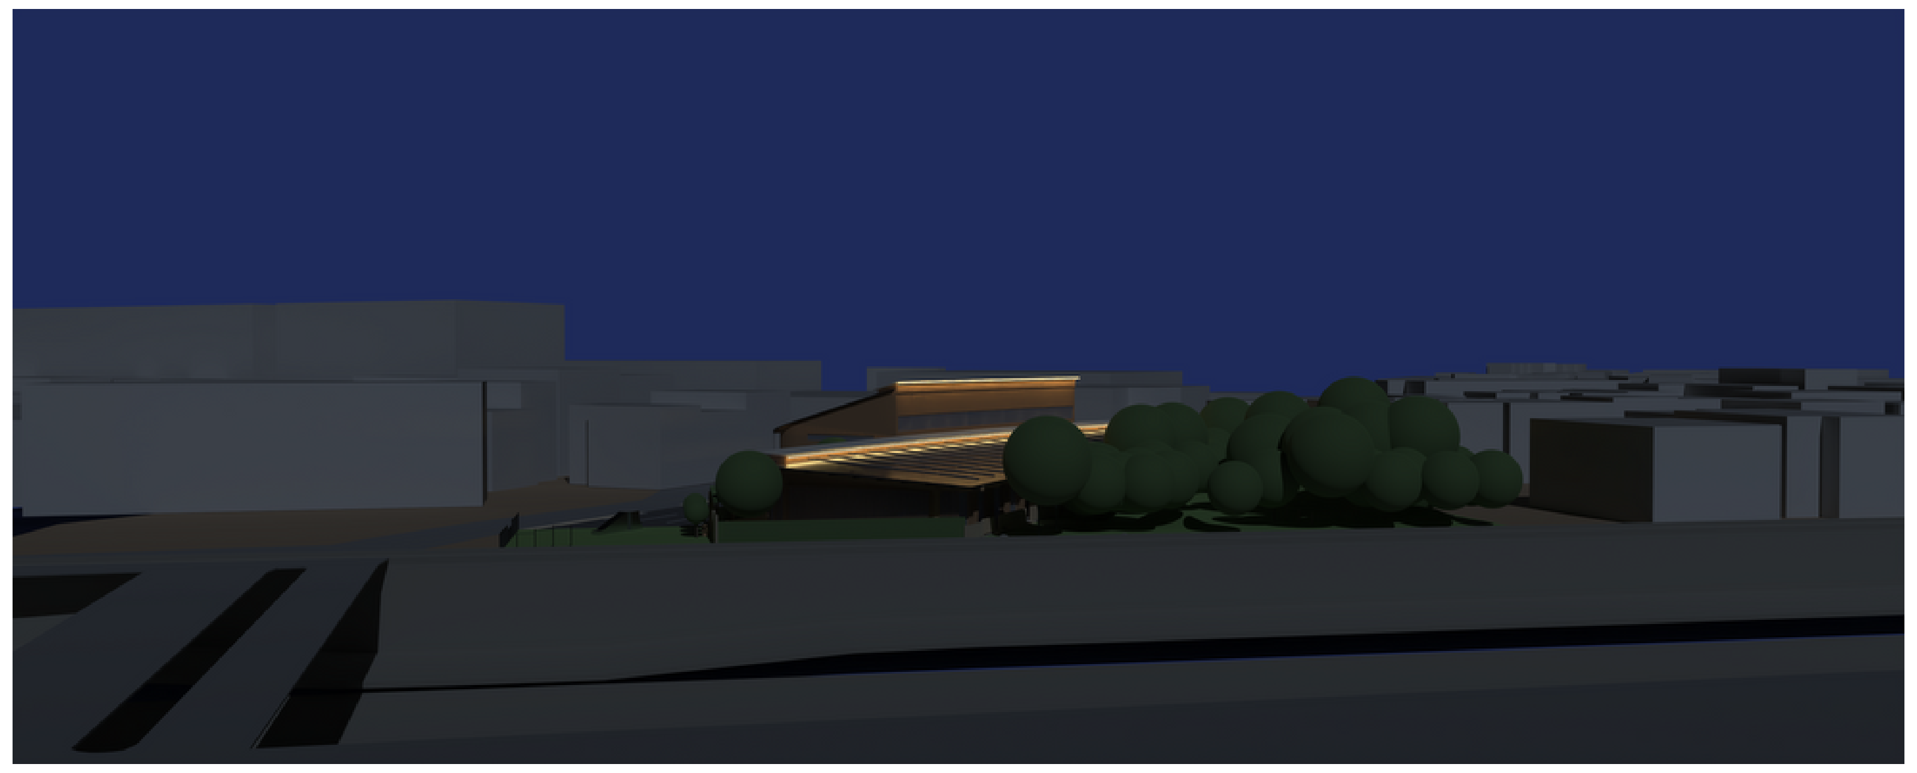

景観の法規

用途地域：第一種低層住居専用地域（都市計画法）。最高の高さは西館の棟で約9.0 m（GLから）。

風致地区（京都市風致地区条例）：高野川特別修景地域（同条例第6条第1項による指定、許可基準は基準告示第7条）。右岸の基準：既存の樹木を保全する／河川に面する部分に植栽帯を設ける／建築物は原則として河川の側に勾配のある下屋を設けた和風の外観とする。対応：川の側に園庭の林と生垣、南に深い軒（下屋）、深い軒と縁側・杉の大和張りの板壁・ゆるい勾配の屋根。

屋根の太陽光：同基準第7条第1項(80)で屋根に太陽光発電装置を原則として設けない。屋根材と一体の太陽電池で、黒い金属の屋根と見分けがつかず周辺の風致に不調和でない（同(80)の例外）。こども園で、同第7条第2項の例外（建築物全体のデザイン・公益上やむを得ない学校等の施設）にもあたるとする。

遠景デザイン保全区域（京都市眺望景観創生条例）：外壁・屋根に禁止色を用いない、山並みと調和する。対応：黒い金属の屋根、木の色のまま。

素材と色

🟫 木の柱・梁（木の色のまま）
🟫 杉の大和張り（銀鼠に枯れる）
⬛ 黒い金属の屋根（太陽光一体）
⬜ 越屋根のガラス・縁側の白
🟩 生垣と園庭の緑

敷地が高野川の右岸にあるという読みは要確認（決定事項：たたき台の読み）

建築設計実習 II — I　2026.11.05　木田

［割付の注記］フォーカス：建物に正対する二つの立面（園庭の側・道路の側）で、伸びやかな梁と縁側、西館の立ち上がり。下の段に外から見た姿：目の高さの透視図（公園の角から西の道、お向かいさんとの関係）と、川の向こう岸から見た沿川の景観（昼・夜、透視図）　／　目に入る順：園庭の側・道路の側の立面図 → 透視図（A4）・沿川の景観（昼・夜）→ 景観の法規・素材と色

松ヶ崎こども園　3断面と環境

縦断面図A　1/100　保育室の中ほどの弧で切って展開、西を見る（左が南の高野川）

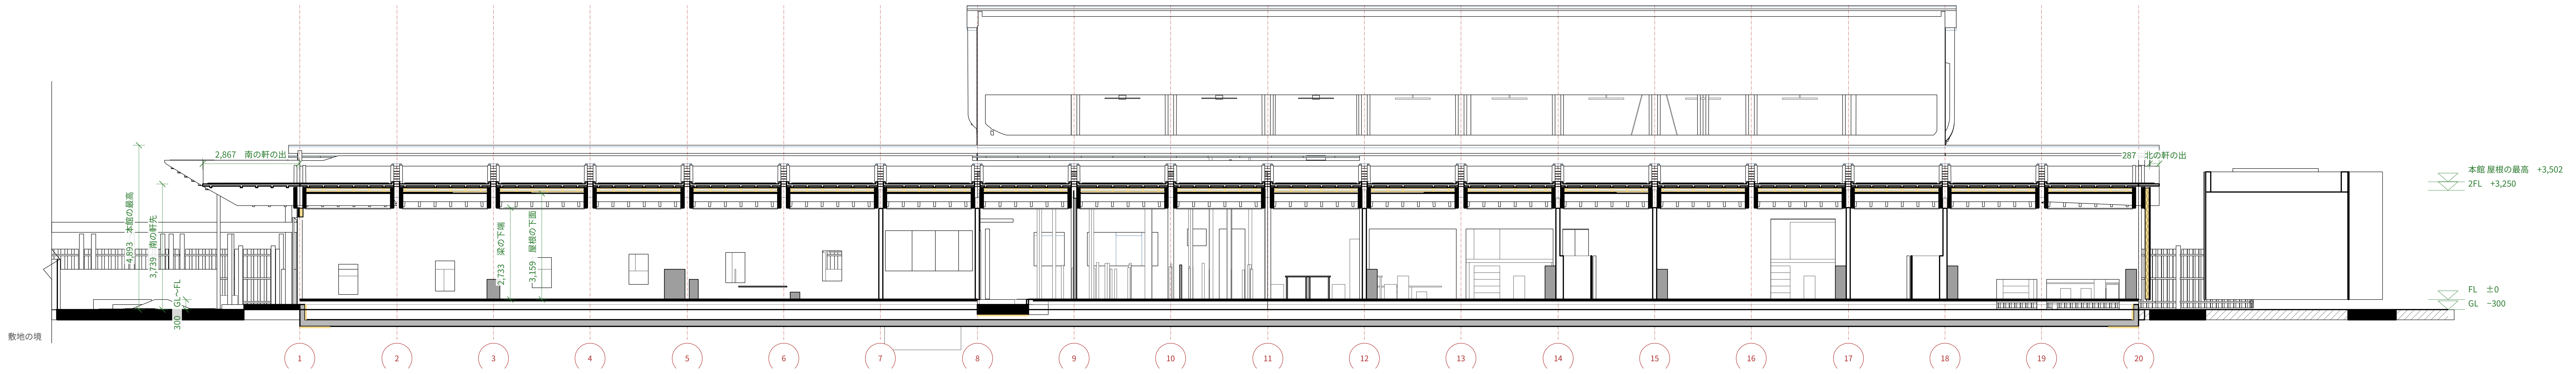

2,867　南の軒の出
287　北の軒の出
4,893　本館の最高
3,739　南の軒先
GL～FL
300
2,733　梁の下端
3,159　屋根の下面
敷地の境
本館 屋根の最高　+3,502
2FL　+3,250
FL　±0
GL　−300
1
2
3
4
5
6
7
8
9
10
11
12
13
14
15
16
17
18
19
20

断面図C　東西に切る（4歳・遊戯室）　1/100　空気の環境：本館と西館の架構、昼と夏の夜の風の道

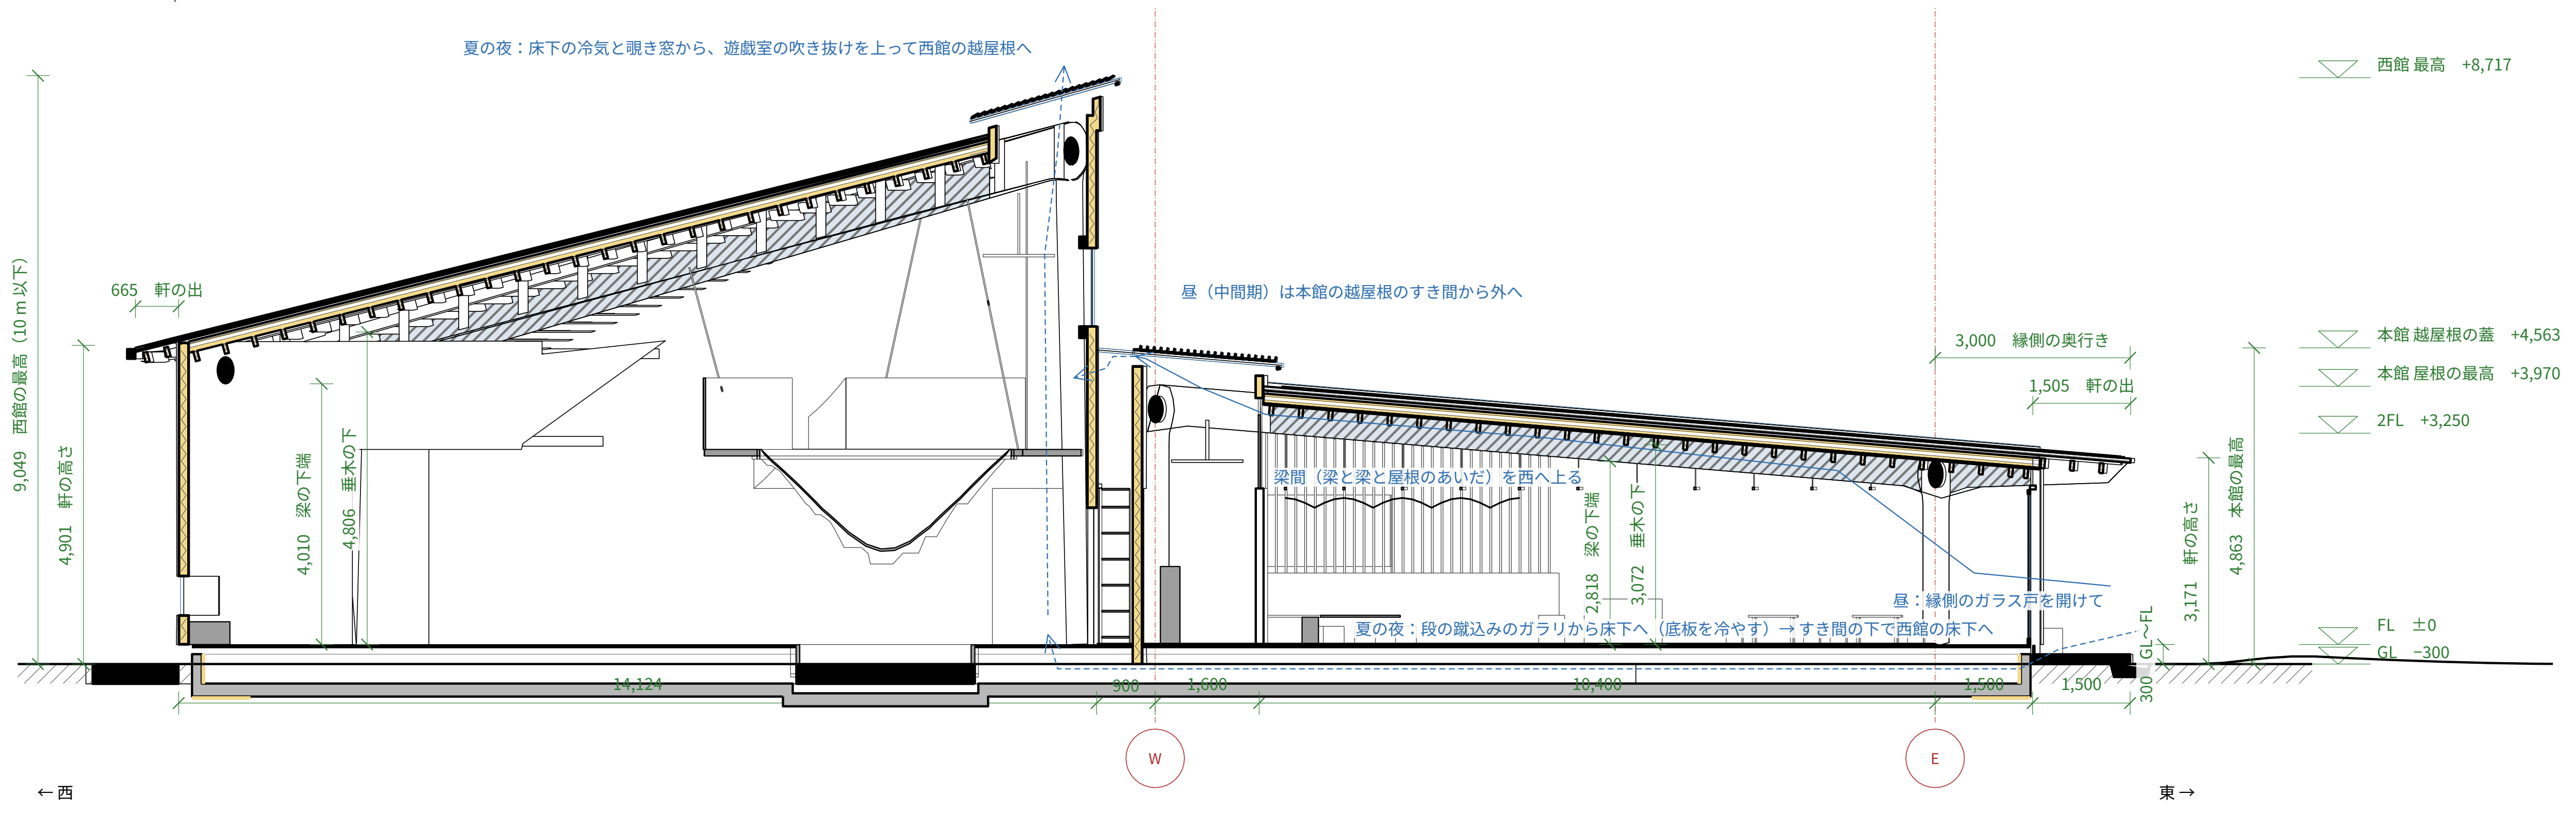

夏の夜：床下の冷気と覗き窓から、遊戯室の吹き抜けを上って西館の越屋根へ
昼（中間期）は本館の越屋根のすき間から外へ
梁間（梁と梁と屋根のあいだ）を西へ上る
昼：縁側のガラス戸を開けて
夏の夜：段の蹴込みのガラリから床下へ（底板を冷やす）→すき間の下で西館の床下へ
665　軒の出
9,049　西館の最高（10 m以下）
4,901　軒の高さ
4,010　梁の下端
4,806　垂木の下
2,818　梁の下端
3,072　垂木の下
3,000　縁側の奥行き
1,505　軒の出
3,171　軒の高さ
4,863　本館の最高
GL～FL
300
14,124
900
1,600
10,400
1,500
1,500
西館 最高　+8,717
本館 越屋根の蓋　+4,563
本館 屋根の最高　+3,970
2FL　+3,250
FL　±0
GL　−300
W
E
←西
東→

断面図D　本館の横断（光の筋で切る）　1/100　北を見る　光の環境：光の筋の鏡面の溝・東のガラス戸・深い軒・西の吹き抜けの越屋根

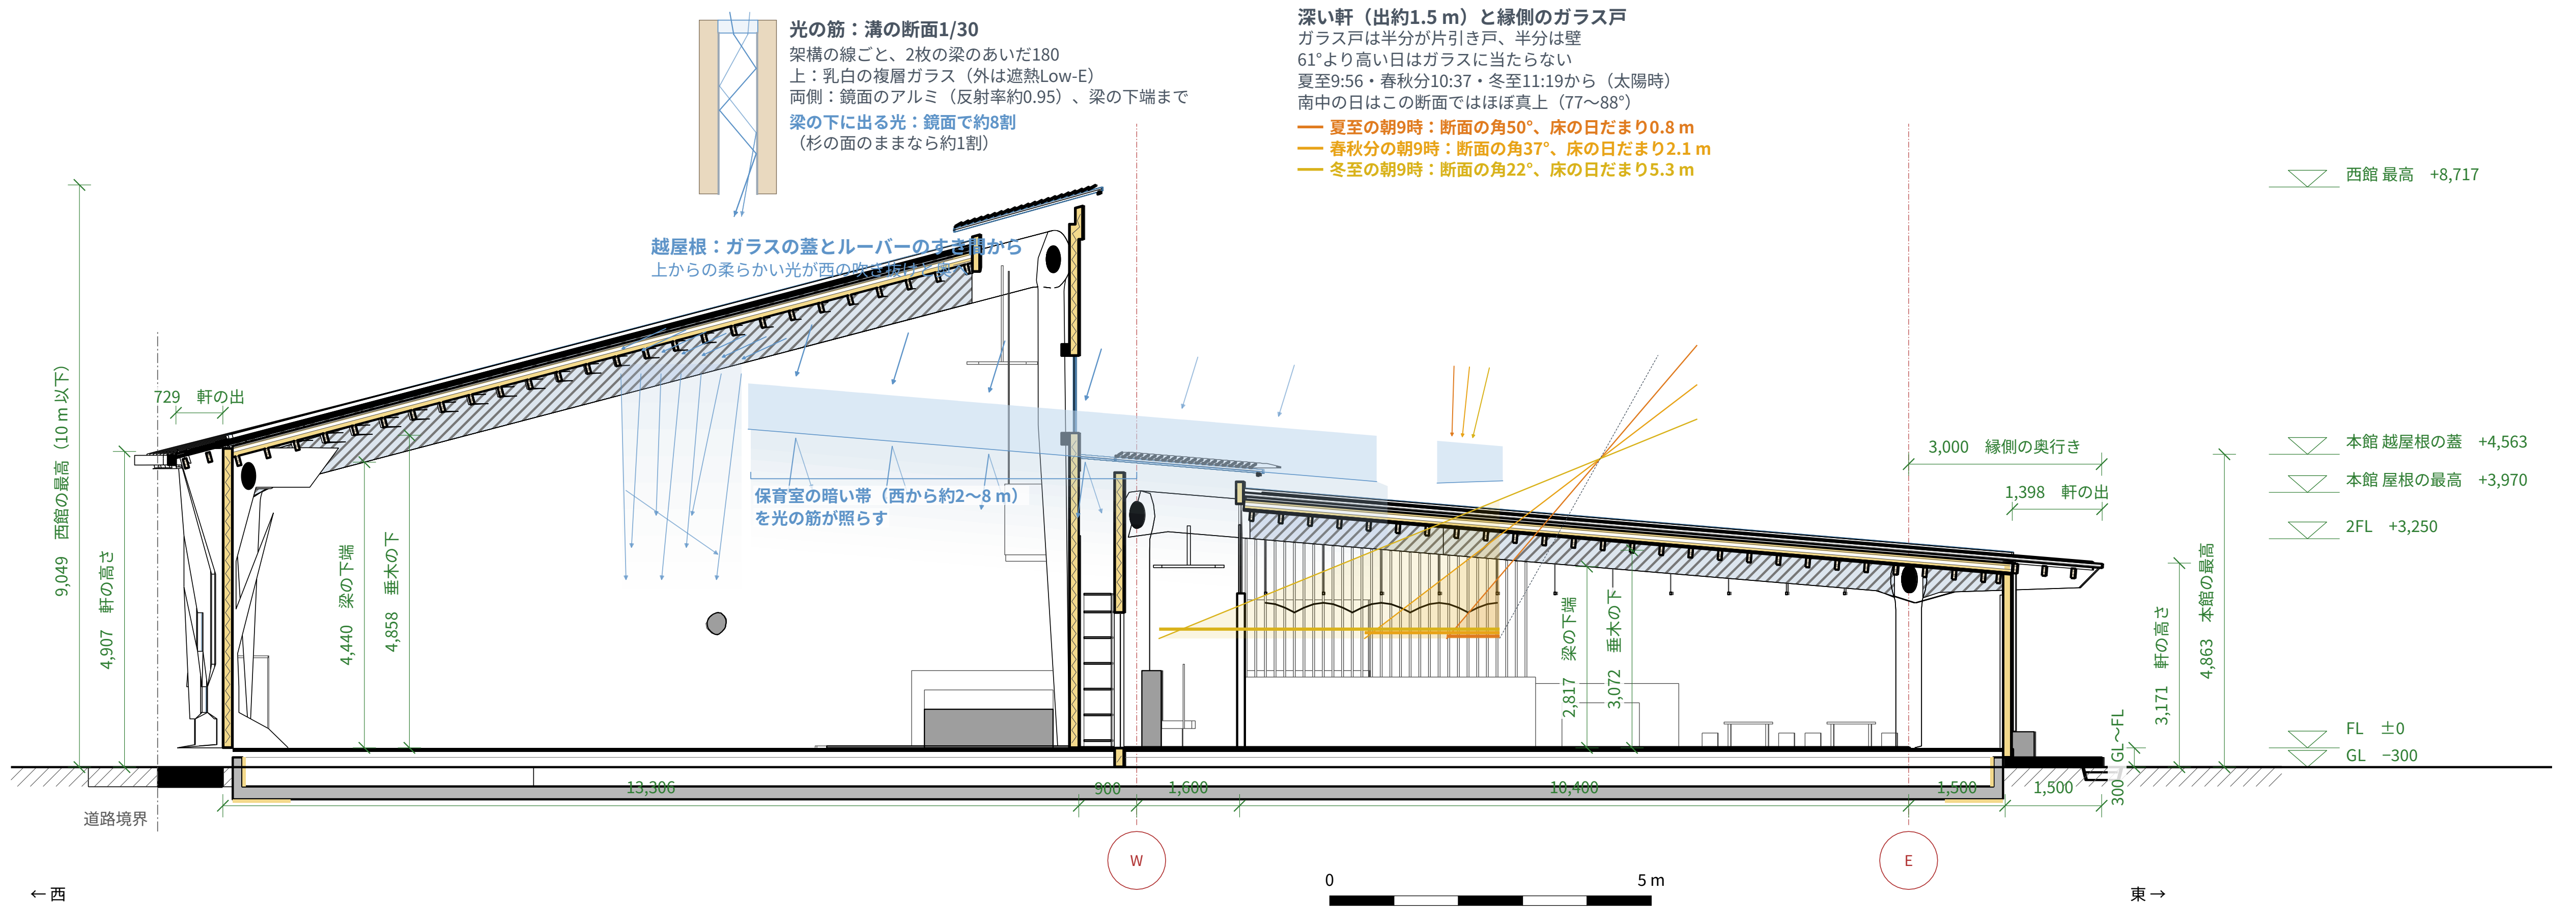

光の筋：溝の断面1/30
架構の線ごと、2枚の梁のあいだ180
上：乳白の複層ガラス（外は遮熱Low-E）
両側：鏡面のアルミ（反射率約0.95）、梁の下端まで
梁の下に出る光：鏡面で約8割
（杉の面のままなら約1割）
深い軒（出約1.5 m）と縁側のガラス戸
ガラス戸は半分が片引き戸、半分は壁
61°より高い日はガラスに当たらない
夏至9:56・春秋分10:37・冬至11:19から（太陽時）
南中の日はこの断面ではほぼ真上（77～88°）
— 夏至の朝9時：断面の角50°、床の日だまり0.8 m
— 春秋分の朝9時：断面の角37°、床の日だまり2.1 m
— 冬至の朝9時：断面の角22°、床の日だまり5.3 m
越屋根：ガラスの蓋とルーバーのすき間から
上からの柔らかい光が西の吹き抜けと奥へ
保育室の暗い帯（西から約2～8 m）
を光の筋が照らす
729　軒の出
9,049　西館の最高（10 m以下）
4,907　軒の高さ
4,440　梁の下端
4,858　垂木の下
2,817　梁の下端
3,072　垂木の下
3,000　縁側の奥行き
1,398　軒の出
3,171　軒の高さ
4,863　本館の最高
GL～FL
300
13,306
900
1,600
10,400
1,500
1,500
道路境界
西館 最高　+8,717
本館 越屋根の蓋　+4,563
本館 屋根の最高　+3,970
2FL　+3,250
FL　±0
GL　−300
W
E
0
5 m
←西
東→

季節ごとの空気環境

夏は夜の外気で床下の重さを冷やし、昼はその冷えと、触れて冷たい壁と天井扇で過ごす。冬は閉じて床から暖め、熱と湿気を逃がさない。春と秋は床下から越屋根へ風を通す。

季節	開け閉め	動かすもの	効くもの
夏の昼	窓・越屋根・床下の入口を閉じる	放射冷房のパネル・天井扇（下向き）・床下の送風	深い軒、夜に冷やした底板
夏の夜	縁側のガラリと西館の越屋根を開く（本館の越屋根は閉じる）	開け閉めは自動（外気が涼しいとき・雨で閉じる）	外気が床下の底板を冷やす。遊戯室の吹き抜けの高低差約8 mで引く
春・秋	窓・越屋根を開く	機械は止める	通風（梁間から越屋根へ）
冬	すべて閉じる	床下の暖房・全熱交換の換気・加湿・天井扇（上向きに弱く）	断熱と気密。ガラス戸の際の床からの暖気がガラスの冷えを止める

> **放射冷房のパネル**
> 保育室と遊戯室の壁、こどもの手の届く高さに置く。表面は約15°Cで、触れて「つめた！」とわかる。結露した水を外へ流して除湿も兼ねる。風が無いので静かで、午睡を妨げない。

環境への配慮（LEED v5 Goldを目指す）

LEED v5（USGBC）　https://www.usgbc.org/leed/v5

統合的なプロセス（IP）	一つの形で二つ以上を解く。本館の弧＝朝の日と、夏の夜に谷を下りる冷気（1枚目）。片流れの屋根＝景観と、越屋根へ上る空気の流れ（断面C）。縁側の段のガラリ＝夜の外気を床下へ入れ、ガラス戸をすっきり保つ。井戸＝冷暖房の熱源と、災害時の近隣の水
立地と交通（LT）	車は5台に絞り、送迎は徒歩と自転車（駐輪21台）。西の道に歩道を開く
持続可能な敷地（SS）	小竹薮公園と既存の木を残す。園庭の林。雨庭と浸透側溝で雨を敷地に返す
水の効率（WE）	雨を庭へ。地下水を使う
エネルギーと大気（EA）	断熱・気密、深い軒と遮熱Low-Eで日射を切る、ベタ基礎の底板に夜の冷えをためる、放射冷房と全熱交換、地下水を熱源にしたヒートポンプ、屋根材型の太陽光と蓄電池
材料と資源（MR）	北山杉の間伐材、木造。3 mの架構は残し中は変えられる（スケルトン＆インフィル）。野菜くずのコンポスト
室内環境の質（EQ）	光の筋の鏡面で奥まで昼光。風の音のない放射冷房。自然換気（床下→梁間→越屋根）。静養室と大人の便所は別の換気。2階の窓から川と空
地域の優先（PR）	災害時の持ちつ持たれつ：太陽光と蓄電池の電気と、地下水を近隣に提供できる。浸水のときは京都工芸繊維大学へ避難の協定

計画
120.5
60.0
181.2
266.1
17.2
982.2
69.8
60.4
30.1
65.7
13.9
30.0
36.2
○
○
1,310.9

建築設計実習Ⅱ—Ⅰ　2026.11.05　木田

［割付の注記］フォーカス：上に縦断A（弧の長さ）を一続きに。その下で二つの横断（1/100）が主役：断面Cに空気の環境（本館と西館の架構と風の道）、断面D（本館、光の筋で切る）に光の環境。右の列に季節ごとの空気環境・環境への配慮・inspired byと面積表　／　目に入る順：縦断A（上の帯）→断面C（空気）→季節ごとの空気環境・配慮→断面D（光）→inspired by・面積表

松ヶ崎こども園　4平面図　1階・2階

平面図　1階　FL+1500 で切断／2階（西館）2FL+1000 で切断　1/100

高野川が下に（配置図と同じ向き）。2階は西の道路の外に同じ向きで描いた（遊戯室の吹き抜けから見下ろす）。一点鎖線は敷地の境。二点鎖線は切断より上にある物（屋根の外形・庇屋根・2階の床の縁など）

吹抜（遊戯室）
会議室 29.8 m²
職員の更衣・ロッカー 12.9 m²
休憩室 60.4 m²
ホール 18.8 m²
便所 2.9 m²
下
12,194　2階の南北（南の妻の外面～2階の床の北の縁、東の縁で）
11,366　2階の東西（西の外面～2階の床の東の縁）
30,194　西館の南北の全長（東の線で）　架構 8～18・10 スパン
1,000　西の道路境界まで（西の外壁は後退の1 mの線の上）
14,235　西館の東西の幅（架構 15 の線で、外壁の外面から外面）
遊戯室 266.1 m²
倉庫 4.6 m²
倉庫 4.8 m²
倉庫 3.8 m²
階段 4.4 m²
上
調理の更衣・便所・前室 6.3 m²
キッチン 59.4 m²
1,600　2階の床の東の縁（東の線から）
R205,000（W通り）
1,156　北東の隣地境界まで（機械室）
R193,000（E通り）
2,081　北東の隣地境界まで（本館）
5歳 60.6 m²
路地 15.1 m²
倉庫 6.5 m²
便所 8.6 m²
4歳 60.3 m²
便所 3.0 m²
倉庫 3.5 m²
路地 15.2 m²
3歳 60.3 m²
便所 8.6 m²
背骨（W通り）の弦は約56.8 m・矢高は約2.0 m（二点鎖線）
東の帯 26.0 m²
多目的便所 8.0 m²
事務室 22.2 m²
西吹き抜け 63.3 m²
西吹き抜け＝越屋根の幅
ホール 75.2 m²
部屋の帯（保育室・ホールなど）
10,400
15,000　計（W通り～東の軒先、どの架構でも同じ）
あまのがわ（W通りの上、架構8から）
2,200
内縁側
1,500
外縁側
1,500
⌒53,663　E通り（R193,000）の上の長さ、架構1～20
⌒57,000　W通り（R205,000、背骨）の上の長さ、架構1～20（19×⌒3,000、スパンもW通りの上）
⌒3,000
事務 4.9 m²
静養室 8.6 m²
医務 21.6 m²
西吹き抜け 11.4 m²
2歳 60.0 m²
受け取り土間 11.2 m²
0・1歳 120.5 m²
4,329　高野川の側の境界まで（避難の帯）
4,200
南の軒の出（架構1から、東の軒先→西の角）
1,800　軒の出
R190,000（東の軒先）
2,824（E通りの上）
0.838°
W
E
1
2
3
4
5
6
7
8
9
10
11
12
13
14
15
16
17
18
19
A
B
C
D
N
0
5 m

部屋の色

🟩	0・1歳～5歳
🟨	こどものみんなの場所（遊戯室・はれのま）
▨	通り・つなぐ場所（はだし）
🟫	土足の床
🟪	大人の場所
🟪	キッチン・調理の更衣
🟦	水まわり

松ヶ崎こども園　5動線とこどもたちの環境

一日の帯：上は1/600の小さな配置（建物＋園庭）と三者の動線（こども緑・保育士茶・調理青）、下にそれぞれの一日

登園 8:00

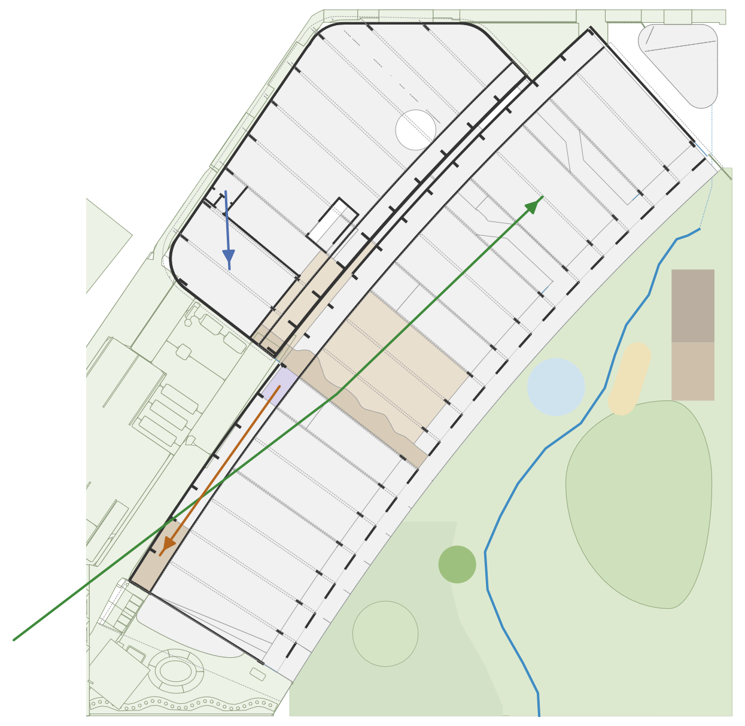

こども公園→木戸→小径→海峡。0・1歳は受け取り土間

保育士おはようの窓口で挨拶、受け取り土間で手渡し

調理　検収と下処理（南のガラス越しに見える）

外で遊ぶ 9:30

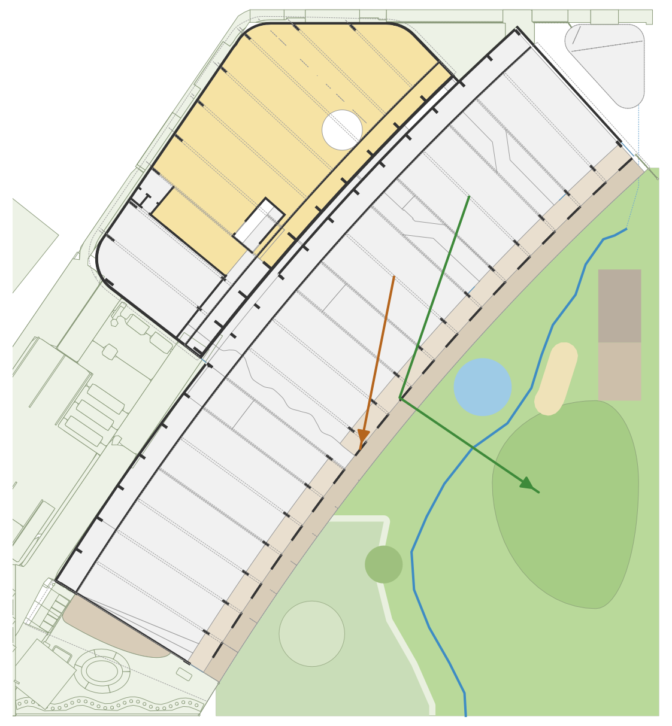

こども3〜5歳はだいさんかく、0〜2歳はしずかのもり

保育士縁側の縁に腰掛けて庭全体を見る

調理　仕込み。今日のごはんの窓にこどもが寄る

食べる 11:30

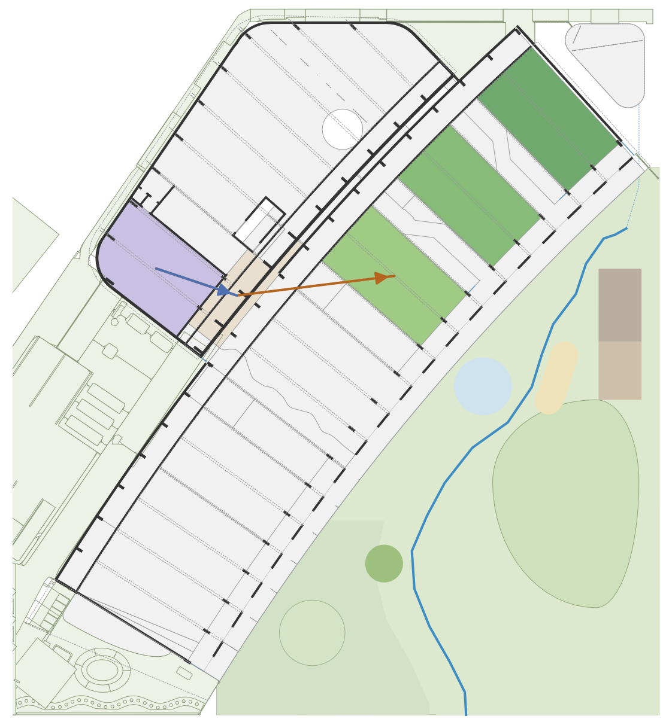

こども保育室の食卓でクラスごとに食べる

保育士配膳口から飛び石を渡って配る。いっしょに座って食べる

調理　オープンキッチンでこどもと目が合う

寝る 12:45

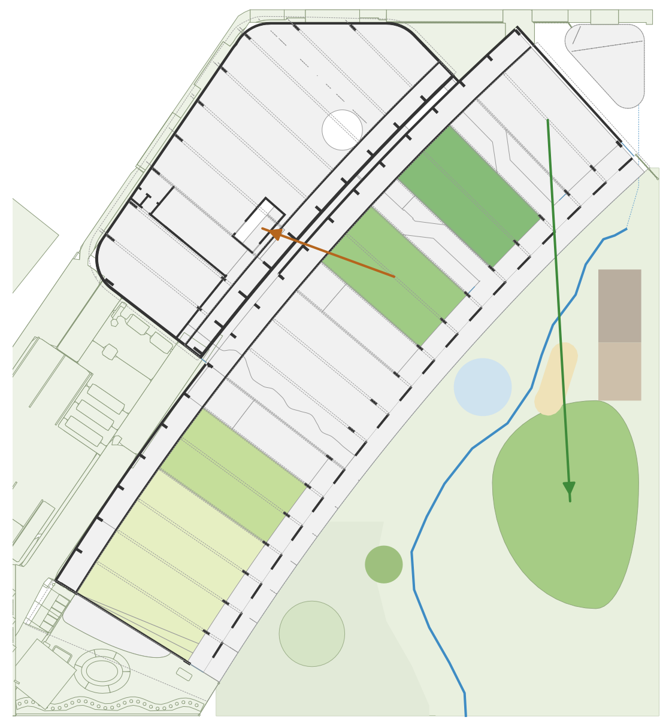

こどもねどこ・ロフトの下。起きている5歳は北の築山と遊戯室

保育士交代で2階の休憩室へ（こどもから離れる）、記録の机

調理　片付けと洗浄、おやつの仕込み

当番 15:00

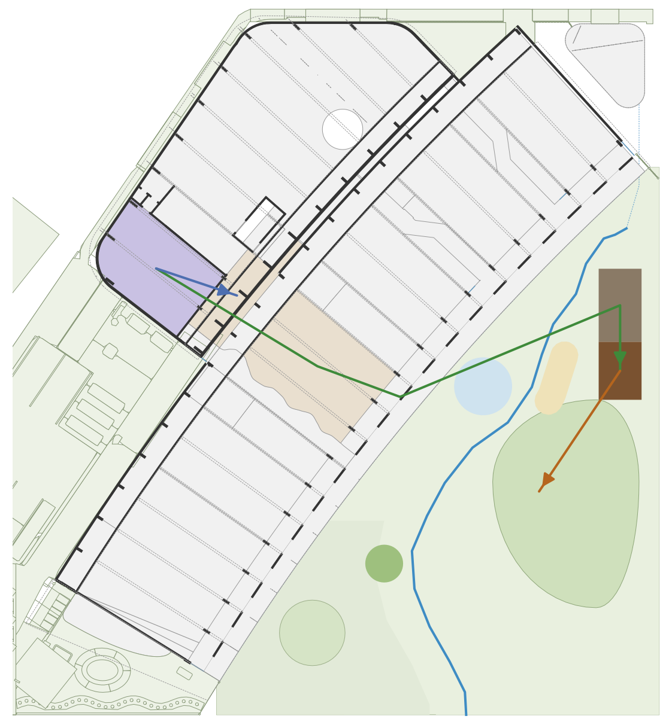

こども4・5歳のコンポスト当番：キッチン→小屋

保育士当番に付き添い、できた土を菜園へ

調理　受け取り台で野菜くずを渡す、保育室でおやつ

降園 16:30

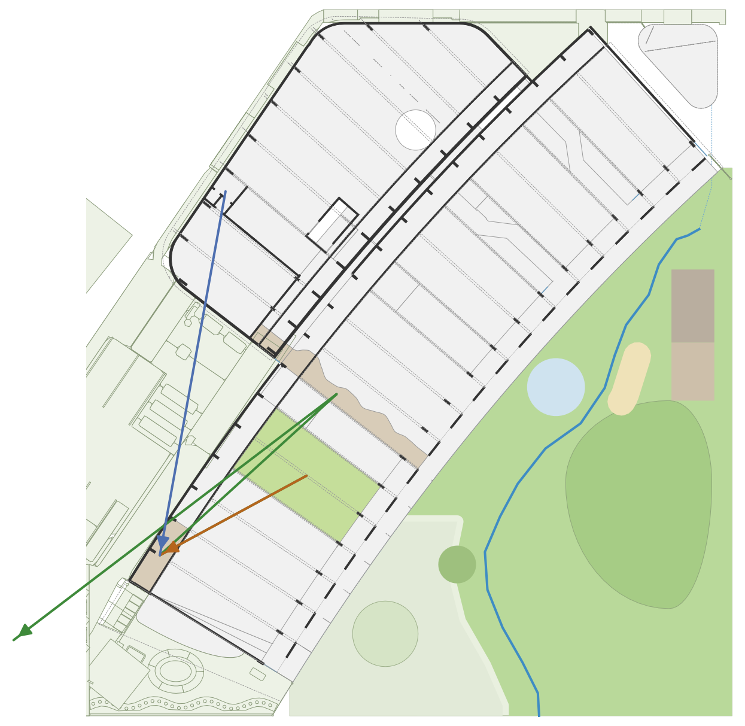

こども2歳の部屋で延長保育、迎えを待つ夕方の園庭

保育士縁台でお茶をしながら保護者と話す、2階で会議

調理　職員の通用口から帰る

こどもたちの環境

園庭　だいさんかく・しずかのもり　約1/320（配置1/200を縮小）

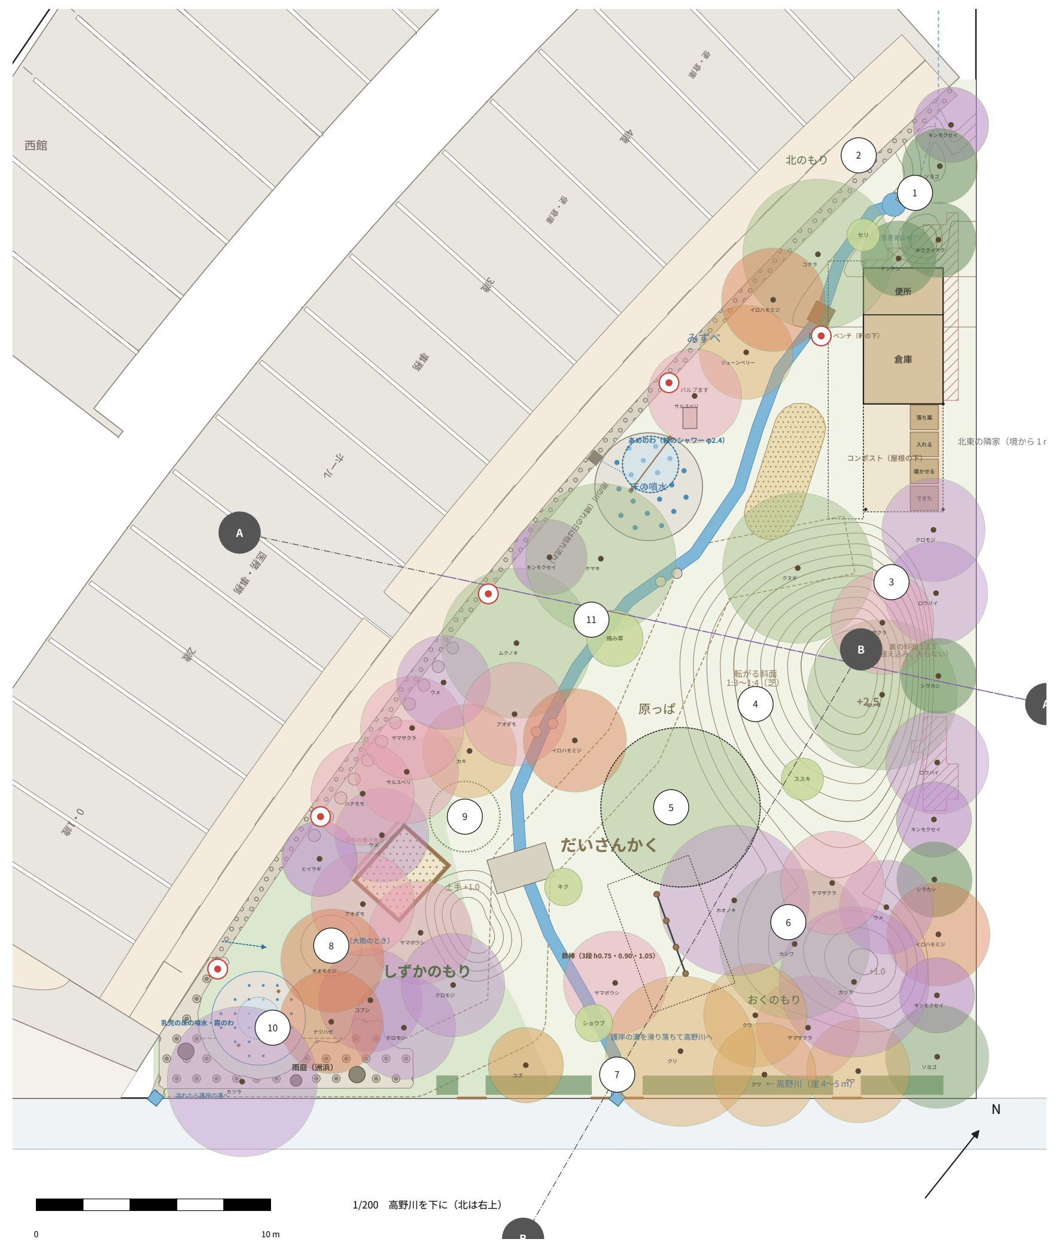

遊戯室

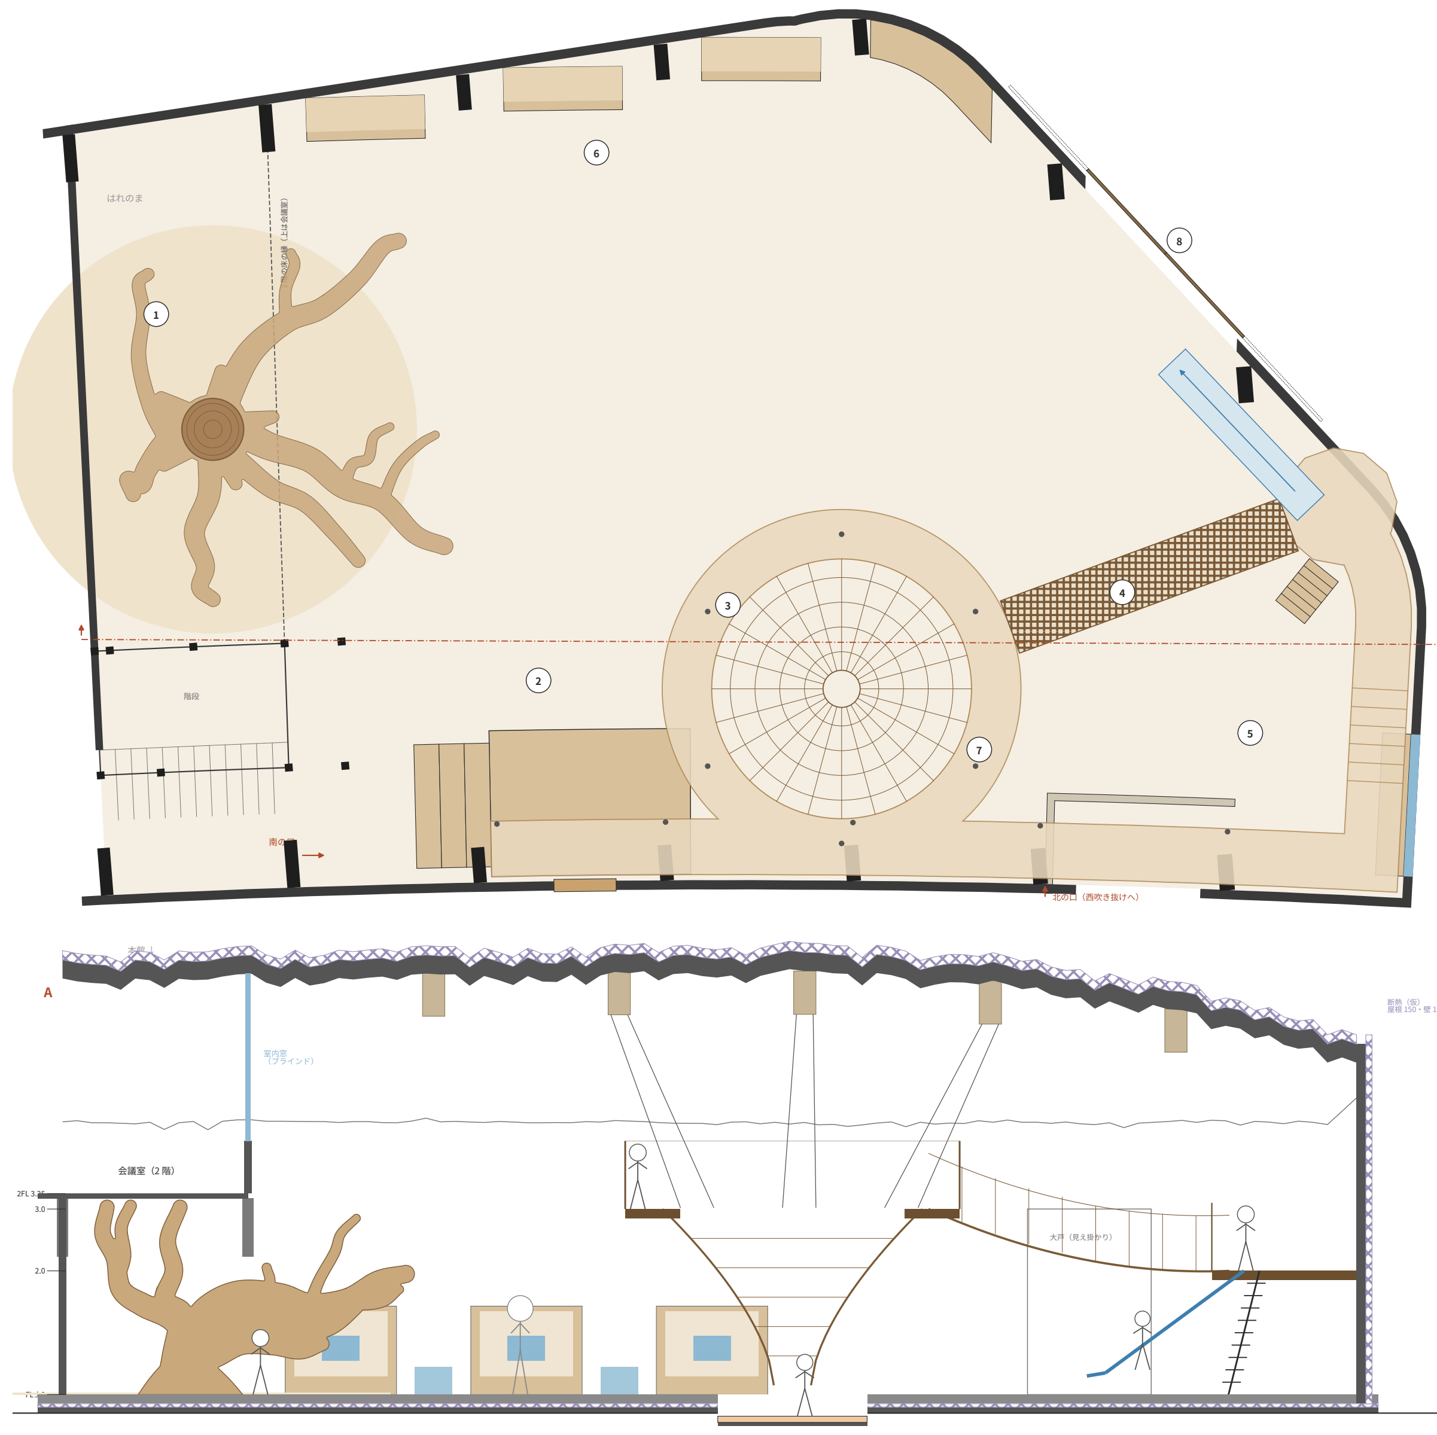

平面・断面 A 1/100

平面は FL+1.2 で切る。淡い茶は
キャットウォーク・輪・踊り場
（h3.0／2.0）、黒い点は吊り材。
断面 A は東から 4.3 で切って西を見る

遊び方

- ① 洞とクスノキ　てっぺんが 2 階の床に届く
- ② デッキと登り壁　→ キャットウォーク h3.0
- ③ 擂鉢ネットと穴の底　ネットからも輪へ登れる
- ④ 輪 → 網の吊り橋 → 踊り場 h2.0　空中で一周する
- ⑤ 北の段 3.0→2.0・はしご・すべり台（落下 2.0 m 以下）
- ⑥ ひだ：くぼみ・丸いベンチ・窓辺の腰掛け（モミジを見る）
- ⑦ 北の口のついたて（吸音）
- ⑧ 搬入の大戸（外付けの引き戸）

安全

手すりは縦格子 h1.1・すき間 90
（頭が通らない、横桟なし）
床の板のすき間 8 未満
網目 上 90・下 50、ロープ φ18

支え方

重さは梁から吊る（梁のあいだを通す、吊り材 M20）。横の揺れは壁とハの字の吊り材で止め、吊り橋だけ揺れる。吊り橋の引きはキャットウォークとの閉じた輪で受ける。梁 90×800×2（強い集成材）は満員でも持つ

断熱（仮）
屋根 150・壁 100・床 50

音

階段の箱がホールとの衝立。
北の口に吸音のついたて、
東の覗き窓は夜だけ開く

→ 北

0　5 m

ホールの北山杉の林

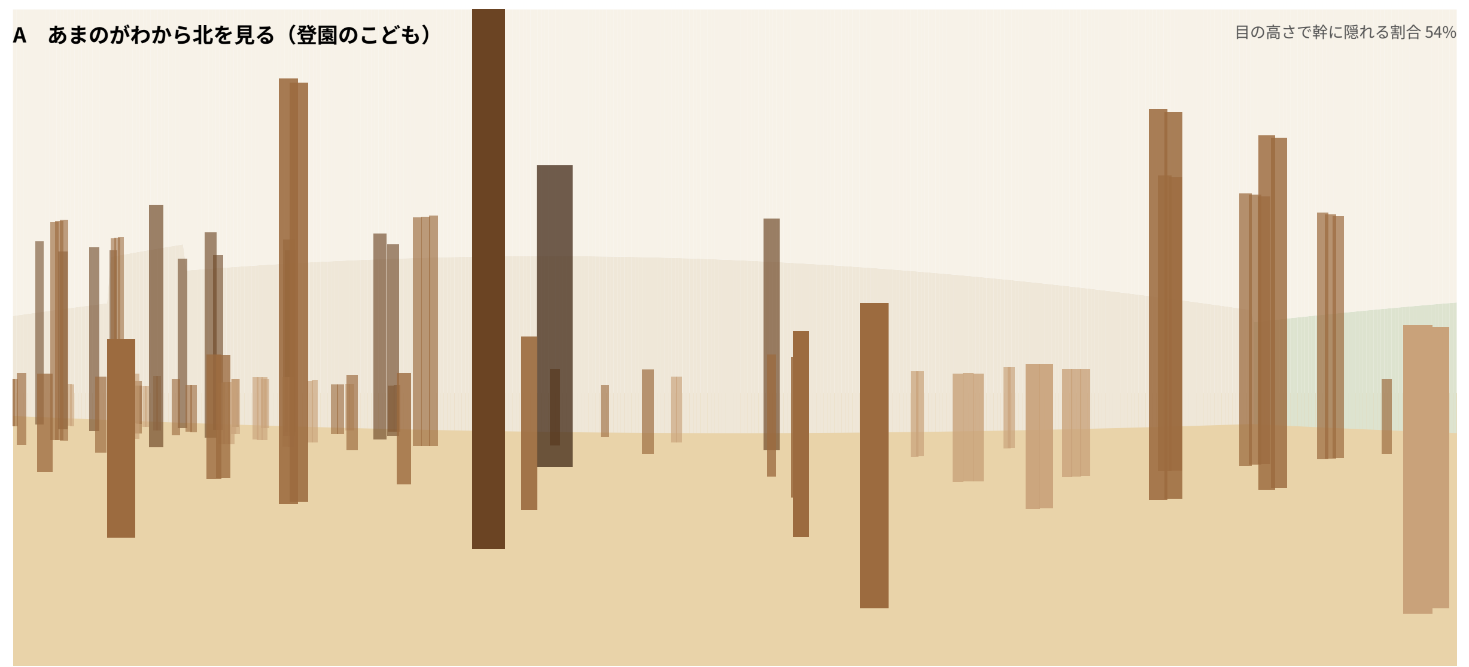

A　あまのがわから北を見る（登園のこども）

目の高さで幹に隠れる割合 54%

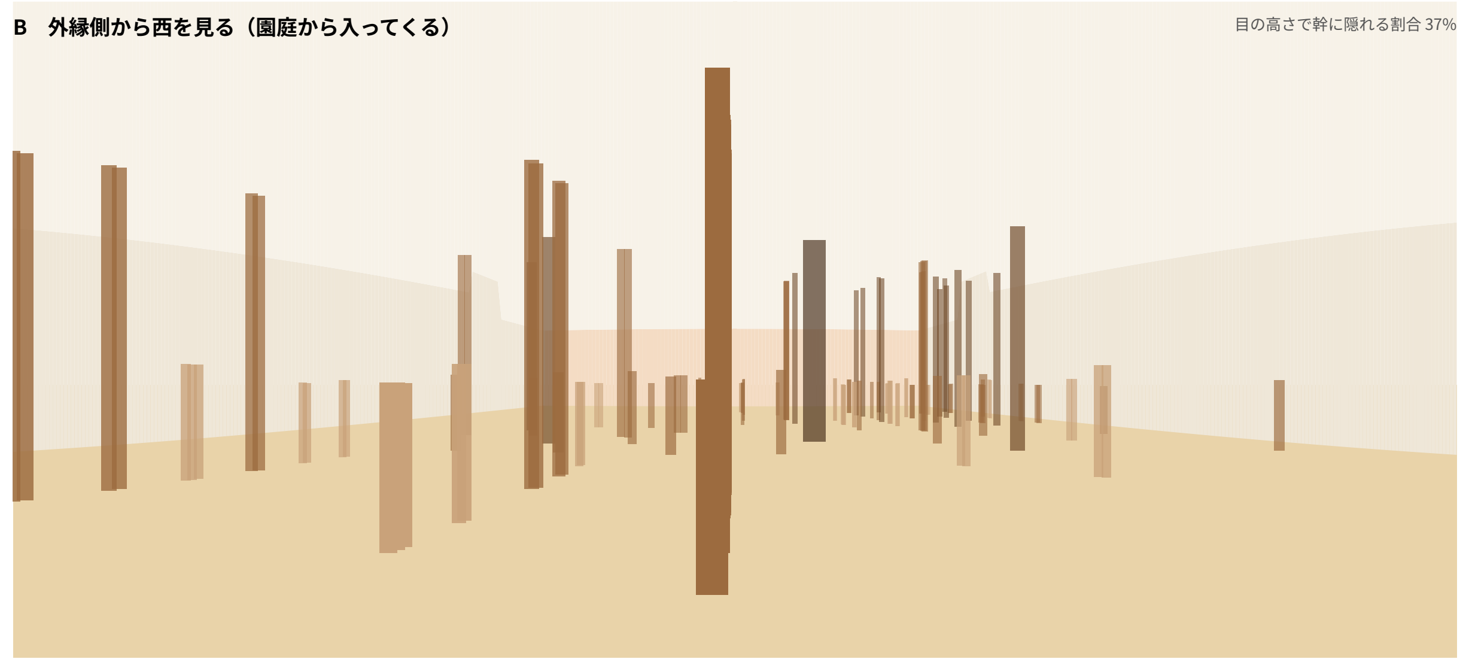

B　外縁側から西を見る（園庭から入ってくる）

目の高さで幹に隠れる割合 37%

教室　3歳の保育室

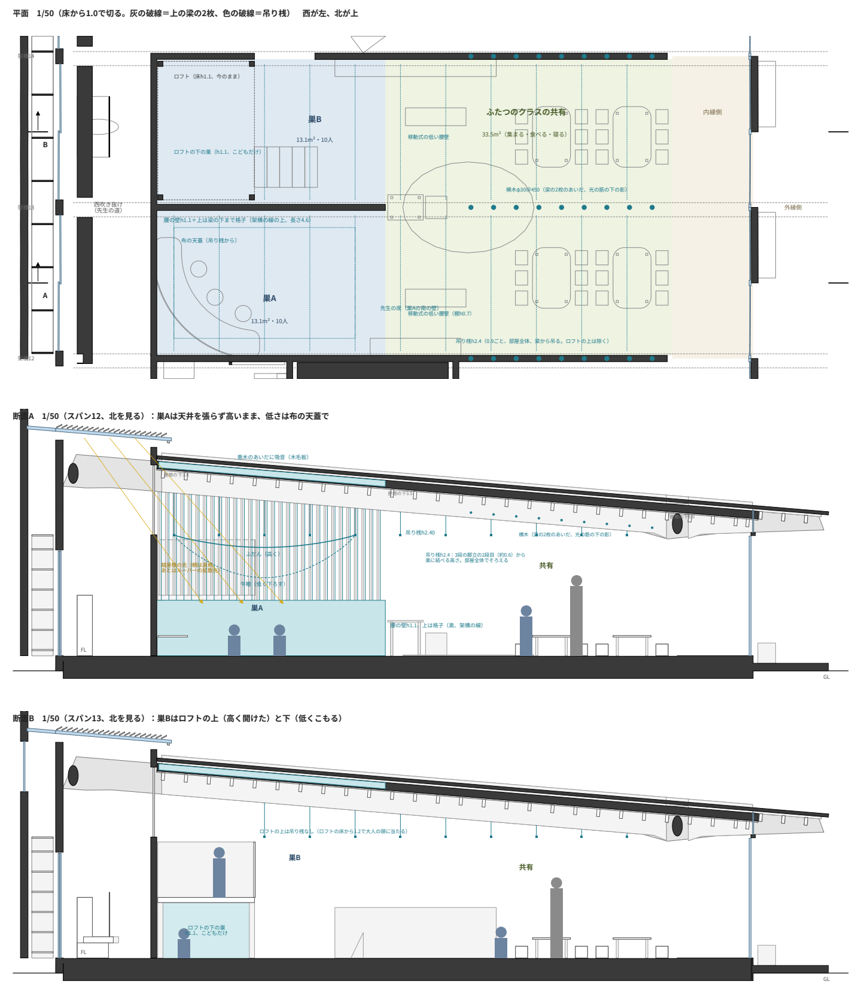

3歳の保育室の分け方

本館係　2026-10-24　スパン12–13（どの学年も同じ形）

ふたつの巣と共有の場所

20人を10人ずつの二つのグループに。西の半分を架構の線（u36）で分けて、それぞれの「巣」に。東の半分は二つで一緒に使う。同じ部屋を左右に並べず、みんなの場所 → 自分たちの場所と奥へ入っていく。隣の便所・倉庫のスパンも隣の学年と共有。

西は静か、でも天井は張らない

- 梁と梁のあいだは東から越屋根へ空気が上る換気の道。西に天井を張るとその出口をふさぐ。
- 西は建物でいちばん高く、越屋根の光が落ちる所。「高くて明るくて静か」＝森の中、お堂の落ち着き。

低さは物で

- 巣A：吊り桟（h2.4）から布の天蓋。ふだんは高く、午睡は低く下ろす。先生が自分で吊り替えられる。
- 巣B：今のロフトの下（h1.1）がこどもだけの巣、ロフトの上は高く開けた場所。一つの西に二つの静けさ。

静けさは音で

- 巣の上の垂木のあいだに吸音（木毛板）。
- 巣の床はやわらかく（コルクか畳）。
- 腰の壁h1.1と格子で東のにぎやかさから少し離す。上は格子なので見通しと光の筋の光は通る。

脚立で届く（先生のエスキス）

- 吊り桟h2.4を部屋全体に：3段の脚立の2段目（約0.6）から楽に結べる高さ（先生の身長約158cmで、立つ面＋約1.8）。リボン・布・飾りを先生が自分で結べる。

先生の席と移動式の腰壁

- 先生の机は巣Aの南の壁に沿って、しずかな角の東（巣Aと共有の境）。壁を背にして、巣Aと共有を横から見守る（巣Bは腰の壁の格子ごし）。
- 移動式の低い腰壁2台（1.2×0.35×h0.7、両面の棚）：共有に島として置き、8の字に回れる。午睡は囲い、行事は端へ。

ロフト（巣B）

- 床の上端h1.2、下は1.1：3歳はぎりぎり立て、大人はかがむ。
- 手すりh+0.9（縦格子90以下）、家具階段は1段0.2×5。

■ 今の3dm（切り口）　灰の線＝今の家具・見えがかり
▭ この案で足したもの（3dmのスクリプトに入れた、更新係の作り直し待ち）
▭ 巣（静か）
▭ 共有
▭ 内縁側

面積は壁芯でなく床の上の概算（m^2）。保育室全体は面積表の3歳（約$60m^2$）。

廊下の本棚と読む場所
（図は本館係に依頼）

表の畑と火のオーブン
入口の前の菜園とひろばのかまど
（図はアプローチ係に依頼）

建築設計実習 II — I　2026.11.05　木田

［割付の注記］フォーカス：上は一日の動線（4枚目の平面図の続き）。分離線の下は、こどもたちが地に足をつけて育つ場所：園庭・遊戯室・北山杉の林・教室・廊下の本棚・表の畑と火のオーブン　／　目に入る順：一日の帯と動線 → 分離線 → 園庭 → 遊戯室・林 → 教室・本棚・畑