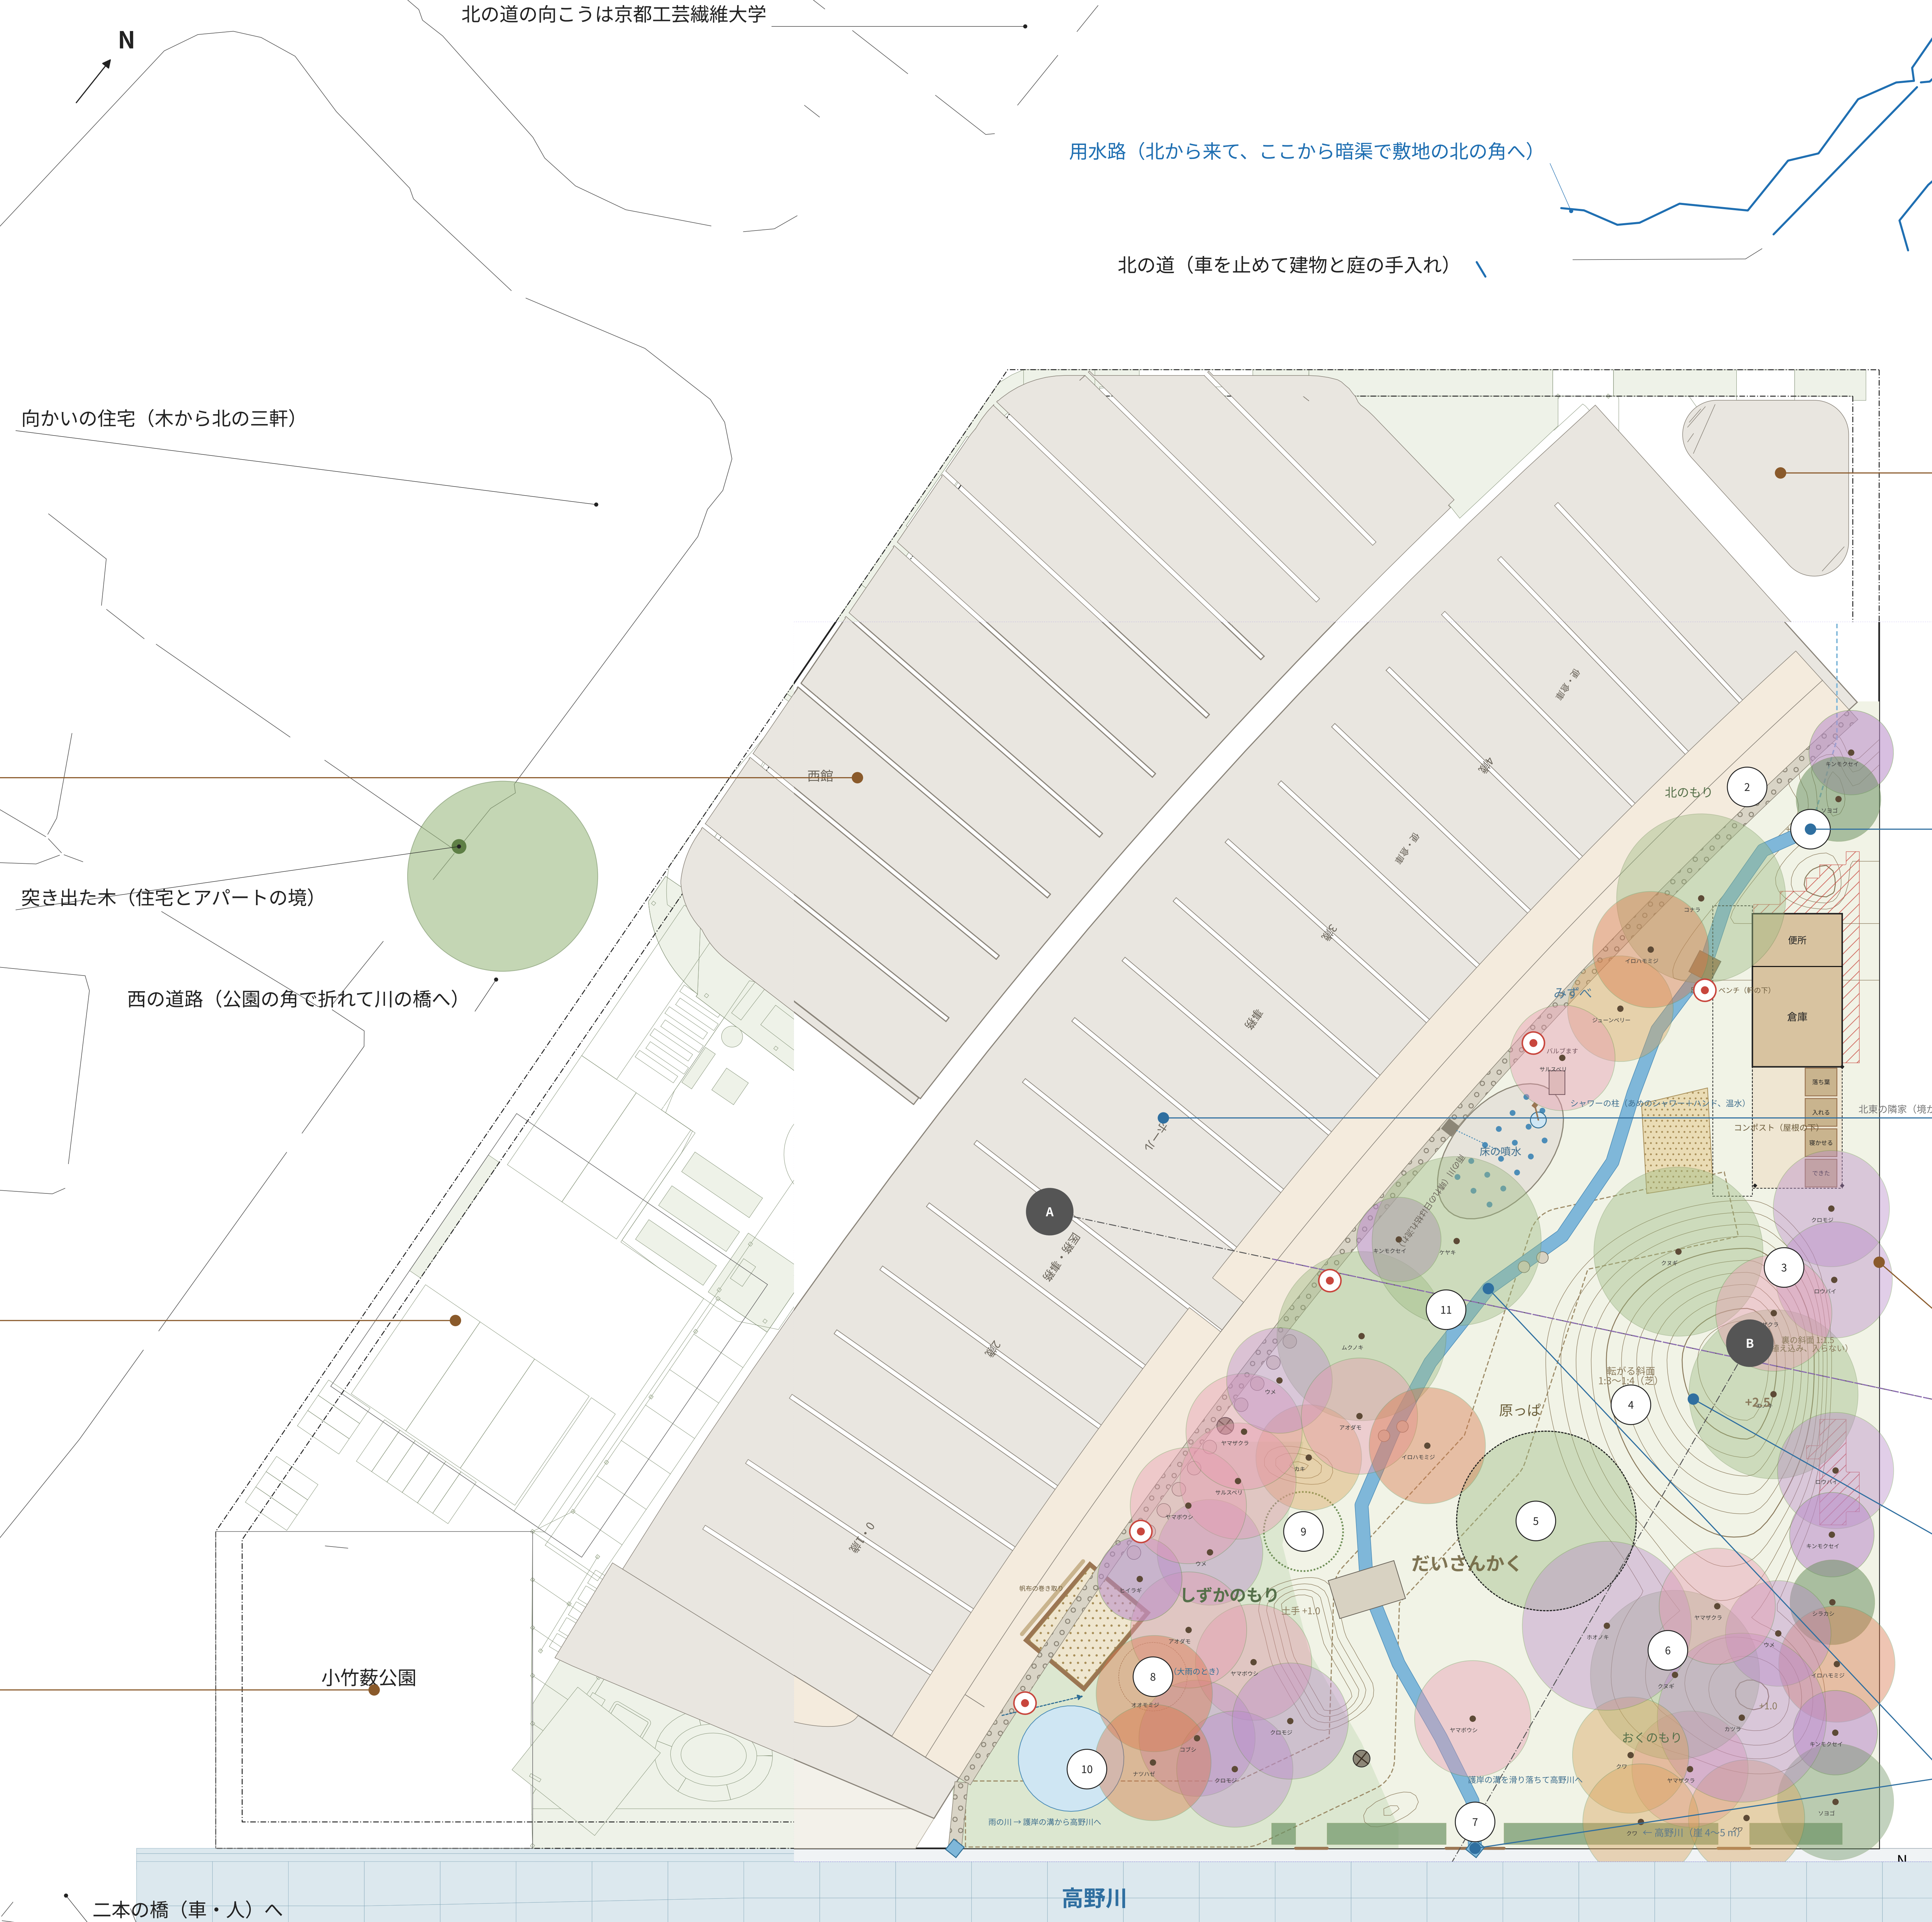
N
北の道の向こうは京都工芸繊維大学
用水路（北から来て、ここから暗渠で敷地の北の角へ）
北の道（車を止めて建物と庭の手入れ）
向かいの住宅（木から北の三軒）
西館
突き出た木（住宅とアパートの境）
西の道路（公園の角で折れて川の橋へ）
小竹薮公園
二本の橋（車・人）へ
高野川
便・倉庫
4歳
便・倉庫
3歳
事務
ホール
医務・事務
2歳
0・1歳
A
B
1
2
3
4
5
6
7
8
9
10
11
北のもり
キンモクセイ
ソヨゴ
コナラ
イロハモミジ
便所
倉庫
ベンチ（軒の下）
みずべ
ジューンベリー
バルブます
サルスベリ
シャワーの柱（あめのシャワー＋ハンド、温水）
北東の隣家（境
コンポスト（屋根の下）
落ち葉
入れる
寝かせる
できた
床の噴水
雨の川（晴れの日は枯れ流れ）
キンモクセイ
ケヤキ
クヌギ
クロモジ
ロウバイ
ヤマザクラ
裏の斜面 1:1.5
（植え込み、入らない）
転がる斜面
1:3〜1:4（芝）
原っぱ
+2.5
エンキ
ムクノキ
ウメ
アオダモ
ヤマザクラ
カキ
イロハモミジ
サルスベリ
ヤマボウシ
ウメ
ヒイラギ
帆布の巻き取り
しずかのもり
土手 +1.0
だいさんかく
アオダモ
（大雨のとき）
ヤマボウシ
オオモミジ
クロモジ
コブシ
ナツハゼ
クロモジ
雨の川 → 護岸の溝から高野川へ
ヤマボウシ
護岸の溝を滑り落ちて高野川へ
ホオノキ
ヤマザクラ
ウメ
シラカシ
イロハモミジ
クヌギ
+1.0
カツラ
キンモクセイ
おくのもり
クワ
ヤマザクラ
ソヨゴ
クワ
← 高野川（崖 4〜5 m）
クワ