こどもたちの育ち舎　1/5　敷地と園庭

建築設計実習 II — I　2026.11.05　木田

地に足をつけて育つ

ゆるやかな弧を東の比叡へひらく木造平屋の本館に0歳から5歳のすべての部屋を並べ、縁側と深い庇で園庭とつなぐ。園庭には用水を借りた小川と、比叡に見立てた築山を置く。玄関ホールに面したオープンキッチンを園の中心に据えて食べることを日々の求心力とする。野菜くずはこどもの手で土に還し、野菜を育て、土のなかのミミズに驚くことで、命の循環を知る。園庭には季節ごとに香る木と実のなる木を植え、こどもは手と鼻と舌で季節を知る。3 mスパンの木造架構によるスケルトン＆インフィルで用途の変化を受け止め、越屋根の温度差換気と夏の夜の冷気で、LEED v5 Gold相当を目指す。

設計趣旨 約277字（課題は300字程度）。文字3.6 mmなら1 m離れて読める

立地と応答

比叡（東から24°）
小さな図＋
冷気→本館は東向き
越屋根で夏の夜に冷やす

高野川と崖4〜5 m
小さな図＋
川へ下がる屋根・植栽帯
浸水1.5 m→大学へ避難

扇状地と用水
小さな図＋
用水を借りた小川と築山
＝園内の高野川と比叡

西の細い道と住宅
小さな図＋
西館の屋根を西で低く
車は突き出た木より南で

模型写真　A4（入口の一枚）
園庭からこどもの目線（模型で約10 mm）
縁側・深い庇・築山の向こうに比叡の方向
選抜で最初に目に入る位置

配置図　1/200　高野川を下に（川向こうから見る向き、北は右上）

点線の枠＝園庭のチャットの配置1/200（garden01）を実寸で重ねた。本番は一枚に描き直す

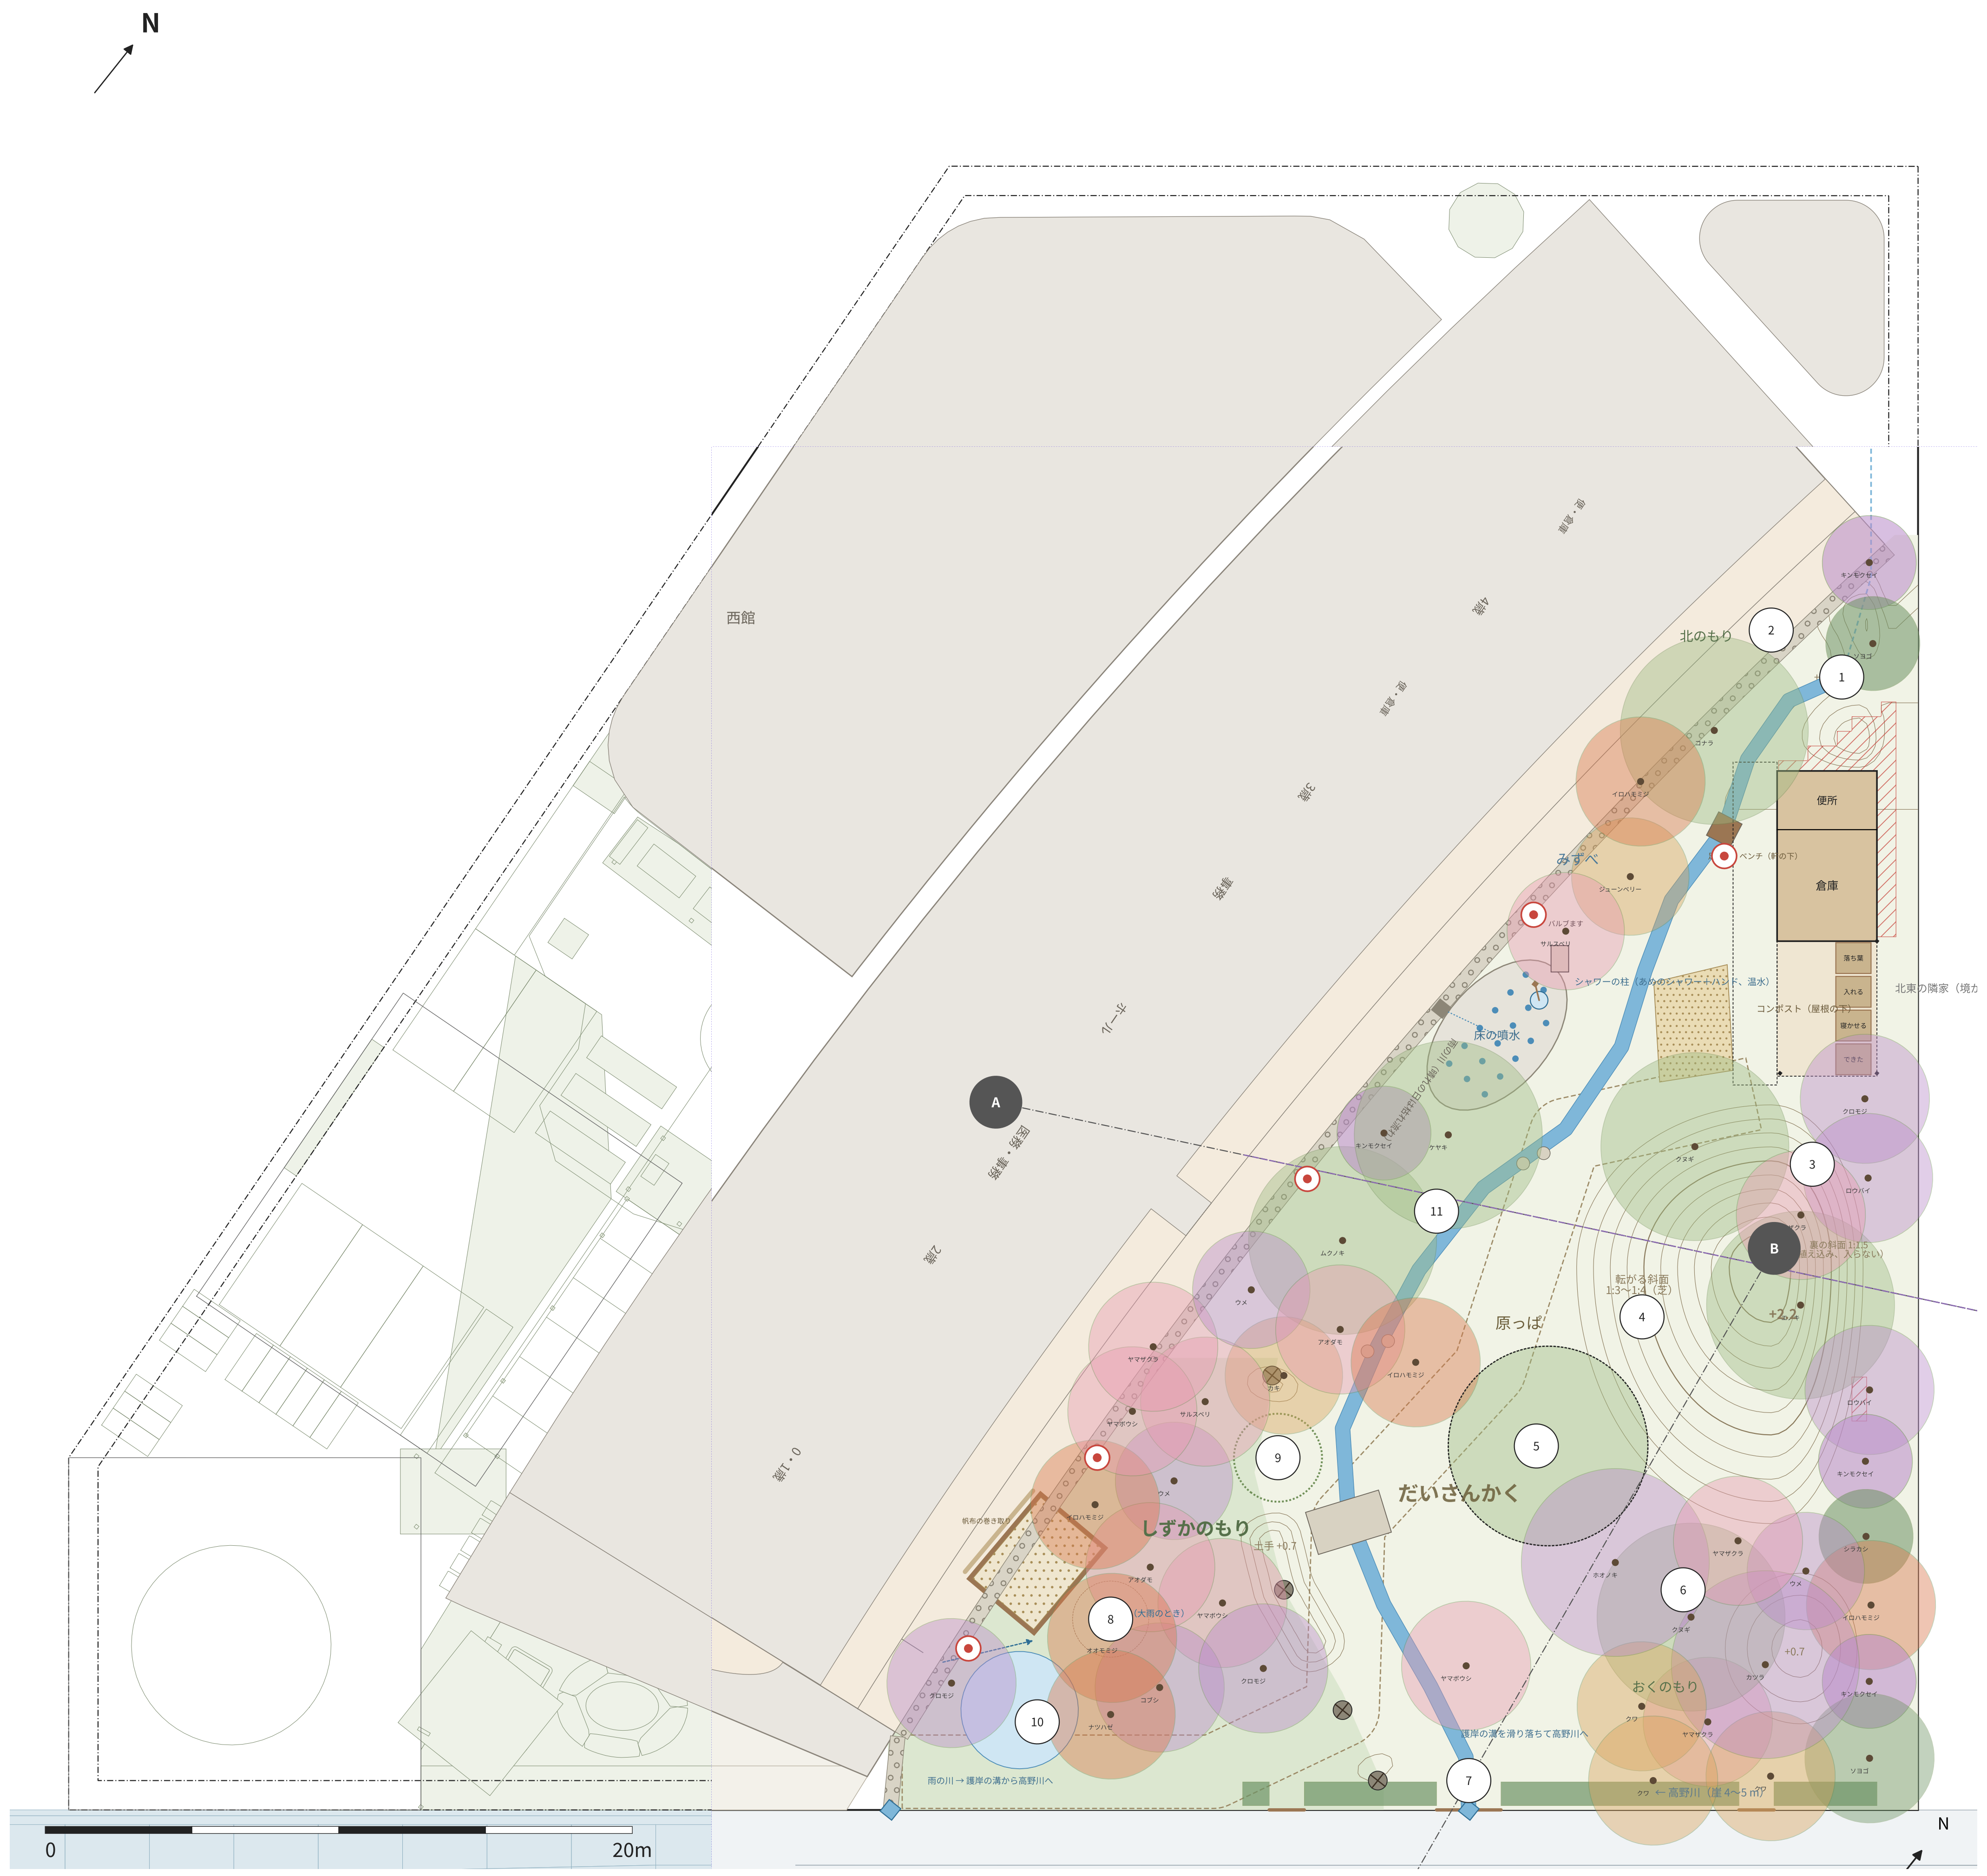
N
西館
ホール
3歳
4歳
便・倉庫
事務
医務・事務
2歳
0・1歳
北のもり
みずべ
床の噴水
シャワーの柱（あめのシャワー＋ハンド、温水）
ベンチ（軒の下）
バルブます
便所
倉庫
落ち葉
入れる
寝かせる
できた
コンポスト（屋根の下）
北東の隣家（境
原っぱ
転がる斜面 1:3〜1:4（芝）
裏の斜面 1:1.5（植え込み、入らない）
+2.2
だいさんかく
しずかのもり
土手 +0.7
帆布の巻き取り
（大雨のとき）
おくのもり
+0.7
護岸の溝を滑り落ちて高野川へ
雨の川 → 護岸の溝から高野川へ
← 高野川（崖 4〜5 m）
キンモクセイ
ソヨゴ
コナラ
イロハモミジ
ジューンベリー
サルスベリ
ケヤキ
ムクノキ
クヌギ
クロモジ
ロウバイ
ヤマザクラ
ウメ
アオダモ
ヤマボウシ
カキ
オオモミジ
コブシ
ナツハゼ
ホオノキ
シラカシ
カツラ
クワ
A
B
1
2
3
4
5
6
7
8
9
10
11
0
20m

園庭　本物に触れて遊ぶ

見立て　築山＝比叡、小川＝高野川
小さな図＋
ホールから頂の向こうに比叡
足もとを掘った土で盛る
遊具を置かず、地形と木で遊ぶ

水の行方を隠さない
小さな図＋
用水→みなもと→小川→護岸の溝→高野川
雨は樋なしで屋根から落ち、雨の川へ
溢れたらすりばちが雨の池に

土と世代のめぐり
小さな図＋
キッチンの野菜くず→コンポスト（4・5歳の当番）
→入口前の菜園→給食、余りは農家へ
柳の家は上の子が小さい子のために編む

静かな場所と先生の目
小さな図＋
南のしずかのもり（寝ている0〜2歳の前）
ニッチ11か所、死角は植え込みだけ
取り除くのは命に関わる危険だけ

模型写真　鳥瞰
敷地と高野川・崖・公園・西の道・園庭
配置図と同じ向き（高野川を手前）にそろえる

［割付の注記］フォーカス：この案が敷地から生まれたこと（比叡・高野川・扇状地・西の細い道）と、主題の舞台としての園庭　／　目に入る順：模型写真（入口の一枚）→ タイトルと趣旨の冒頭 → 配置図と園庭 → 園庭の筋 → 立地と応答

こどもたちの育ち舎　2/5　こどもの一日　1階平面

建築設計実習 II — I　2026.11.05　木田

1階平面図 1/100　道路・隣地境界線・家具。北が右、園庭が下（縁側の前の園庭まで）

建物（庇・おむすび・みなみのさんかくまで）75.5×31.8 m → 1/100で755×318 mm。窓799×392 mmに入る。西の道路の幅は3dmに無いので描き足す

こどもの一日　園庭と部屋を行き来して　食べる・遊ぶ・寝る・当番

一日の帯は1/700の小さな配置（建物＋園庭、3dmとgarden.jsonから自動）。北が右・園庭が下

登園8:00

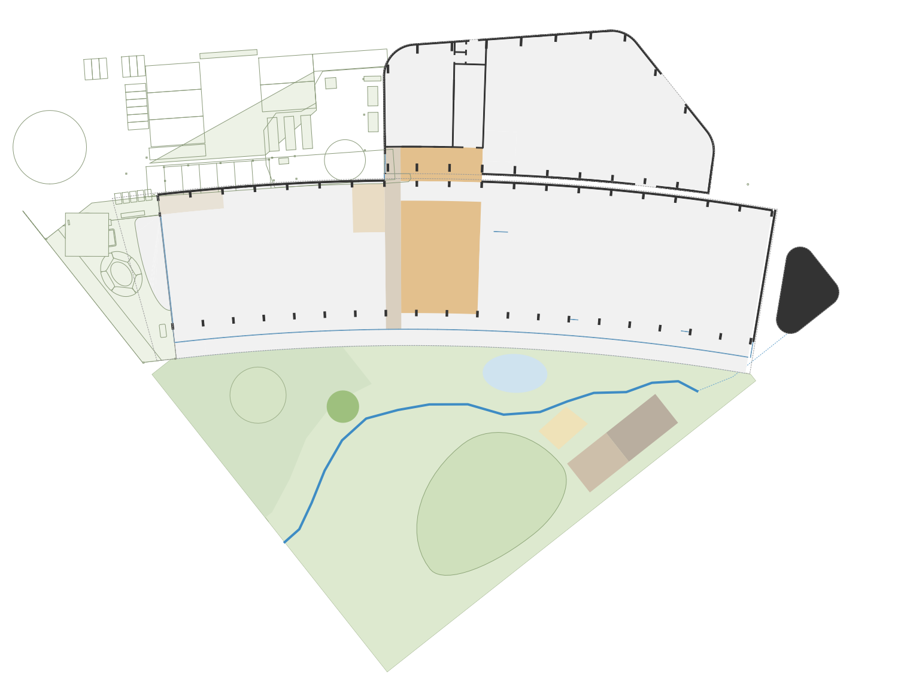

公園→木戸→小径→海峡／0・1歳は受け取り土間

外で遊ぶ9:30

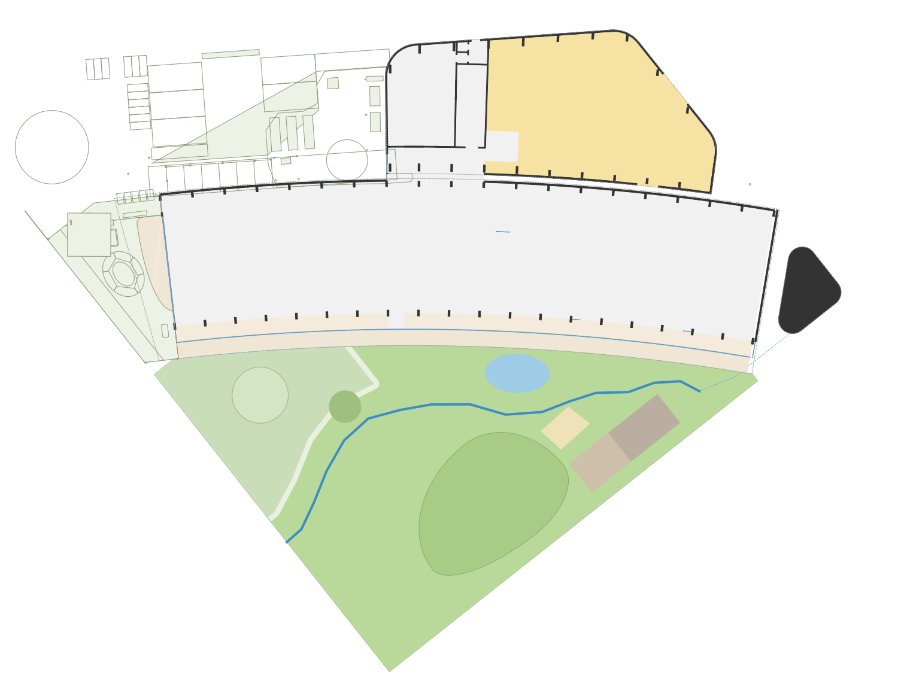

3〜5歳はだいさんかく（築山・小川・もり、夏は床の噴水）
0〜2歳はしずかのもり／雨の日は遊戯室

食べる11:30

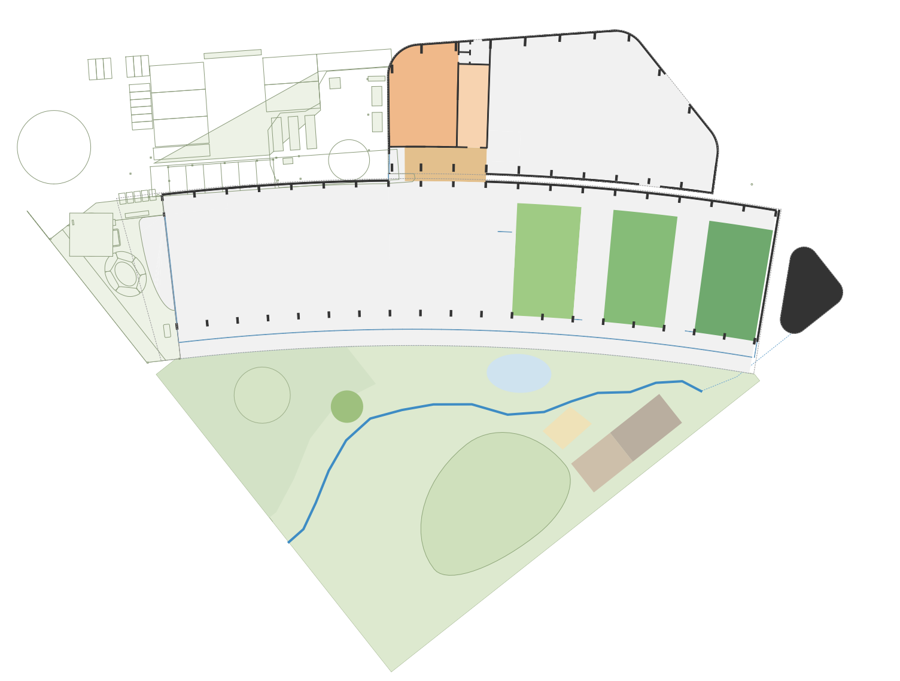

キッチンから海峡を通って配膳
縁側から見える台所

寝る12:45

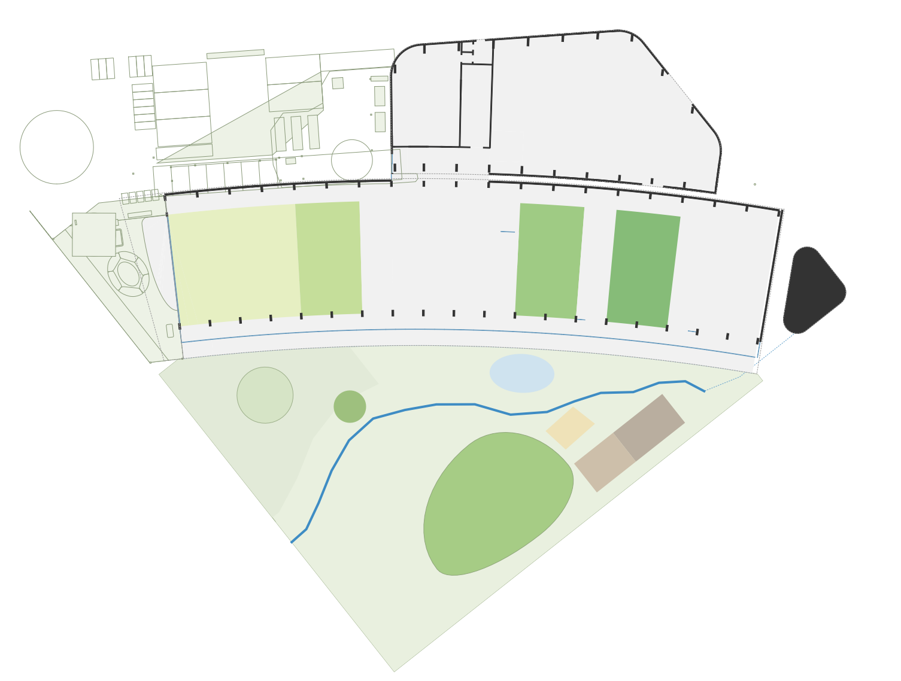

ねどこ・ロフトの下／南のしずかのもりは静かに
起きている5歳は北の築山・遊戯室で

当番15:00

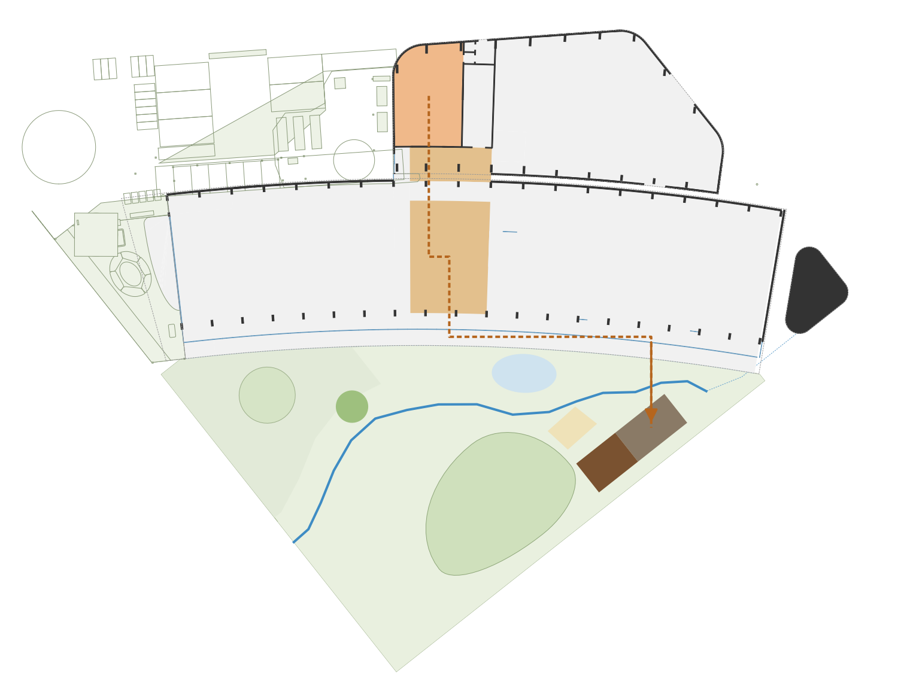

4・5歳のコンポスト当番：キッチンの野菜くず→小屋
できた土は入口前の菜園へ（余りは農家へ）

降園16:30

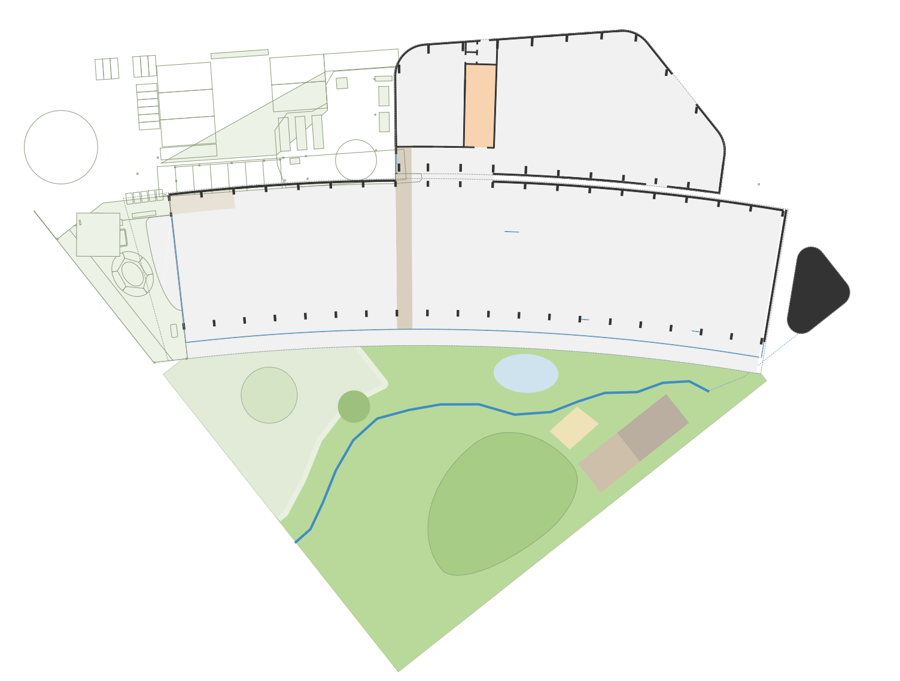

はれのまで延長保育／縁台でお茶
迎えを待つあいだ夕方の園庭

［割付の注記］フォーカス：こどもが一日を過ごす場所としての平面（家具・午睡・靴の線・歳とともに延びる道）　／　目に入る順：部屋の色 → 海峡とホール・キッチン → 縁側 → 家具 → 一日の帯（部屋と園庭）

こどもたちの育ち舎　3/5　どう見えるか　立面と縦断

建築設計実習 II — I　2026.11.05　木田

東立面図（園庭側）　1/100　1階平面と同じ横位置

2枚目の真下に貼ると、平面と柱の位置が縦にそろう

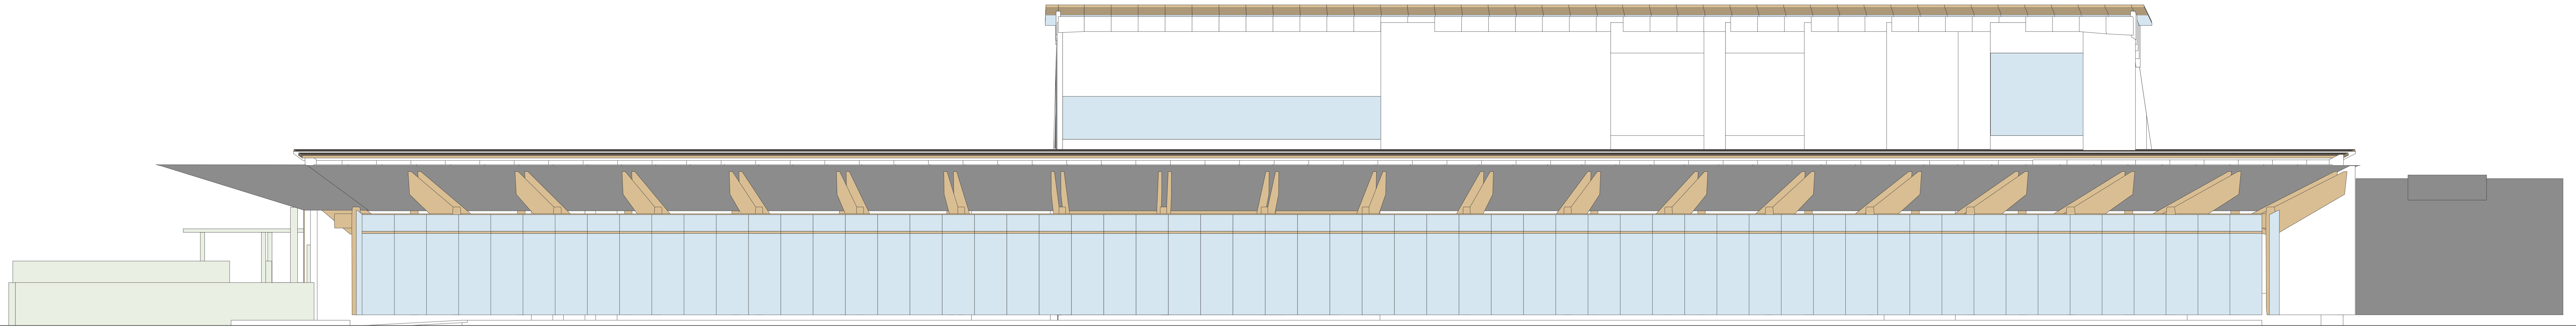

縦断面図A　1/100　保育室の中ほどr=197 mで切って展開、西を見る

自動の断面Aをそのまま実寸で（model/drawings）

断面 A　縦断（展開）　保育室の中ほど r=197 m の弧で切って平らに伸ばす、西を見る

本館 屋根の最高　+3,500
2FL　+3,250
FL　±0
GL　−300
1
2
3
4
5
6
7
8
9
10
11
12
13
14
15
16
17
18
19
20
北→
高野川の護岸（現況、寸法は仮）
←南（高野川）

模型写真　西の道から
人の目の高さ1.5 m（模型15 mm）
低い軒と縦格子

模型写真　公園の木戸から
アプローチの入口
見送りの小径の奥にひろば

西立面図（道路側）　1/100　北が左

道の向かいの住宅の高さを点線で描き足す（圧迫感の説明）

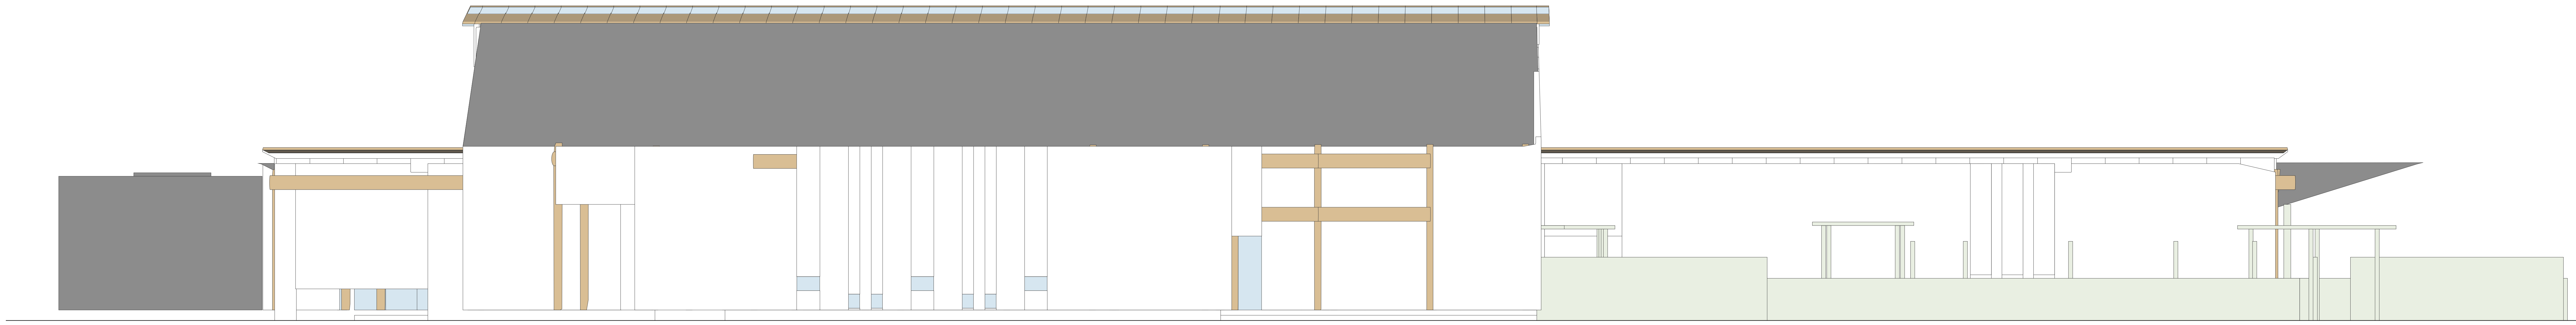

［割付の注記］フォーカス：57 mの縁側と深い庇のリズム（東）、街に対して低い構え（西）　／　目に入る順：東立面（平面の真下、柱がそろう）→ 縦断 → 西立面

こどもたちの育ち舎　4/5　どう息をするか　断面と環境

建築設計実習 II — I　2026.11.05　木田

断面図C　4歳・遊戯室　1/50（1/100の自動の図を2倍）　西の道路から園庭へ

左右に 道・向かいの住宅／園庭・築山 を描き足す。空気の矢印と①〜⑨を重ねる。断熱は帯で

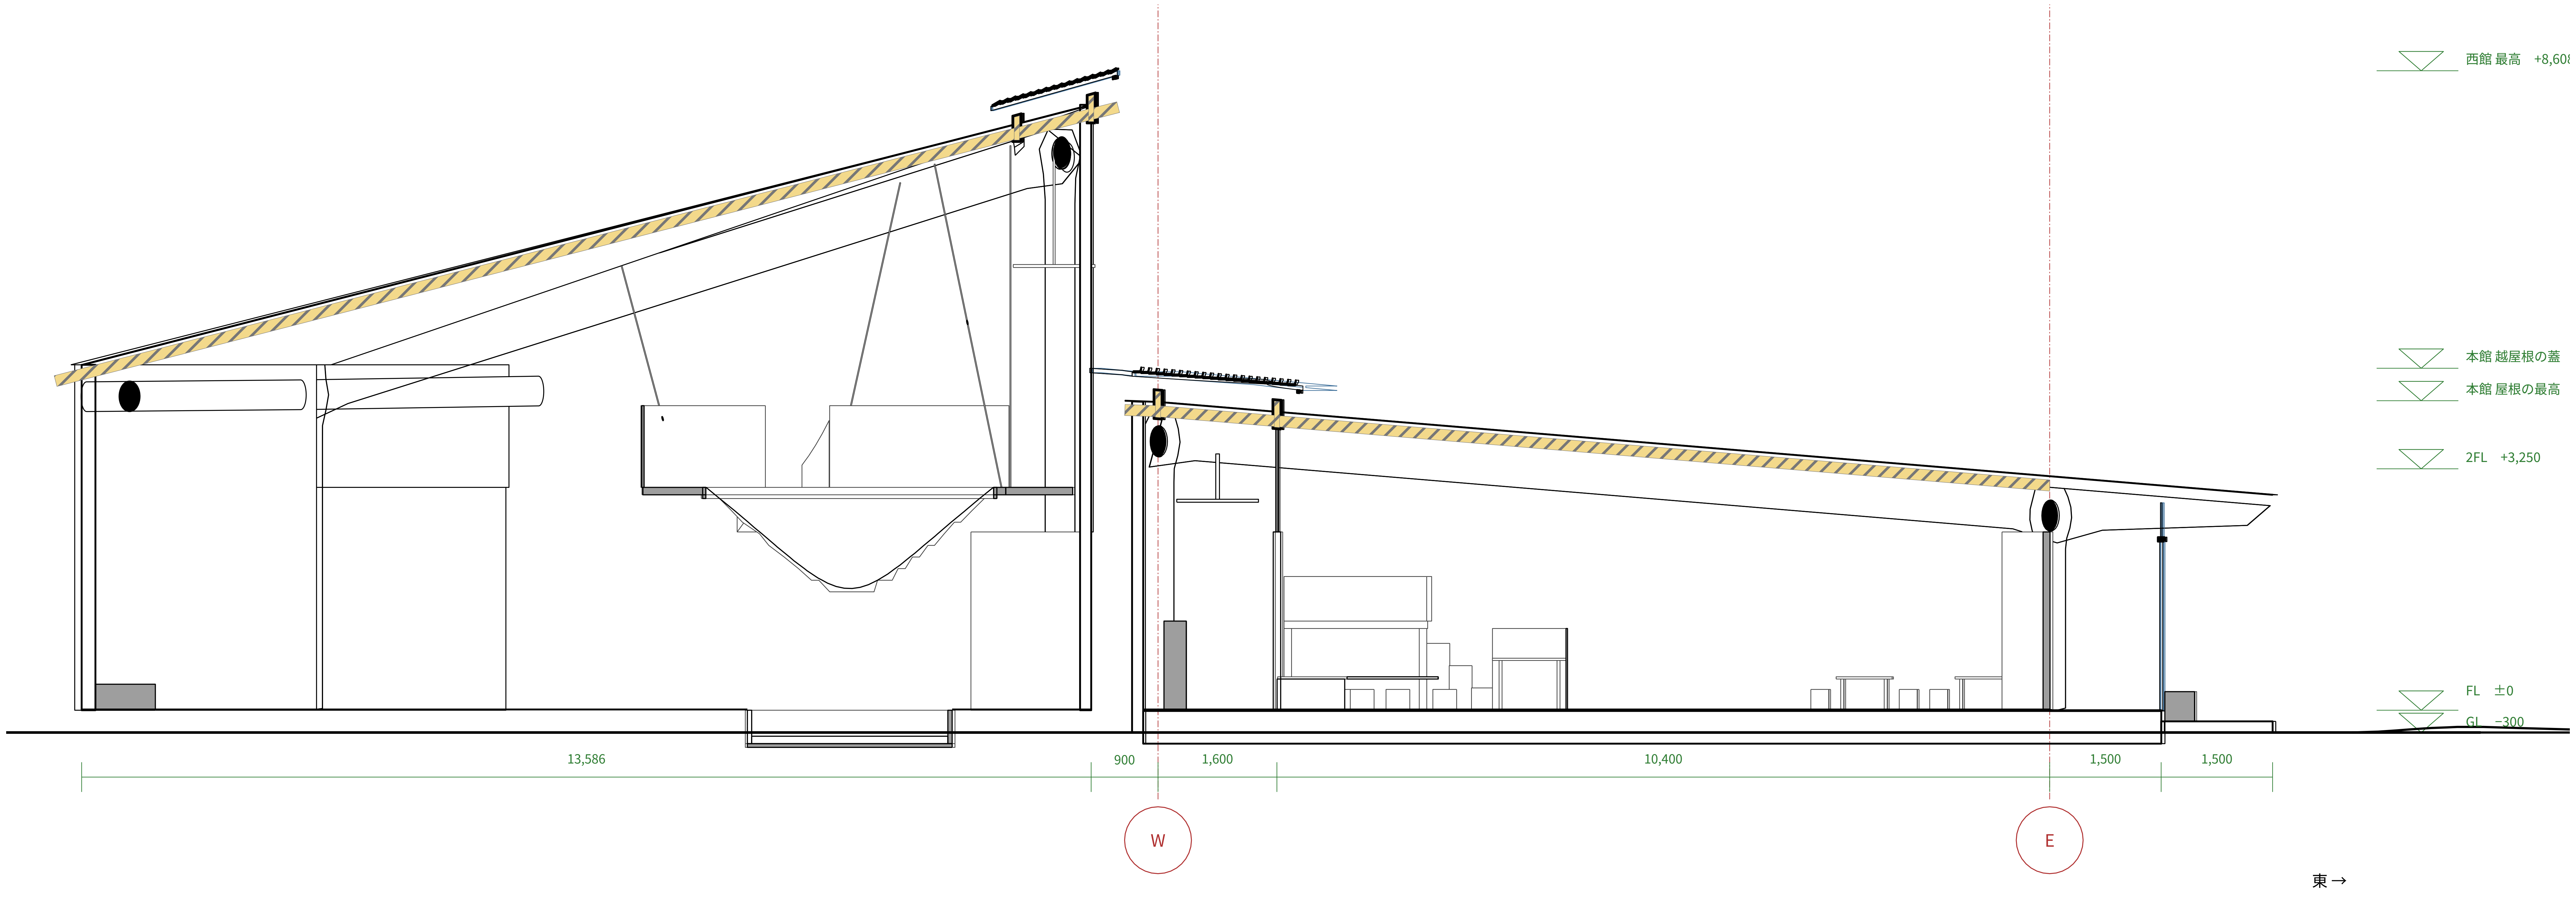
西館 最高　+8,608
本館 越屋根の蓋
本館 屋根の最高
2FL　+3,250
FL　±0
GL　−300
13,586
900
1,600
10,400
1,500
1,500
W
E
東→

環境の枠
LEED v5
Gold相当

脱炭素 ①〜⑤
生活の質 ⑥⑦
生態系 ⑧⑨

夏の昼
庇で遮る・越屋根から抜く

夏の夜
比叡の冷気で冷やす（自動の窓）

春・秋
手で開ける（表示灯）

冬
床暖房・熱交換の換気・断熱

断面図B　海峡　1/100　南の入口・キッチン・2階・すき間・本館・縁側

断面 B　海峡（スパン 8+0.75）　南の入口・キッチン・2 階・すき間・本館・縁側、北を見る

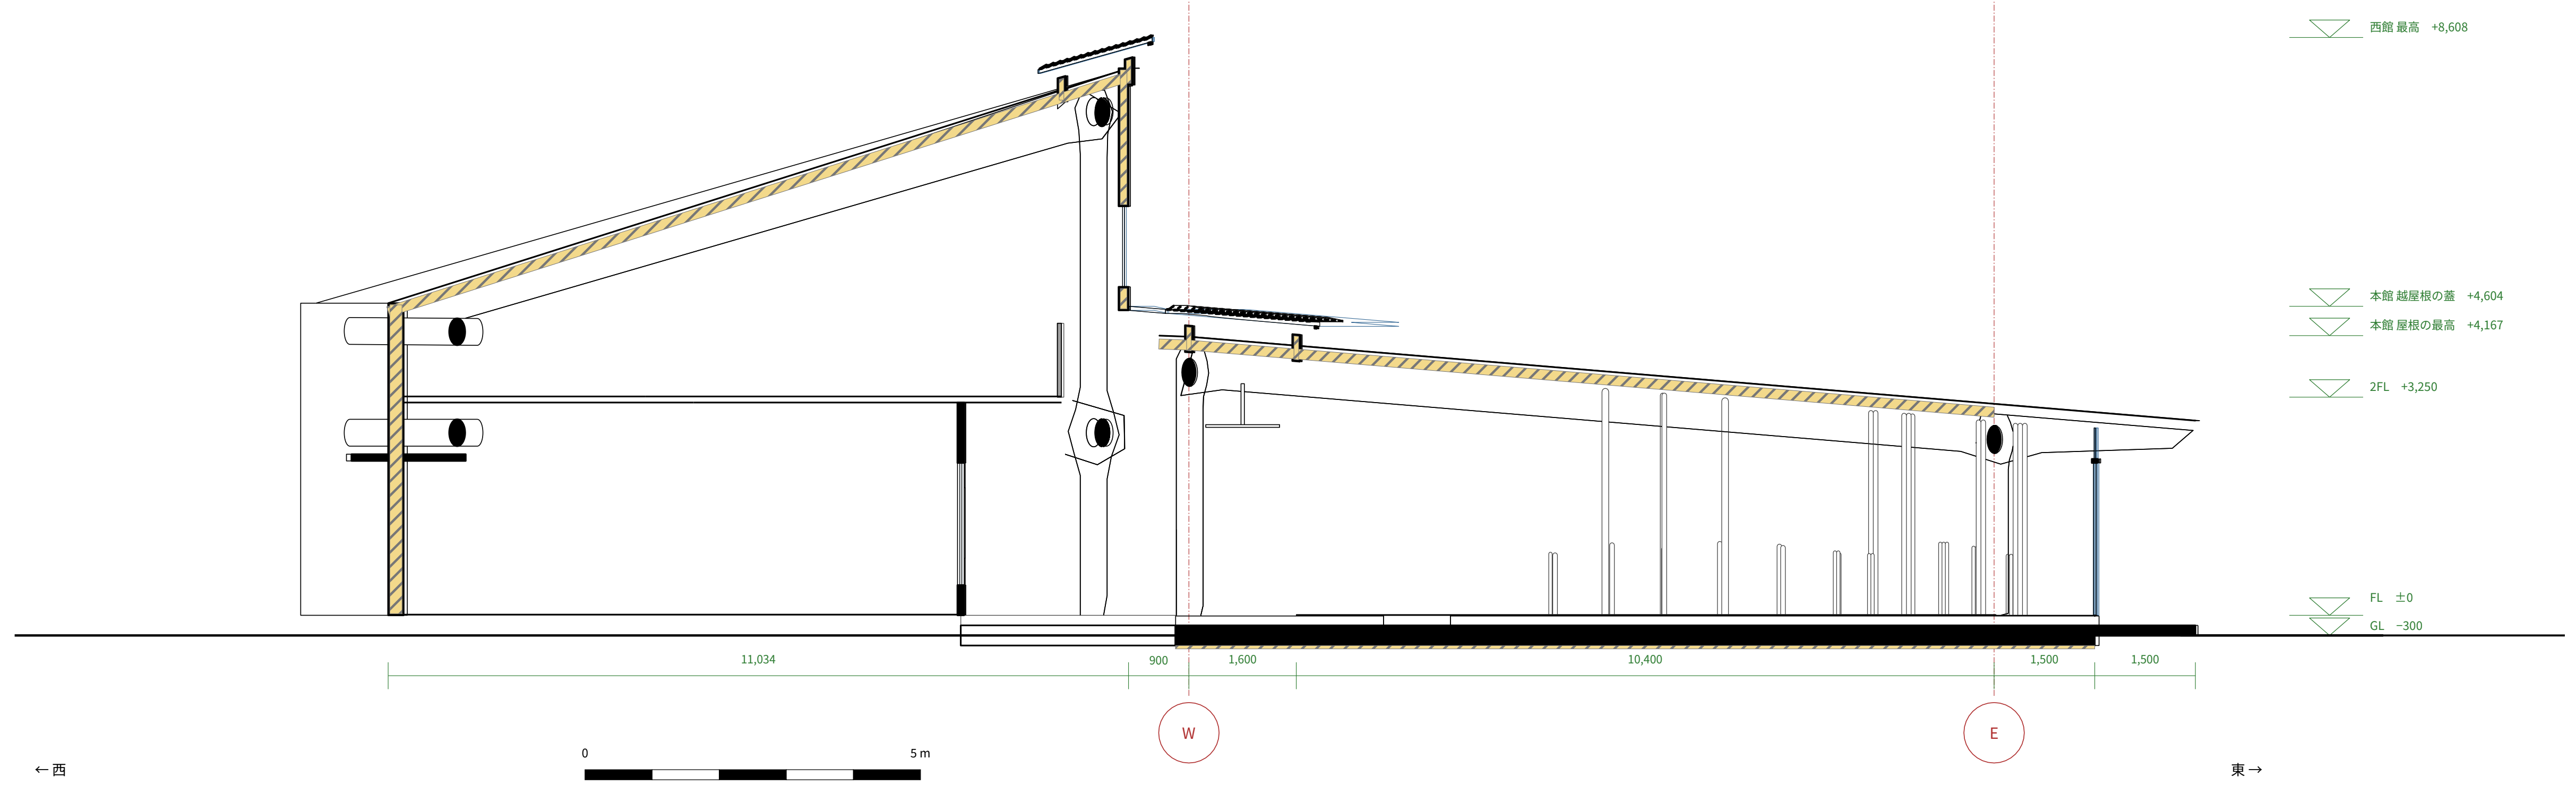
西館 最高　+8,608
本館 越屋根の蓋　+4,604
本館 屋根の最高　+4,167
2FL　+3,250
FL　±0
GL　−300
11,034
900
1,600
10,400
1,500
1,500
W
E
←西
0
5 m
東→

2階平面図（西館）　1/100

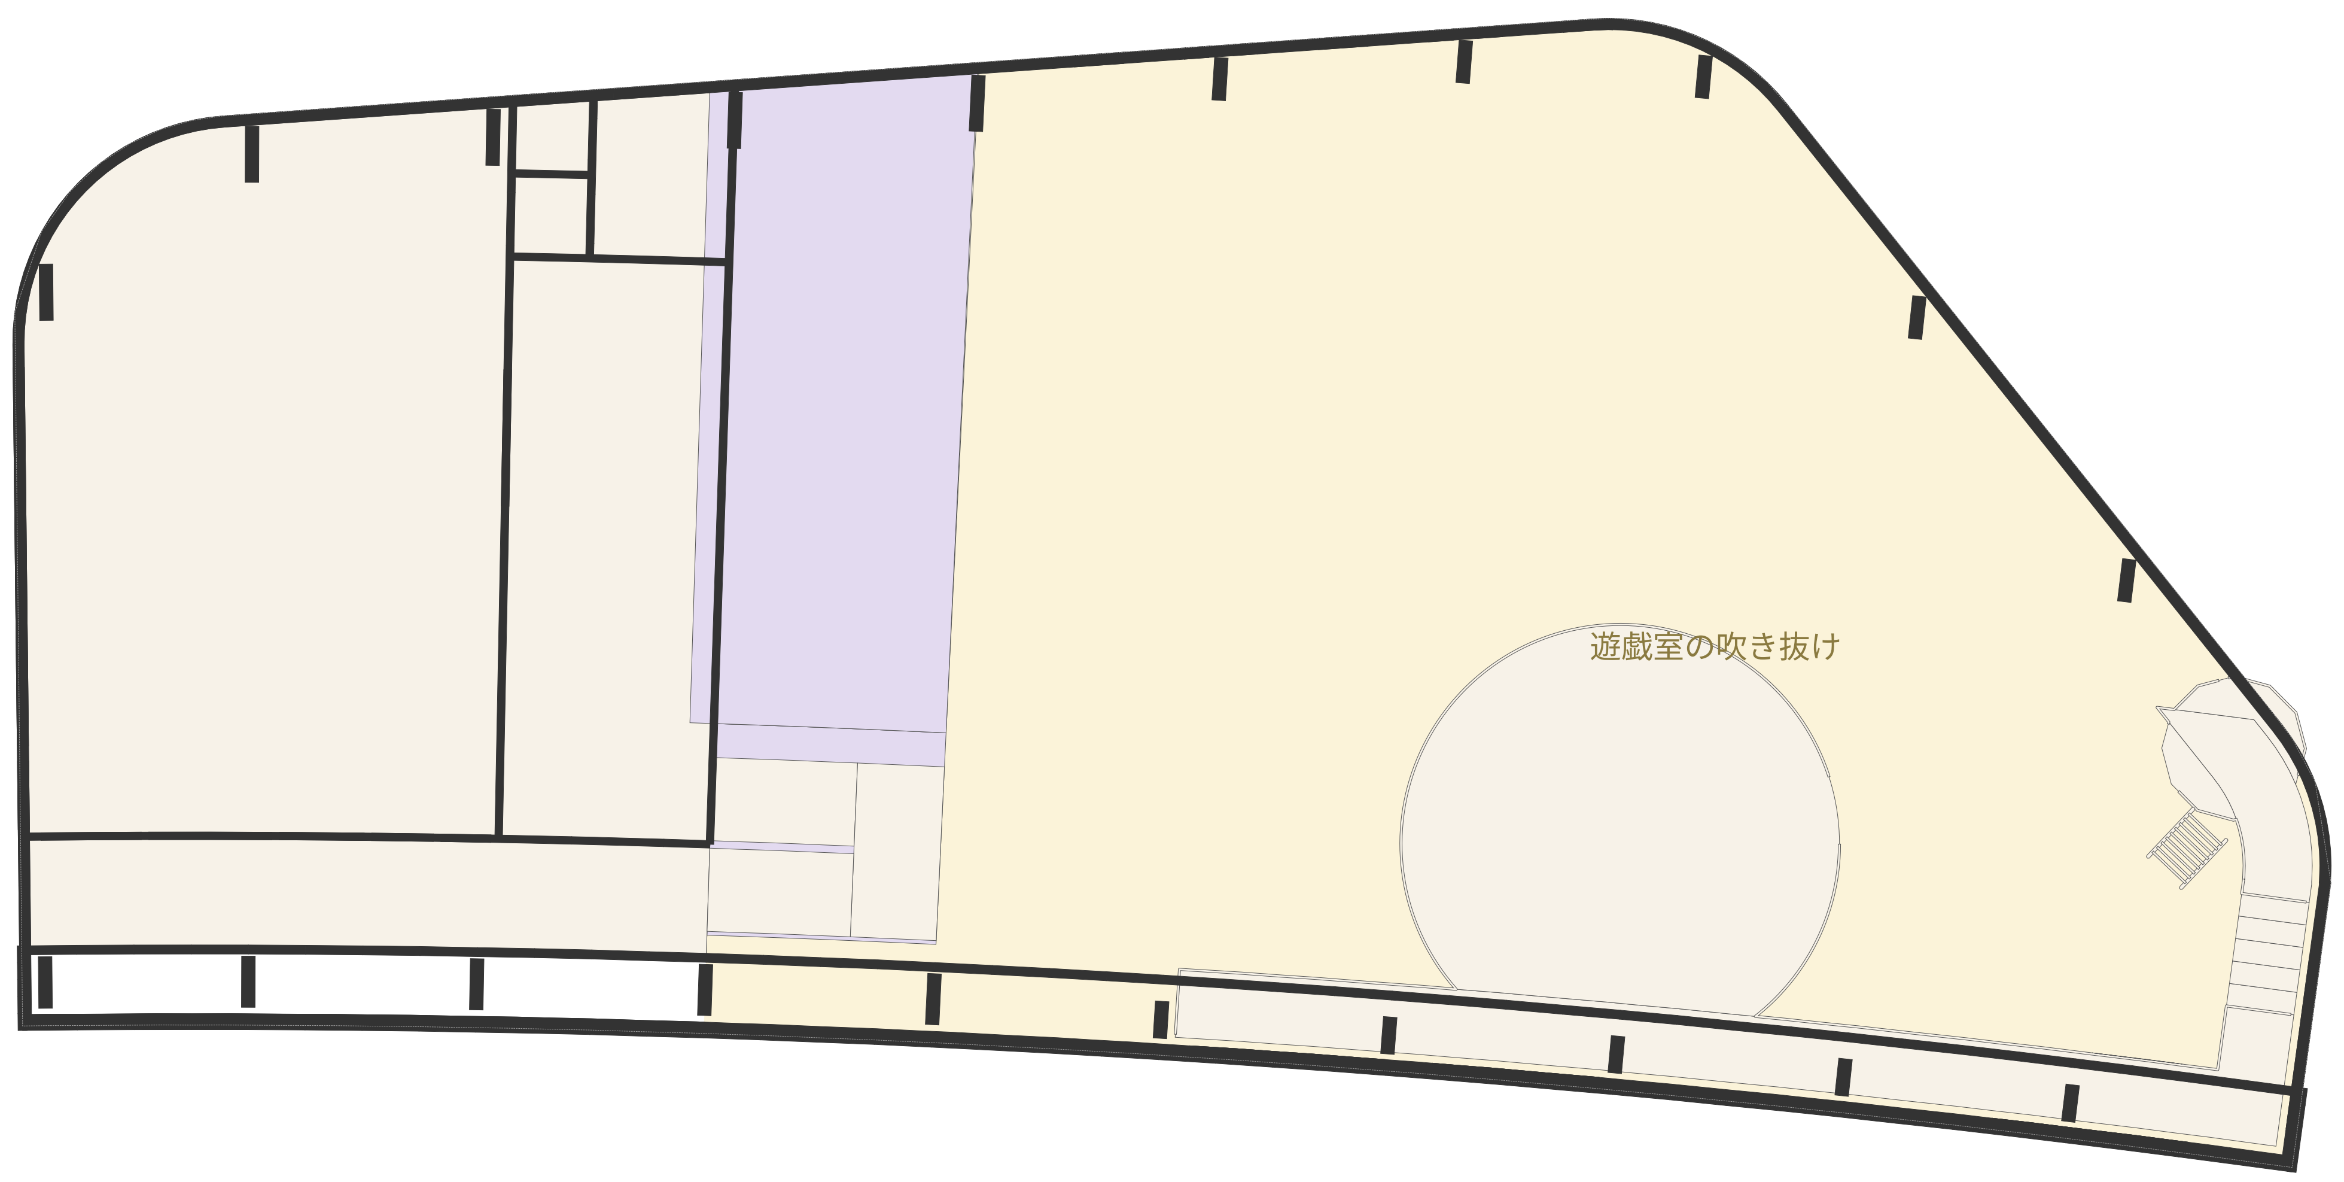

西館33×17 m → 326×172 mm（1階平面と同じ向き）

［割付の注記］フォーカス：空気・光・熱の流れが形の理由になっていること（断面Cを主役に）　／　目に入る順：断面C 1/50 → ①〜⑨ と環境の枠 → 運転表 → 断面B → 2階

こどもたちの育ち舎　5/5　暮らしと構造

建築設計実習 II — I　2026.11.05　木田

内観　ホール（A4）
海峡と飛び石・オープンキッチン
梁の見える天井・越屋根の光の線
（レンダリングか模型写真）

同じ部屋の一日　3〜5歳の保育室　断面1/100

10:00
遊ぶ

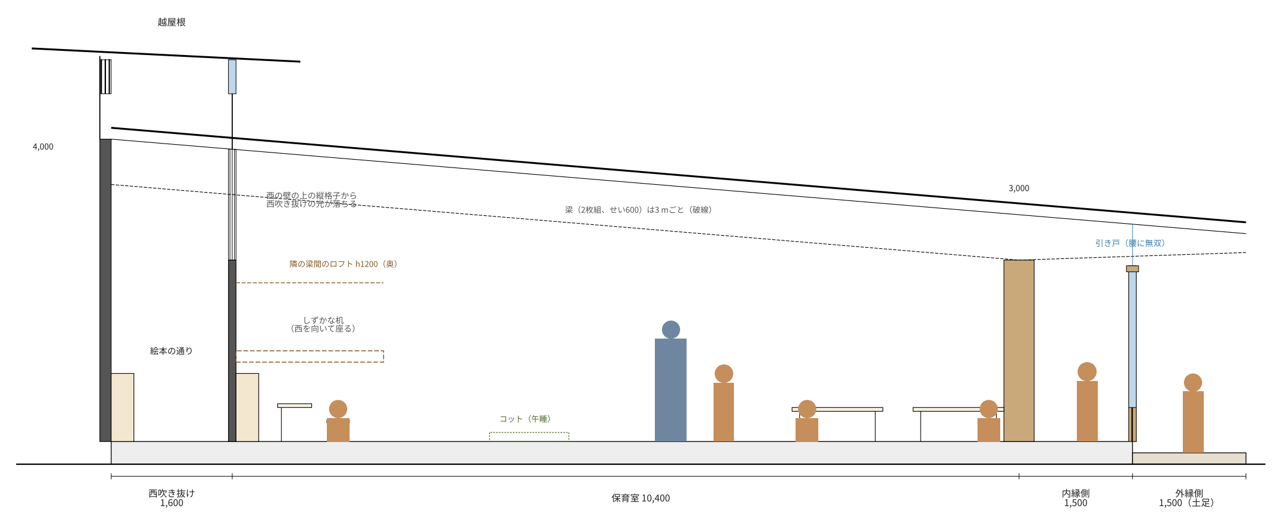

11:30
食べる

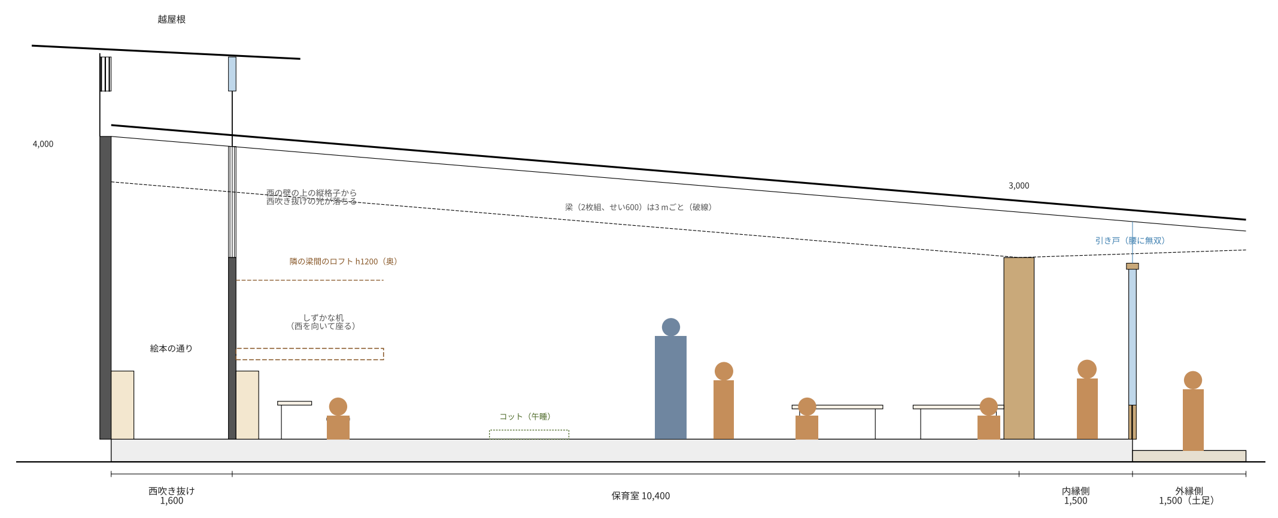

13:30
寝る

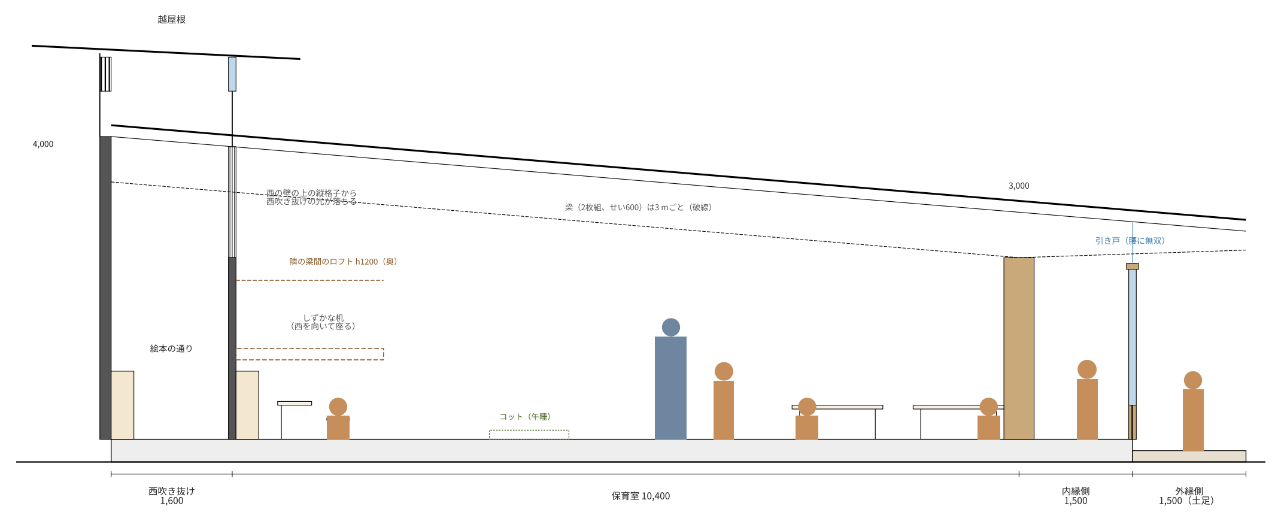

今は同じ図（既存の1/50を縮小）。時刻ごとに家具・人・光を描き分ける

遊戯室　平面・断面（縮小、遊戯室のチャット）

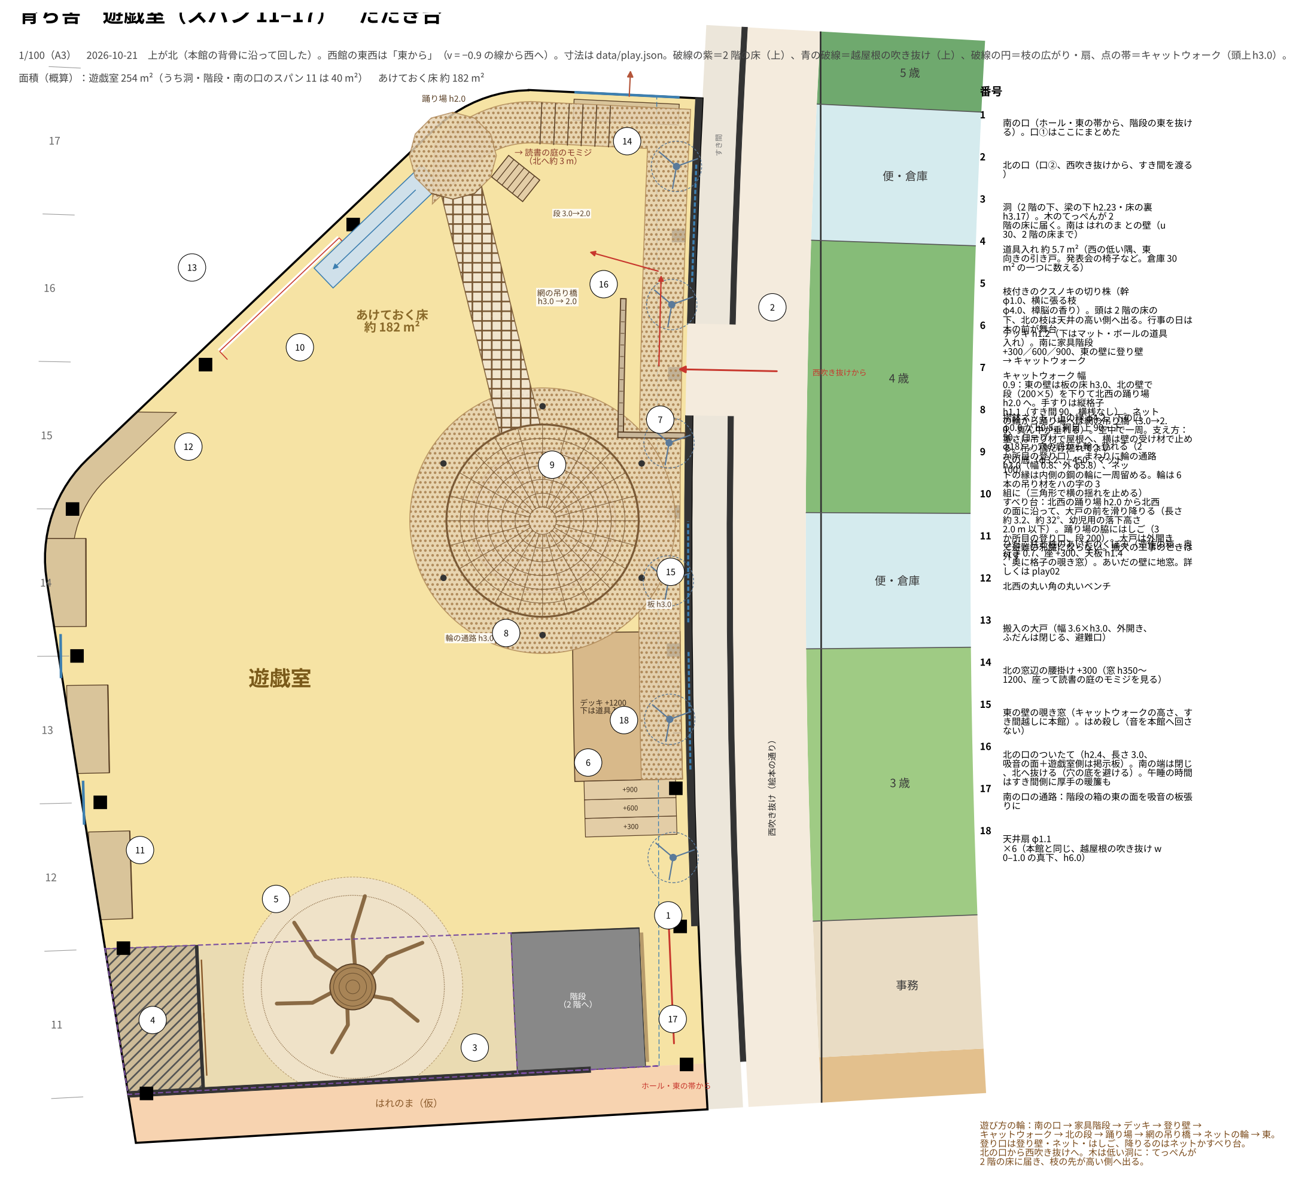

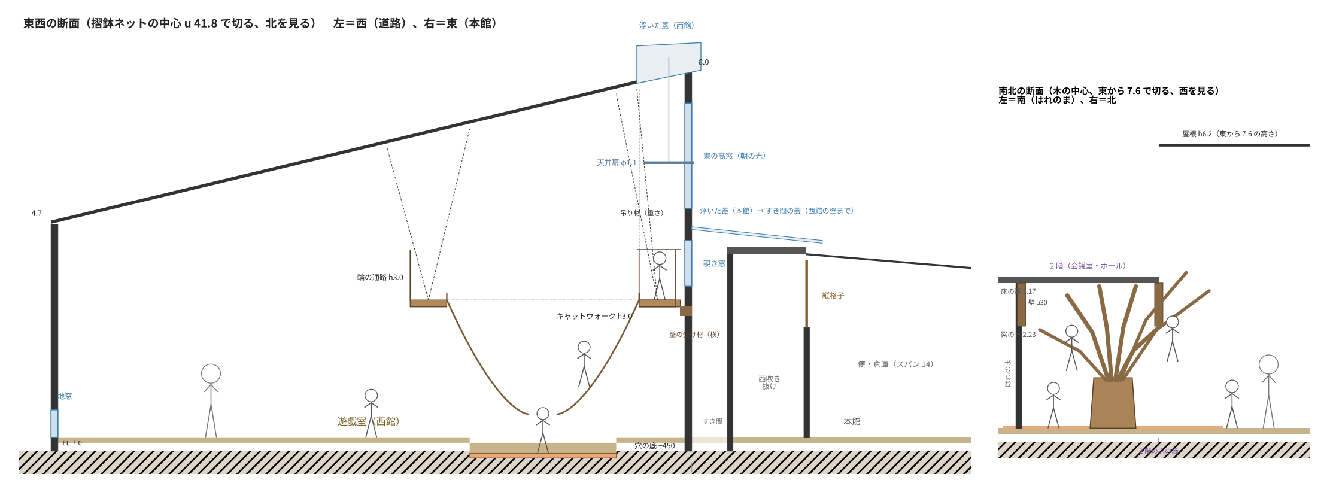

接合部　タメディア型　2枚の梁で柱を挟む（縮小）

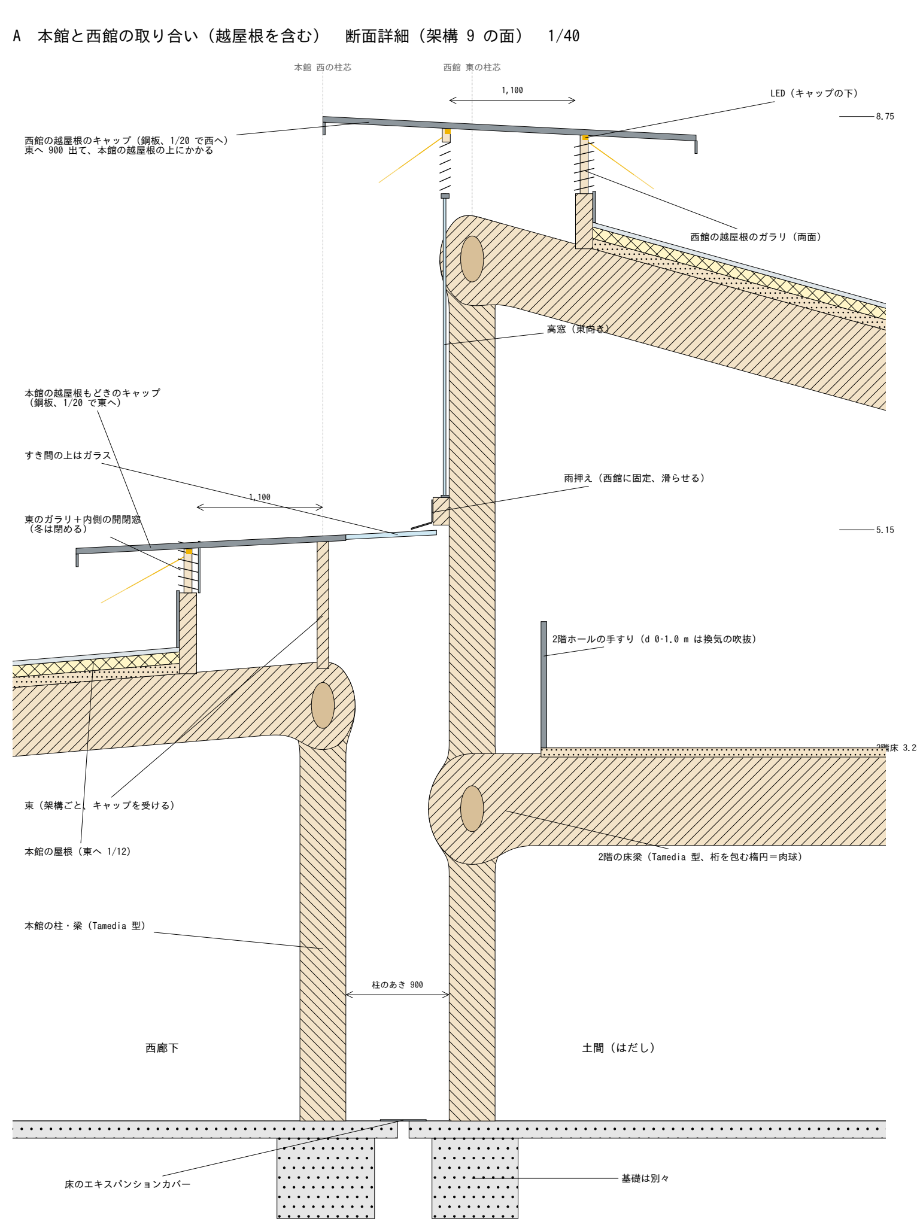

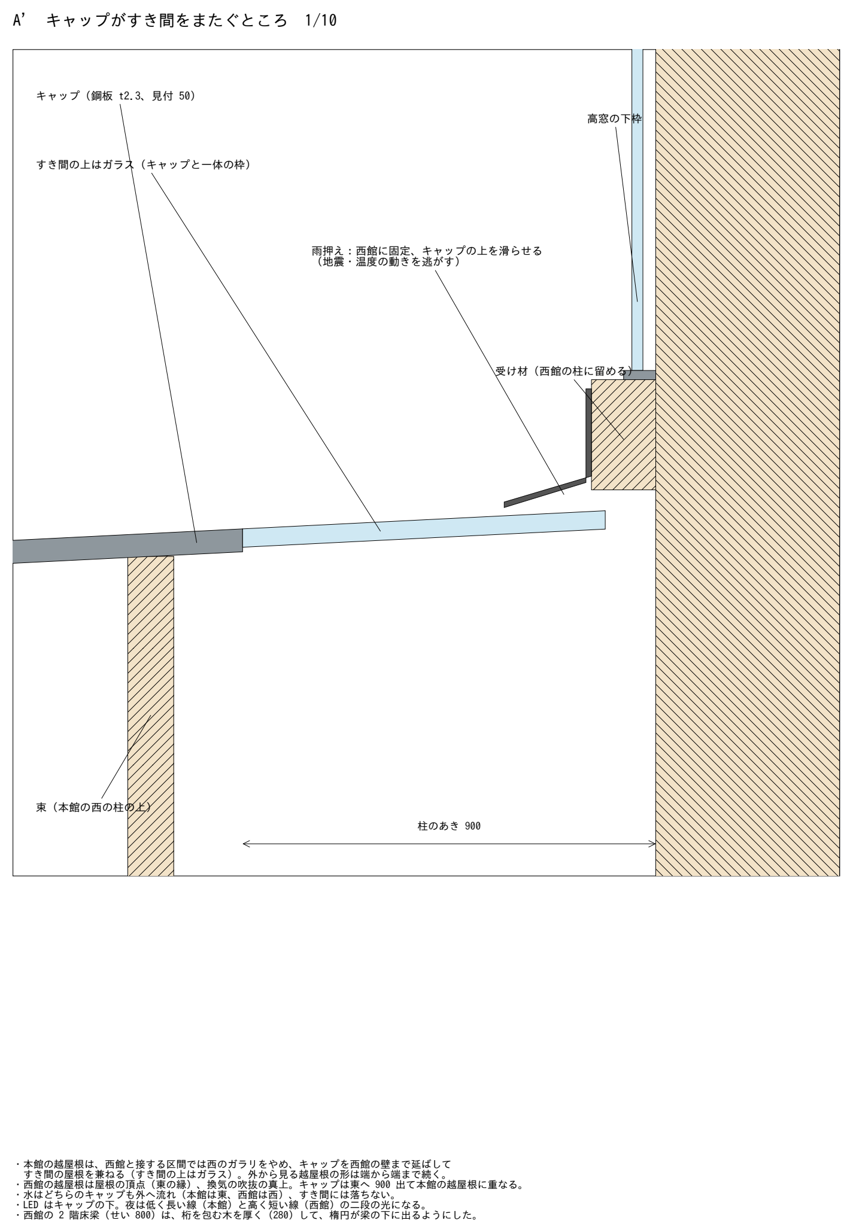

京都の間伐材・金物を減らした接合

スケルトン＆インフィル
3mスパンの骨格（固定）と
間仕切り・家具（可変）を色分け

今／定員が変わる／
学童・地域の場 の3コマ

園庭の断面　縮小（園庭のチャット）

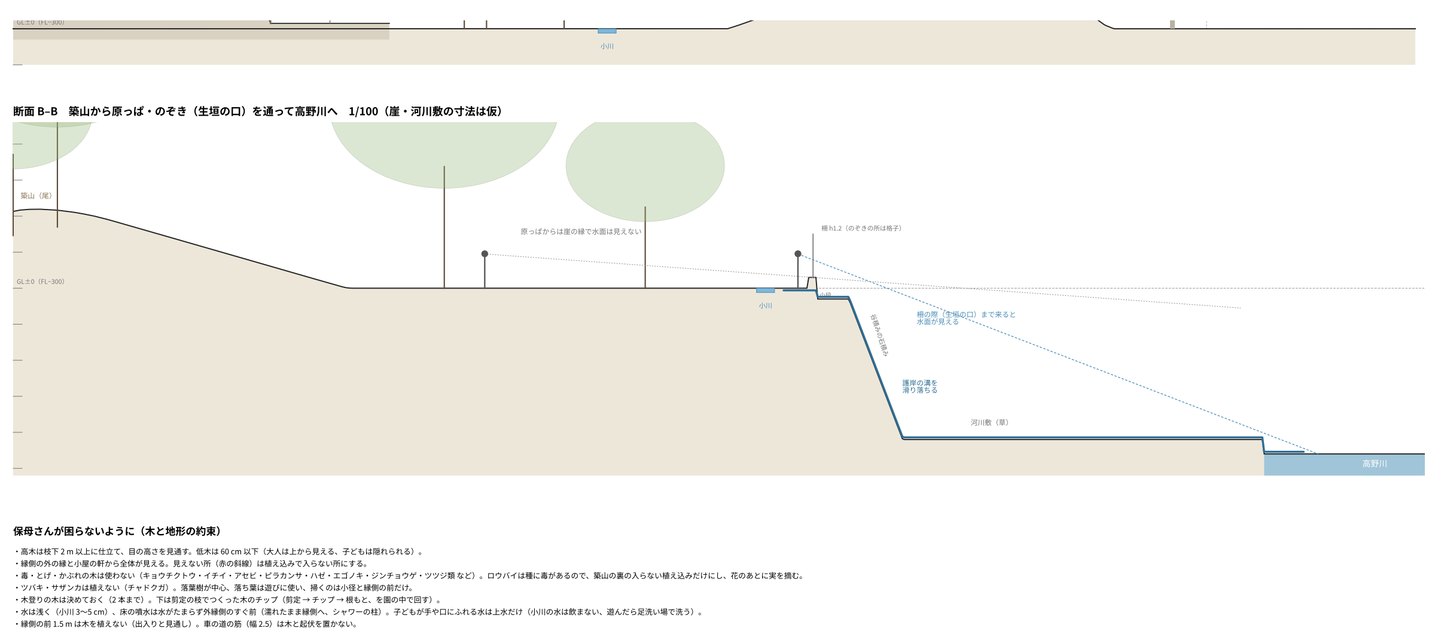

築山・小川・水遊び場は遊ぶの答え

面積表　㎡（仮）

室	要求	計画
乳児室（0・1歳）	約60×2	120.7
保育室（2歳）	約60	60.3
保育室（3歳）	約60	60.3
保育室（4歳）	約60	60.3
保育室（5歳）	約60	60.3
遊戯室	240以上	237.9
調理室	約60	60.5
医務室	約30	21.6
事務室	約60	23.0
休憩・会議（2階）	60＋30	94.1
はれのま	（追加）	21.9

3dmの床から自動で測った仮の値。
医務・事務の不足を確かめる。
園庭350・駐車5・延床2,000・
倉庫30・機械室30を本番で足す

inspired by

Asilo Nido Iride　Mario Cucinella Architects・Guastalla・2015
→ 梁の列が並ぶ長細い本館と、外に付く付属の建物

Tamedia　坂茂・Zürich・2013
→ 梁の端の楕円の頭と、それを貫く楕円の桁

レイモンド斑鳩こども園　キノアーキテクツ・斑鳩・2026
→ 室内に木を立てる（ホールの北山杉）

KAIT工房　石上純也・厚木・2008
→ 柱の配列：見る向きで景色が変わる並び

認定こども園らみどり　はりゅうウッドスタジオ・須賀川・2026
→ 内と外の二重の縁側、遊具を置かない地形の園庭

仙田満の園舎　環境デザイン研究所
→ 摺鉢のネット、キャットウォーク、ニッチ

Waldorf School of the Peninsula　California
→ 遊戯室の切り株

［割付の注記］フォーカス：近づいて読む人のための細部：寝る・遊ぶ・組み方・変わり方　／　目に入る順：内観 → 同じ部屋の一日 → 遊戯室 → 接合部 → S&I → 面積表 → inspired by