平面図　1階　FL+1500 で切断／2階（西館）2FL+1000 で切断　1/100

高野川を下に（配置図と同じ向き）。2階は西の道路の外に同じ向きで置いた（遊戯室は吹き抜けから見下ろす）。一点鎖線は敷地の境。二点鎖線は切断より上にある物（屋根の外形・越屋根・2階の床の縁など）

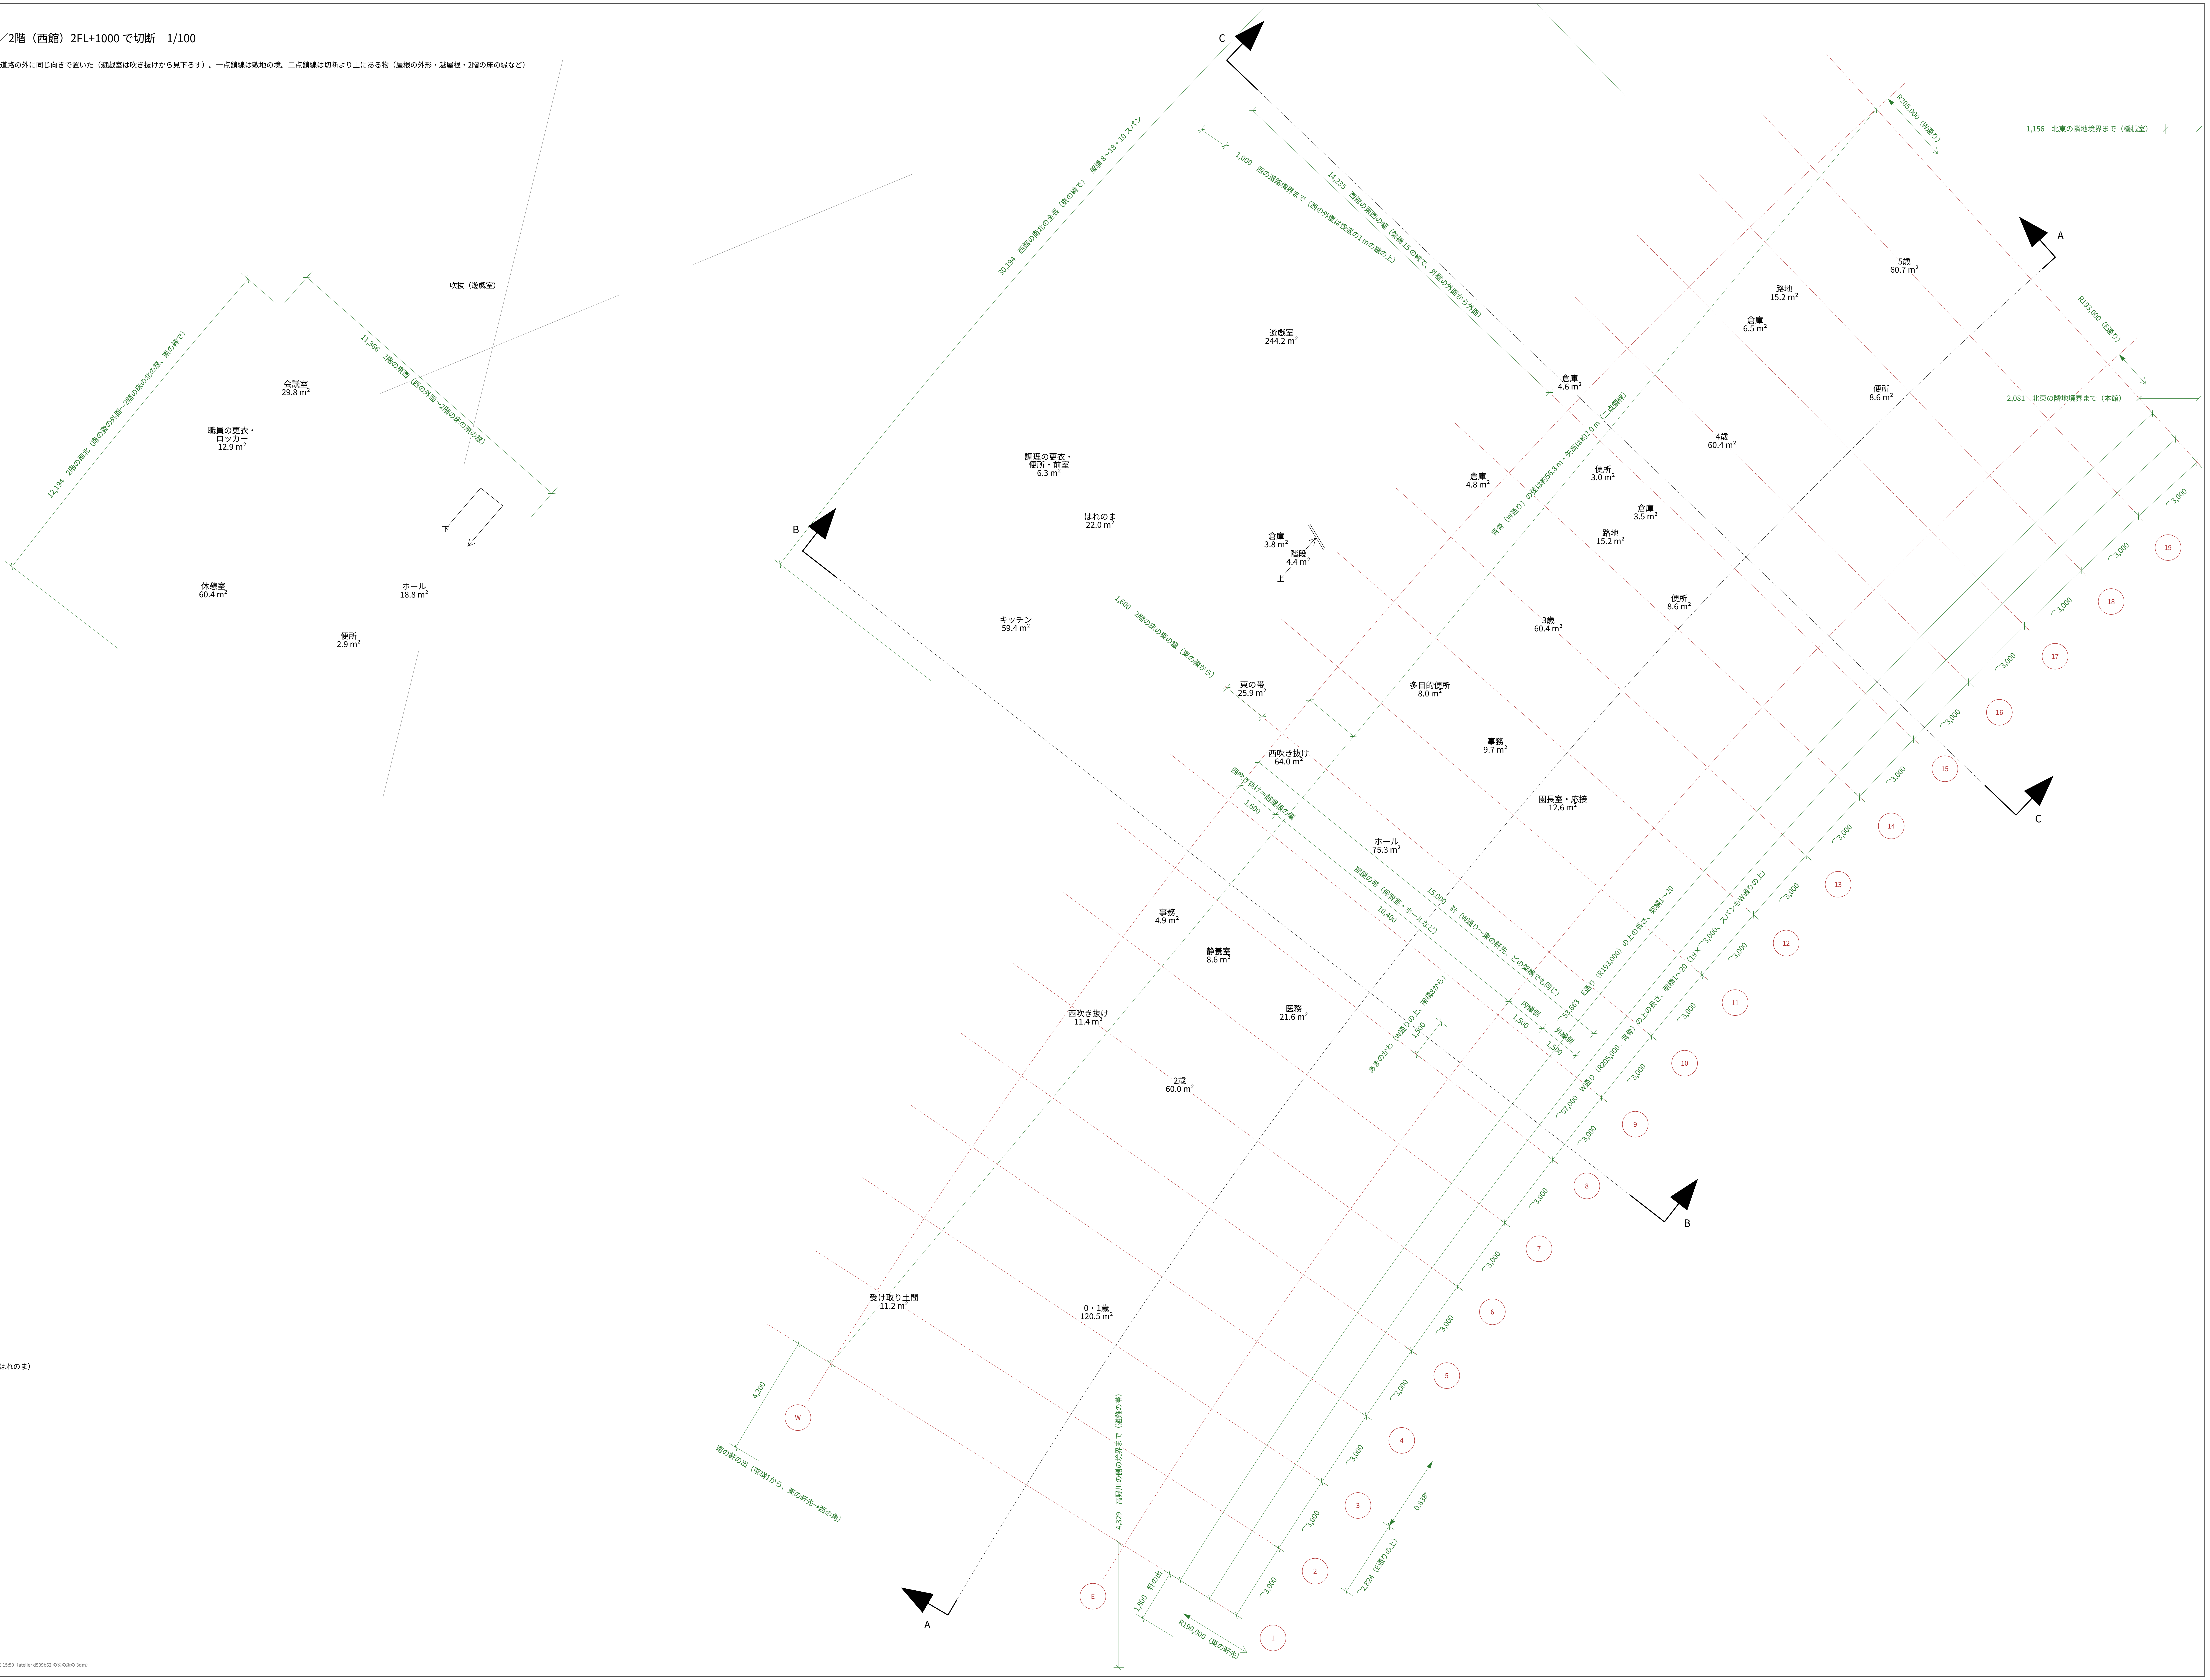

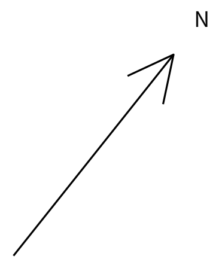

部屋の色

🟩 0・1歳〜5歳
🟨 こどものみんなの場所（遊戯室・はれのま）
🟫 通り・つなぐ場所（はだし）
🟫 土足の床
🟪 大人の場所
🟪 キッチン・調理の更衣
🟦 水まわり

0　5 m

こどもたちの育ち舎　3dm（sodachiya.3dm）から自動で作図　2026-10-28 15:50（atelier d509b62 の次の版の 3dm）