


平面　1/50（床から1.0で切る。灰の破線＝上の梁の2枚、色の破線＝吊り桟）　西が左、北が上

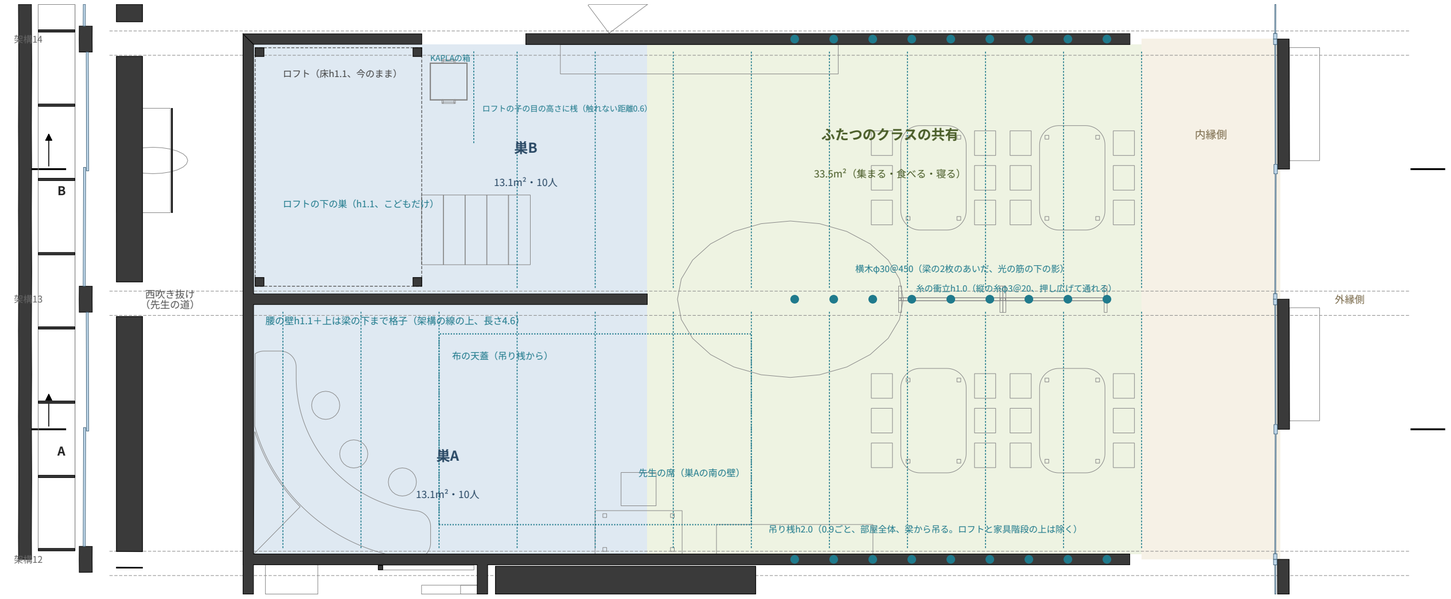

断面A　1/50（スパン12、北を見る）：巣Aは天井を張らず高いまま、低さは布の天蓋で

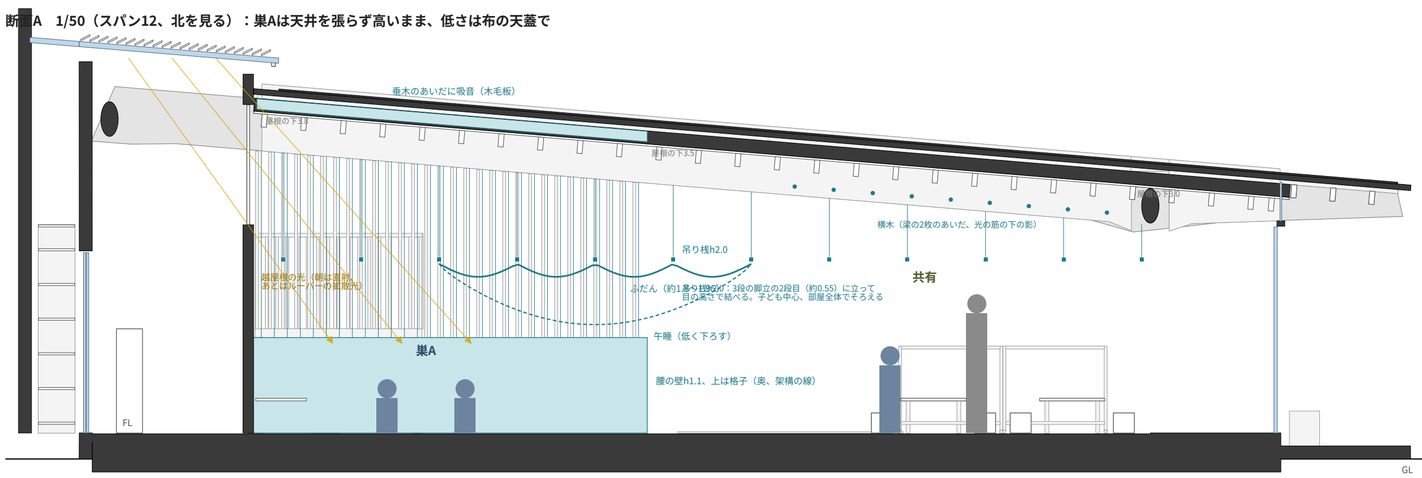

断面B　1/50（スパン13、北を見る）：巣Bはロフトの上（高く開けた）と下（低くこもる）

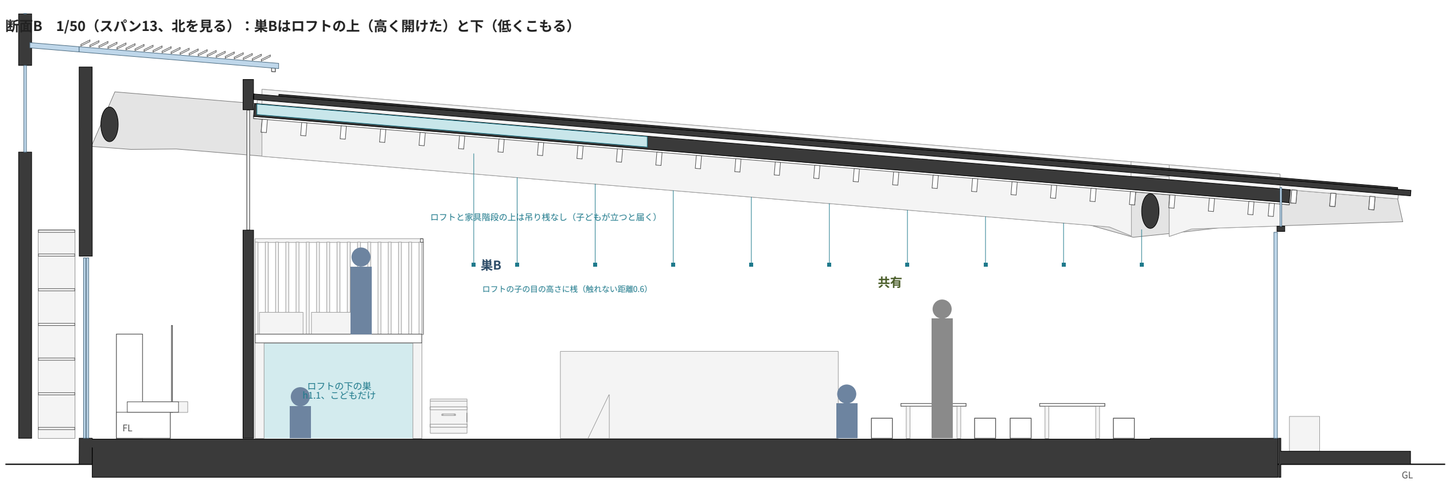

3歳の保育室の分け方

本館係　2026-10-24　スパン12–13（どの学年も同じ形）

ふたつの巣と共有の場所

20人を10人ずつの二つのグループに。西の半分を架構の線（u36）で分けて、それぞれの「巣」に。東の半分は二つで一緒に使う。同じ部屋を左右に並べず、みんなの場所 → 自分たちの場所と奥へ入っていく。隣の便所・倉庫のスパンも隣の学年と共有。

西は静か、でも天井は張らない

- 梁と梁のあいだは東から越屋根へ空気が上る換気の道。西に天井を張るとその出口をふさぐ。
- 西は建物でいちばん高く、越屋根の光が落ちる所。「高くて明るくて静か」＝森の中、お堂の落ち着き。

低さは物で

- 巣A：吊り桟（h2.0）から布の天蓋（しずかな角の上は空け、東へ）。ふだんは約1.8〜1.95、午睡は低く下ろす。先生が自分で吊り替えられる。
- 巣B：今のロフトの下（h1.1）がこどもだけの巣、ロフトの上は高く開けた場所。一つの西に二つの静けさ。

静けさは音で

- 巣の上の垂木のあいだに吸音（木毛板）。
- 巣の床はやわらかく（コルクか畳）。
- 腰の壁h1.1と格子で東のにぎやかさから少し離す。上は格子なので見通しと光の筋の光は通る。

脚立の2段目で目の高さ（子ども中心）

- 吊り桟h2.0を部屋全体に：3段の脚立の2段目（約0.55）に立った先生（身長155〜160）の目の高さで結べる。背の高い先生は少しかがむ。リボン・布の下端は子どもの手の届く高さより上で止める（首に絡まない）。

先生の席

- 先生の机は巣Aの南の壁に沿って、しずかな角の東（巣Aと共有の境、天蓋の下）。壁を背にして、巣Aと共有を横から見守る（巣Bは腰の壁の格子ごし）。

ロフト（巣B）

- 床の上端h1.2、下は1.1：3歳はぎりぎり立て、大人はかがむ。
- 手すりh+1.1（縦格子90以下）、家具階段は1段0.2×5。

今の3dm（切り口）　灰の線＝今の家具・見えがかり

この案で足したもの（3dmのスクリプトに入れた、更新係の作り直し待ち）

巣（静か）

共有

内縁側

面積は壁芯でなく床の上の概算（m²）。保育室全体は面積表の3歳（約60m²）。