育ち舎　園庭（だいさんかく・しずかのもり）　たたき台６

配置 1/200　断面 1/100（A2）　2026-10-21　遊具を置かず、木と地形で遊ぶ庭。山・川・原っぱ・森、そのあいだにたくさんのニッチ。

地形は GL（＝FL−300）からの高さ。等高線 0.2 m ごと（1 m を太く）。築山の位置と形はこの図で決め直した（Keynote の位置は前提にしていない）。



1/200　高野川を下に（北は右上）

凡例

- 高木・落葉（ケヤキ・エノキ・ムクノキ・コナラ・クヌギ）／中木・落葉（ヤマザクラ・イロハモミジ・エゴノキ・アオダモ・ヤマボウシ）
- 実のなる木（カキ・ジューンベリー・ウメ）
- 境の常緑（シラカシ・ソヨゴ・モチノキ）
- 木登りの木（エノキ、下は木のチップ）
- 小川（幅 0.5、岸は急、底は平らで浅い。終わりは護岸の溝を滑り落ちる）・水浴び場
- 床の噴水（水遊び場、上水をためずに一度だけ使う、排水は雨の川へ）
- 暗渠（用水路から北の角を通って、みなもとまで）
- 雨の川（雨落ちの溝、玉石。本館の雨は樋なしで落ち、南へ流れて護岸の溝から高野川へ。溢れたらすりばちが雨の池）
- 砂場・粒の遊び場（1〜2 mm）
- 等高線 0.2 m（太線 1.0 m）
- 剪定・搬入の車の道（芝の保護材 幅 2.5、ふだんは庭）
- 先生のいる所（縁側の外の縁・小屋の軒、目の高さ GL+1.35）
- 死角：どの先生からも子どもの頭（地面+0.9）が見えない所

ニッチ（静かに遊べる・ひとりになれる所）

1. みなもと：二つの丘のあいだから湧き出す石組み
2. 丸太の輪：切り株の腰掛け（北のもり）
3. ほら：築山の北西の面の木の枠のくぼみ（3歳の縁側から見える向き）
4. 山の肩の平ら：腰掛ける段（丸太の土留め）
5. 木登りの木（エノキ）の根もと
6. おくのもり：低い起伏と倒木
7. のぞき：小川が護岸の溝を滑り落ちる所（生垣の口、柵ごしに高野川を覗き込む）
8. すりばち：小さなくぼ地（お話の輪）
9. 柳の家：小川のほとりの生きたヤナギのドーム、しずかのもりの入口
10. 水浴び場（0〜2 歳、上水）と粒の遊び場
11. 川辺の座り石

数字（この図から）

だいさんかく（しずかのもりを含む）約 886 m²　うち しずかのもり 約 162 m²（3〜5 歳 70 人で 1 人 10.3 m²、基準は 3.3）

築山：頂 +2.2 m、裾の広さ 約 127 m²、土 約 108 m³。起伏・土手を足すと盛る土は 約 146 m³

→ 北のもりへの上り（最大 +0.45）も含む。基礎・小川・すりばち・遊戯室の穴の底を掘った土で足りる量（運び込まない、外へ出さない）

小川：地上の長さ 約 46 m、川床 GL−0.15 → −0.40（勾配 約 1/200）。木 48 本（下書き、種類はこれから）

床の噴水：約 17 m²、噴き口 17 個（0.8 m ごと）＋シャワーの柱。上水、排水は雨の川へ。雨の川：屋根 約 880 m²、100 mm/h で南の端 約 24 L/s、溝 0.5×0.2・1/200 で 約 50 L/s（目安）

小屋：19.7 m²（便所 6.8＋倉庫 12.9）。倉庫は教材庫×2（13.0）＋遊戯室の道具入れ（5.7）に足して 30 m² を超える


コンポスト：小屋の軒の下に木枠 1×1 m×4（落ち葉・入れる・寝かせる・できた）。4・5 歳の当番がキッチンから野菜くずをもらい、落ち葉と重ね、できた土を畑へ運ぶ（ユーザー）

死角：約 28 m²。築山の裏（隣家側）の植え込みと、北のもりの奥。植え込みは入らない所にする

保母さんが困らないように（木と地形の約束）

- 高木は枝下 2 m 以上に仕立て、目の高さを見通す。低木は 60 cm 以下（大人は上から見える、子どもは隠れられる）。
- 縁側の外の縁と小屋の軒から全体が見える。見えない所（赤の斜線）は植え込みで入らない所にする。
- 毒・とげ・かぶれの木は使わない（キョウチクトウ・イチイ・アセビ・ピラカンサ・ハゼ など）。
- ツバキ・サザンカは植えない（チャドクガ）。落葉樹が中心、落ち葉は遊びに使い、掃くのは小径と縁側の前だけ。
- 木登りの木は決めておく（2 本まで）。下は剪定の枝でつくった木のチップ（剪定 → チップ → 根もと、を園の中で回す）。
- 水は浅く（小川 5〜10 cm）、床の噴水は水がたまらず外縁側のすぐ前（濡れたまま縁側へ、シャワーの柱）。子どもが手や口にふれる水は上水だけ（小川の水は飲まない、遊んだら足洗い場で洗う）。
- 縁側の前 1.5 m は木を植えない（出入りと見通し）。車の道の筋（幅 2.5）は木と起伏を置かない。

断面 A–A　ホールから築山の頂を通って比叡山の向きへ　1/100

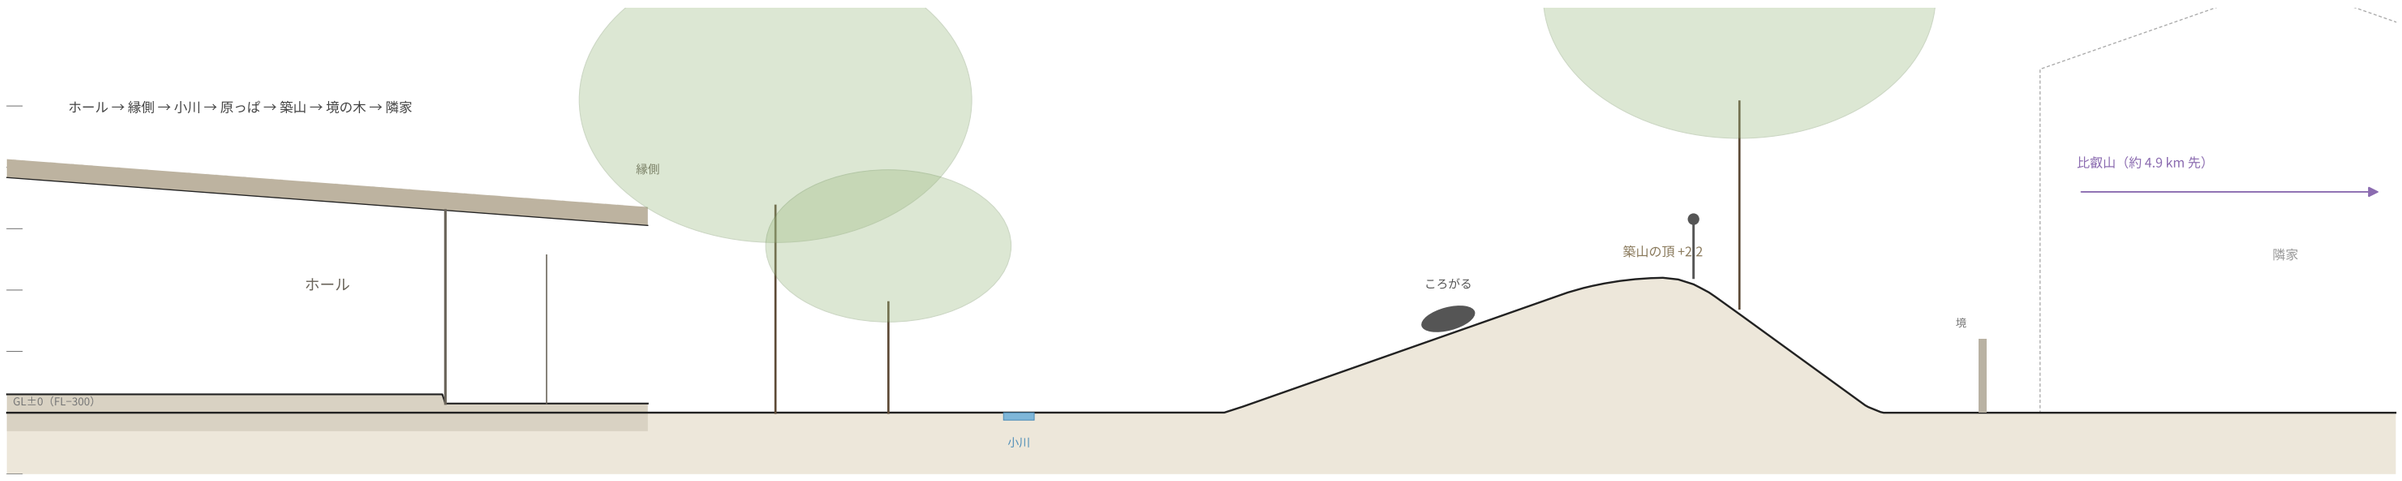

断面 B–B　築山から原っぱ・のぞき（生垣の口）を通って高野川へ　1/100（崖・河川敷の寸法は仮）

