
育ち舎　南の入口まわり（キッチン・はれのま・事務・医務）　ラフ

1/100（A3）　2026-10-21　架構の番号は南から（架構 k は南の妻から 3(k−1) m、スパン k は架構 k と k+1 のあいだ）。面積（芯々、概算）：キッチン 60 m²　はれのま 20 m²　事務（スパン7 の西）13 m²　医務 22 m²＋内縁側

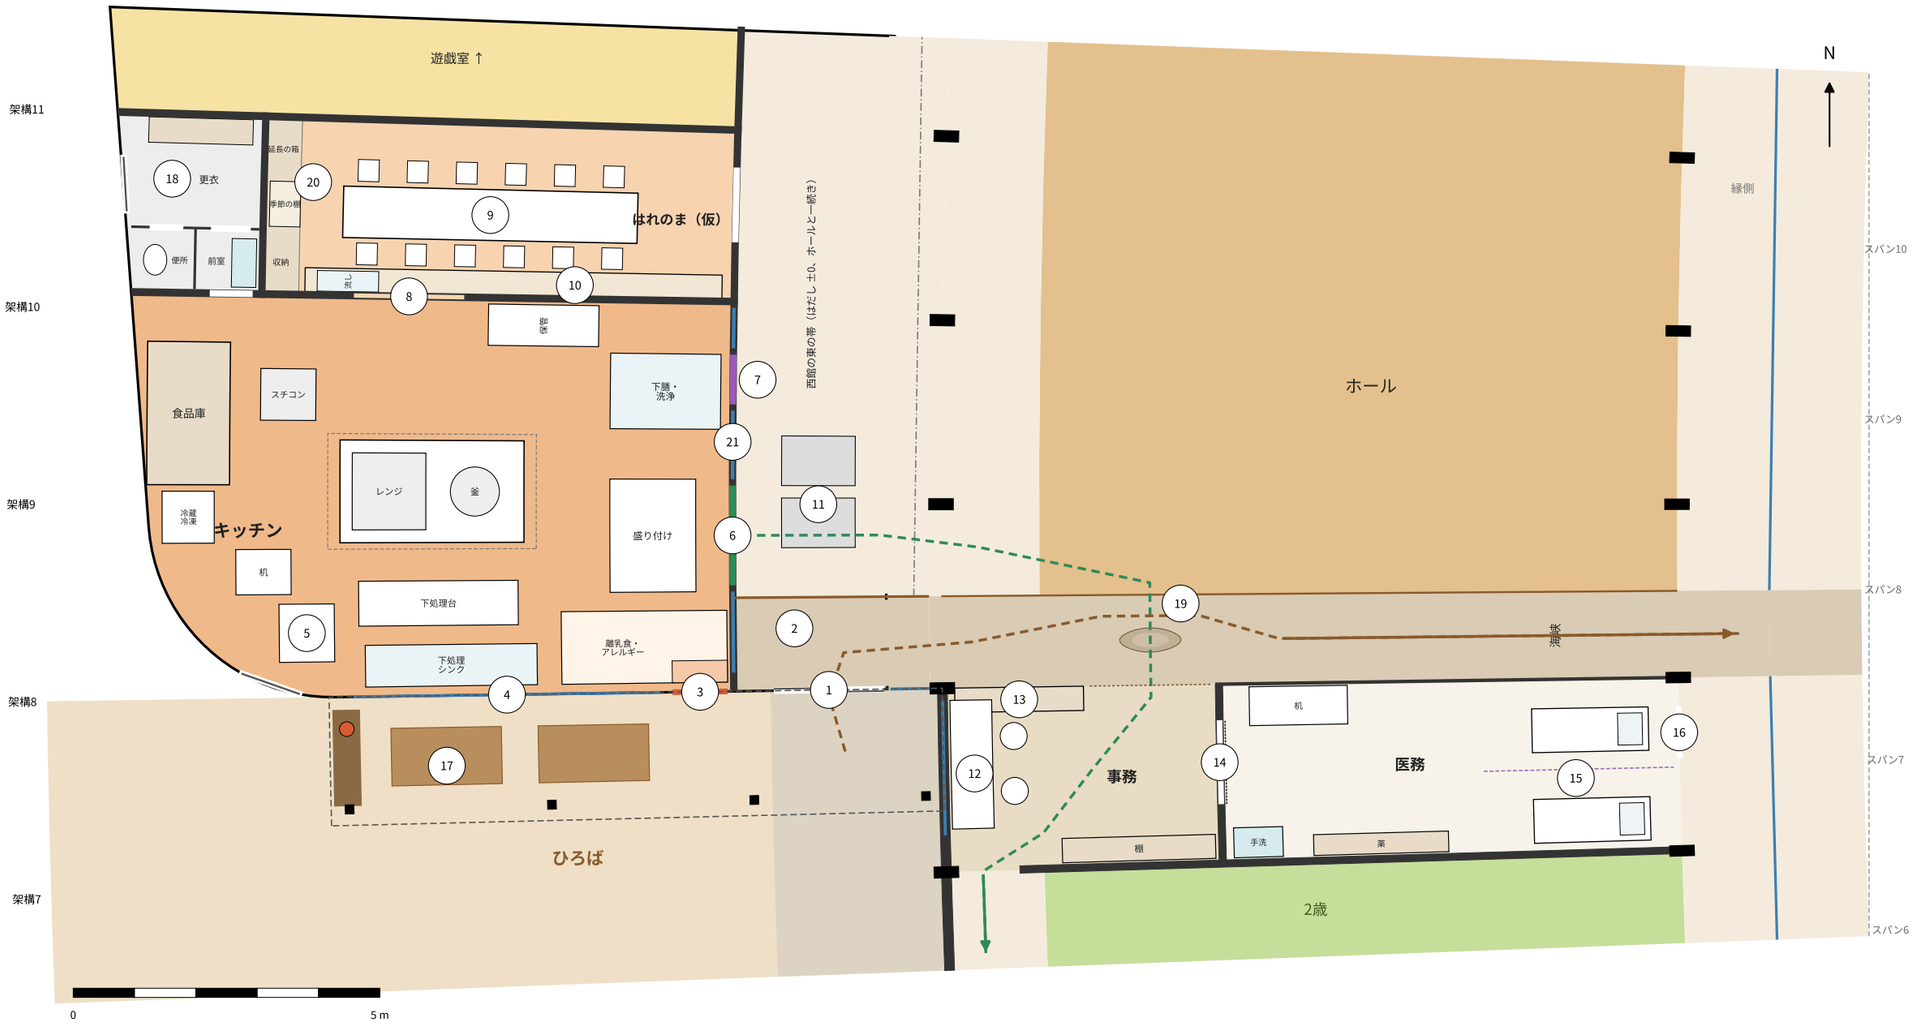

1　入口（西館の南の面、引き戸 1.8）。すき間はガラス

2　海峡の延長（土足 −150）。框から北は東の帯（はだし ±0）

3　「今日のごはん」の窓（子どもの高さ、中は見本の棚）

4　キッチンの南のガラス（下処理が見える）

5　検収（勝手口のすぐ内側）

6　配膳口（盛り付け → ワゴン）

7　返却口（配膳口と分ける、一方通行）

8　見える台所（はれのまへの受け渡しの窓）

9　はれのまの机（幅 0.8、12 人）

10　キッチン沿いのカウンター h600（子どもの流し・おやつの台・食育）

11　配膳のワゴン置き場（東の帯）

12　事務の机（西の窓：小径の出口・手水・ひろば・入口が見える）

13　おはようの窓口（低いカウンター）。その脇が開いた口（幅 2.0、戸なし）で、前に飛び石

14　医務への開口（引き込み戸、ふだんは開けておく）

15　ベッド×2（カーテンで分ける、静養・隔離）

16　医務の戸（内縁側から、先生が子どもを連れてくる）

17　下屋の下の縁台とお茶の棚（電気ポットは h1100 の棚の上：給湯ロック・転倒湯もれ防止・蒸気レス・マグネットプラグ）

18　調理の職員の更衣・便所・前室（外から直接：西の面の戸 → 更衣 → 前室 → キッチン）

19　飛び石（流れに沿うレンズ形 0.4×1.0、上面は床の高さ、縁はなだらか）

20　はれのまの収納（西の端の壁、延長の箱・季節の棚）

21　キッチンの東の面：低い位置（h450）からのガラス（オープンキッチン、東の帯とホールから見える）

┅ 緑：配膳の保育士と 2 歳の道（配膳口 → 東の帯 → ホールの西 → 飛び石で海峡を渡る → 事務を曲がりながら抜ける → 2 歳の道）。┅ 茶：3〜5 歳（入口 → 海峡 → 縁側、おはようの窓口の前を通る）。キッチンは 検収 → 下処理 → 加熱 → 盛り付け → 配膳口、返却口 → 洗浄 → 保管 の一方通行。

西館の東の帯とすき間は、エキスパンションをはさんでホールと一続き（はだし ±0）。本館の西の壁はホールの範囲では開く。はれのまの日常：朝夕の延長保育（キッチンが近く、補食・おやつ）、5 歳のお手伝い当番・おやつづくり、3〜5 歳がクラスごとに順番に食べる日。ときどき：誕生会・行事食・保護者の試食会・離乳食の相談。