

高野川の側の立面図　1/100　（川の向こうから、川の辺に直角に。北西を見る、右が北東）

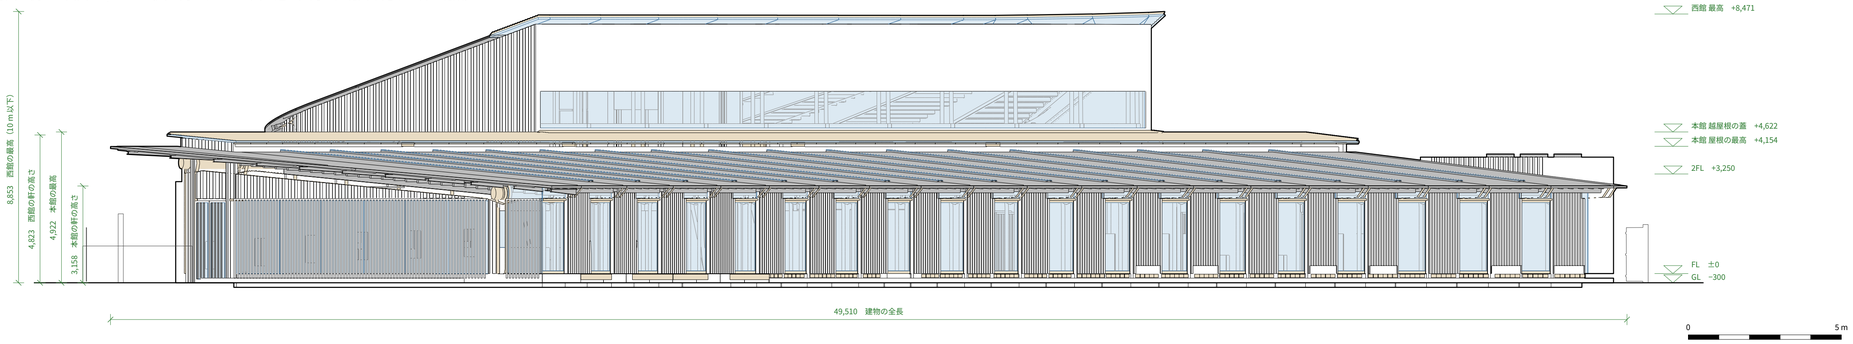

北の妻の立面図　1/100　（架構 20 に正対。南を見る、右が西）

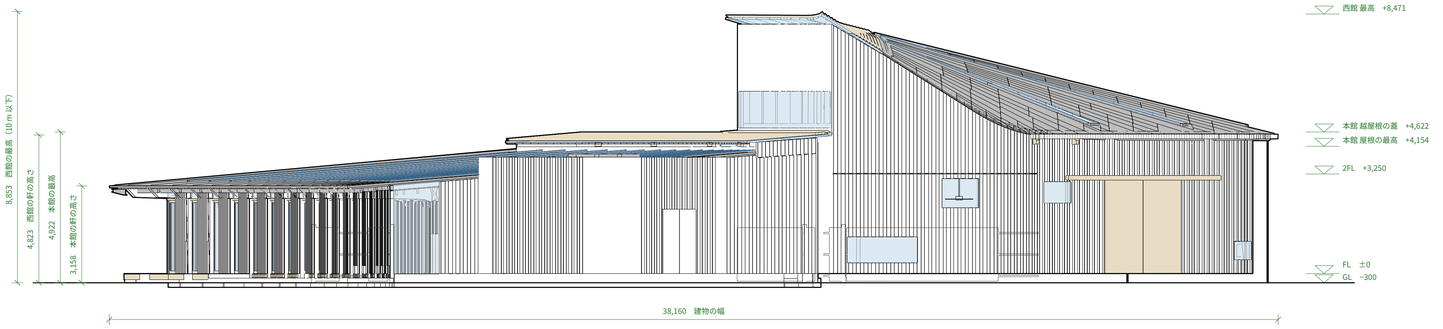

建物と、その手前の外構（塀・柵・木戸・棚・柱、細い線）。駐車・駐輪・室内の家具は省いた。灰色は屋根の面、薄い青はガラス（崇は細い灰色の線で透けて見える）。建物の外形は太い線。
高野川の側は川の向こうから川の辺に直角に。北の妻は架構 20 に正対。

立面図 2　高野川の側・北の妻　1/100（A1）