育ち舎　遊戯室（スパン 11–17）　たたき台

1/100（A3）　2026-10-21　上が北（本館の背骨に沿って回した）。西館の東西は「東から」（v＝−0.9 の線から西へ）。寸法は data/play.json。破線の紫＝2 階の床（上）、青の破線＝越屋根の吹き抜け（上）、破線の円＝枝の広がり・扇、点の帯＝キャットウォーク（頭上h3.0）。

面積（概算）：遊戯室 254 m²（うち洞・階段・南の口のスパン 11 は 40 m²）　あけておく床 約 182 m²




番号

1. 南の口（ホール・東の帯から、階段の東を抜ける）。口①はここにまとめた
2. 北の口（口②、西吹き抜けから、すき間を渡る）
3. 洞（2 階の下、梁の下 h2.23・床の裏 h3.17）。木のてっぺんが 2 階の床に届く。西に腰掛けの台 +300
4. 道具入れ 約 5.7 m²（西の低い隅、発表会の椅子など。倉庫 30 m² の一つに数える）
5. 枝付きの切り株（幹 φ1.0、枝の広がり φ4.0）。頭は 2 階の床の下、北の枝は天井の高い側へ出る。行事の日は木の前が舞台
6. デッキ h1.2（下はマット・ボールの道具入れ）。南に家具階段 +300／600／900、東の壁に登り壁 → キャットウォーク
7. キャットウォーク h3.0、幅 0.9（東の壁と北の角に沿う、手すり h1.1）。ネットの輪から北の側へ橋（幅 0.9）を渡し、空中の輪にする
8. 摺鉢ネット（上の縁 φ4.2、下の口 φ0.6 が h0.5）。まわりに輪の通路 h3.0（幅 0.8、外 φ5.8）、ネットの縁は通路の内側の鋼の輪に一周留める。輪は梁から 6 本の吊り材
9. 穴の底（φ3.2、−450、マット 100）
10. すべり台（キャットウォークの西の端 → 床）
11. ひだ：柱と柱のあいだのくぼみ（造作の箱、奥行き 0.7、座 +300、天板 h1.4、奥に格子の覗き窓）。あいだの壁に地窓。詳しくは play02
12. 北西の丸い角の丸いベンチ
13. 搬入の大戸（幅 3.6×h3.0、ふだんは閉じる、避難口）
14. 北の窓辺の腰掛け +300（窓 h350〜1200、座って読書の庭のモミジを見る）
15. 東の壁の覗き窓（キャットウォークの高さ、すき間越しに本館）
16. 天井扇 φ1.1 ×6（本館と同じ、越屋根の吹き抜け w 0–1.0 の真下、h6.0）

遊び方の輪：南の口 → 家具階段 → デッキ → 登り壁 → キャットウォーク ⇄ ネットの輪 ⇄ 橋 → ネットで降りる（穴の底）／すべり台 → 北の口から西吹き抜けへ。木は低い洞に：てっぺんが 2 階の床に届き、枝の先が高い側へ出る。

東西の断面（摺鉢ネットの中心 u 41.8 で切る、北を見る）　左＝西（道路）、右＝東（本館）

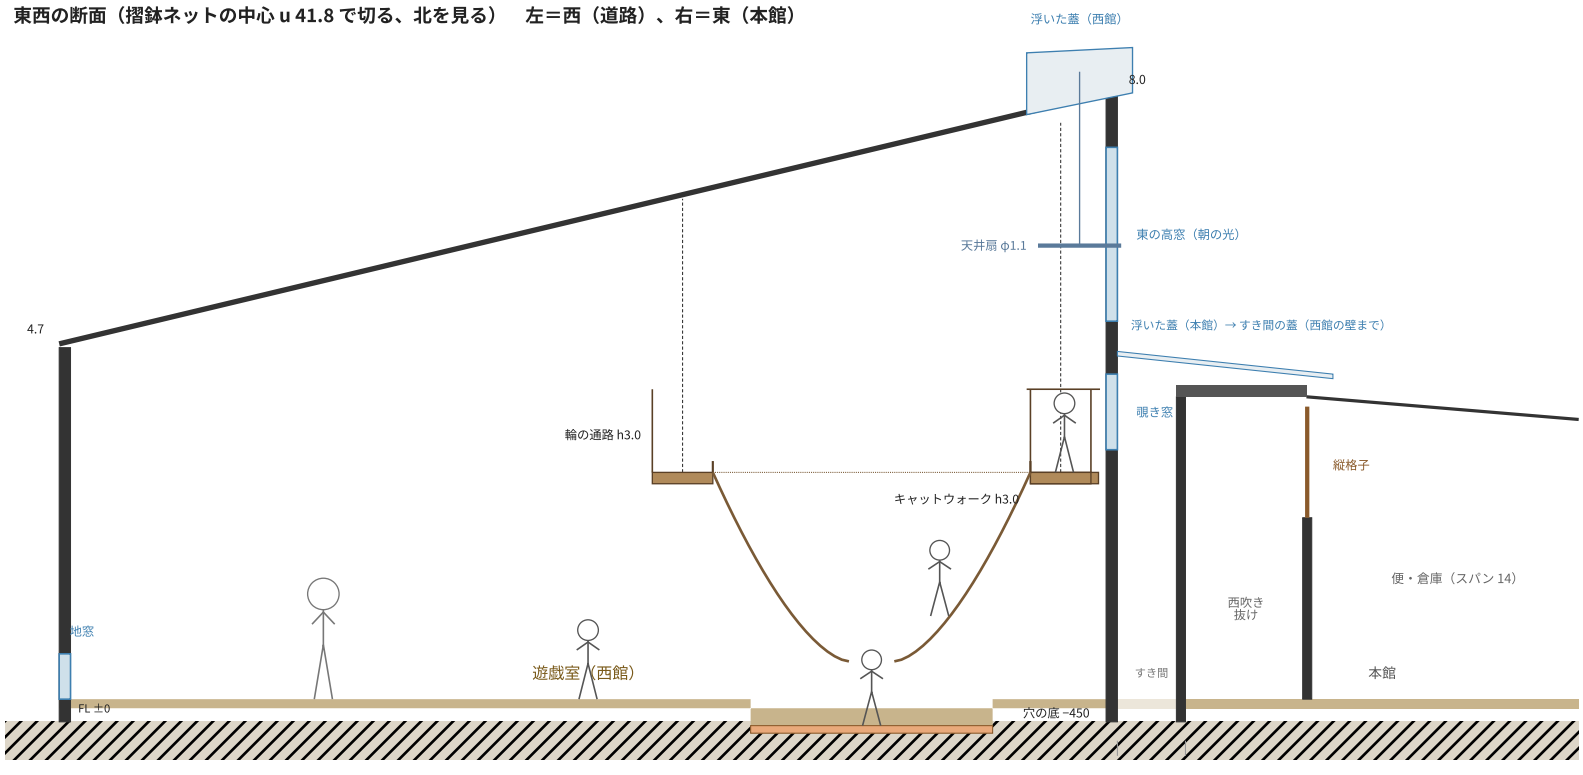

南北の断面（木の中心、東から 7.6 で切る、西を見る）
左＝南（はれのま）、右＝北

