壁に貼ったとき　左：1〜3を縦につなぐ（高さ約1.8 m）　右：4・5を縦につなぐ

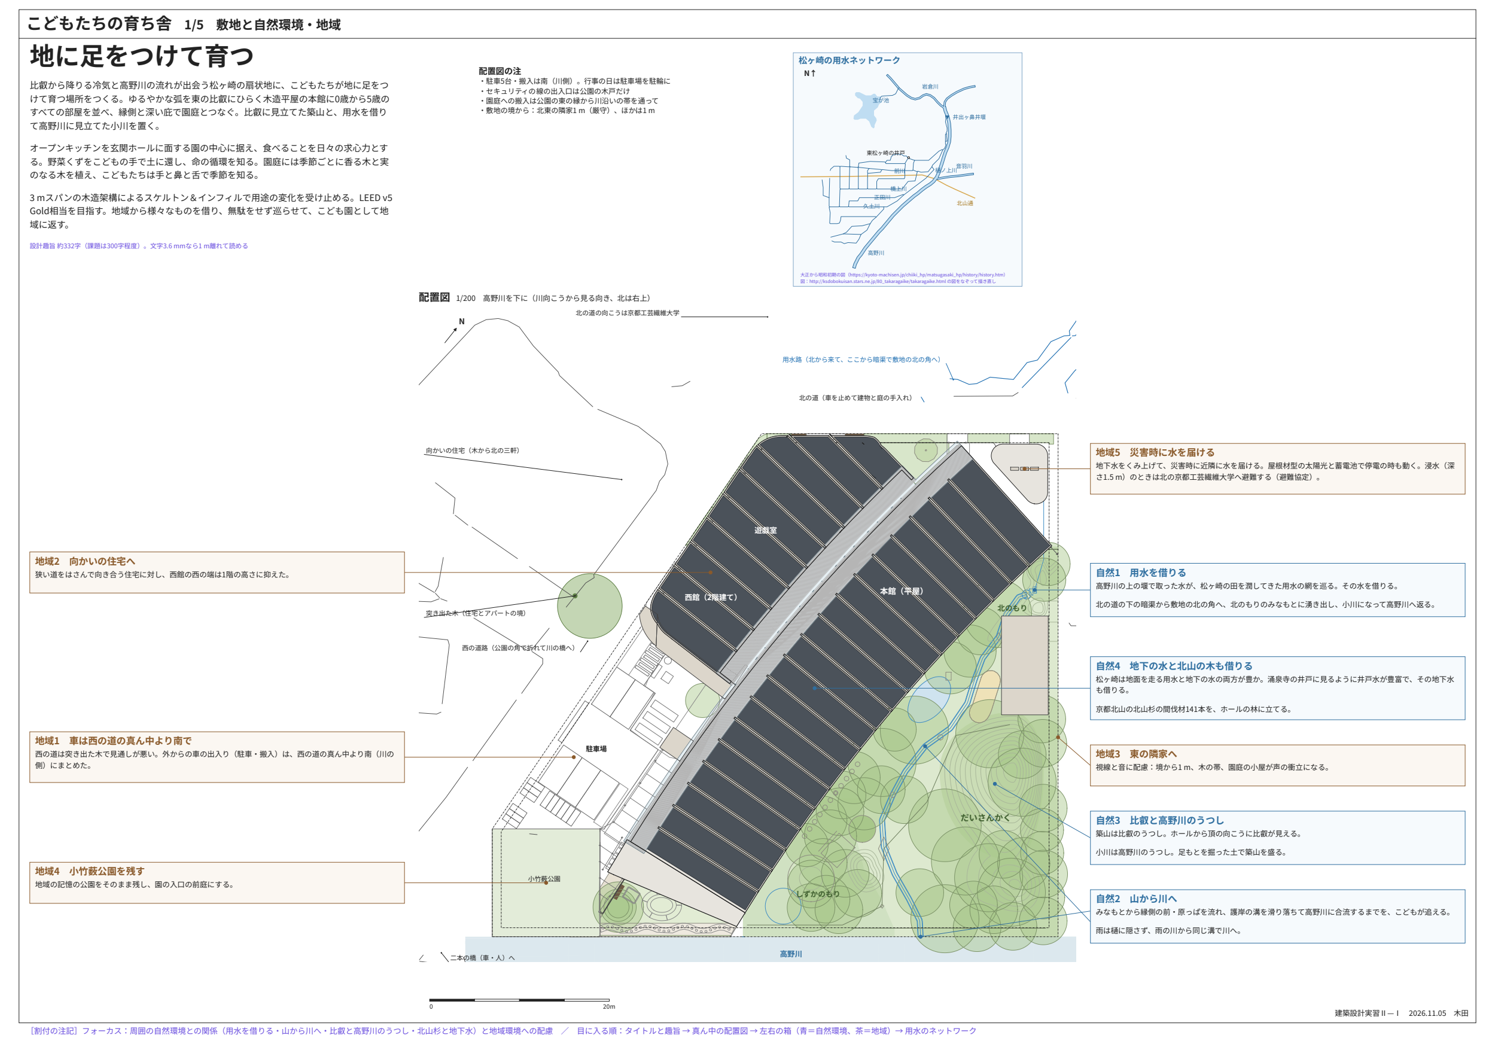
こどもたちの育ち舎　1/5　敷地と自然環境・地域
地に足をつけて育つ
配置図　1/200　高野川を下に（川向こうから見る向き、北は右上）
松ヶ崎の用水ネットワーク
地域4　小竹藪公園を残す
地域5　災害時に水を届ける
高野川

目の高さ1.5 m

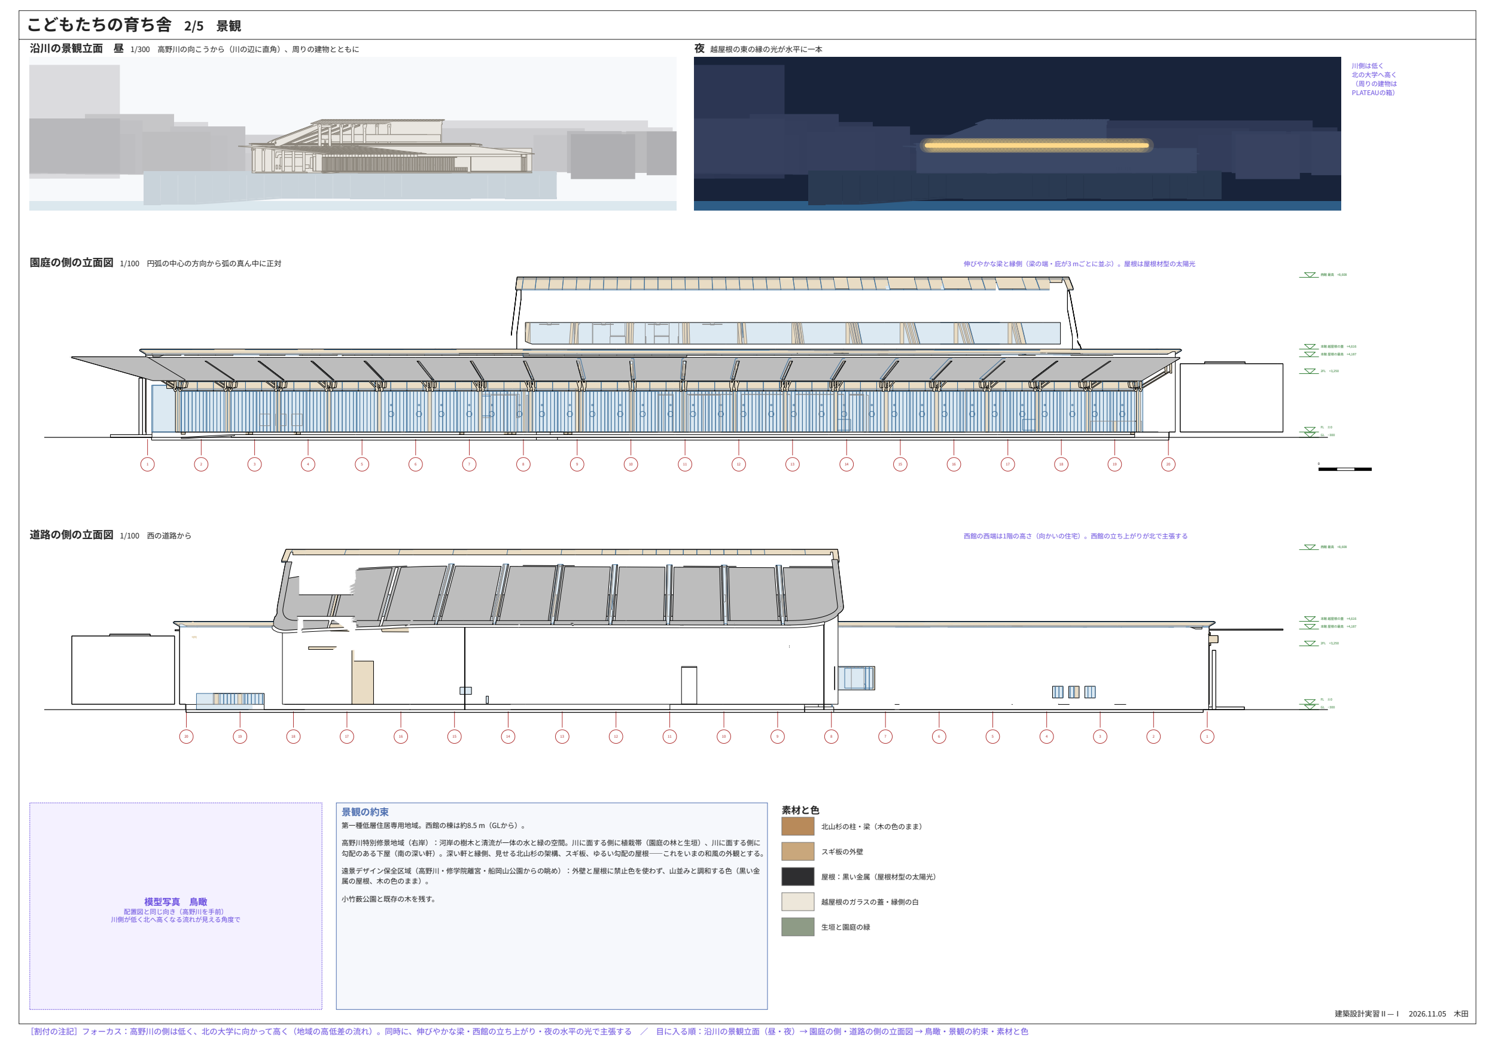
こどもたちの育ち舎　2/5　景観
沿川の景観立面　昼　1/300　高野川の向こうから（川の辺に直角）、周りの建物とともに
夜　越屋根の東の縁の光が水平に一本
園庭の側の立面図　1/100　円弧の中心の方向から弧の真ん中に正対
模型写真　鳥瞰

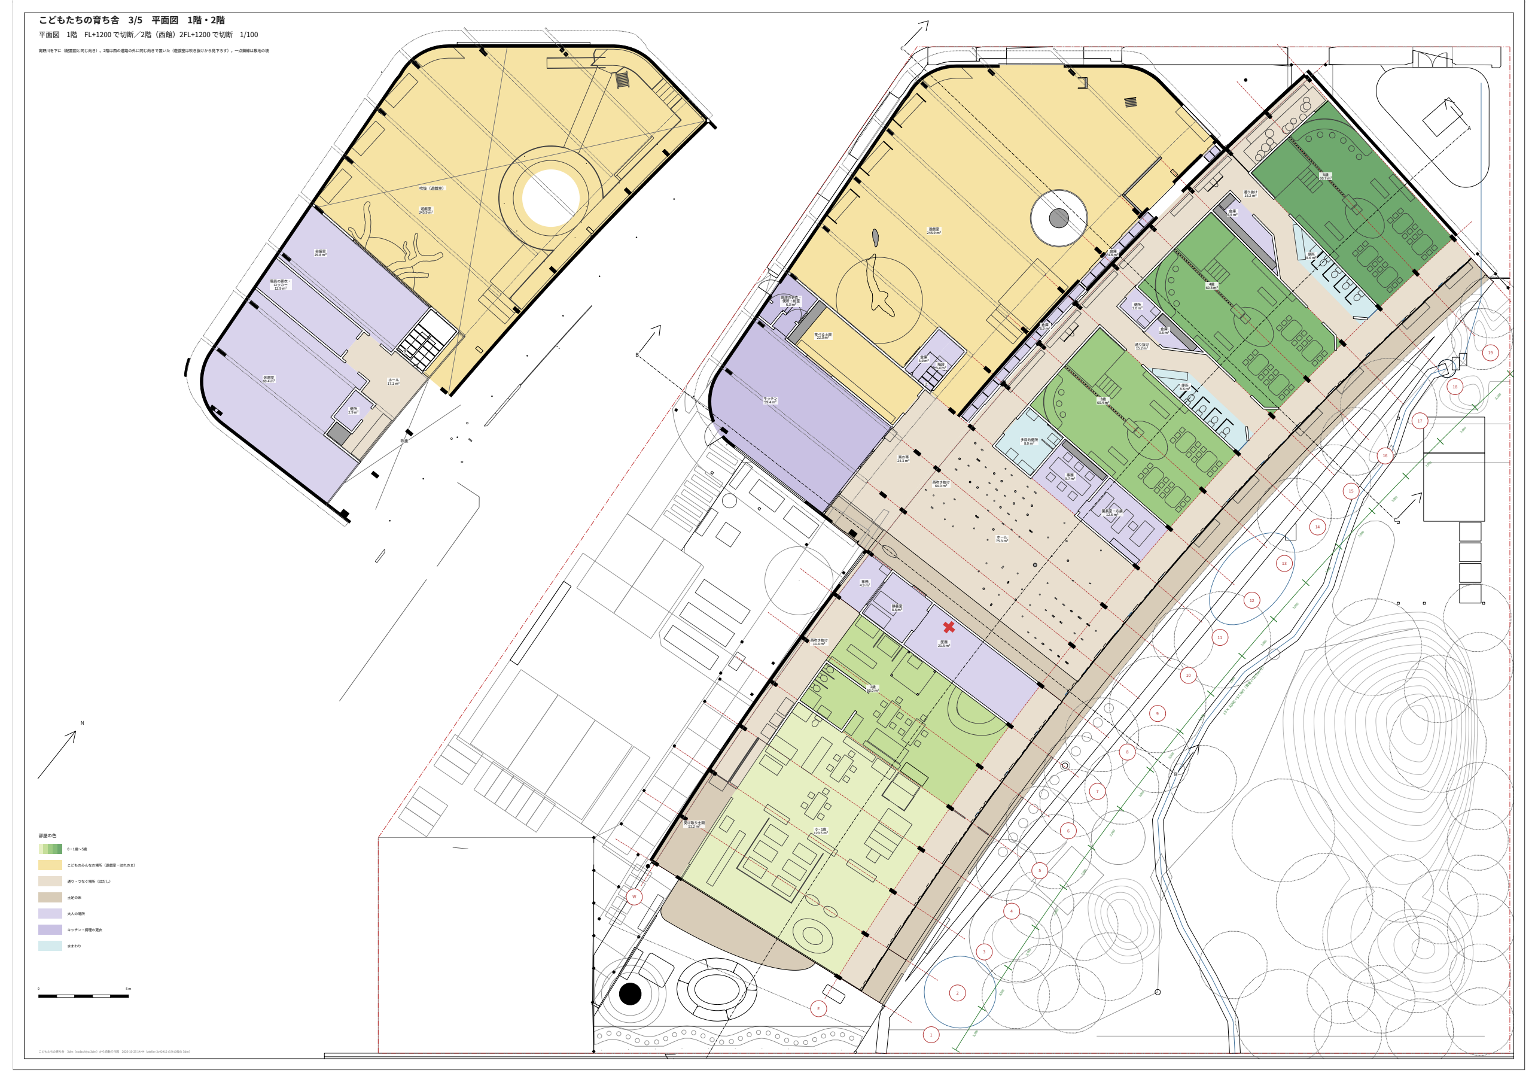
こどもたちの育ち舎　3/5　平面図　1階・2階
平面図　1階　FL+1200 で切断／2階（西館）2FL+1200 で切断　1/100

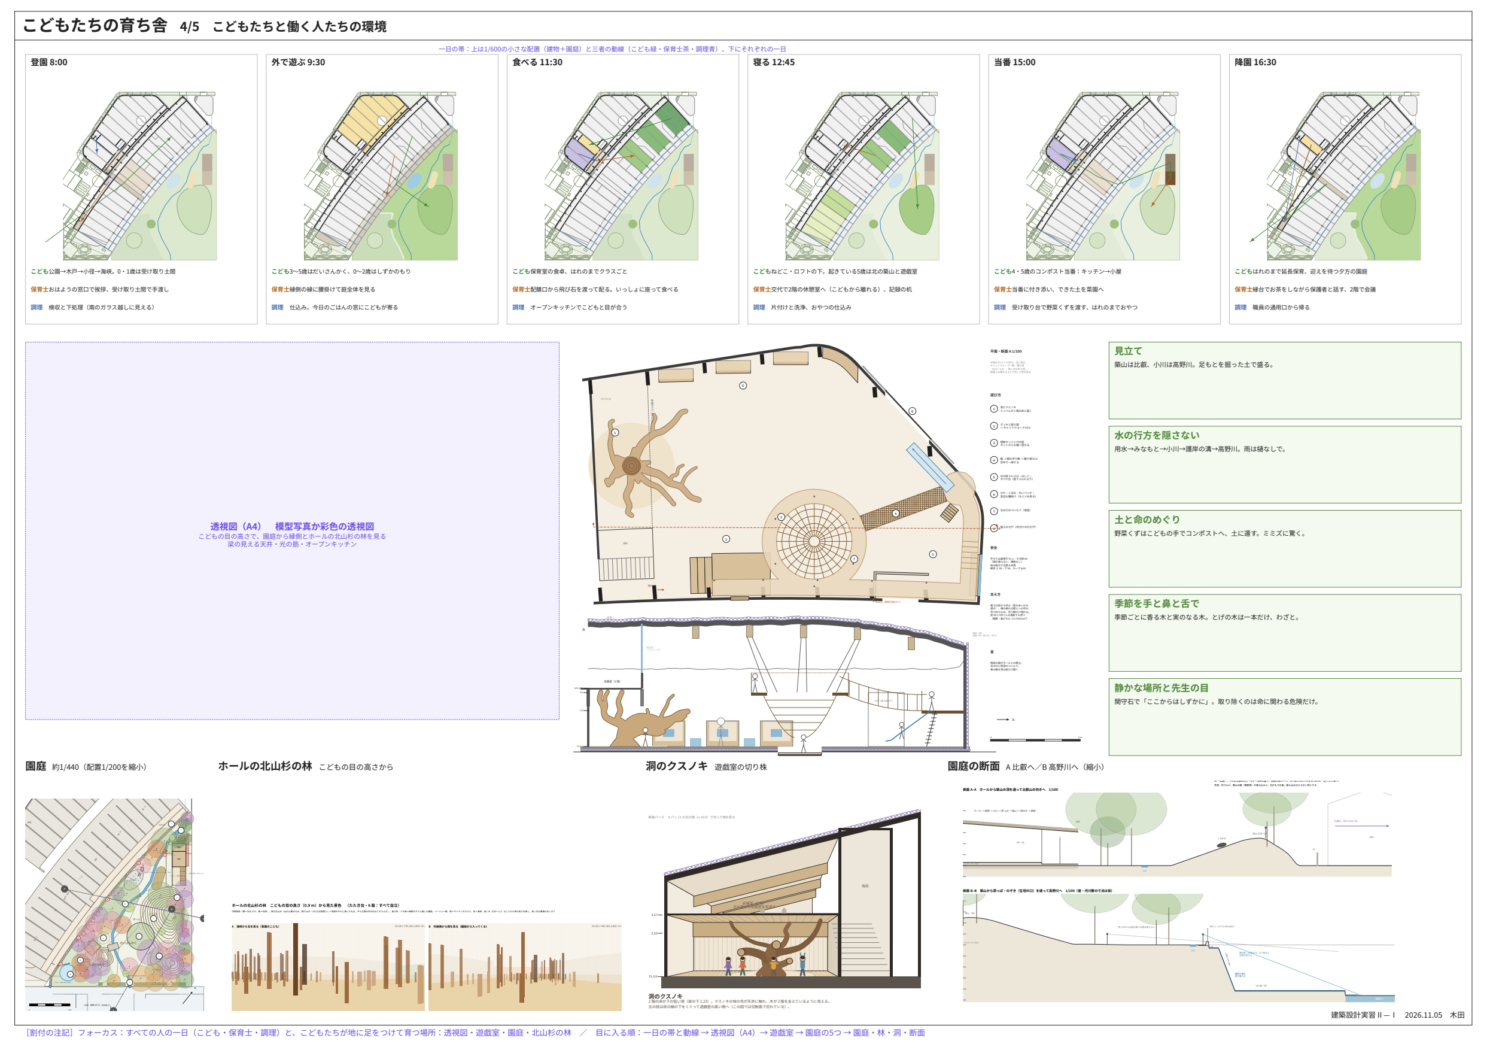

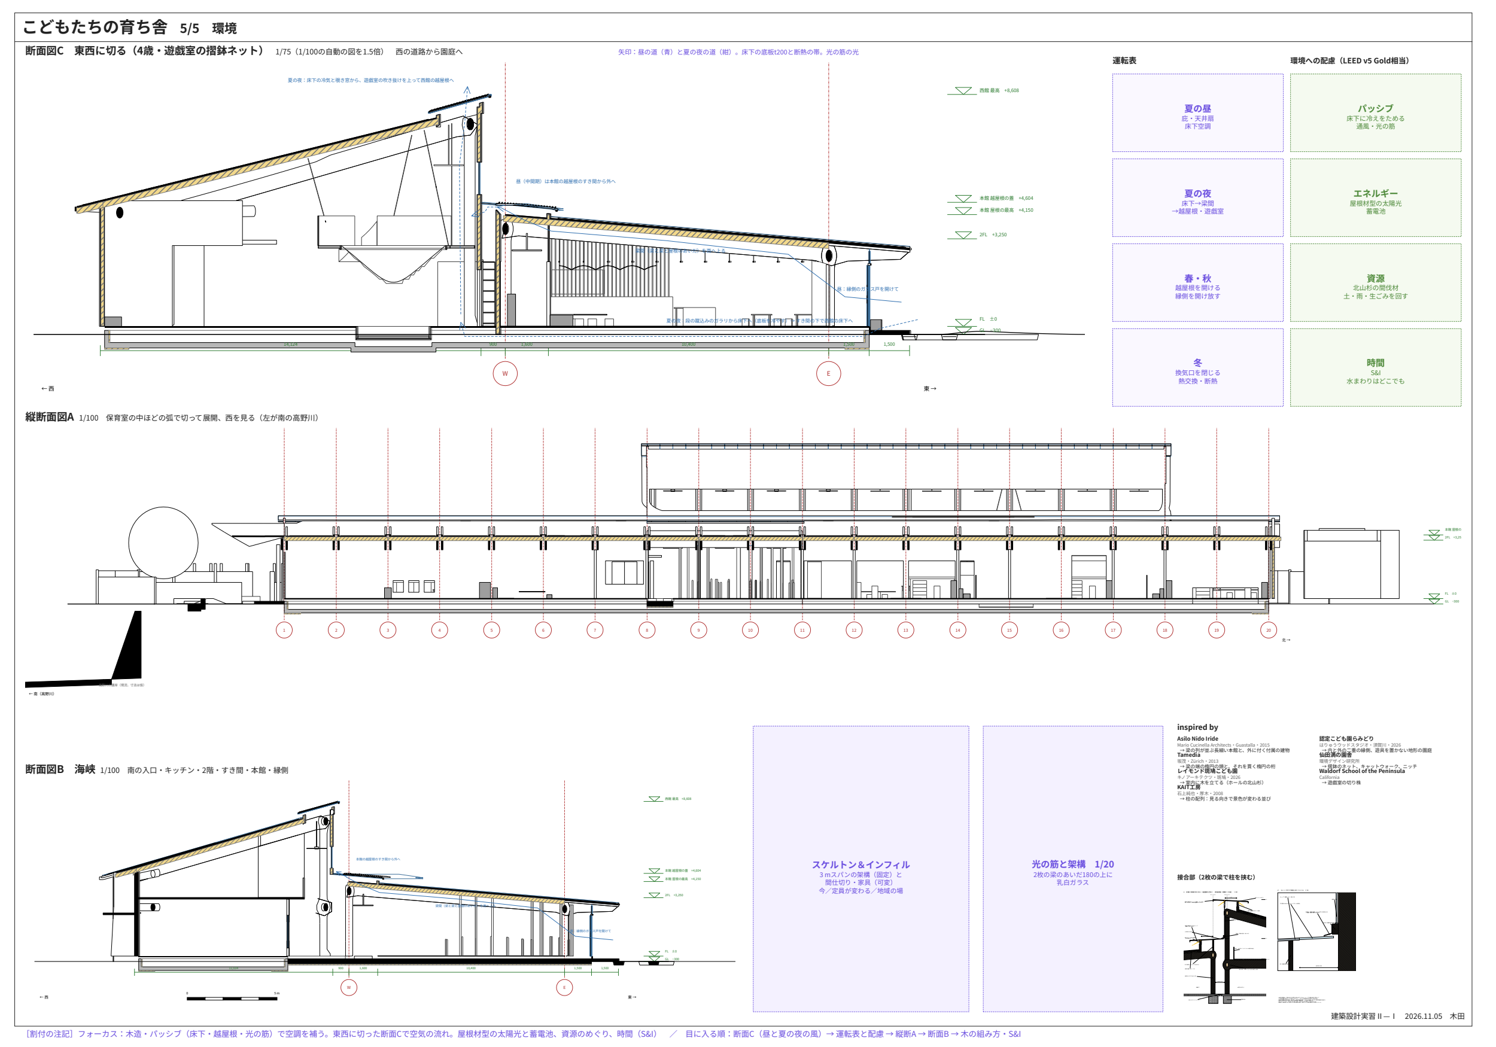
こどもたちの育ち舎　5/5　環境
断面図C　東西に切る（4歳・遊戯室の擂鉢ネット）　1/75（1/100の自動の図を1.5倍）　西の道路から園庭へ

左の列：1 敷地と自然環境・地域 → 2 景観 → 3 すべての人の一日。

右の列：4 こどもたちへの環境 → 5 環境。

目の高さに来るのは景観（立面）と園庭・遊戯室。

2・3・5枚目の平面・立面・断面は3dmから自動の図を実寸で貼る。

製図台に置くなら2+2+1（1・2／3・4／5）に切り分ける。

床