
平面図　2階（西館）　2FL+1000 で切断　1/100

高野川を下に（配置図と同じ向き）。1階の平面図と同じ位置・同じ縮尺（重ねると上下が合う）。西館の外（本館の屋根・園庭・周り）は上から見た見えがかり。二点鎖線は切断より上にある物（西館の屋根の外形など）

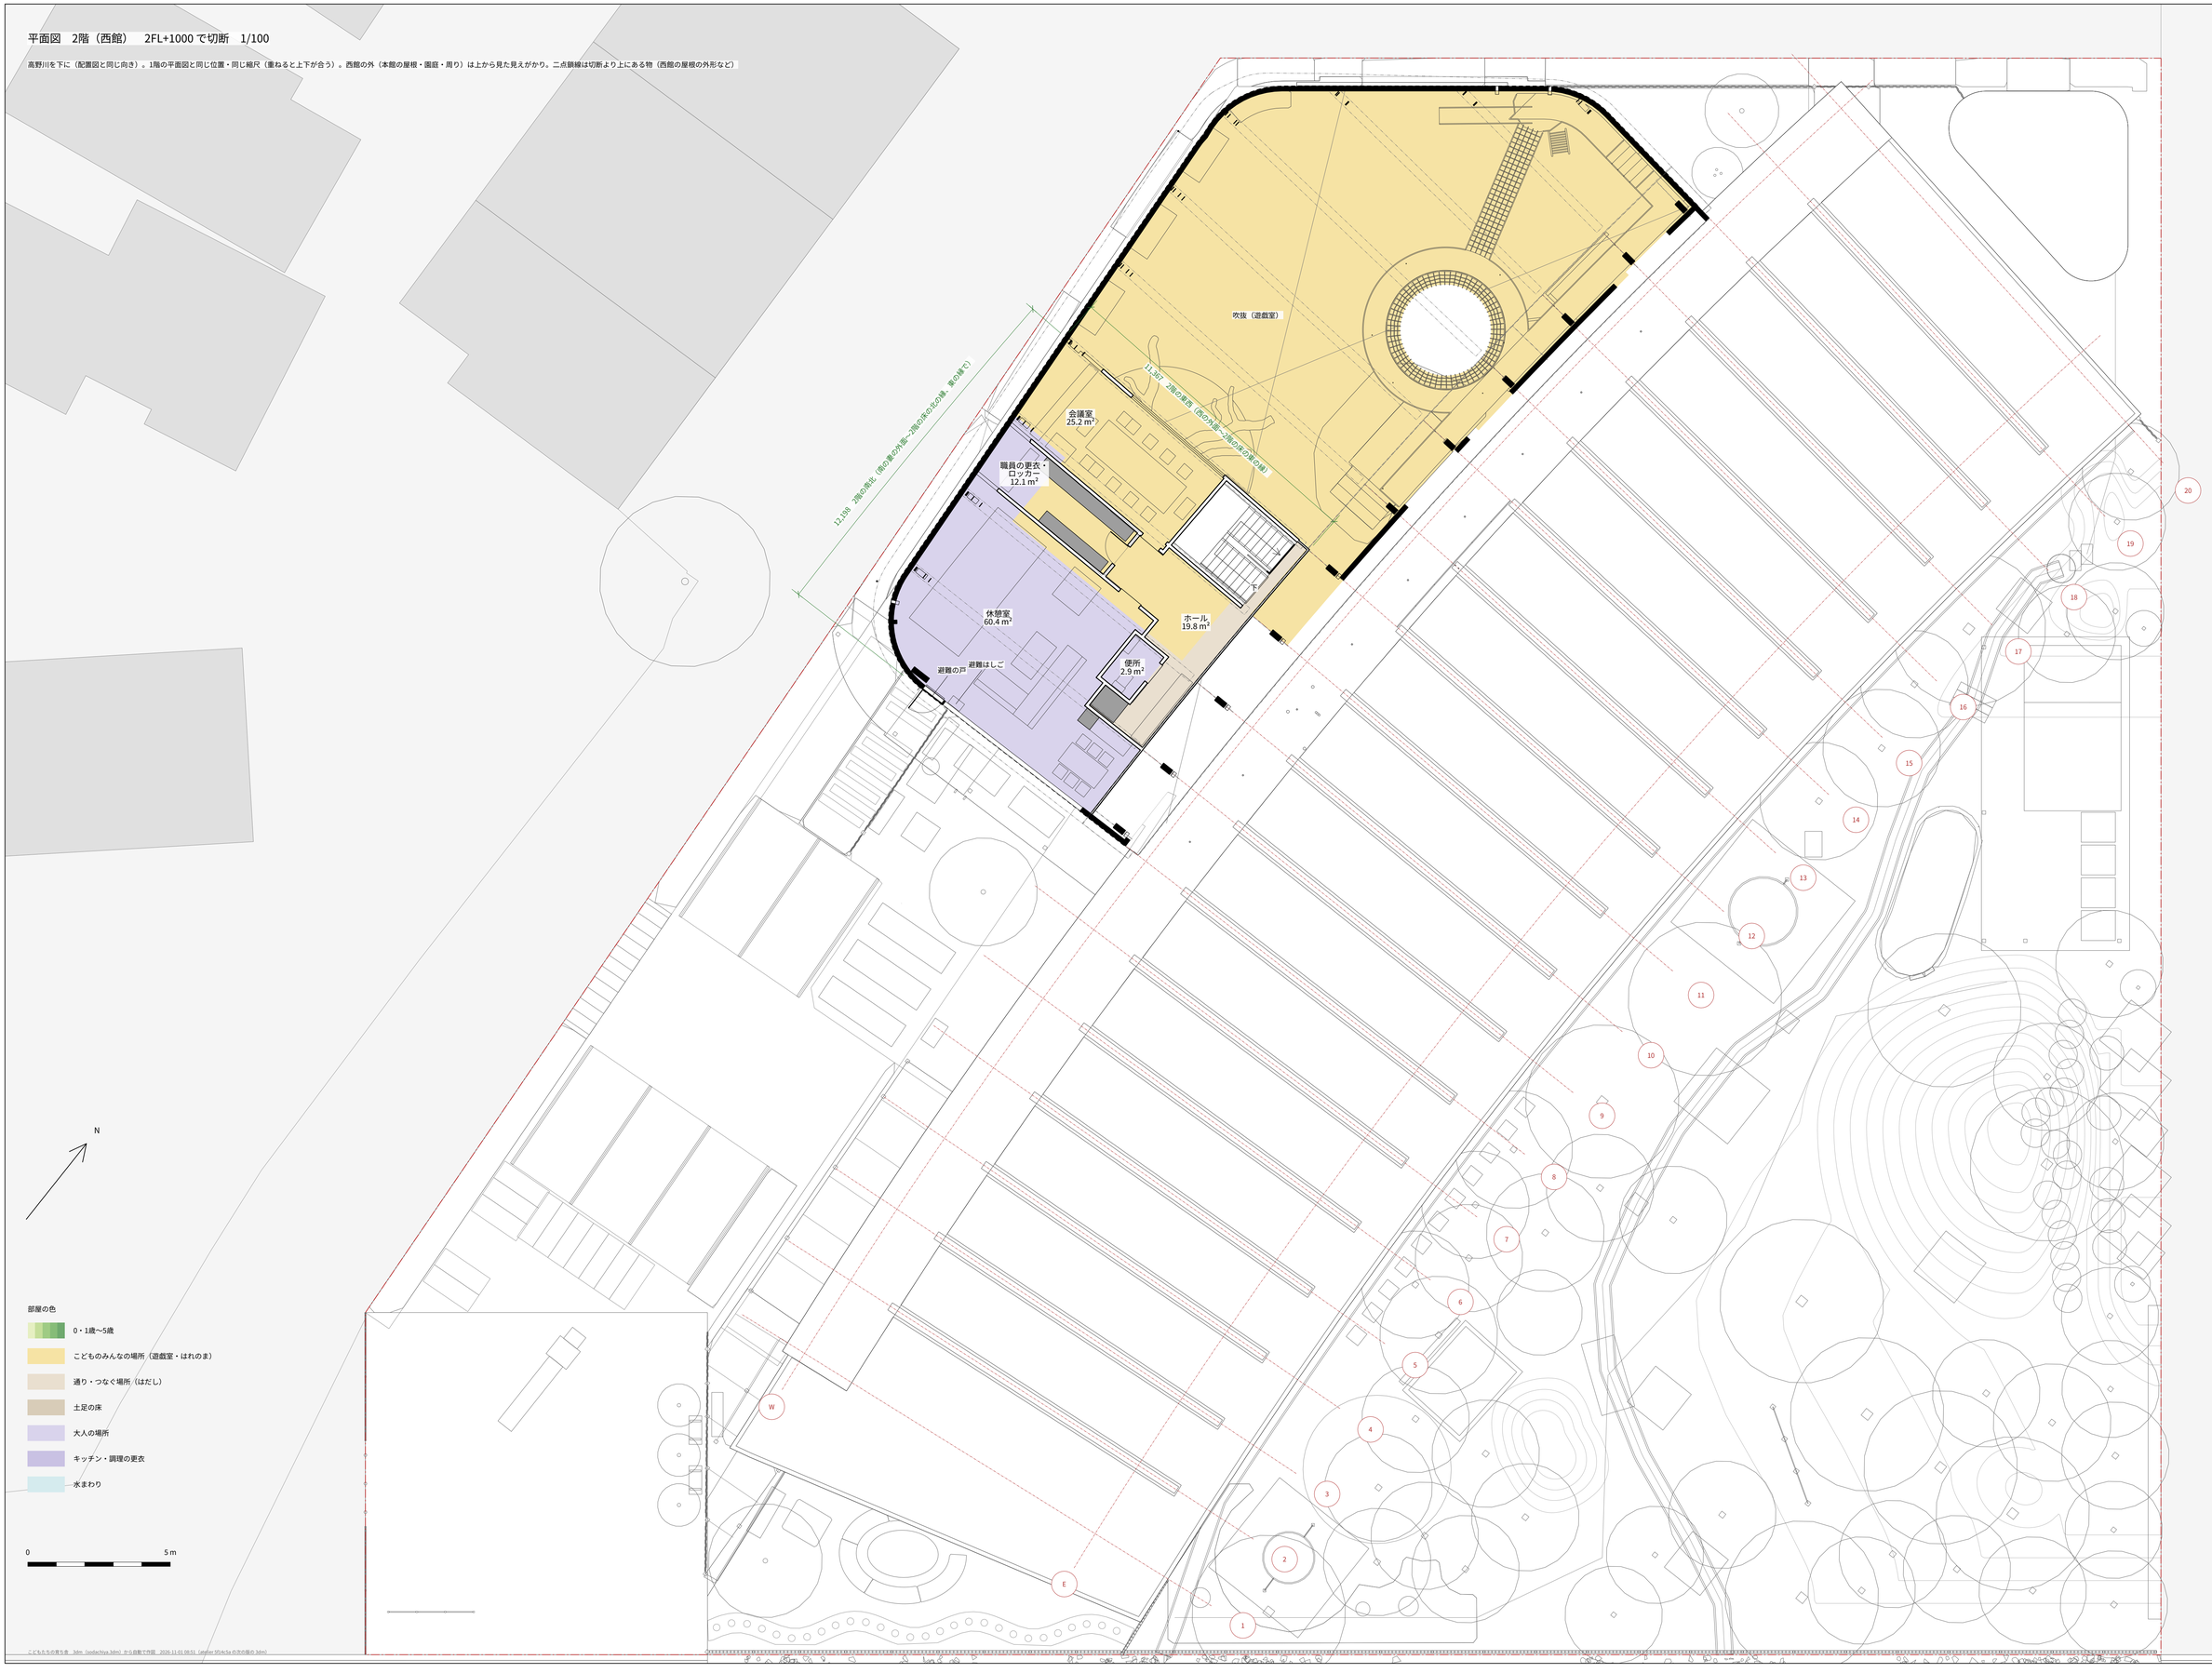

こどもたちの育ち舎　3dm（sodachiya.3dm）から自動で作図　2026-11-01 08:51（atelier 5的4c5a 作次の指示 3dm）